

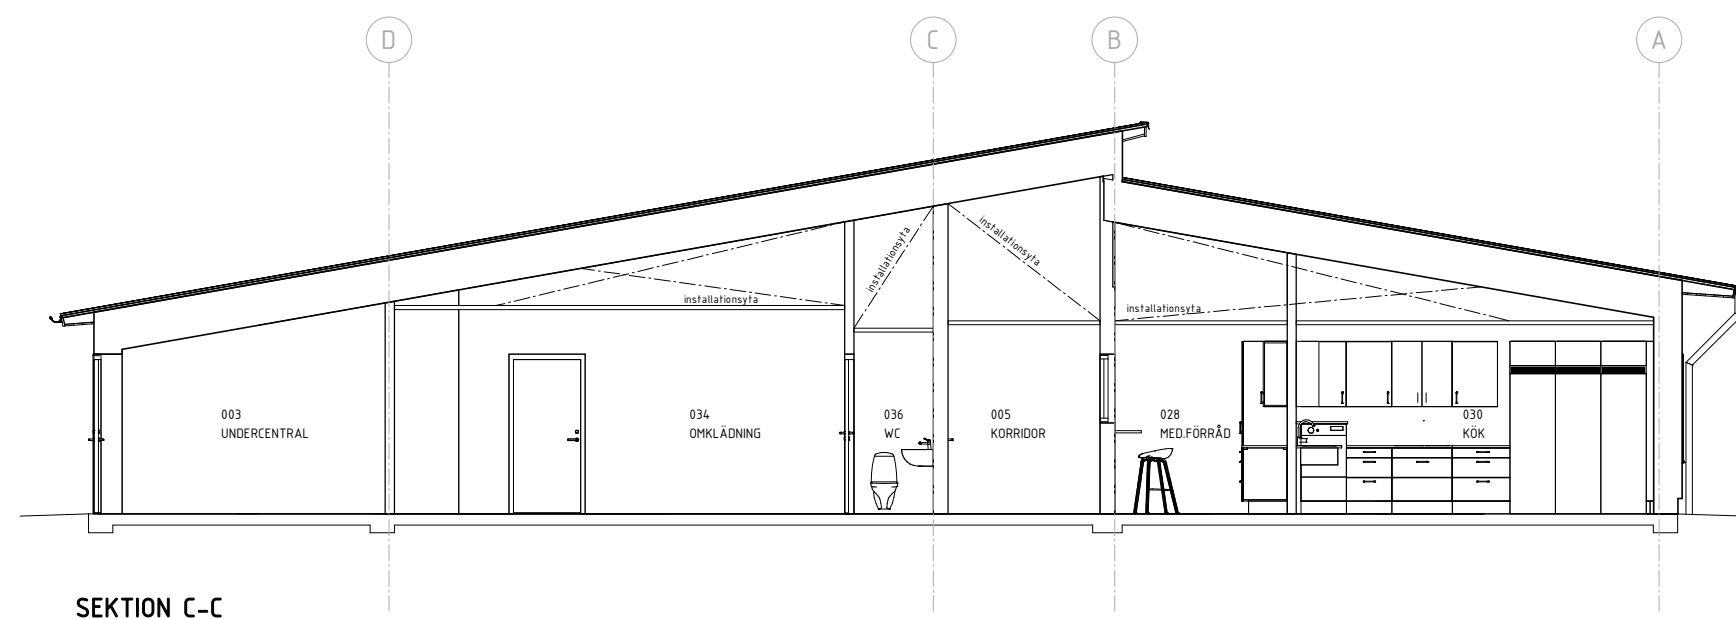
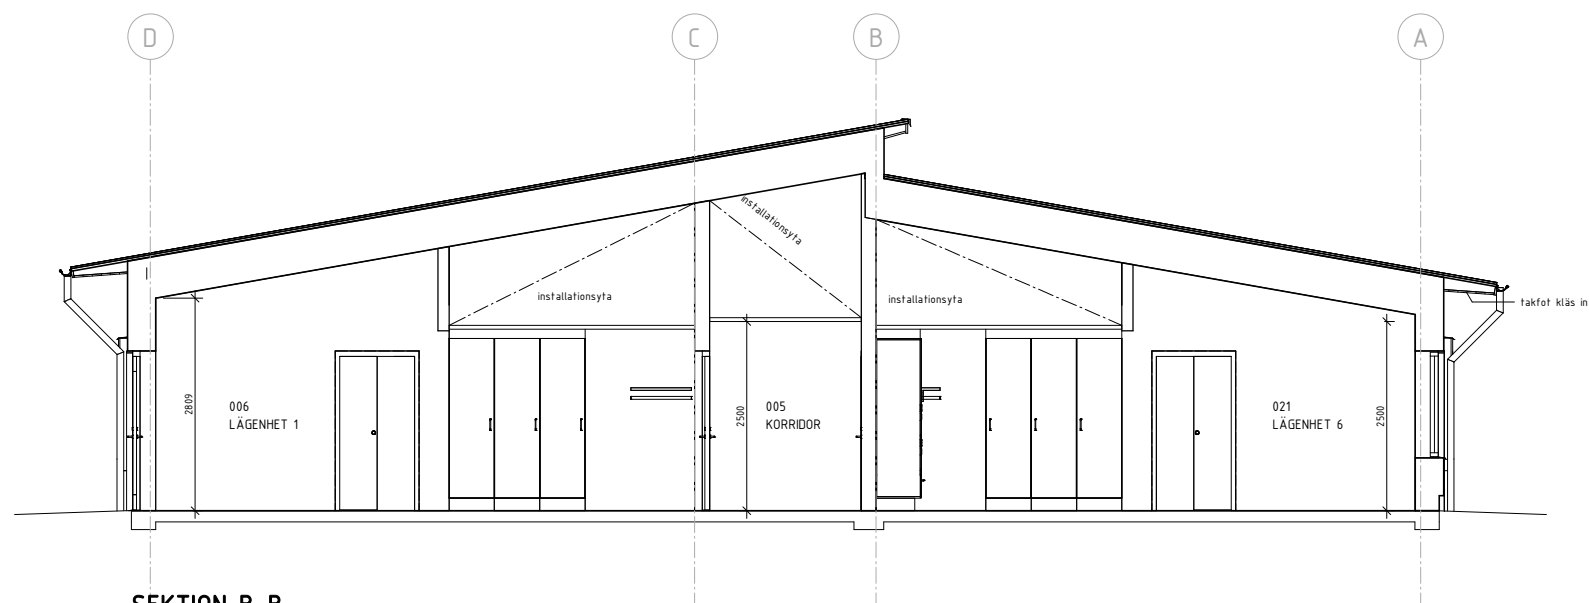


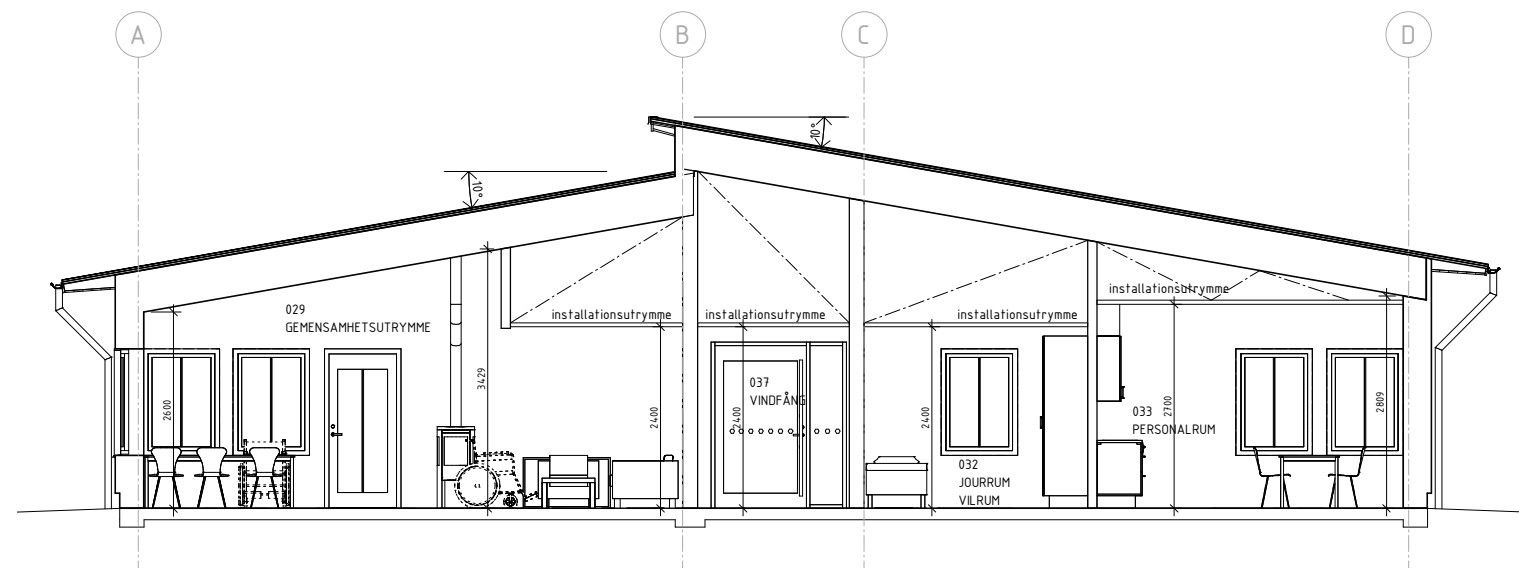

SKALA 1:50 (A3 1:100)

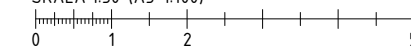

METER

BET	ÄNDRINGEN AVSER	DATUM	SIGN
FÖRFRÅGNINGSUNDERLAG			
SANDVIKENS KOMMUN LASARETTET 110			
 Sandvikens Kommun			
☒	A	SKOOG	ARKITEKTER
	L	SKOOG	ARKITEKTER
	E	RAMBÖLL	SVERIGE AB
	VVS	VVESH SYSTEMS	AB
	SP	BRIAB	
	BR	BRIAB	
UPPDRAG NR		RTÄD/KONSTR. AV	HANDLÄGGARE
23-220		JKL	JKL
DATUM		JÄNDSVARG	
2024-08-12		JKL	
LAKARSTIGEN			
NYBYGGNAD LSS-BOENDE 2024-25			
SEKTION A-A			
SKALA	NUMMER		BET
A 1: 50	A-40-2-01		
A 3: 1:100			