




P:\SANDVIKEN\Vallov-2-4 - Lasarettet-110\03 - Modell\Vallov - lss-boende.rvt
2024-12-16 08:14:13

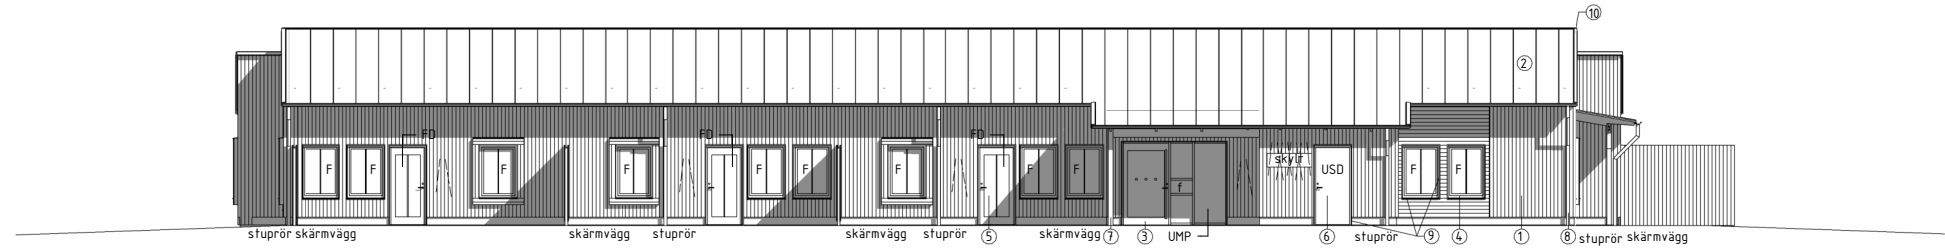


FASAD MOT NORR

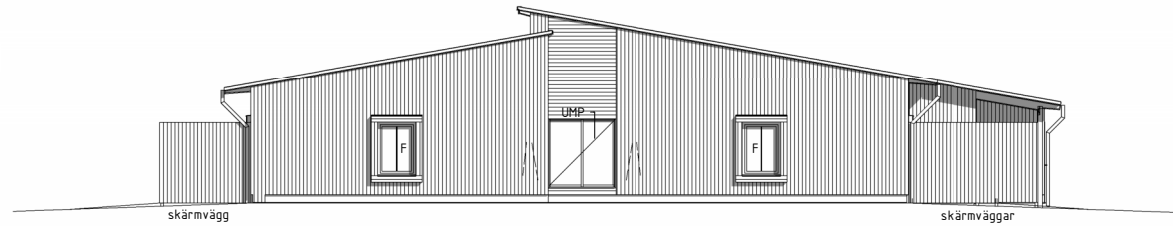

FASAD MOT ÖSTER

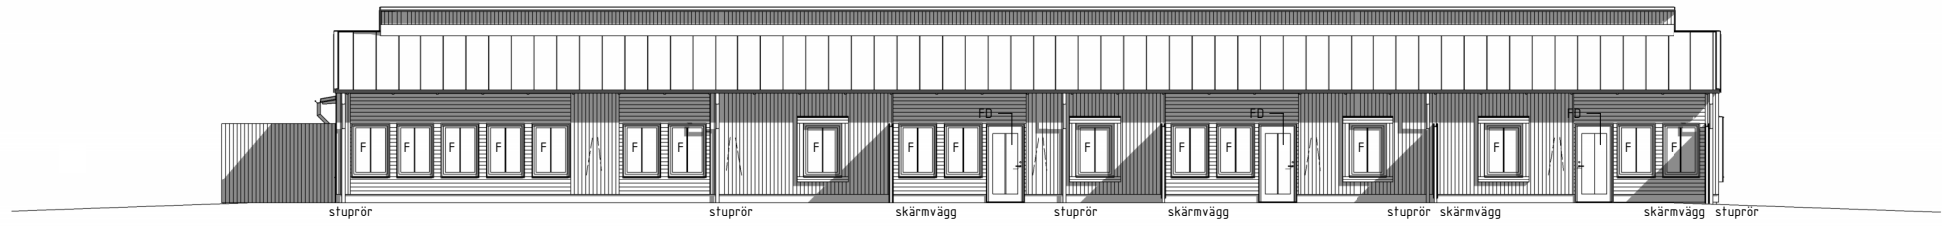


FASAD MOT SÖDER

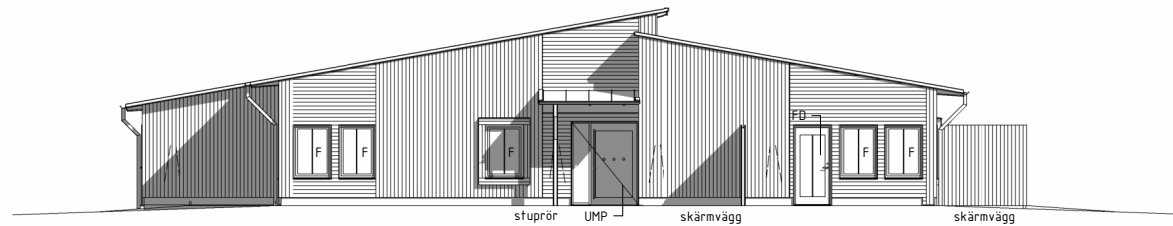

FASAD MOT VÄSTER



INSPIRATIONSBild - ERSKINE "NYA BRUKET"
BYGGNADEN DELAS UPP I MINDRE ENHETER
GENOM EN VARIERAD FASADPANEL VILKET
FÖRSTÄRKER KÄNSLAN AV DEN ENSKILDA BOSTADEN

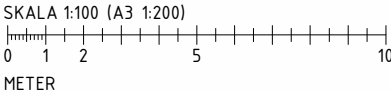

FÖRKLARING

UTVÄNDIG KULÖRSÄTTNING

- 1 YTTERVÄGGSPANEL: LASYRFÄRG;
JOTUN TYRILIN 1208 KJERAG
- 2 BANDTÄCKNING: RAL 9007, MÖRK SILVERMETALLIC
- 3 U. METALLPARTIER: RAL 7009, GRÖNGRÅ
- 4 FÖNSTER RAL 7009, GRÖNGRÅ
- 5 FÖNSTERDÖRRAR RAL 7009, GRÖNGRÅ
- 6 STÅLDÖRRAR RAL 7009, GRÖNGRÅ
- 7 SYNLIKT TRÄ, LIKA YTTERVÄGGSPANEL
SKÄRMVÄGGAR OD
- 8 TAKAVÄTTNING RAL 9007, MÖRK SILVERMETALLIC
- 9 PLÅTKOMPL. KULÖR LIKA FÖNSTER/DÖRRAR
OD
- 10 PLÅTKOMPL. PÅ KULÖR LIKA YTTERTAK
YTERTAK (STOSAR OD)

FÖRKORTNINGAR:
F= FÖNSTER
FD= FÖNSTERDÖRR
USD= UTVÄNDIG STÅLDÖRR
UMP= UTVÄNDIGT METALLPARTI
f= FYLNING I METALLPARTI

BET	ÄNDRINGEN AVSER	DATUM	SIGN
FÖRFRÅGNINGSUNDERLAG			
SANDVIKENS KOMMUN LASARETTET 110			
 Sandvikens Kommun			
☒	A	SKOOG	ARKITEKTER tel. 026-62 40 30
☐	L	SKOOG	ARKITEKTER tel. 026-62 40 30
☐	E	RAMBÖLL SVERIGE AB	tel. 070-5191799
☐	VVS	VVESS SYSTEMS AB	tel. 070-6623244
☐	SP	BRIAB	tel. 0708-729202
☐	BR	BRIAB	tel. 0707-91 00 20
UPPDRAG NR 23-220		RIKADKONSTR. AV JKL	HANDLÄGGARE JKL
DATUM 2024-08-12		ANSVARIG JKL	
LAKARSTIGEN NYBYGGNAD LSS-BOENDE 2024-25 FASADER			
SKALA A1 1:100 A3 1200	NUMMER A-40-3-01		BET