




2024-12-16 08:44:44 P:\SANDVIKEN\Valhöv-2-4 - Lasarettet-110\03 - Modell\Valhöv - lss-boende.rvt

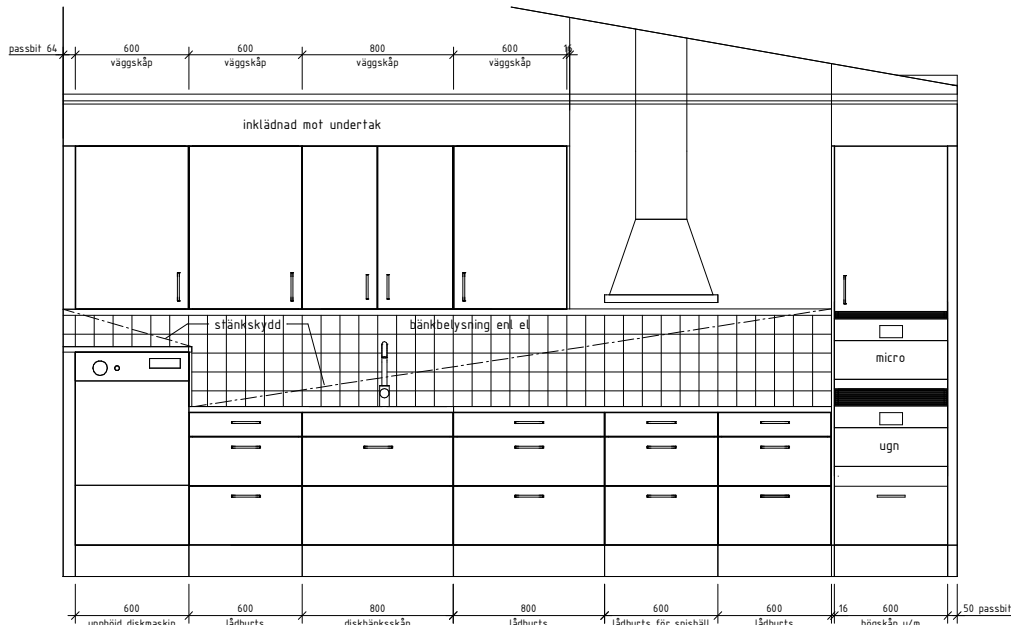


GEMENSAMT KÖK - VY 1

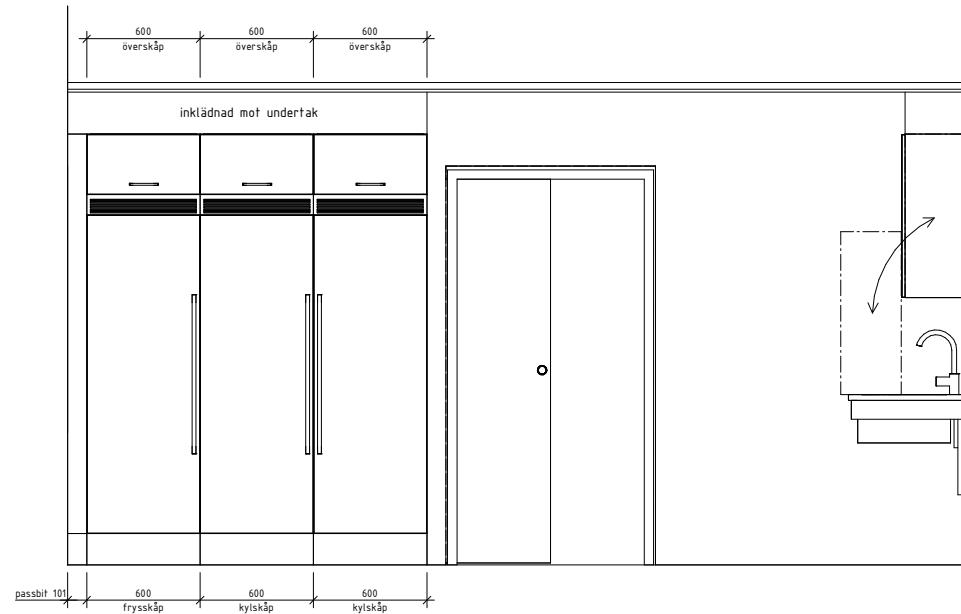


GEMENSAMT KÖK - VY 3

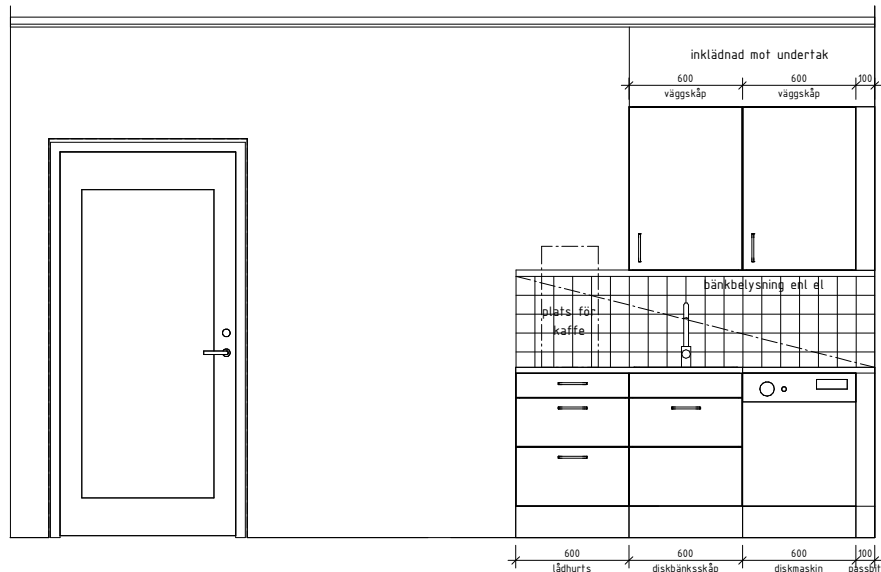


PENTRY I PERSONALRUM 033

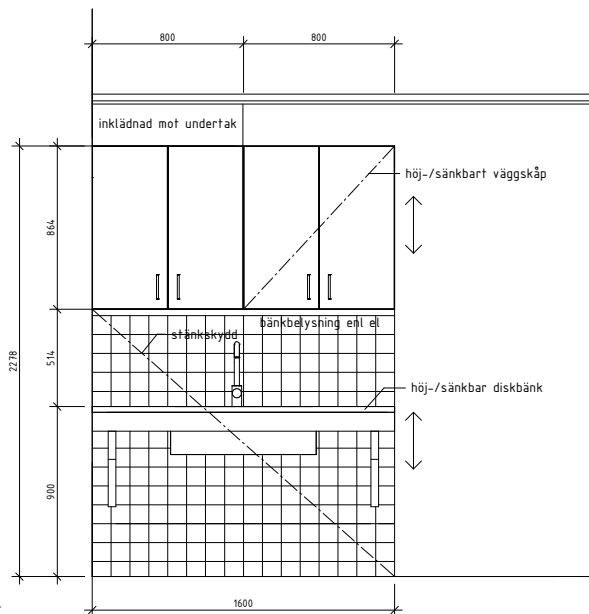


GEMENSAMT KÖK - VY 2 SKÅPINREDNING TYP 2

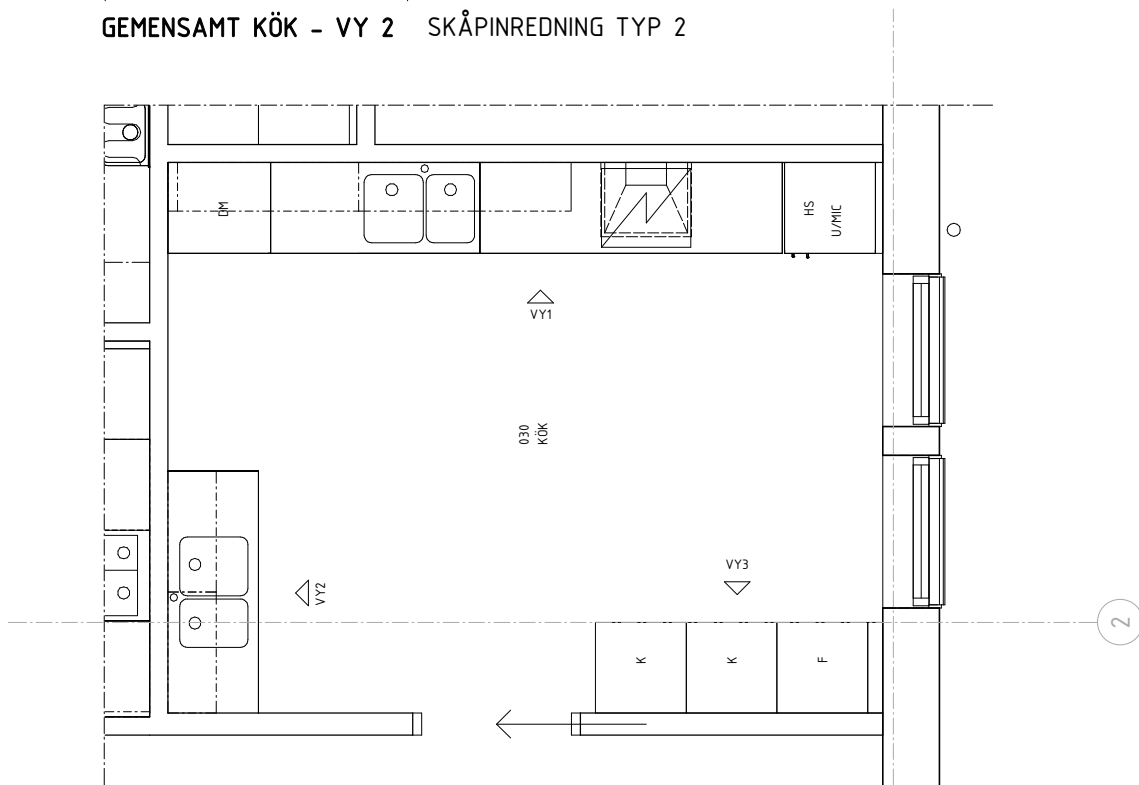

PLAN SKALA 1:25 (A3 1:50)

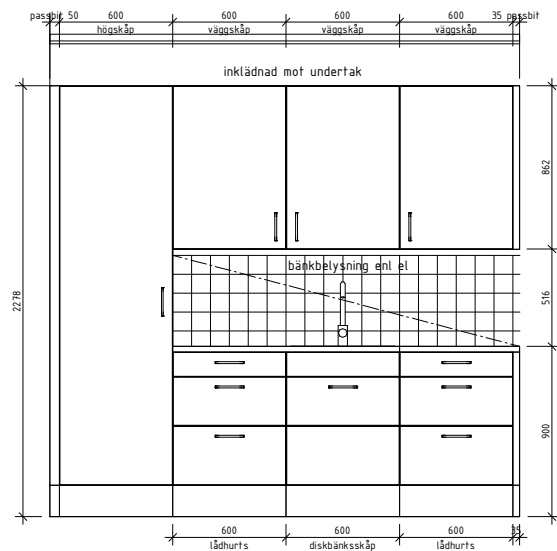

BÄNKINREDNING MEDICINRUM

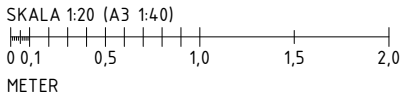

FÖRESKRIFTER

MÅTT ANGES I MILLIMETER

SAMTLIGA SKÅP SKA FÖRSES MED INKLÄDNAD MOT TAK, YTSKIKT GIPS, KULÖR LIKA OMGIVANDE VÄGGAR

SKÅPINREDNING GENERELLT

SKALL VARA **MARBODAL** LUCKOR, SKÅPSTOMMAR, PASSBITAR I SERIEN:

TORÖ EK, VIT
BÄNKSÅP STÄLLS PÅ BEN MED DEMONTERBAR SOCKEL SOCKEL SKALL VARA KULÖR **EK**
TÄCKSIDOR UTFÖRS MED SAMMA UTSEENDE SOM LUCKOR.

SKÅPINREDNING 2

STOMME SKALL VARA **GRANBERG** LUCKOR, SKÅPSTOMMAR, PASSBITAR I SERIEN TORÖ EK, VIT. 1 VÄGGSÅP OCH DISKBÄNK SKALL VARA HÖJ- OCH SÄNKBAR. EV TÄCKSIDOR UTFÖRS MED SAMMA UTSEENDE SOM LUCKOR.

HANDTAG

SKALL VARA, SKÅPSLUCKOR/LÅDOR: **TRÅD ROSTFRI 128 MM**

BÄNKSIVA

SKALL VARA **LAMINAT EK**, KANTPROFIL **MF2 30MM**

STÄNKSKYDD

SKALL VARA **SKANDIKAKEL, SERIE KULÖR 97X97X5,5MM** ELLER LIKVÄRDIGT, KULÖR **LJUSGRÅ**. FÖG, KULÖR **LJUSGRÅ** OMFATTNING ENL. ELEVATION

KAKELLIST

SKALL VARA AV EK, RAK LIST MED URSPARNING FÖR KAKELPLATTOR. DIMENSION 12X34.

DISKBÄNK

FRANKE DELUX G 30MM. 1200MM 1 ½ DISKLÄDA

VITVAROR

ELECTROLUX / FRANKE
KYL: **ERF3866AOW, VIT**
FRYS: **EUF2946AOW, VIT**
KYL/FRYS: **EN3453MOW, VIT**
INDUKTIONSHÅLL: **HMB650FBK**
MIKROVÅGSUGN: **EMS26254OW, VIT**
DISKMASKIN: **ESF5201LOW, VIT**
UGN: **EVY3841AOW, VIT**
KOLFILTERFLÄKT: **FRANKE TENDER 729, VIT**

ÖVRIGT

SAMTLIGA LÅDOR OCH LUCKOR SKALL FÖRSES MED DÄMPNINGSFUNKTION. DISKBÄNK SKALL FÖRSES MED SORTERINGSKÄRL. ÖVERSTA LÅDAN I EN LÅDHURTS SKALL FÖRSES MED LÅSBAR BESTICKLÅDA.

BET	ÄNDRINGEN AVISER	DATUM	SIGN
FÖRFRÅGNINGSUNDERLAG			
SANDVIKENS KOMMUN LASARETTET 110			
 Sandvikens Kommun			
☒	A	SKOOG	ARKITEKTER tel. 026-62 40 30
☐	L	SKOOG	ARKITEKTER tel. 026-62 40 30
☐	E	RAMBÖLL	SVERIGE AB tel. 070-5191799
☐	VVS	VVESS SYSTEMS AB	tel. 070-6623244
☐	SP	BRIAB	tel. 0708-729202
☐	BR	BRIAB	tel. 0707-91 00 20
UPPDRAG NR 23-220		RTADKONSTR. AV JKL	HANDLÄGGARE JKL
DATUM 2024-08-12		ANSVARIG JKL	
LAKARSTIGEN NYBYGGNAD LSS-BOENDE 2024-25 GEMENSAMT KÖK			
SKALA A1 1:20 A3 1:40	NUMMER A-46-4-01		BET