




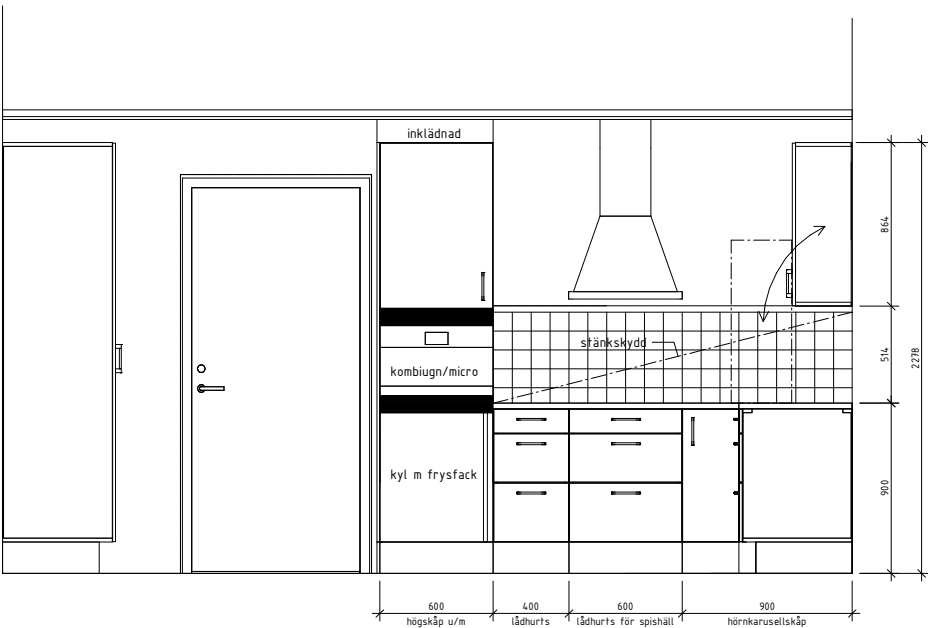

BOENDEKÖK - VY 1

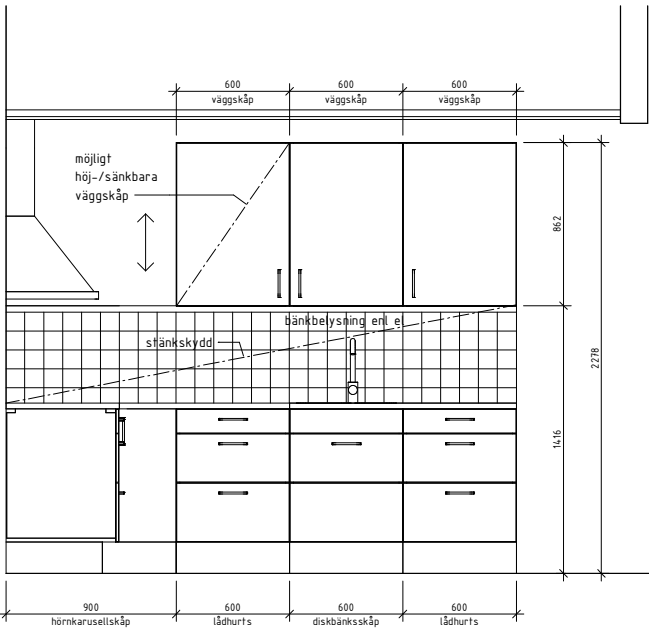

BOENDEKÖK - VY 2

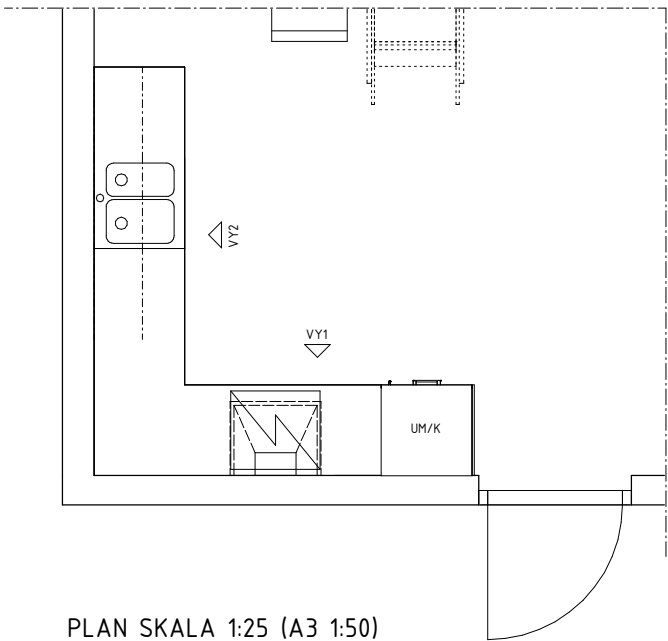

PLAN SKALA 1:25 (A3 1:50)

FÖRESKRIFTER

MÅTT ANGES I MILLIMETER

SAMTLIGA SKÅP SKA FÖRSES MED INKLÄDNAD MOT TAK, YTSKIKT GIPS, KULÖR LIKA OMGIVANDE VÄGGAR

SKÅPINREDNING 1
SKALL VARA **MARBODAL**.
LUCKOR, SKÅPSTOMMAR, PASSBITAR I SERIEN:
TORÖ EK, VIT
BÄNKSÅP STÄLLS PÅ BEN MED DEMONTERBAR SOCKEL
SOCKEL SKALL VARA KULÖR **EK**
TÄCKSIDOR UTFÖRS MED SAMMA UTSEENDE SOM LUCKOR.

HÖJ- OCH SÄNKBARA VÄGGSKÅP SKA HA STOMME FRÅN **GRANBERG**. 1 VÄGGSKÅP SKALL VARA HÖJ- OCH SÄNKBART.

HANDTAG
SKALL VARA: **TRÅD ROSTFRI 128 MM**

BÄNKSIVA
SKALL VARA **LAMINAT EK**. KANTPROFIL **MF2 30MM**

STÄNKSKYDD
SKALL VARA **SKANDIKAKEL, SERIE KULÖR 97X97X5,5MM**
ELLER LIKVÄRDIGT, KULÖR **LJUSGRÅ**. STÄENDE MONT.
FÖG, KULÖR **LJUSGRÅ**
OMFATTNING ENL. ELEVATION

KAKELLIST
SKALL VARA AV EK, RAK LIST MED URSPARNING FÖR KAKELPLATTOR. DIMENSION 12X34.

DISKBÄNK
FRANKE DELUX G 30MM, 1200MM 1 ½ DISKLÄDA

VITVARÖR
ELECTROLUX / FRANKE
KYL M FRYSPACK: **LFB3AE82R, VIT**
INDUKTIONSHÄLL: **HHB650FBK**
KOMBINERAD
VÄRMFLUTSUGN/MICRO: **00M907NB, 800 COMBIQUICK**
KÖLFILTERFLÄKT: **FRANKE TENDER 729, VIT**

ÖVRIGT
SAMTLIGA LÅDOR OCH LUCKOR SKALL FÖRSES MED DÄMPNINGSFUNKTION. DISKBÄNK SKALL FÖRSES MED SORTERINGSKÄRL. ÖVERSTA LÅDAN I EN LÅDHURTS SKALL FÖRSES MED LÅSBAR BESTICKLÄDA.

BET	ÄNDRINGEN AVSER	DATUM	SIGN
FÖRFRÅGNINGSUNDERLAG			
SANDVIKENS KOMMUN LASARETTET 110			
 Sandvikens Kommun			
☒	A	SKOOG	ARKITEKTER
☐	L	SKOOG	ARKITEKTER
☐	E	RAMBÖLL	SVERIGE AB
☐	VVS	VVSS SYSTEMS AB	
☐	SP	BRIAB	
☐	BR	BRIAB	
UPPDRAG NR 23-220			
DATUM 2024-08-12		ANSVARIG JKL	HANDLÄGGARE JKL
LAKARSTIGEN NYBYGGNAD LSS-BOENDE 2024-25 BOENDEKÖK			
SKALA A1 1:20 A3 1:40	NUMMER A-46-4-02		BET

