



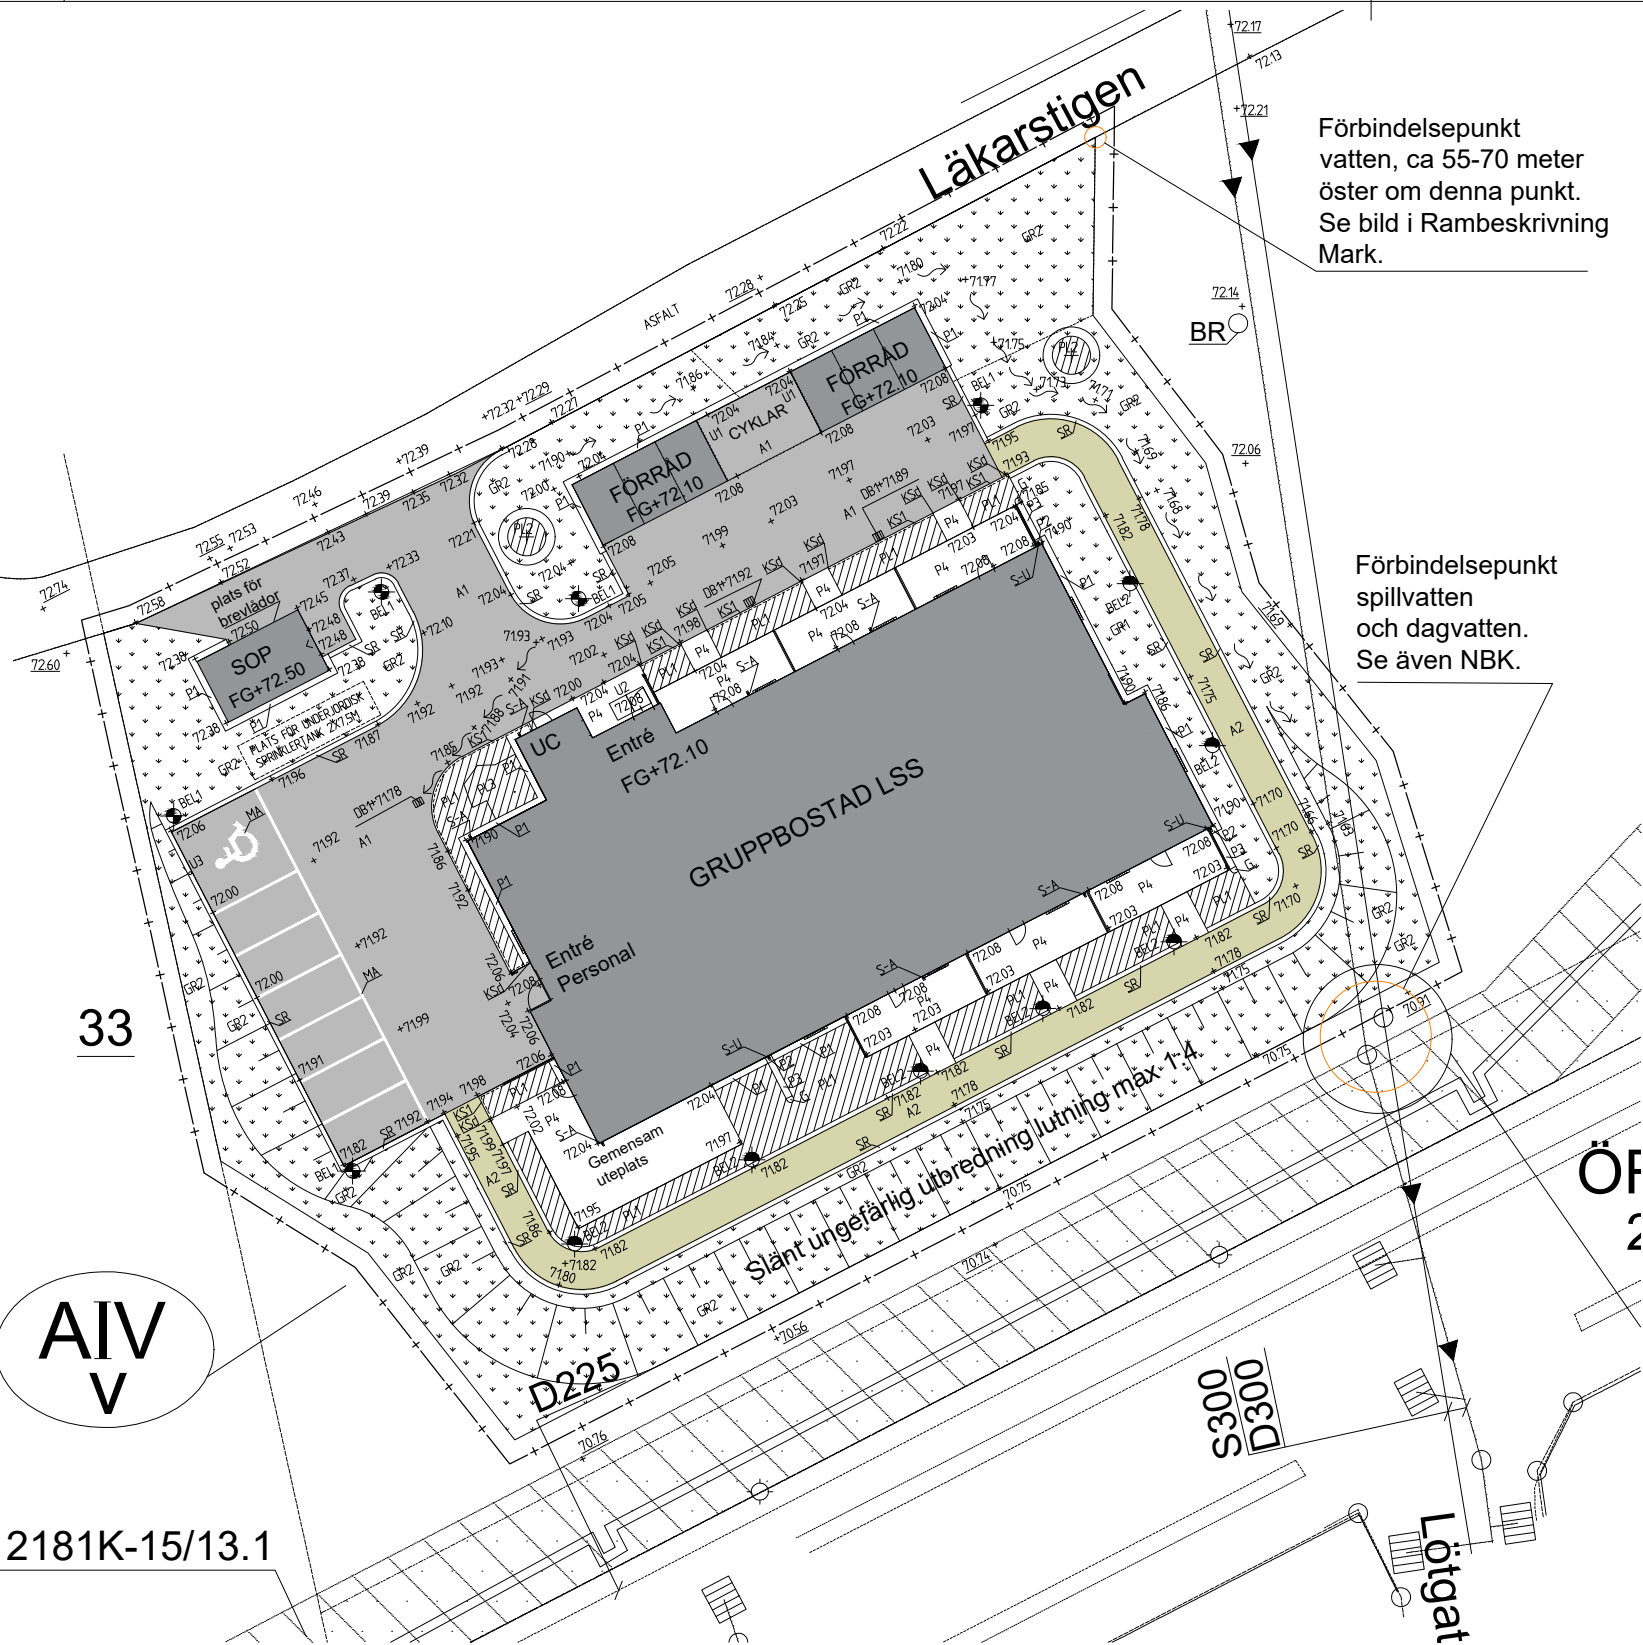


Förbindelsepunkt vatten, ca 55-70 meter öster om denna punkt. Se bild i Rambeskrivning Mark.

Förbindelsepunkt spillvatten och dagvatten. Se även NBK.

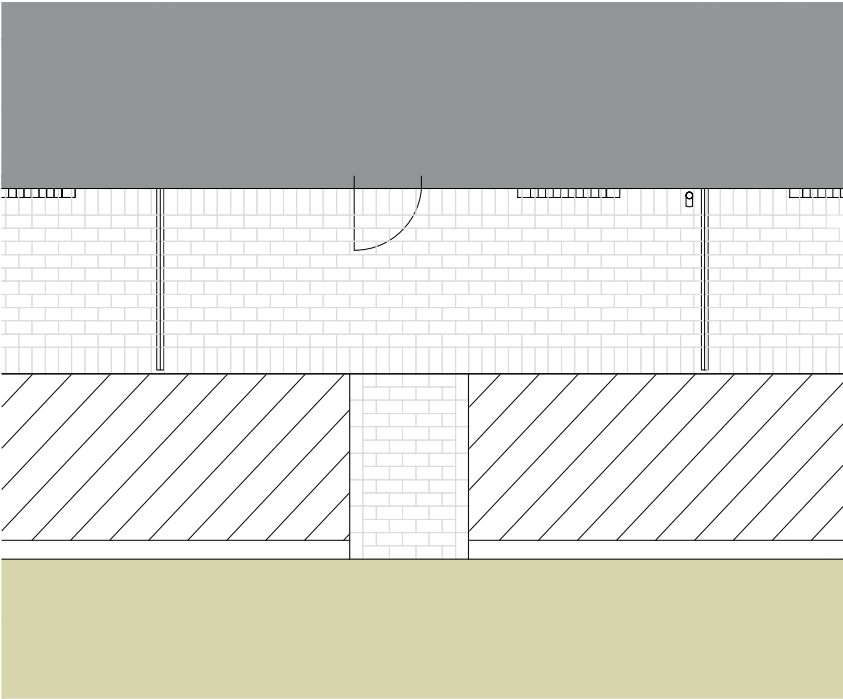

PRINCIP MÖNSTERLÄGGNING BETONGMARKSTEN P4

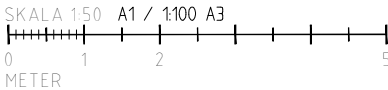

Lr 2181K-15/13.1

UTRUSTNING

- U1 CYKELSTÄLL Typ Nola Goggle cykelställ special 6cpt cc600 Standardkolor: RAL 9005
- U2 SKRAPGALLER Typ 2 st 1000X1000mm Weland Gallerdurk A33x11 art.nr: A0331125210100 Inklusive ingjutningsram. Ingjutningsram gjuts fast i betongram.
- U3 STOLPE MED SKYLTA PARKERING + RÖRELSEHINDRADE Skyltstolpe höjd 2m med skyltar i aluminium E19+T7. Inkl. nedgravningsfundament.

FÖRKLARINGAR


- ARBETSOMRÅDESGRÄNS Ritad 1 m utanför egentligt gräns.
- BEF MARKHÖJD SOM BEHÅLLS NY MARKHÖJD HÖJD FÄRDIGT GOLV
- NY ASFALTSYTA KÖRYTA I=545 mm 45 mm Slitlager asfalt AB111 160/220 80 mm Bärager 0-32 420 mm Förstärkningslager 0-90 Geotextil
- NY ASFALTSYTA, GC-TRAFIK I=205 mm 45 mm Slitlager asfalt AB111 160/220 160 mm Bärager 0-32 Geotextil
- NY GRÄSYTA, SÄDD I=150 mm Grässädd typ Weibulls Norr 2kg/100m2 150 mm Mineraljord typ A 200 mm luckrad terrass.

- NY ÄNGSYTA, SÄDD I=150 mm Ängssädd typ. Veglech Ängsfrö 6701 300g/100m2 med inblandning av Veglech Blomsteräkerfrö 6801 50g/100m2 150 mm Mineraljord typ A oögdostad 200 mm luckrad terrass.
- NY PLANTERINGSYTA, BUSKAR I=400 mm 400 mm typ Hasseltors trädgårdsjord B10 200 mm luckrad terrass
- NY PLANTERINGSYTA, TRÄD I=800 mm 400 mm typ Hasseltors trädgårdsjord B10 400 mm Mineraljord typ A 200 mm luckrad terrass
- NY PLANTERINGSYTA, SURJORD I=400 mm 400 mm typ Hasseltors Rhododendronjord 200 mm luckrad terrass

- P1 PLATTYTA, MOT HUSGRUND S.T ERIKS KLASSIK 350X350X40 NATURGRÅ 40 mm betongmarkplattor 30 mm Såltsand 80 mm Bärager 0-32 Geotextil
- P2 RÄNNALSPALTA, VID STUPRÖRSUTKASTARE S.T ERIKS RÄNNAL SUPER 350X350X52-65 TYP U, NATURGRÅ 52-65 mm Betongmarkplattor 30 mm Såltsand 80 mm Bärager 0-32 Geotextil
- P3 RÄNNALSPALTA S.T ERIKS RÄNNAL SUPER 350X350X52-65 TYP R, NATURGRÅ 52-65 mm Betongmarkplattor 30 mm Såltsand 80 mm Bärager 0-32 Geotextil

- P4 BETONGMARKSTEN S.T ERIKS KLASSIK 175X350X40 NATURGRÅ 52-65 mm Betongmarkplattor 30 mm Såltsand 80 mm Bärager 0-32 Geotextil
- G GRUSKROSS, EROSIONSSKYDD VID RÄNNALSPALTA 300 mm Makadam 16-32 Geotextil
- SR STÖDREMSA MOT ASFALTSYTA Bäragermaterial. Hl. intilliggande asfaltöverbyggnad läggs i nivå med asfalten.
- KS1 KANTSTÖD GRANIT, VISNINGSHÖJD 10cm KANTSTÖD DOPPAS
- DB1+00,00 NY DAGVATTENBRUNN

- BEL1 BELYSNINGSSTOLPE ENLIGT EL
- BEL2 POLLARBELYSNING ENLIGT EL
- + PLANTERING AV NYTT TRÄD
- S-A LÄGPNKTSLINJE FÖR YTVATTENAVRINNING
- S-U STUPRÖR SOM ANSLUTS PÅ DAGVATTENLEDNING
- MA STUPRÖR MED UTKASTARE
- MÅLNING AV ASFALT. EXTRUDERAD TRAFIKMASSA b=100mm

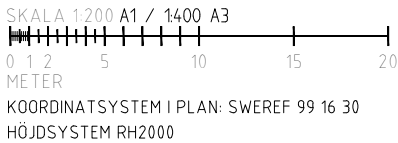

BET	ÄNDRINGEN AVISER	DATUM	SIGN
FÖRFRÅGNINGSUNDERLAG			
SANDVIKENS KOMMUN LASARETTET 110			
Sandvikens Kommun			
A	SKOOG	ARKITEKTER	tel. 026-62 40 30
L	SKOOG	ARKITEKTER	tel. 026-62 40 30
E	RAMBÖLL	SVERIGE AB	tel. 070-519 17 99
VVS	VVSS SYSTEMS		tel. 026-51 56 35
SP	BRIAB		tel. 0708-72 92 02
BR	BRIAB		tel. 076-832 57 01
UPPDRAG NR 23-221		RITAD/KONSTR. AV SH	HANDLÄGGARE SH
DATUM 2024-08-12		ANSVARIG SH	
LASARETTET 110 LÄKARSTIGEN MARKPLANERINGSPLAN GRUPPBOSTAD			
SKALA A1 1:200 A3 1400	NUMMER	L-30-1-01	
		BET	