


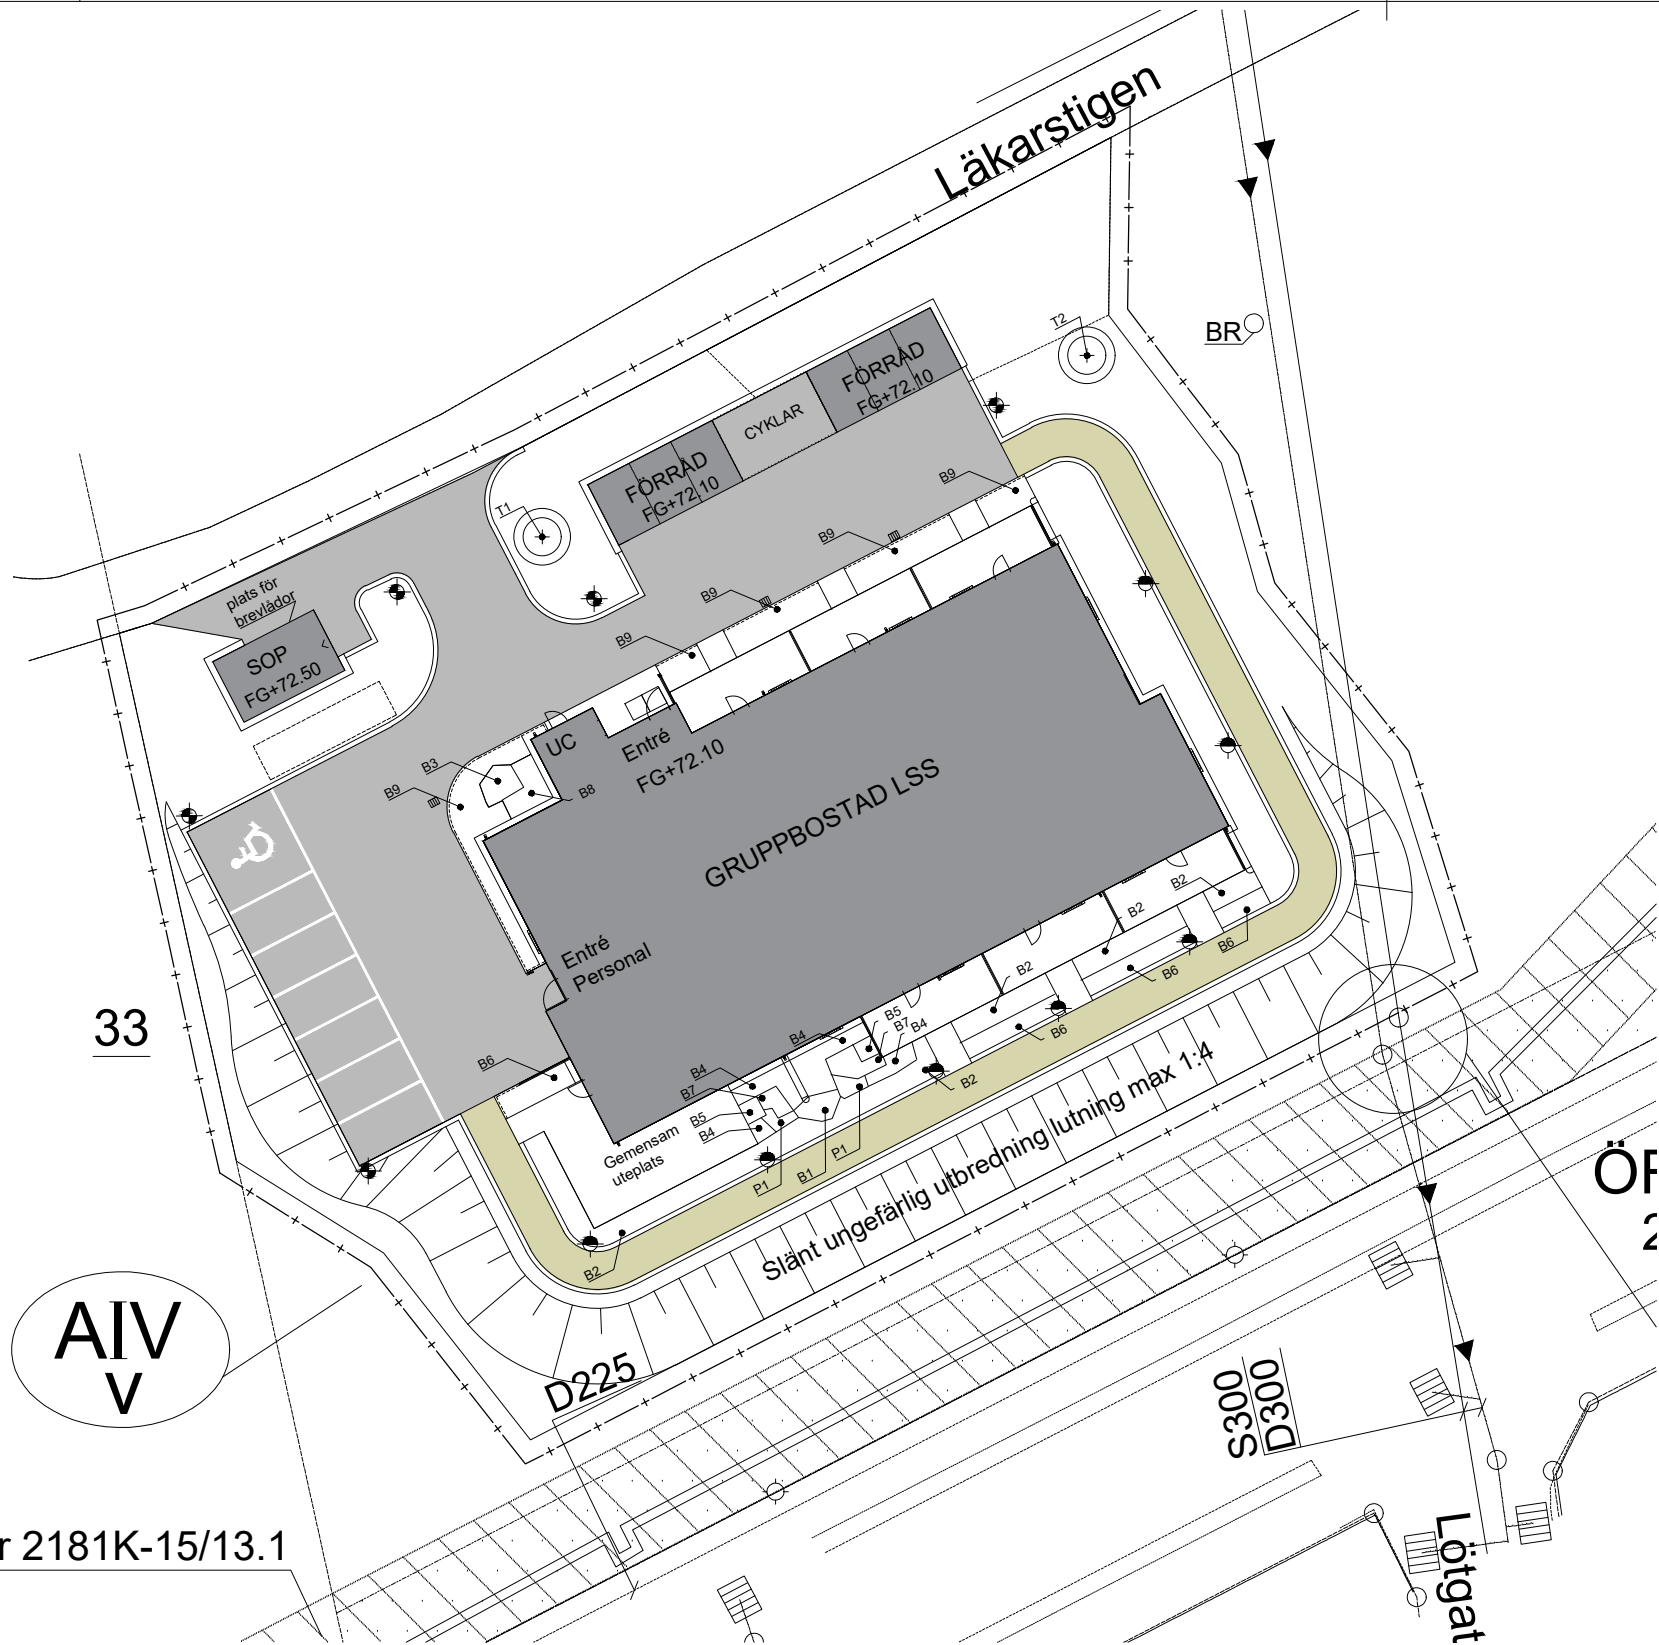

VÄXTFÖRTECKNING
TRÄD

ART	ANT.	VETENSKAPLIGT NAMN / SVENSKT NAMN	Zon	KVAL.	ANM.
T1	1	Malus 'Fredrik' E - Apple	Zon: 1-4	10-12	Träduppbindn. 1 m höjd, sadelgjord 3 rundstörar enligt typritning DDC11:2. Gnagskydd på stam min 150 cm högt
T2	1	Malus 'Cox Pomona' - Apple	Zon: 1-4	10-12	Träduppbindn. 1 m höjd, sadelgjord 3 rundstörar enligt typritning DDC11:2. Gnagskydd på stam min 150 cm högt
BUSKAR					
B1	5	Cytisus nigicans 'Cyni' - svartginsl	Zon: 1-5	Höjd: 0,8-1,2 m Bredd: 1-1,4 m	70 busk co 3,5 l
B2	137	Dasiphora 'Lemon Meringue' - gul ölandstok	Zon: 1-4	Höjd: 0,6-0,9 m Bredd: 0,6-0,9 m	60 busk co 3,5 l
B3	9	Hydrangea arborescens 'Annabelle' - vidjehortensia	Zon: 1-4	Höjd: 0,8-1,2 m Bredd: 1-1,4 m	60 busk co 3,5 l
B4	20	Hippophae rhamnoides 'Hikul' - Havtorn	Zon: 1-4	Höjd: 1-1,5 m Bredd: 1-1,5 m	80 busk co 3,5 l
B5	2	Hippophae rhamnoides 'Hillevi' - Havtorn	Zon: 1-4	Höjd: 1,4-1,6 m Bredd: 1,4-1,6 m	100 busk co 3,5 l
B6	26	Philadelphus 'Mont Blanc' - smulfronschersmin	Zon: 1-5	Höjd: 1-1,5 m Bredd: 1-2 m	70 busk co 3,5 l
B7	6	Pinus mugo var. pumilio FK Sauherad - balkanbergstall	Zon: 1-6	Höjd: 1-1,5 m Bredd: 2,2-5 m	100 co/kl, 40-50
B8	3	Rhododendron yak. 'Silberwolke' - Lågväxande rododendron	Zon: 1-4	Höjd: 0,8-1,2 m Bredd: 1,5 m	120 solitär 3x, kl 80-90
B9	65	Spiraea trilobata - sibirisk spirea	Zon: 1-6	Höjd: 0,5-1 m Bredd: 1-1,5 m	80 busk co 3,5 l
PRYDNADSGRÄS					
P1	4	Calamagrostis x acutiflora Karl Foester - tuvrör		100	A-kval, co

SKALA 1:200 A1 / 1400 A3
0 1 2 5 10 15 20
METER
KOORDINATSYSTEM I PLAN: SWEREF 99 16 30
HÖJDSYSTEM RH2000

BET	ÄNDRINGEN AVISER	DATUM	SIGN
FÖRFRÅGNINGSUNDERLAG			
SANDVIKENS KOMMUN LASARETTET 110			
 Sandvikens Kommun			
A	SKOOG	ARKITEKTER	tel. 026-62 40 30
X	L	SKOOG	ARKITEKTER tel. 026-62 40 30
E	RAMBÖLL SVERIGE AB		tel. 070-519 17 99
VVS	VVS SYSTEMS		tel. 026-51 56 35
SP	BRIAB		tel. 0708-72 92 02
BR	BRIAB		tel. 076-832 57 01
UPPDRAG NR 23-221	RITAD/KONSTR. AV SH	HANDLÄGGARE SH	
DATUM 2024-08-12	ANSVARIG SH		
LASARETTET 110 LÄKARSTIGEN PLANTERINGSPLAN GRUPPBOSTAD			
SKALA A1 1:200 A3 1400	NUMMER L-32-1-01	BET	