


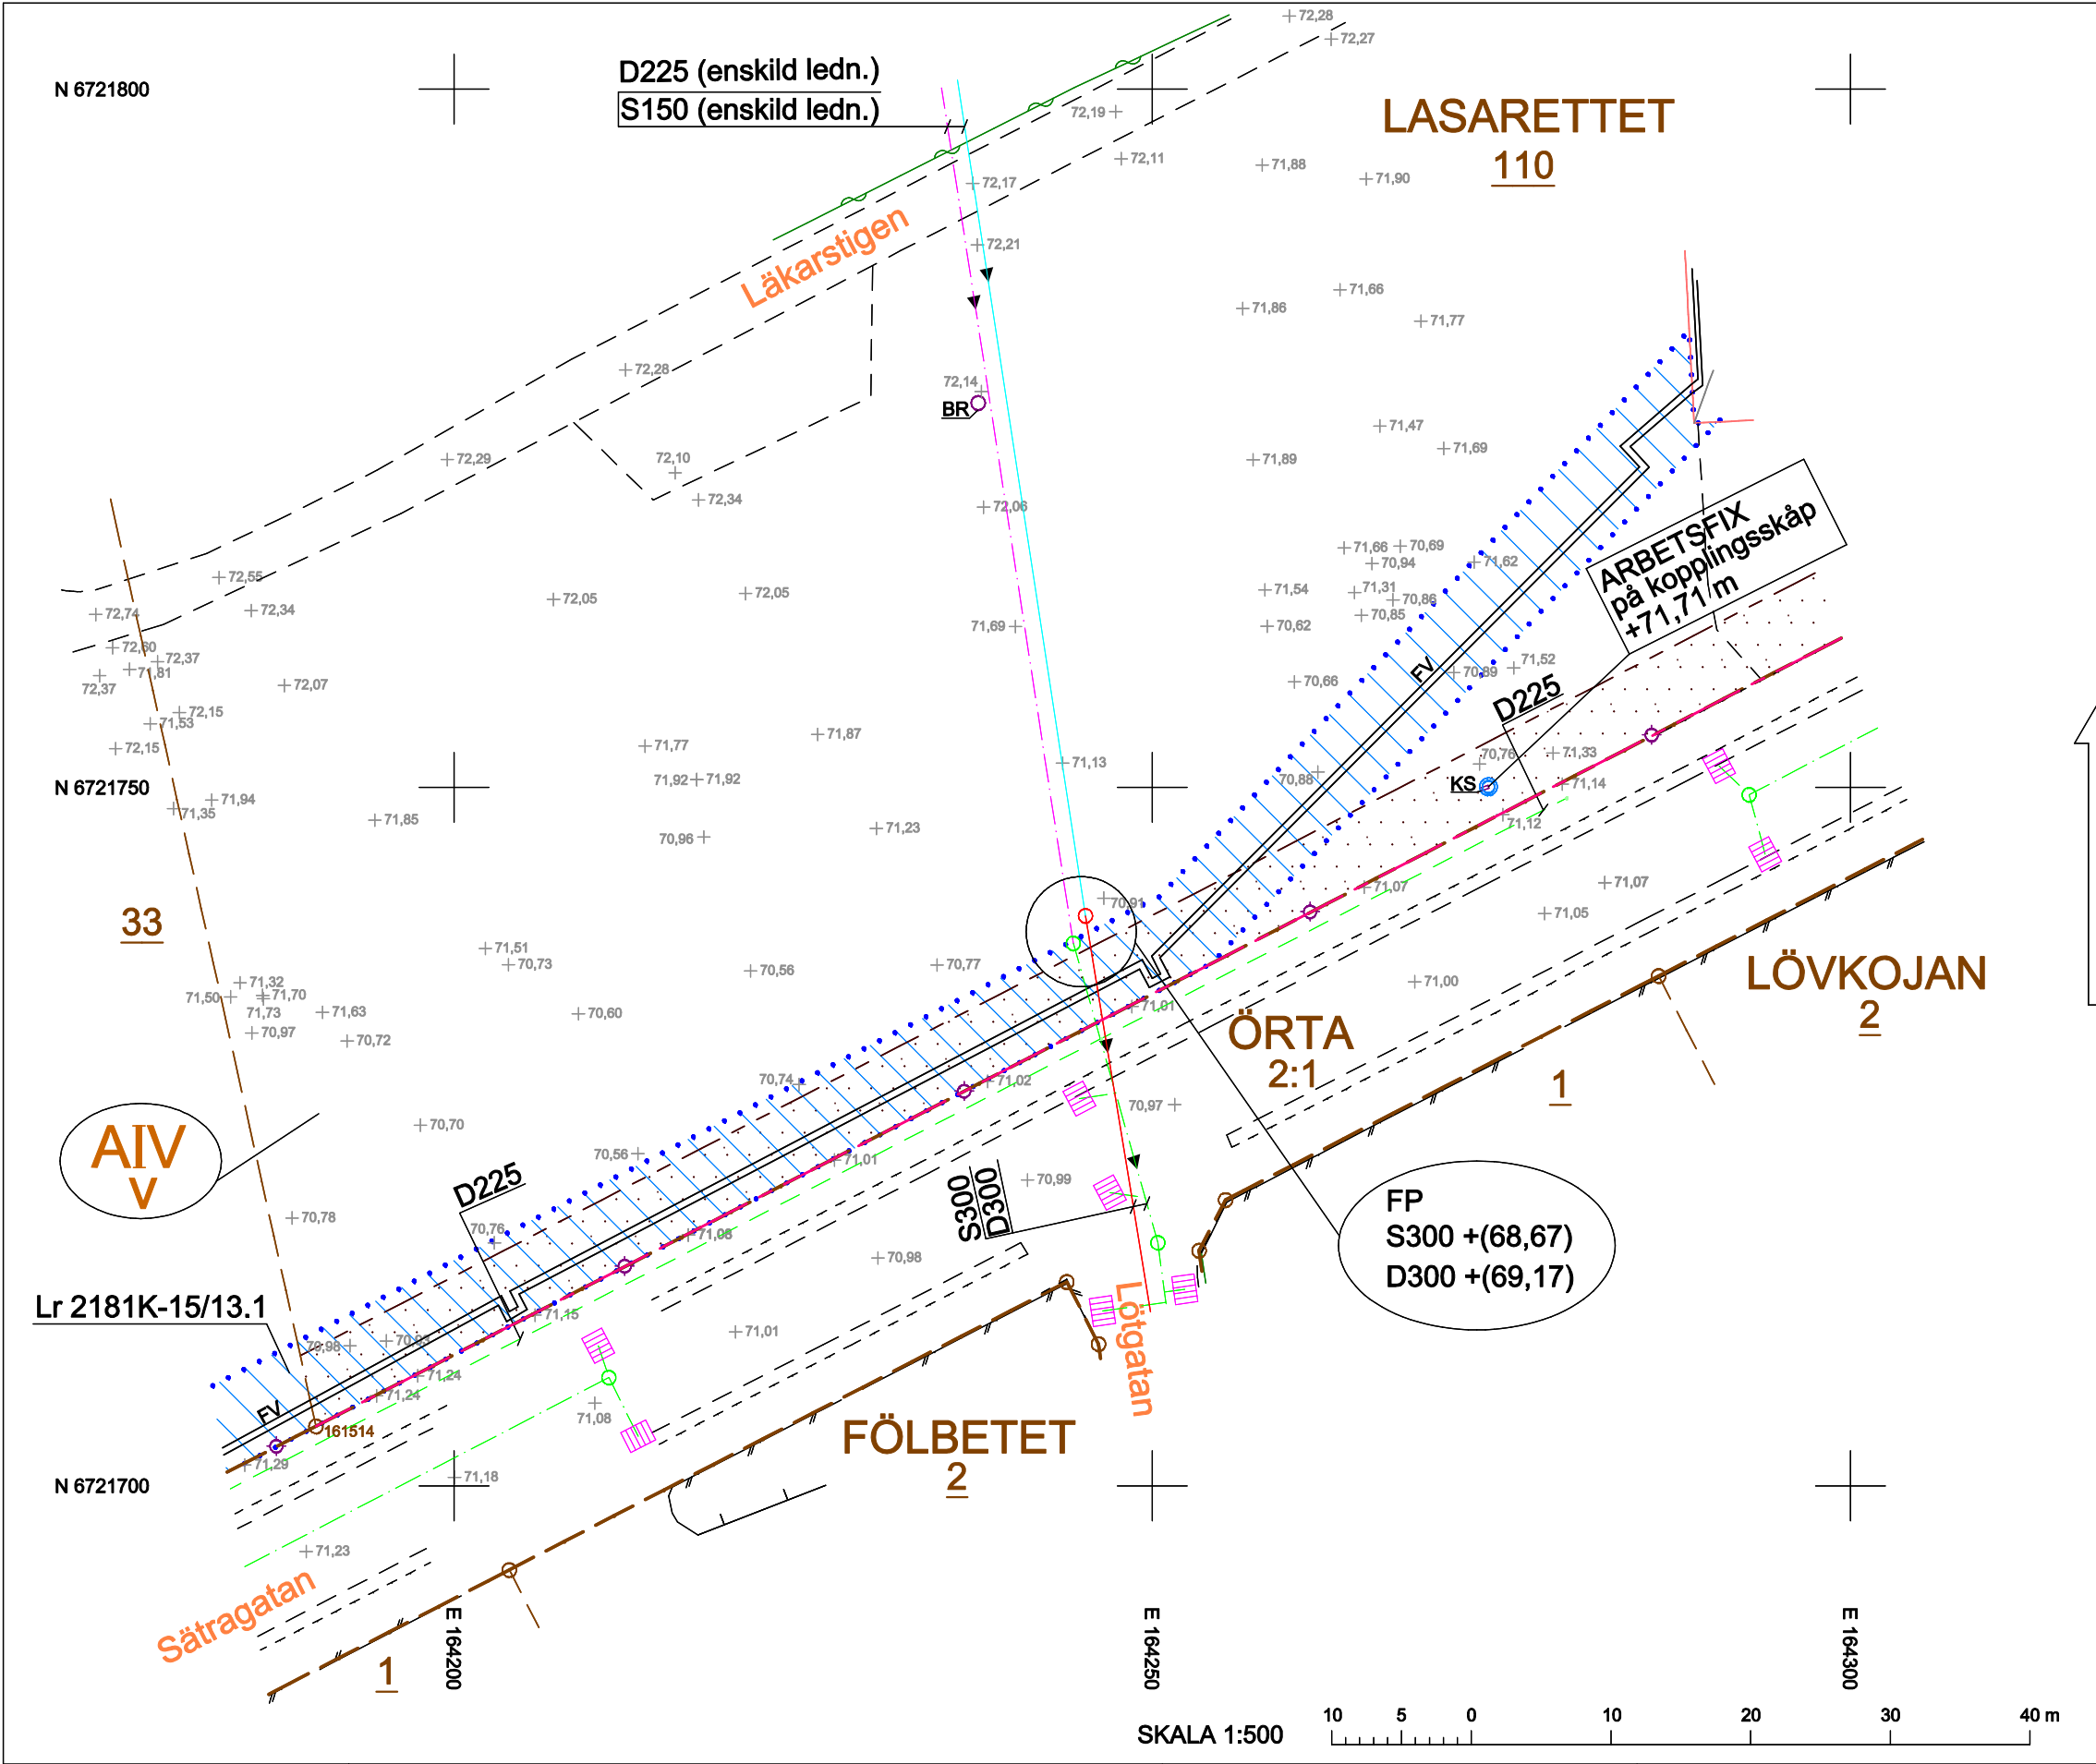

FORMAT **A3** DIARIENR **VGS-KL-2023-240**

Västra Gästriklands samhällsbyggnadsförvaltning
Kart- och lantmäterienheten
NYBYGGNADSKARTA

UPPRÄTTAD 2023-10-12
Nybyggnadskartan är giltig 2 år om inget ändrats i berört område.
Fastighetsägaren ansvarar för att meddela VGS att uppdatering av nybyggnads-
kartan behöver göras.

FASTIGHET
LASARETTET 110

KOMMUN HOFORS ☐ OCKELBO ☐ SANDVIKEN ☒

PRELIMINÄR ADRESS
Läkarstigen 7
811 60 Sandviken

FASTIGHETENS
(TOMTENS) AREA
M² 22010

MARKREGLERANDE BESTÄMMELSER
Detaljplan ☒ 1948-03-05 akt 2181-1484
Områdesbestämmelser ☐
Utom planområde ☐

Berört område ligger inom skyddsområde för vattentäkt
Ja: ☐ Nej: ☒

FASTIGHETSÄTTSLIG STATUS
Fastigheten överensstämmer med detaljplan
Ja: ☒ Nej: ☐

Gränserna på denna karta är redovisade enligt
senaste förrättningar, akt 2181K-08/34

TECKENFÖRKLARING

Traktgräns eller kvartersgräns
Fastighetsgräns
Rättighetsyta
Samhällsfunktion (fasad)
Väg/kantsten
Gång och cykelbana
Staket
Häck
Stödmur
KÖLNAN Traktnamn eller kvartersnamn
3:7 Registerbeteckning för fastighet med traktnamn
2 Registerbeteckning för fastighet med kvartersnamn
Lr Ledningsrätt
+ Koordinatkryss
145312 Gränspunkt med gränspunktsnummer
73,25 Belysningsstolpe
BR Befintlig markhöjd
BR Brunn
KS Kopplingskåp
Spillvatten, S
Dagvatten, D
Spillvatten, S (enskild ledn.)
Dagvatten, D (enskild ledn.)
Fjärrvärme, FV

För fullständig detaljplaneinformation och dess teckenförklaring, se gällande
detaljplan

Markdetaljer kontrollerade: 2023-10-04

Mätosäkerhet i plan för berörd fastighet: +/- 50 mm
Mätosäkerhet i höjd för berörd fastighet: +/- 50 mm

Koordinatsystem i plan: SWEREF 99 16 30
Koordinatsystem i höjd: RH 2000

Upprättad av : **ALB** Granskning: **JEB** Markkontroll och mätning: **PEOL**

På kartan redovisas följande ledningar i
mark, om de finns i berört område:
• Fjärrvärme
• Kommunala VA-ledningar
Andra ledningar i mark redovisas ej, om
inte annat anges.
Mer information om ledningar kan fås via
www.ledningskollen.se

Förbindelsepunkter, FP, till kommunala ledningar:
vatten, V, ☐ befintlig tryckledning, T, ☐ befintlig
spillvatten, S, ☒ befintlig dagvatten, D, ☒ befintlig ☐ omhändertas lokalt
+ (0,00) Befintligt eller planerat avlopps höjdläge. Dagvattnets däckningsnivå = markyta

Uppgifter om VA-ledningar:
SANDVIKEN ENERGI VATTEN, AB
2023-09-27 Mats Eriksson
Befintliga kommunala- och enskilda ledningar
redovisas. Observera att enskilda ledningar går igenom
berörd fastighet.
För förfrågan om anslutning till befintligt ledningsnät,
kontakta Sandviken Energi Vatten AB, tel 026-24 16 00

Uppgifter om fjärrvärme:
SANDVIKEN ENERGI AB, VÄRME
2023-10-02
Befintliga fjärrvärmeledningar redovisas.
Befintlig anslutning finns inte. Förfrågan om möjlighet
att ansluta till befintligt fjärrvärmenät, kontakta
Sandviken Energi AB, Värme, tel 026-24 16 00