

FÖRRÅD

FÖRRÅD

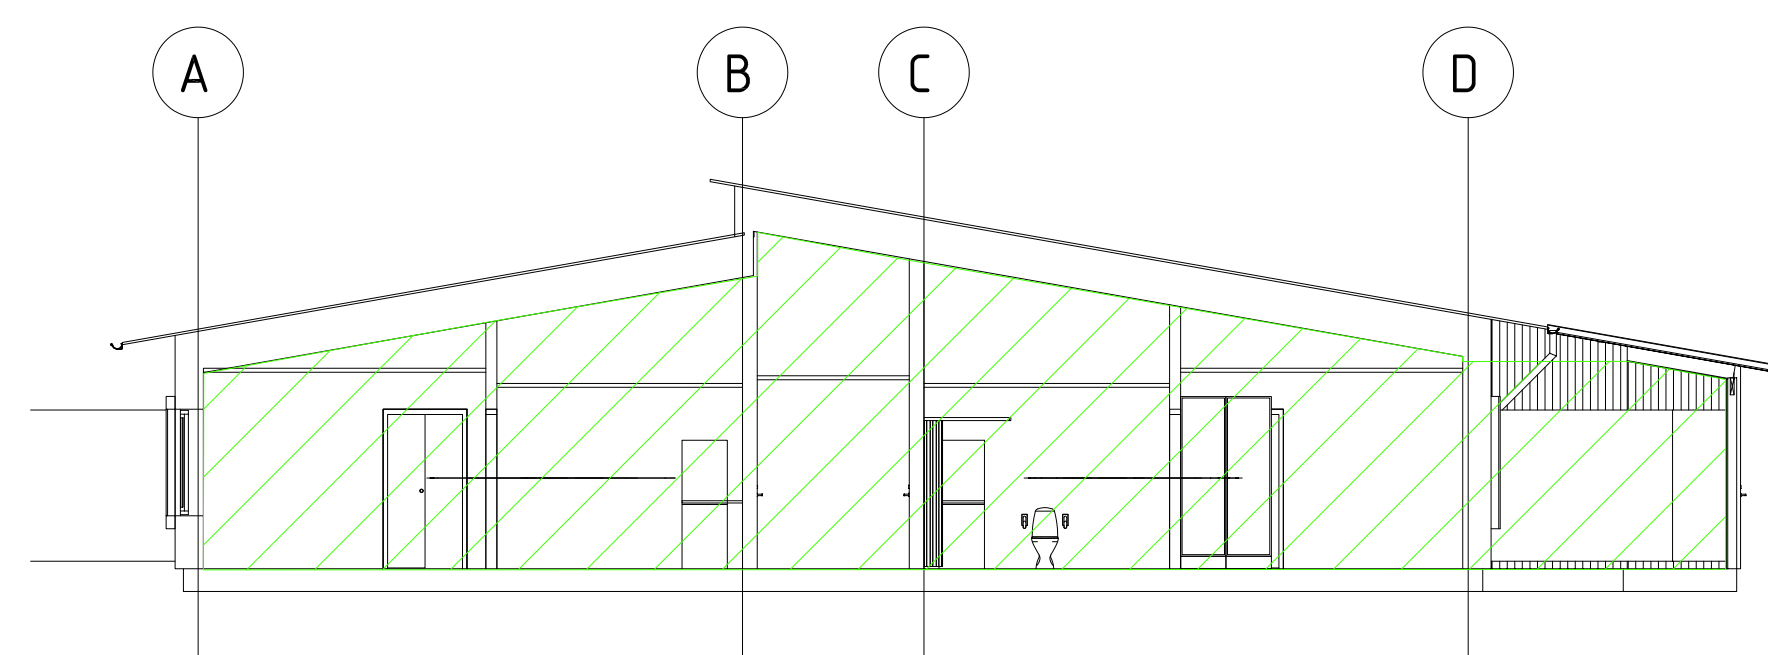
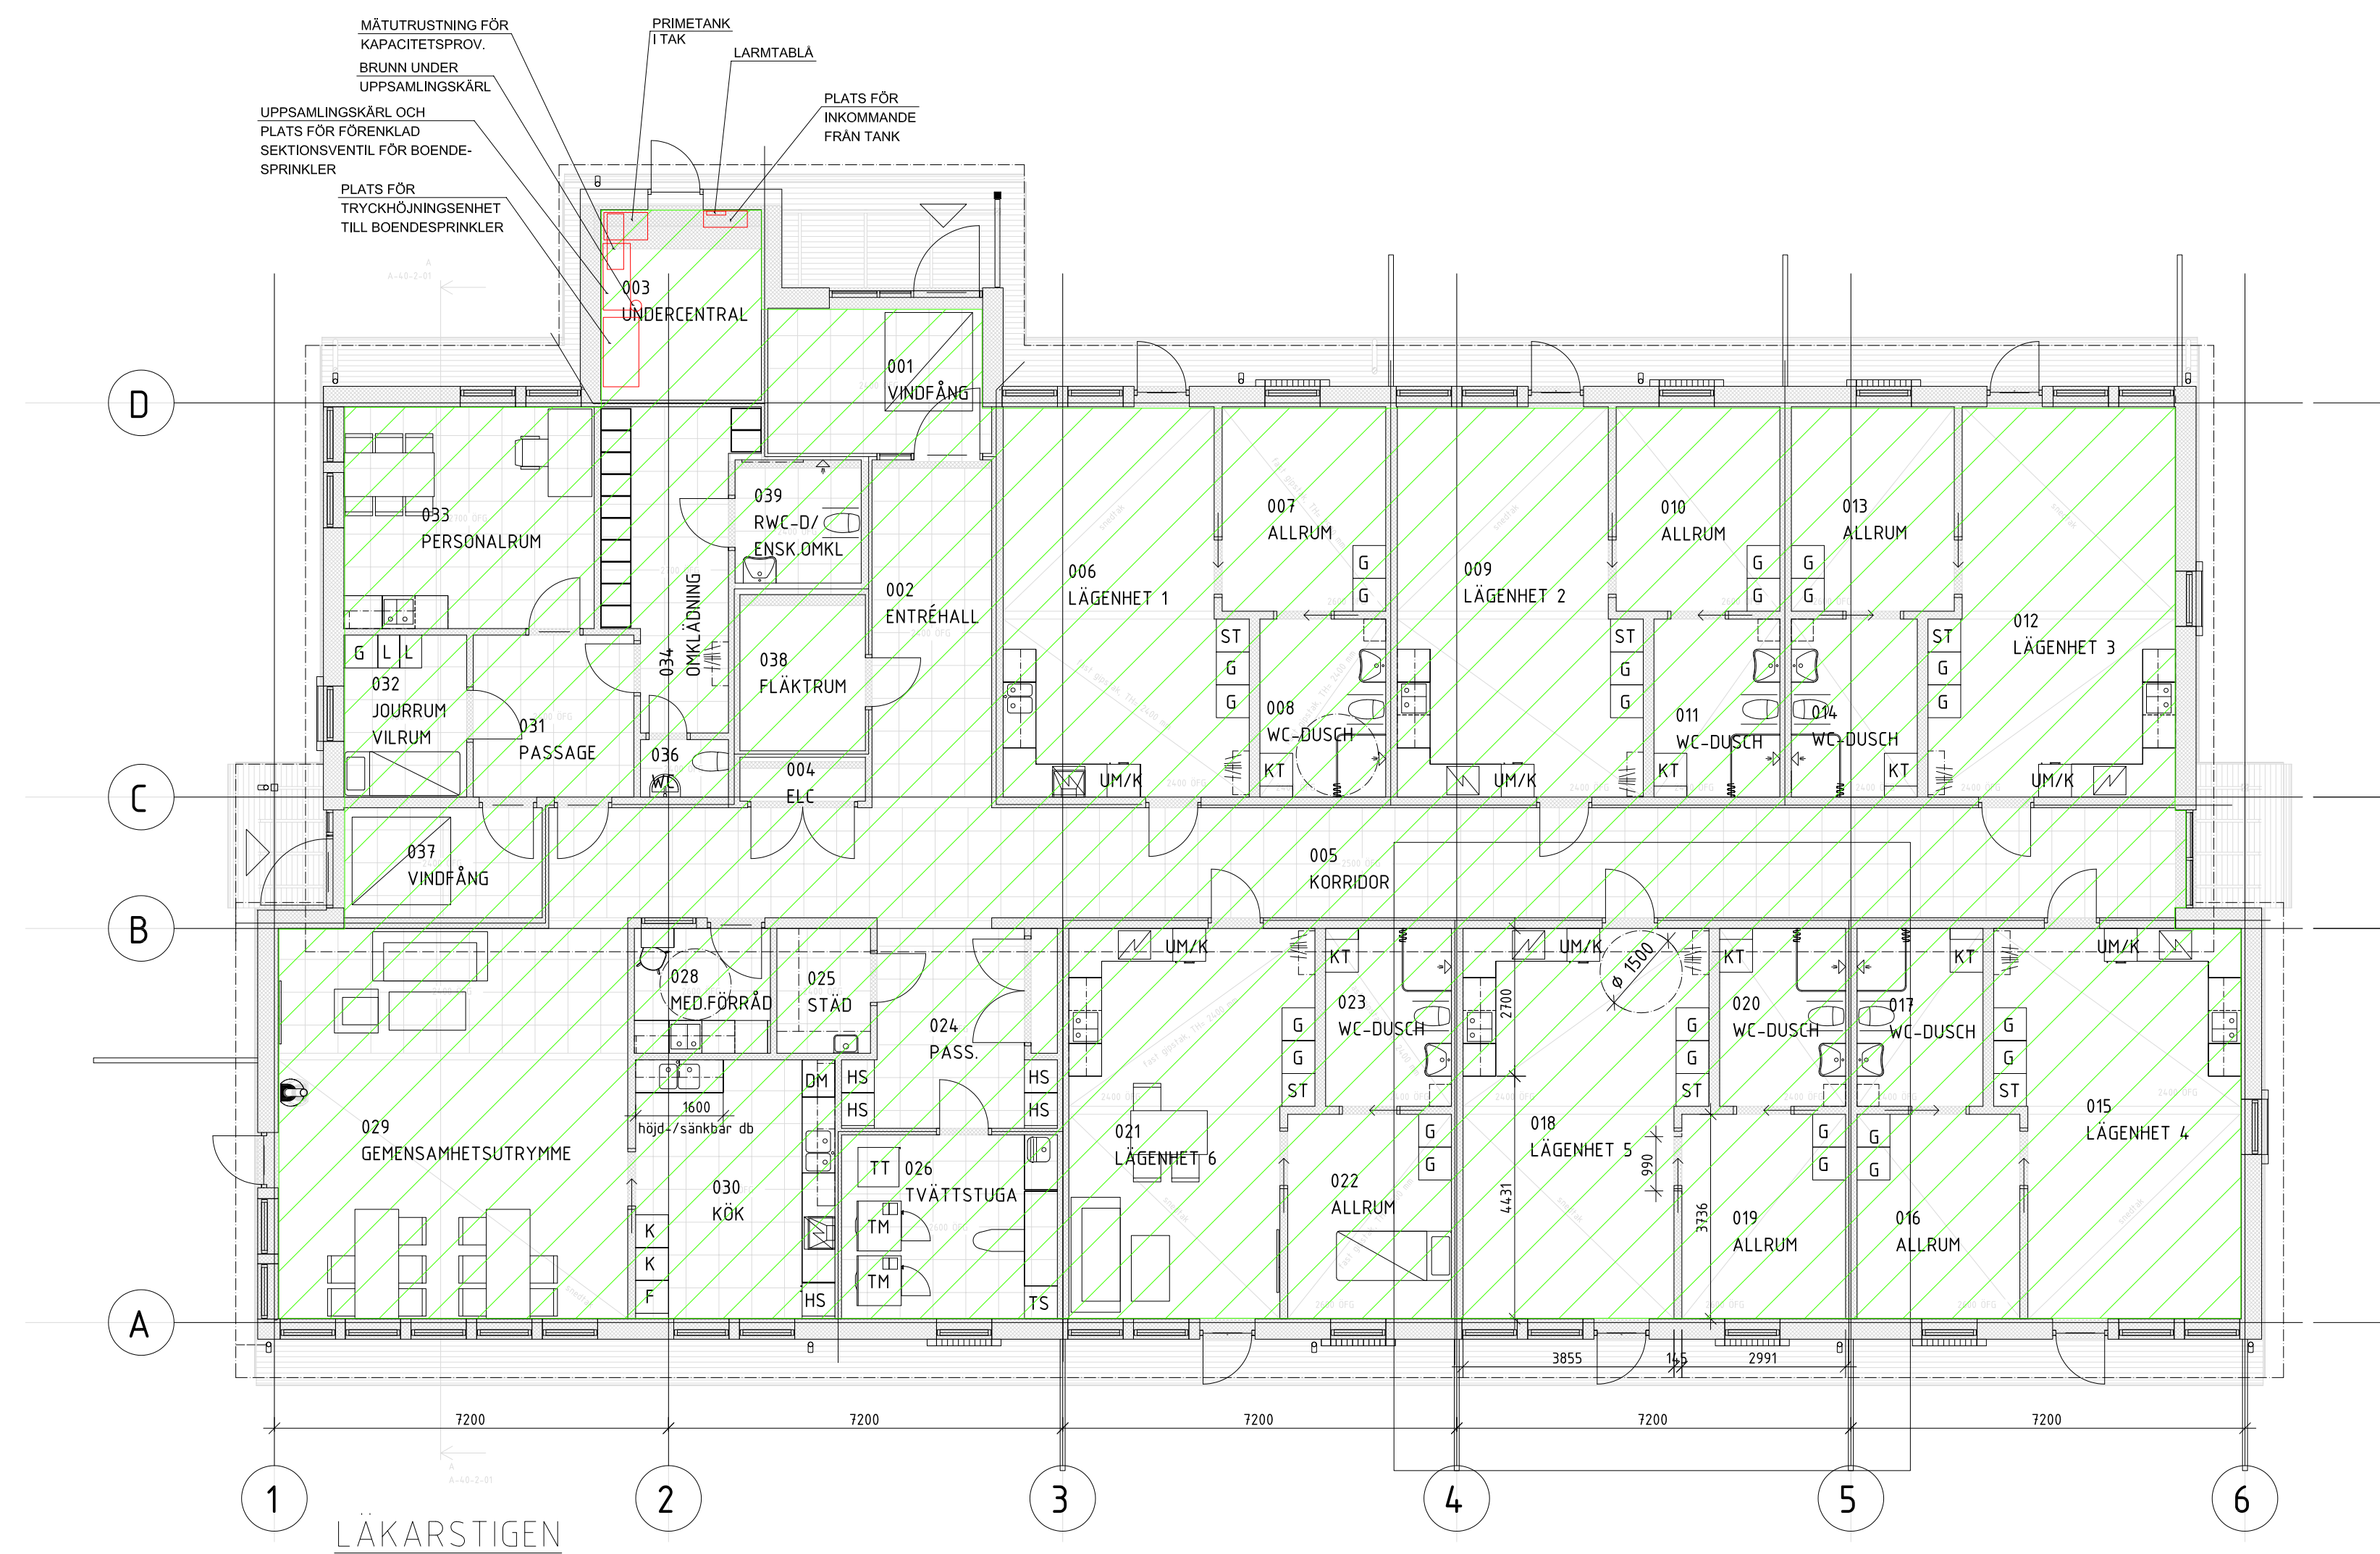
FÖRRÅD

SPRINKLERTANK

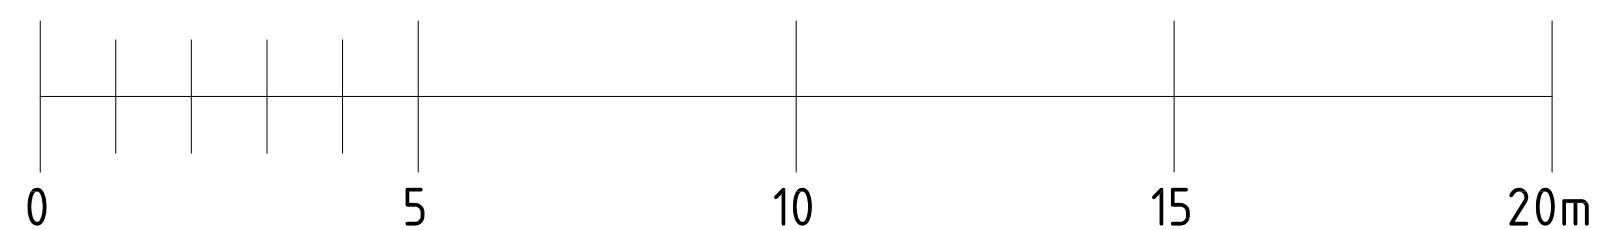
ANVISNINGAR

Installationsanvisningar och regelverk:
Installationen ska utföras i enlighet med
SS-EN 16925:2018.

Risiklass Boendesprinkler typ 3:
4 st sprinkler@ 4,1 mm/min,m2

 Yta som sprinklas.

METER



SKALA 1:100

BET	ÄNDRINGEN AVSER	DATUM	SIGN
-----	-----------------	-------	------

FÖRFRÅGNINGSUNDERLAG

SANDVIKENS KOMMUN
LASARETTET 110



A	SKOOG	ARKITEKTER	tel. 026-62 40 30
L	SKOOG	ARKITEKTER	tel. 026-62 40 30
E	RAMBÖLL SVERIGE AB		tel. 070-519 17 99
	VVS VVSS SYSTEMS		tel. 026-51 56 35
X	SP	BRIAB	tel. 0708-72 92 02
	BR	BRIAB	tel. 076-832 57 01

IFFORDPARK 2402061	RETAKONSTR. AV A-L P	HANDELSGÅRDE A-L P
DATUM 2024-08-12	ANSVARIG MST	
LASARETTET 110 LÄKARSTIGEN SPRINKLER LSS-BOENDE		
BEKVAL A1 1:100 A3 1:200	NUMMER SP54.1-01	BET