
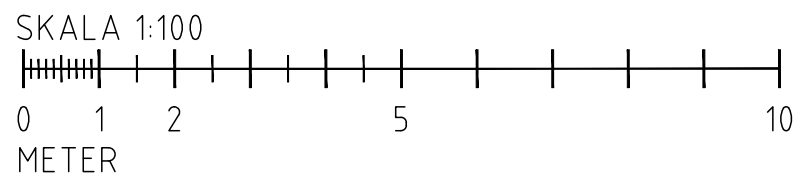


XREF: ..\Komplementfil\slipstext1 rör ovan bjälklag.dwg; ..\..\LA Modell\A40-P10_Vallhov.dwg

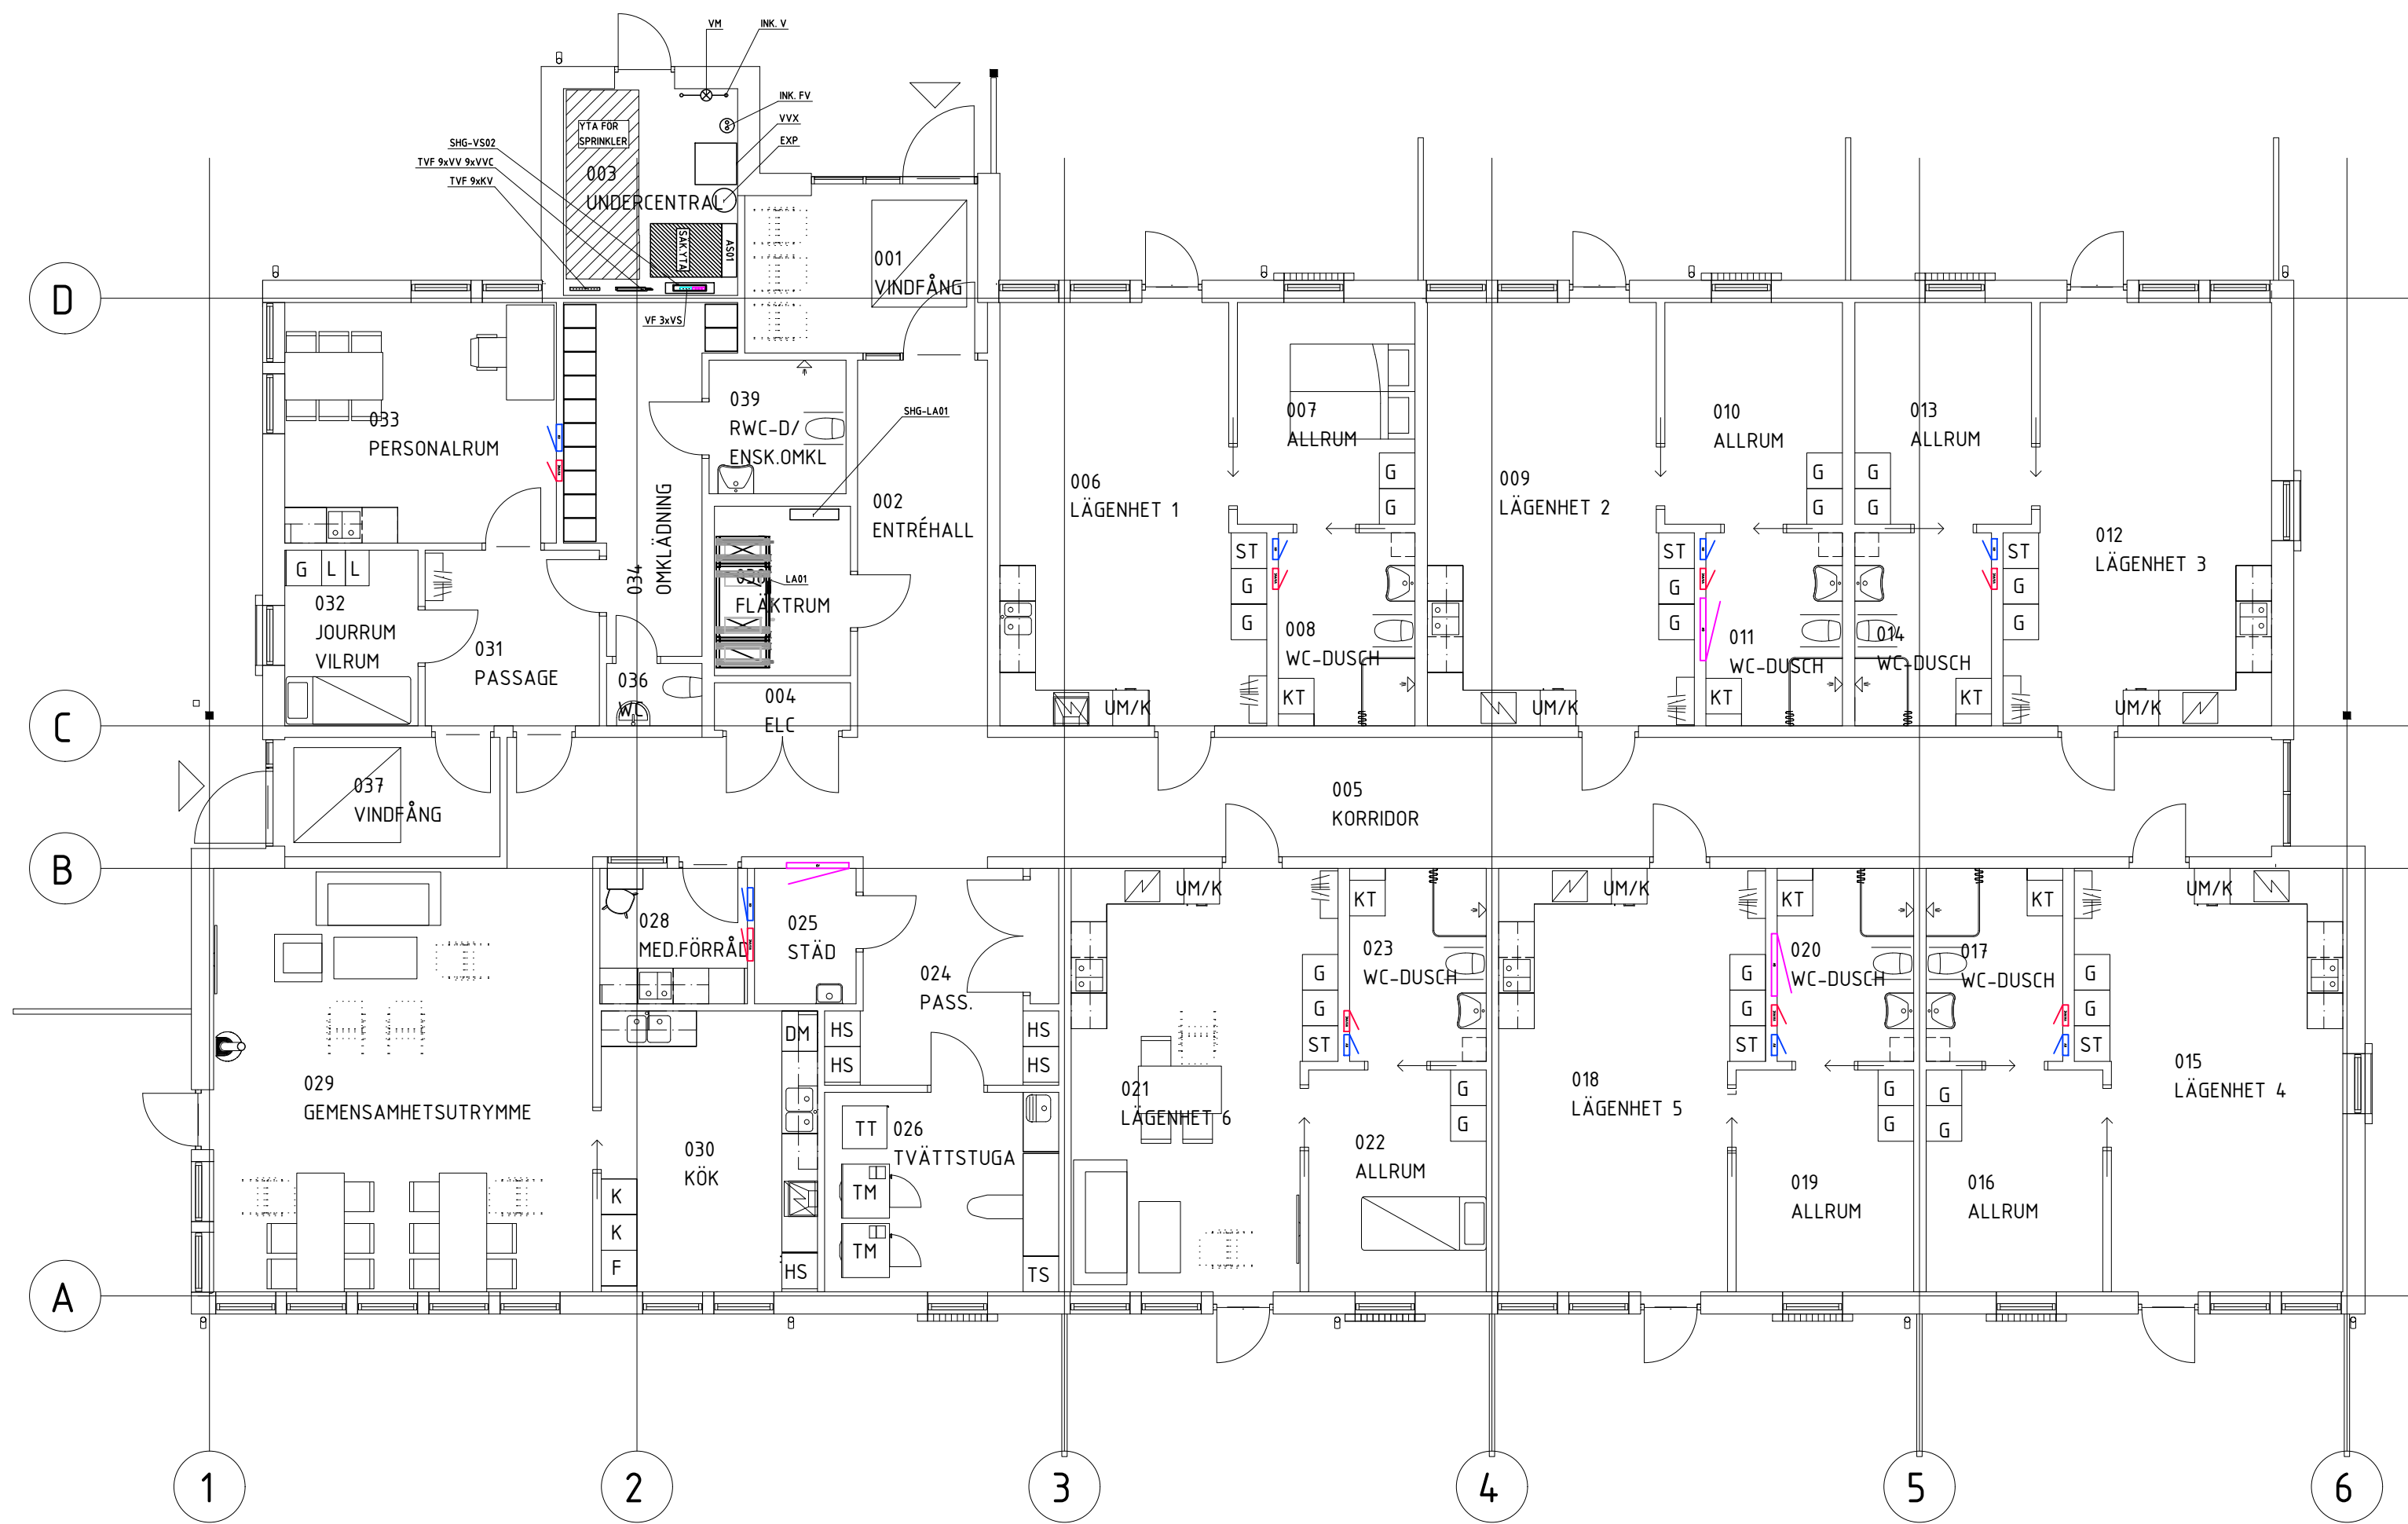

FÖRKLARINGAR:

- FÖRSLAG PÅ PLACERING AV FÖRDELARSKÅP GOLVVÄRME
- FÖRSLAG PÅ PLACERING AV FÖRDELARSKÅP KALLVATTEN
- FÖRSLAG PÅ PLACERING AV FÖRDELARSKÅP VARMVATTEN

BET	ÄNDRINGEN AVSER		DATUM	SIGN
FÖRFRÅGNINGSUNDERLAG				
SANDVIKENS KOMMUN LASARETTET 110				
 Sandvikens Kommun				
A	SKOOG	ARKITEKTER	tel. 026-62 40 30	
L	SKOOG	ARKITEKTER	tel. 026-62 40 30	
E	RAMBÖLL	SVERIGE AB	tel. 070-519 17 99	
☒	VVS	VVSS SYSTEMS AB	tel. 026-51 56 35	
SP	BRIAB		tel. 0708-72 92 02	
BR	BRIAB		tel. 076-832 57 01	
UPPRAG NR 2415		RITAD/KONSTR. AV LaB	HANDLÄGGARE LaB	
DATUM 2024-08-12		ANSVARIG Lars Berthilsson		
LASARETTET 110 VALLHOVSGLÄNTAN PLAN 1 LUFTBEHANDLINGSSYSTEM				
SKALA A1 1:100 A3 1:200	NUMMER V-57-1-100		BET	

