



XREF:

LAGER: SB11

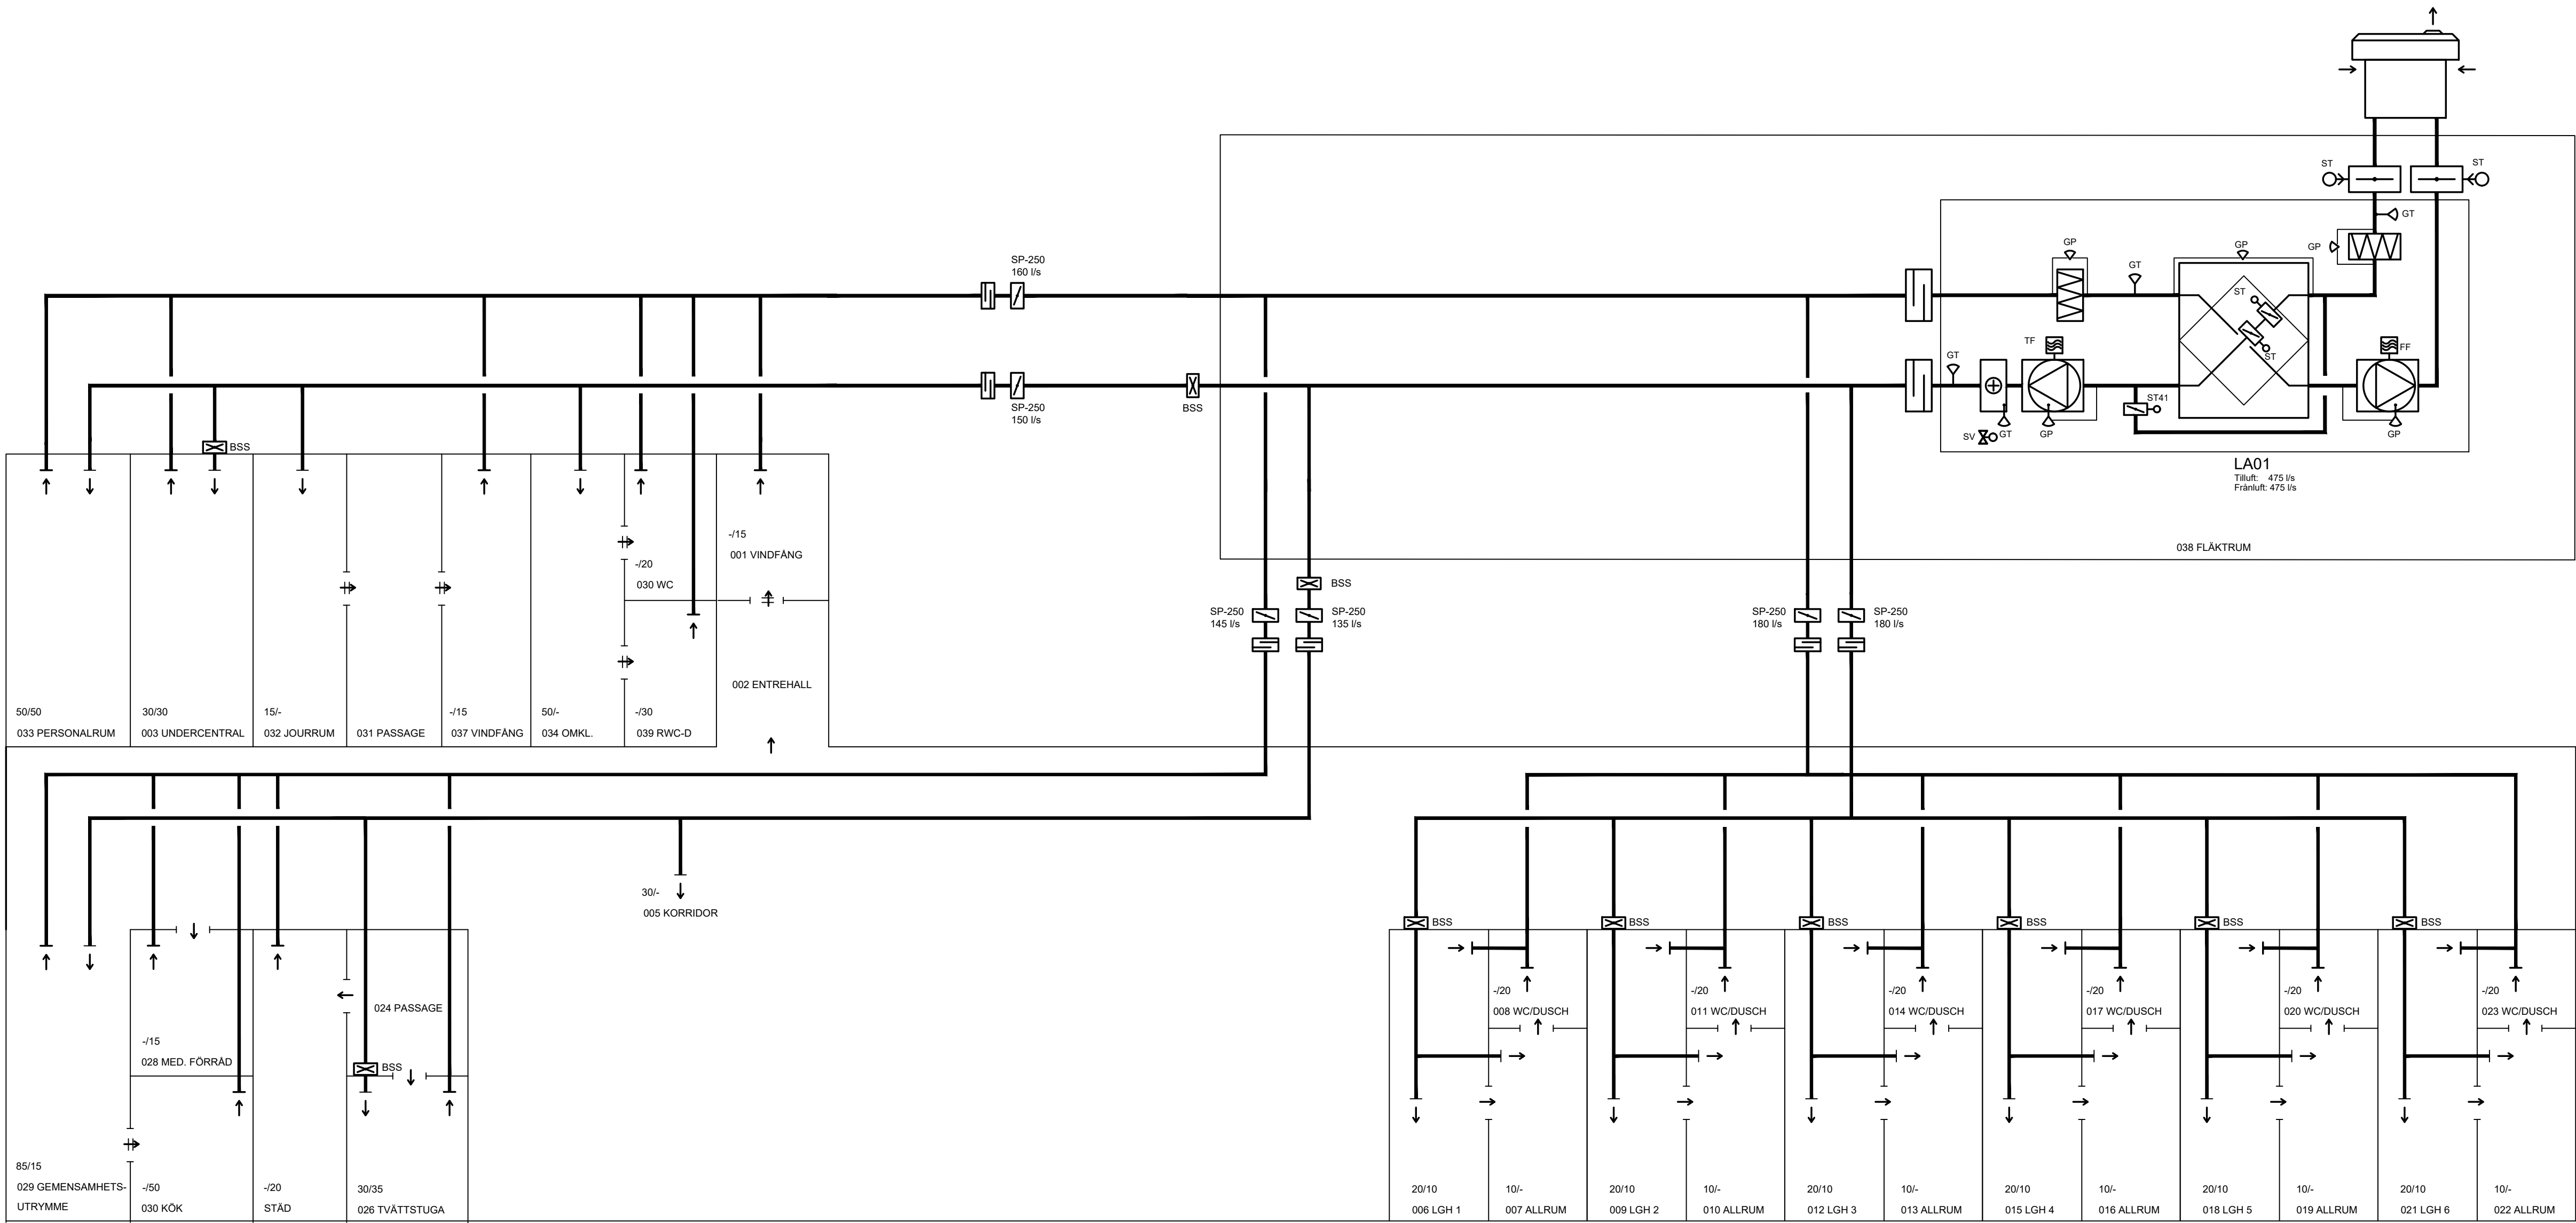

FÖRKLARINGAR:

- TF, TILLUFSFLÄKT
FF, FRÄNLUFSFLÄKT
- FO, FREKVENSONFORMARE
- LUFTVÄRMARE
- LUFTKYLARE
- VÄRMEÅTERVINNARE, RÖTERANDE
- VÄRMEÅTERVINNARE, MOTSTRÖM
- LF, LUFTFILTER
- SP, INJUSTERINGSSPÄLL
- AVSTÄNGNINGSSPÄLL, REGLERANDE
- AVSTÄNGNINGSSPÄLL, SPÄNNINGSLÖST STÄNGT
- KFD, KONSTANTFLÖDESDON
VFD, VARIABELFLÖDESDON
- BST, BRANDGASSPÄLL, SPÄNNINGSLÖST STÄNGT
BST, BRAND-/BRANDGASSPÄLL, SPÄNNINGSLÖST STÄNGT
- TRYCKAVLASTNINGSSPÄLL, SPÄNNINGSLÖST ÖPPET
- BSS, BACKSPÄLL
- LD, LUDDÄMPARE
- YG, YTTERVÄGGSGALLER
- TD, TILLUFTSDON
- FD, FRÄNLUFTSDON
- ÖD, ÖVERLUFTSDON
- GT, GIVARE TEMPERATUR
GP, GIVARE TRYCK
GF, GIVARE FLÖDE
GQ, GIVARE KONCENTRATION
- SV, STYRVENTIL MED STÄLLDON, 2-VÄGS

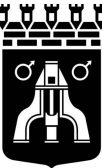BET	ÄNDRINGEN AVSER	DATUM	SIGN
FÖRFRÅGNINGSUNDERLAG			
SANDVIKENS KOMMUN LASARETTET 110			
 Sandvikens Kommun			
A	SKOOG	ARKITEKTER	tel. 026-62 40 30
L	SKOOG	ARKITEKTER	tel. 026-62 40 30
E	RAMBÖLL	SVERIGE AB	tel. 070-519 17 99
X	VVS	VVSS SYSTEMS AB	tel. 026-51 56 35
SP	BRIAB		tel. 0708-72 92 02
BR	BRIAB		tel. 076-832 57 01
UPPRAG NR 2415			
RITAD/KONSTR. AV LaB		HANDLÄGGARE LaB	
DATUM 2024-08-12		ANSVARIG Lars Berthilsson	
LASARETTET 110 VALLHOVSGLÄNTAN FLÖDESSKEMA LUFTBEHANDLINGSSYSTEM			
SKALA A1 - A3 -	NUMMER V-57-8-001	BET	



ORIGINALFORMAT: A1

X:\PROJEKT\2415- VALLHOVSGLÄNTAN LSS SHIRTINGAR\V\MODELL\TKARSTIGEN\V-57-8-001.DWG LASSE