
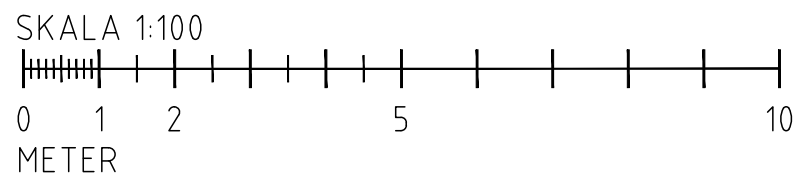


XREF: ..\Komplementfil\slipstext1 rör ovan bjälklag.dwg: ..\..\LA Modell\A40-P10_Vallhov.dwg

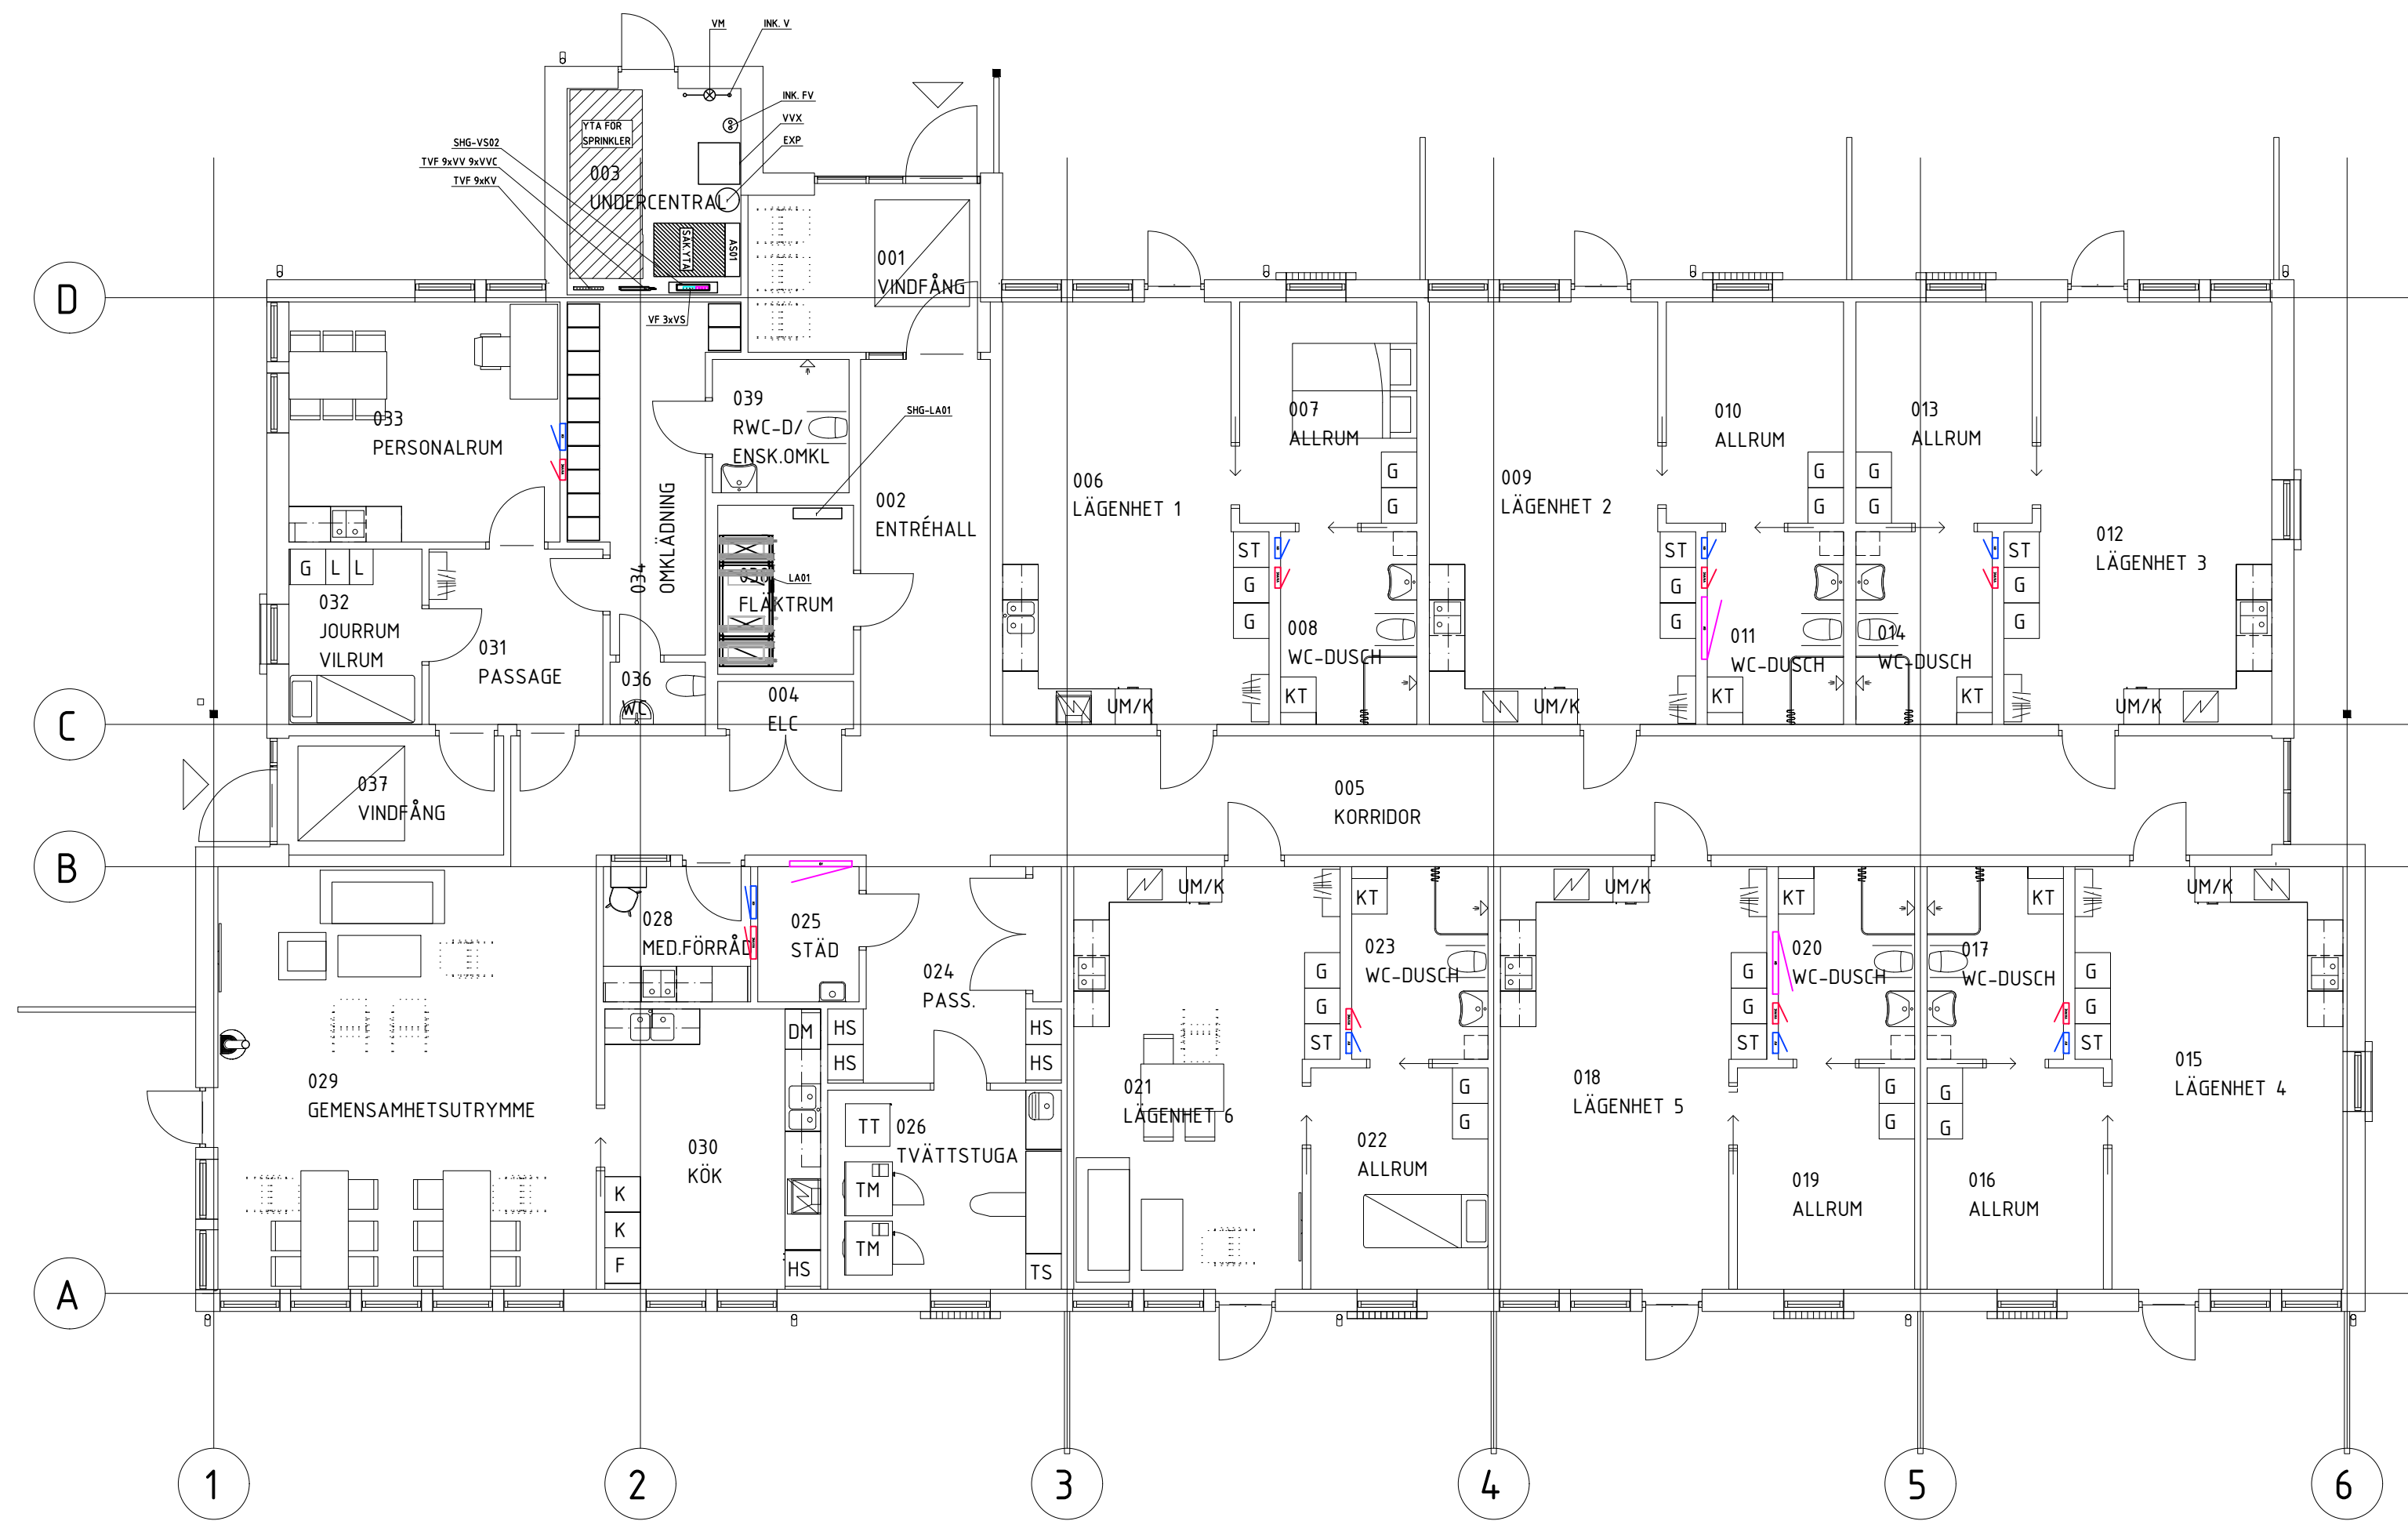

FÖRKLARINGAR:

- FÖRSLAG PÅ PLACERING AV FÖRDELARSKÅP GOLVVÄRME
- FÖRSLAG PÅ PLACERING AV FÖRDELARSKÅP KALLVATTEN
- FÖRSLAG PÅ PLACERING AV FÖRDELARSKÅP VARMVATTEN

BET		ÄNDRINGEN AVSER		DATUM		SIGN	
FÖRFRÅGNINGSUNDERLAG							
SANDVIKENS KOMMUN LASARETTET 110							
				Sandvikens Kommun			
A		SKOOG		ARKITEKTER		tel. 026-62 40 30	
L		SKOOG		ARKITEKTER		tel. 026-62 40 30	
E		RAMBÖLL		SVERIGE AB		tel. 070-519 17 99	
☒		VVS		VVSS SYSTEMS AB		tel. 026-51 56 35	
SP		BRIAB				tel. 0708-72 92 02	
BR		BRIAB				tel. 076-832 57 01	
UPPRAG NR 2415				RITAD/KONSTR. AV LaB		HANDLÄGGARE LaB	
DATUM 2024-08-12				ANSVARIG Lars Berthilsson			
LASARETTET 110 LÄKARSTIGEN PLAN 1 RÖRSYSTEM							
SKALA A1 1:100 A3 1:200		NUMMER W-50-1-100				BET	

