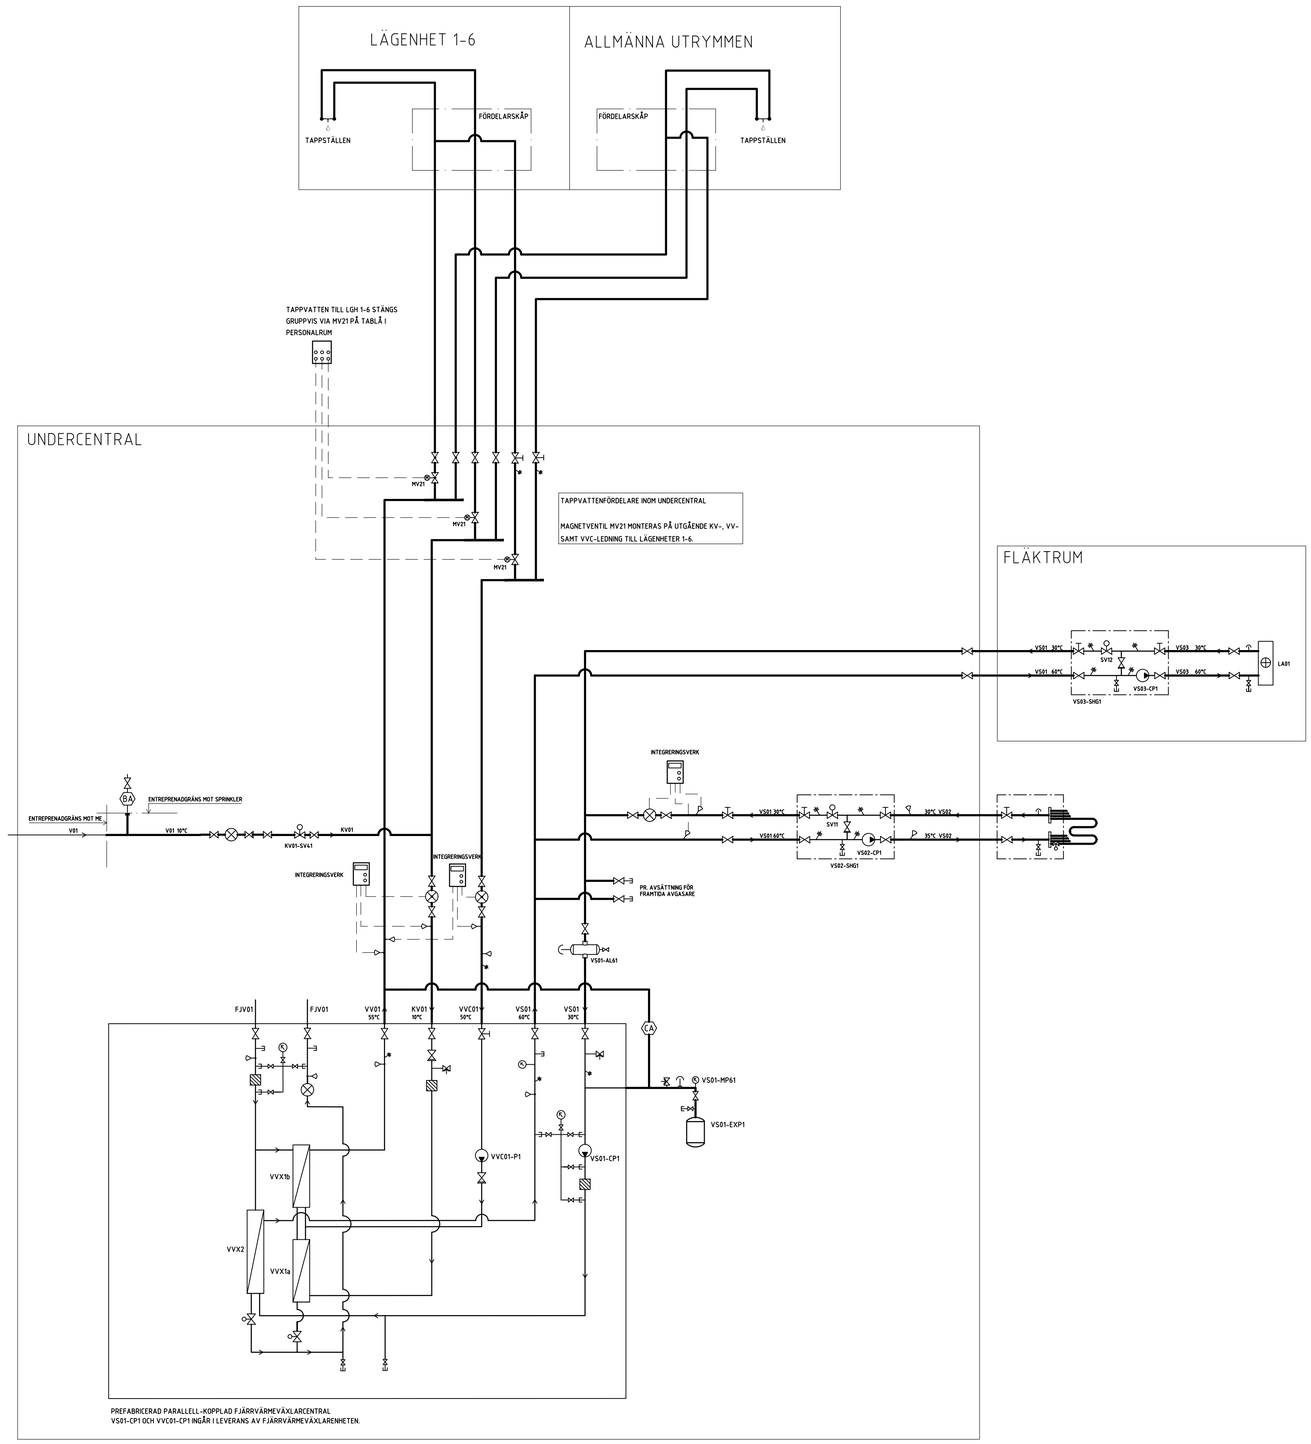


SYSTEMBET. / MEDIA

VO1	KALLVATTENLEDNING (OMÄTT)
KV01	KALLVATTEN, SYSTEMTEMPERATUR CA +10° C
VV01	VARMVATTEN, SYSTEMTEMPERATUR CA +55° C
VVC01	VARMVATTENCIRKULATION, SYSTEMTEMPERATUR CA +50° C
FJV01	FJÄRRVÄRME SYSTEMTEMPERATUR VINTER +100/43°C SOMMAR +65/22°C
VS01	VÄRME SEKUNDÄR,SYSTEMTEMPERATUR +60°C/~+30°C (VID DUT)
VS02	VÄRME SEKUNDÄR, SHUNTAT GOLVVÄRME SYSTEMTEMPERATUR +35°C/+30°C (VID DUT)
VS03	VÄRME SEKUNDÄR, SHUNTAT LUFTBEHANDLINGSAGGREGAT LA01 SYSTEMTEMPERATUR +60°C/+30°C (VID DUT)

SYSTEMBET./SYMBOL/ FÖRKLARING

- AVSTÄNGNINGSVENTIL
- AVSTÄNGNINGS-/INJUSTERINGSVENTIL
- STYRVENTIL, REGLERANDE MED STÄLLDON ENLIGT SÖE
- MAGNETVENTIL
- BACKVENTIL
- SÄKERHETSVENTIL/DN/ÖPPNINGSTRYCK (BAR)
- AVTAPPNINGSVENTIL
- AVLUFTARE
- FLÖDESMÄTARE KV
- VÄRMEMÄNGDSMÄTARE
- TRYCKMÄTARSATS 3-PUNKTER
 TRYCKMÄTARSATS 4-PUNKTER
- TRYCKMÄTARARE, SIGNALMANOMETER MED LARM
- GIVARPLACERING TEMPERATUR
 GIVARPLACERING TRYCK
- SMUTSFILTER, MASKVIDD 0,6 MM
- ÅTERSUGNINGSSKYDD, SKYDDSMODUL KAT. 4
- ÅTERSUGNINGSSKYDD, SKYDDSMODUL KAT. 3
- MÄTARE TEMPERATUR
- CIRKULATIONSPUMP
- EXPANSIONSKÄRL
- LUFT_/SMUTSAVSKILJARE

BET	ÄNDRINGEN AVSER	DATUM	SIGN

FÖRFRÅGNINGSUNDERLAG

SANDVIKENS KOMMUN
LASARETTET 110

Sandvikens Kommun

	A SKOOG	ARKITEKTER	tel. 026-62 40 30
	L SKOOG	ARKITEKTER	tel. 026-62 40 30
	E RAMBÖLL SVERIGE AB		tel. 070-519 17 99
X	VVS VVESS SYSTEMS AB		tel. 026-51 56 35
	SP BRIAB		tel. 0708-72 92 02
	BR BRIAB		tel. 076-832 57 01

UPPDRAG.NR	RITAD/KONSTR. AV	HANDLÄGGARE
2415	ChN	LaB
DATUM	ANSVARIG	
2024-08-12	Lars Berthilson	

LASARETTET 110
LÄKARSTIGEN
FLÖDESSCHEMA
RÖRSYSTEM

SKALA	NUMMER	BET
A1 - A3 -	W-50-8-001	

ORGINALFORMAT: A1

PLO: 2024-12-02 16:02 X:\PROJEKT\2415- VALLHOVSGLANTAN LSS SJUKRITNINGARV\MODELL\LÄKARSTIGEN\W50.8-001.DWG LASSE

XREF:

LAGER: SB11