



Brandskyddsbeskrivning Förfrågningsunderlag



Sätra, Gävle - Pinnmovägen 2 och 4
Ombyggnad för lägenheter

2025-02-10



Projektinformation

Fastighet: Sättra, Pinnmovägen 2 och 4
Kommun: Gävle
Ärende: Ombyggnad av bostäder
Byggherre: AB Gavlegårdarna

Kontaktperson: Emil Ivarsson
emil.ivarsson@gavlegardarna.se
070-164 72 77

Uppdragsansvarig: Andreas Johansson
andreas.johansson@briab.se
070 - 791 00 20

Handläggare: Stina Dufva
stina.dufva@briab.se
076-8325701

Datum	Typ av handling	Upprättad av	Kontrollerad av
2025-02-10	Förfrågningsunderlag	Stina Dufva	Andreas Johansson



Innehåll

1 Inledning	4
1.1 Syfte	4
1.2 Regelverk och styrande dokument	4
1.3 Omfattning och avgränsningar	4
1.4 Kvalitetssystem	4
2 Allmänna förutsättningar	4
3 Brandtekniska förutsättningar	5
3.1 Ändringens omfattning	5
3.2 Verksamhetsklass	5
3.3 Personantal	6
3.4 Byggnadsklass	6
3.5 Dimensionerande brandbelastning	6
3.6 Dimensioneringsmetod	6
4 Brandskydd mellan byggnader	6
4.1 Ytterväggar	6
4.2 Taktäckning	6
5 Brandskydd inom byggnad	6
5.1 Brandceller	6
5.2 Brandteknisk klass avseende dörrar	7
5.3 Schakt	7
5.4 Ytterväggar	7
5.5 Ytskikt och beklädnader	7
6 Möjlighet till utrymning	8
6.1 Utrymningsvägar	8
6.2 Gångavstånd	8
6.3 Utformning av dörrar för utrymning	8
7 Bärande konstruktioner	8
8 Luftbehandlingsinstallationer	8
8.1 Systemuppbyggnad	8
8.2 Skydd vid brand	8
8.3 Imkanal	9
8.4 Upphängning	9
8.5 Isolering	9
8.6 Material	9



9 Hissar	9
10 Installationer och utrustning	10
10.1 Brandvarnare (hyresrättslägenheter, bottenplan)	10
10.2 Brand- och utrymningslarm (serviceboende, plan 1 och 2 tr)	10
10.3 Matlagningsanordningar	10
10.4 Brandgasventilation	10
10.5 Handbrandsläckare	10
11 Möjlighet till räddningsinsats	10
12 Utförandekontroll	11
12.1 Allmänt	11
12.2 Egenkontroller	11
13 Brandskydd under byggtid	12



1 Inledning

1.1 Syfte

Denna handling redovisar hur brandskyddet ska säkerställas vid ombyggnad av bostäder inom fastigheten Sättra Pinnmovägen 2 och 4, Gävle.

Handlingen har upprättats i samband med bygganmälan och som del av förfrågningsunderlag där endast principer och systemval redovisas. Handlingen utgör projekteringsunderlag för övriga projektörer som ansvarar för att brandskydd enligt denna handling inarbetas i respektive handling och på aktuella ritningar. Detaljprojektering ska utföras i samband med upprättande av bygghandlingar.

1.2 Regelverk och styrande dokument

Den brandskyddstekniska dimensioneringen har skett mot Boverkets byggregler, BBR 29 (BFS 2011:6 med ändringar t.o.m. 2020:4).

Avskiljande och bärande konstruktioner har dimensionerats enligt EKS 12 (BFS 2011:10 med ändringar t.o.m. BFS 2022:4).

Dimensionerande brandbelastning har bestämts enligt Boverkets allmänna råd om brandbelastning (BFS 2013:11).

1.3 Omfattning och avgränsningar

Handlingen omfattar ombyggnad för lägenheter inom fastigheten Sättra Pinnmovägen 2 och 4, Gävle.

1.4 Kvalitetssystem

Brandskyddsdimensioneringen omfattas av kontroll enligt anvisningarna i Briabs ledningssystem, vilket är certifierat enligt ISO 9001. Handläggaren, uppdragsansvarig samt en särskild utsedd kontrollant inom Briab kontrollerar att relevanta krav och råd tillgodoses. Kontroll utförs mot särskild checklista och dokumenteras.

2 Allmänna förutsättningar

Nedan beskrivs kortfattat de grundläggande förutsättningarna för brandskyddets utformning. En förändring av dessa förutsättningar kan innebära att brandskyddets utformning måste ses över.

Underlag till denna handling utgörs av planritning. Platsbesök har genomförts den 10 december 2024 av Stina Dufva, Briab.



3 Brandtekniska förutsättningar

3.1 Ändringens omfattning

Ändringen består i huvudsak av viss renovering samt planlösningsändring för nya lägenheter. I bottenplan planeras vanliga hyreslägenheter och i ovanliggande plan utförs servicelägenheter, se verksamhetsbeskrivning nedan.

3.2 Verksamhetsklass

Verksamhetsbeskrivningen är enligt nedan (tillhandahållen från byggherre/beställare):

"Ett serviceboende består av ett antal lägenheter som ligger samlade i samma hus eller kringliggande hus, här finns också gemensamma sällskapsutrymmen. Serviceboende innebär att kunden bor i egen lägenhet med andrahandskontrakt genom Gävle kommun och har stöd från personal inom närområdet dygnet runt. Mellan 10 - 12 lägenheter är kopplade till samma boende. Lägenheterna ligger i vanliga hyreshus och hyrs ut omöblerade. Här bor vuxna personer med psykisk funktionsnedsättning som har fått beslut om särskilt boende enligt 4 kap 1 § SoL. Här får kunden hjälp och stöd i vardagen för att känna trygghet och kunna leva så självständigt som möjligt.

Som vi ser det kommer det inte krävas någon större anpassning av byggnaden för verksamheten/de boende jämfört om det skulle varit en "vanlig hyresrätt". De personer som bor på ett sådant boende är så pass friska och förstående att de kan utrymma enligt instruktioner. Vi får tänka oss att det är ett vanligt hyreskontrakt där hyresgästen får hjälp i vardagen att betala räkningar, planera matlagning, boka tvättstuga mm."

Bedömning av verksamhetsklass

Brandskyddet inom berörda delar dimensioneras utifrån ovanstående beskrivning för verksamhetsklass 3A, dock är boendet behovsprövat enligt SoL.

Enligt uppgift förväntas dock brukare ha möjlighet att utrymma på egen hand (primär utrymning till trapphus) alternativt via balkong och med assistans från räddningstjänst.

Vid eventuella ändrade förutsättningar i detta som medför en kombination av behovsprövat boende och att de boende har begränsade eller inga möjligheter att sätta sig själv i säkerhet så gäller krav enligt verksamhetsklass 5B, varvid behov föreligger i förstärkning av brandskydd (bland annat två oberoende utrymningsvägar utan assistans av räddningstjänst samt boendesprinkler).

Mot bakgrund av att verksamheten trots verksamhetsbeskrivningen bedöms ha ett högre skyddsbehov rekommenderas att brandskyddet utförs med en högre nivå än traditionella bostäder, med följande förstärkande åtgärder inom plan 1-2 tr:

- Installation av automatisk brand – och utrymningslarm
- Installation av spisvakt



3.3 Personantal

Personantalet är inte dimensionerande för brandskyddet.

3.4 Byggnadsklass

Brandskyddet för aktuella byggnader har dimensionerats för att uppfylla kraven för byggnadsklass Br1.

3.5 Dimensionerande brandbelastning

Brandskyddet har dimensionerats för en brandbelastning understigande 800 MJ/m² (golvarea).

3.6 Dimensioneringsmetod

Brandskyddet har dimensionerats enligt förenklad dimensionering. Detta innebär att aktuella föreskrifter uppfylls via de allmänna råden.

4 Brandskydd mellan byggnader

4.1 Ytterväggar

Byggnaden är belägen med ett större avstånd än 8 meter till annan byggnad. Inga särskilda brandskyddstekniska åtgärder krävs för att erhålla tillfredställande skydd.

4.2 Taktäckning

Taktäckning är utförd med obrännbart material (plåt).

5 Brandskydd inom byggnad

5.1 Brandceller

Byggnaden ska delas in i brandceller i sådan omfattning att det medför tillräcklig tid för utrymning och att konsekvenserna på grund av brand begränsas.

Respektive lägenhet ska utföras som egen brandcell med avskiljande konstruktion i lägst brandteknisk klass EI 60. Brandcellsindelning framgår av bifogade skisser.

5.1.1 Genomföringar och installationer

Genomföringar i brandcellsskiljande byggnadsdelar ska utföras och tätas med certifierade eller typgodkända metoder och material för angiven klass.



Installationer i brandcellsskiljande väggar ska utföras på ett sådant sätt att den brandtekniska klassen inte försämras.

5.2 Brandteknisk klass avseende dörrar

Nya dörrar mot trapphus ska utföras i lägst brandteknisk klass EI₂ 30-S₂₀₀. Befintliga dörrar uppfyller erforderlig klass.

Mot personalrum och samlingssal ska dörrar förses med dörrstängare.

5.3 Schakt

5.3.1 Ventilationsschakt

Ev befintliga schakt som betjänar olika brandceller påverkas ska återställas till lägst brandteknisk klass EI 60. Brännbart material som brännbara skivor eller kortlingar ska i övrigt inte förekomma i schakt.

5.3.2 Rörschakt

Installationsschakt ska avskiljas i varje bjälklag som utgör brandcellsgräns. För brännbara rör kan särskilda metoder krävas för att säkerställa avskiljning. Utformning ska redovisas brandkonsult för bedömning.

5.4 Ytterväggar

Byggnadens ytterväggar påverkas inte av ombyggnaden.

5.5 Ytskikt och beklädnader

Undertak och andra byggnadsdelar eller fasta inredningar ska vara upphängda på sådant sätt att de inte faller ner inom 10 min vid en temperatur på 300°C.

5.5.1 Väggar, tak, golv och fast inredning

Kraven på ytskikt och beklädnader gäller byggnadsdelar och fast inredning. Kravnivån på tak, väggar och golv beror på den mängd värme och brandgas som kan tillåtas utvecklas enligt tabell nedan. Fast inredning ska utföras i lägst brandteknisk klass D-s2,d0.

Verksamhet/lokal	Väggar	Tak	Golv
Lägenheter i Br1	C-s2,d0 ²⁾	B-s1,d0 ^{1) 2)}	-

- 1) fäst på material av A2-s1,d0 eller på beklädnad i brandteknisk klass K₂10/B-s1,d0.
- 2) Mindre byggnadsdelar får utföras i lägst brandteknisk klass D-s2,d0 (dörrblad, karmar, lister och balkar mindre än 20 % av anslutande tak eller vägg).



6 Möjlighet till utrymning

6.1 Utrymningsvägar

Grundläggande krav för utrymning är att det från varje lokal där personer vistas mer än tillfälligt finns minst två av varandra oberoende utrymningsvägar.

Utrymning från lägenheterna sker via dörrar till trapphus samt alternativ utrymning via fönster/balkonger med hjälp av räddningstjänst.

6.2 Gångavstånd

Gångavstånd till närmsta utrymningsväg ska inte överstiga 45 meter, vilket uppfylls med redovisad planlösning. Med förestående planlösning uppfylls kravet.

6.3 Utformning av dörrar för utrymning

Dörröppningar ska ha en fri bredd på minst 0,80 meter och beslås med trycke. Dörrar tillåts ha lås som kräver nyckel även från insidan då personer i bostaden förväntas ha tillgång till nyckel.

Dörrar kan utföras med valfri slagriktning.

7 Bärande konstruktioner

Bärande konstruktioner ska hänföras till en brandsäkerhetsklass utifrån risken för personskador om byggnadsdelen kollapsar under ett brandförlopp och ska dimensioneras så att funktionen hos en brandcellsgräns eller annan avskiljande konstruktion erhålls under avsedd tid.

Vid eventuella ändringar i byggnadens stomme ska brandsakkunnig kontaktas för att fastställa erforderlig kravnivå. Ev. avvaxlingar ska utföras i lägst brandteknisk klass R 60.

8 Luftbehandlingsinstallationer

8.1 Systemuppbyggnad

Byggnadens ventilation är befintlig och omfattas inte av ändringen i större omfattning. Skydd mot brand- och brandgasspridning ska dock vara säkerställt.

8.2 Skydd vid brand

Skydd mot brandgasspridning i ventilationssystemet förutsätts generellt utgöras av fläktar i drift i befintlig utformning (frånluftsfläktar på tak med ersättningsluft till respektive lägenhet via uteluft). Ändringen påverkar inte befintlig systemutformning.



Nya aggregat för samlingssal och personalrum kommer endast att betjäna en och samma brandcell, inga brandtekniska åtgärder erfordras (dessa aggregat kräver således inga brandspjäll eller styrning från centralt brandlarm).

8.3 Imkanal

Imkanaler från kök i bostäder ska utföras i lägst brandteknisk klass E 15 med ett skyddsavstånd till brännbart material på minst 30 mm. Alternativt ska kanalen utföras i lägst brandteknisk klass EI 15.

8.4 Upphängning

Upphängningsanordningar för ventilationskanaler samt för brandskyddsspjäll ska utföras i lägst brandteknisk klass R 60. Kravet gäller inom de ytor där nedfallande kanaler påverkar den genombrutna byggnadsdelens brandmotstånd. I övrigt gäller generellt lägst brandteknisk klass R 15.

8.5 Isolering

Ventilationskanaler ska isoleras i erforderlig omfattning vid genombrott av brandcellsskiljande byggnadsdel.

8.6 Material

Kanalsystem och isolering ska utföras av obrännbart material.

9 Hissar

Hisschakt är placerat i samma brandcell som tillhörande trapphus. Följande ska beaktas om hiss byts ut/renoveras:

- Hissmaskin och brytskivor får placeras i samma brandcell som hisschaktet. Hissmaskinskåp med ringa brandbelastning får placeras i hisschakt eller trapphus.
- Strömförsörjning till hissmotorer ska vara säkerställd i händelse av brand. Detta kan säkerställas genom att kabeln utförs med brandresistent kabel som uppfyller funktion vid brand enligt IEC 60331 eller brandsäkert förlagd kabel (motsvarande EI 30) inom de brandceller som hissen betjänar.
- Hiss ska utföras med brandteknisk styrning i enlighet med krav i SS-EN 81-73, vilken innebär att hissen i händelse av brand styrs till ett förbestämt våningsplan.



10 Installationer och utrustning

10.1 Brandvarnare (hyresrättslägenheter, bottenplan)

Brandvarnare ska installeras i varje lägenhet. Brandvarnare ska placeras i, eller utanför, varje rum för sovande personer. Det ska finnas minst en brandvarnare per 60 m².

Brandvarnare ska vara utförd enligt SS-EN 14604 och försedd med larmindikator. Placering ska vara i takets högsta punkt och minst 0,50 meter från vägg, alternativt enligt monteringsanvisning.

10.2 Brand- och utrymningslarm (serviceboende, plan 1 och 2 tr)

Delar som ingår som servicebostäder samt tillhörande utrymningsvägar ska förses med ett brand- och utrymningslarm enligt SBF 110:8, se bifogad utförande specifikation för detaljer.

10.3 Matlagningsanordningar

Spisfläkt eller brännbart material ska placeras minst 0,5 meter från ovansida av spis.

Inom enskilda lägenheter tillhörande serviceboende ska spisvakt installeras.

10.4 Brandgasventilation

Trapphus är befintligt utförda med möjlighet till brandgasventilation via lucka i trapphustopp som kan öppnas från entréplan.

10.5 Handbrandsläckare

Handbrandsläckare ska monteras inom delar som omfattas av serviceboende (plan 1 -2 tr).

Handbrandsläckare ska som minsta omfattning placeras i anslutning till personalrum och samlingssal. Handbrandsläckare ska vara upphängd och placerad väl synlig, lätt åtkomlig och ska vara utmärkt med varselskylt.

11 Möjlighet till räddningsinsats

Insatstiden för räddningstjänsten bedöms understiga 10 min. Tillgång till släckvatten förutsätts vara ordnat mot bakgrund av att byggnaden är befintlig.



12 Utförandekontroll

12.1 Allmänt

Verifiering i de färdiga lägenheterna ska ske genom provning, mätning eller besiktning beroende på vilken egenskap som ska verifieras. Såväl metod som resultat ska dokumenteras.

Lägenheterna ska inte tas i bruk innan brandskyddstekniska installationer är i driftklart skick.

12.2 Egenkontroller

Nedanstående egenkontroller ska finnas tillgängliga för att en slutgiltig bedömning av brandskyddets utförande ska kunna genomföras.

Kontrollpunkt	Omfattning av egenkontroll
Bygg	
Brandcellsavskiljande byggnadsdelar	Erforderlig brandteknisk klass på väggar, dörrar, glaspartier etc. samt monterade enligt monteringsanvisningarna.
Bärande konstruktioner	Uppfyller erforderlig brandteknisk klass (se avsnitt "bärande konstruktioner" i denna handling för mer information).
Genomföringar	Tätade med typgodkända produkter och enligt tillverkarens monteringsanvisningar så att den brandavskiljande konstruktionens brandtekniska klass inte försämras.
Ventilation	
Upphängning	Upphängningsanordningar uppfyller erforderlig brandteknisk klass.
Imkanaler	Utförda i brandteknisk klass och avstånd till brännbart material enligt brandskyddsbeskrivningen.
EI	
Brandvarnare	Omfattning och funktion.
Brand- och utrymningslarm	Funktionsprovning Anläggarintyg Om leveransbesiktning ska beslutas av Byggherren mot bakgrund av att brandlarmet formellt inte är en myndighetsanläggning. Leveransbesiktningsintyg kan dock krävas för att kunna koppla anläggningen mot SOSAB/Räddningstjänst.



13 Brandskydd under byggtid

Bygg-, rivnings- eller markarbetsplatser ska vara ordnade så att tillträde för obehöriga försvåras och så att risken för personskador begränsas. Åtgärder ska vidtas till skydd mot uppkomst och spridning av brand. Vid byggnadsarbeten är riskerna för brands uppkomst och spridning oftast stora. Följande råd ska beaktas under byggtiden:

- Lagring av virke och brännbart material ska inte ske i eller i anslutning till utrymningsvägar och ska inte ske nära fasad.
- Öppna containrar ska placeras minst 6 meter från fasad. Stängda containrar med lås ska placeras minst 2 meter från fasad.
- Förvaring av brandfarliga vätskor och gaser ska ske utomhus på fri och inhägnad plats.
- Brandskydd i tillfälliga byggnader (som byggbodan) ska beaktas vad gäller utformning och placering. Se SBF:s rekommendationer, Brandskydd byggbodan, 2009.
- Risk för brand ska beaktas vid installation av tillfälliga uppvärmningsanordningar.
- Elektriska installationer ska vara utformade så att risk för brand minimeras under byggtiden.
- Heta arbeten ska utföras av behörig personal enligt gällande föreskrifter. Se Svenska Brandskyddsföreningens säkerhetsregler för Heta arbeten.
- Handbrandsläckare eller annat släckredskap ska finnas på byggarbetsplatsen.
- Brandposter i gata ska vara tillgängliga under hela byggtiden.
- Räddningsvägar och uppställningsplatser för räddningstjänsten till intilliggande byggnader får inte blockeras.
- För att minska riskerna att en eventuell brand påverkar hela byggnaden under byggtiden ska brandcellsgränser och brandtätning färdigställas så fort det är möjligt.

Briab – The right side of risk

Stina Dufva


Andreas Johansson

NYTT LGH-NR 4002-1101
NY LÄGENHET 2 RoK ca 60 m2

NYTT LGH-NR 4002-1102
NY LÄGENHET 2 RoK ca 59 m2

NYTT LGH-NR 4002-1202
NY LÄGENHET 2 RoK ca 54 m2

NYTT LGH-NR 4002-1203
BEF LÄGENHET NR 4002-1204
2 RUM o KÖKVRÅ 40,0 m2

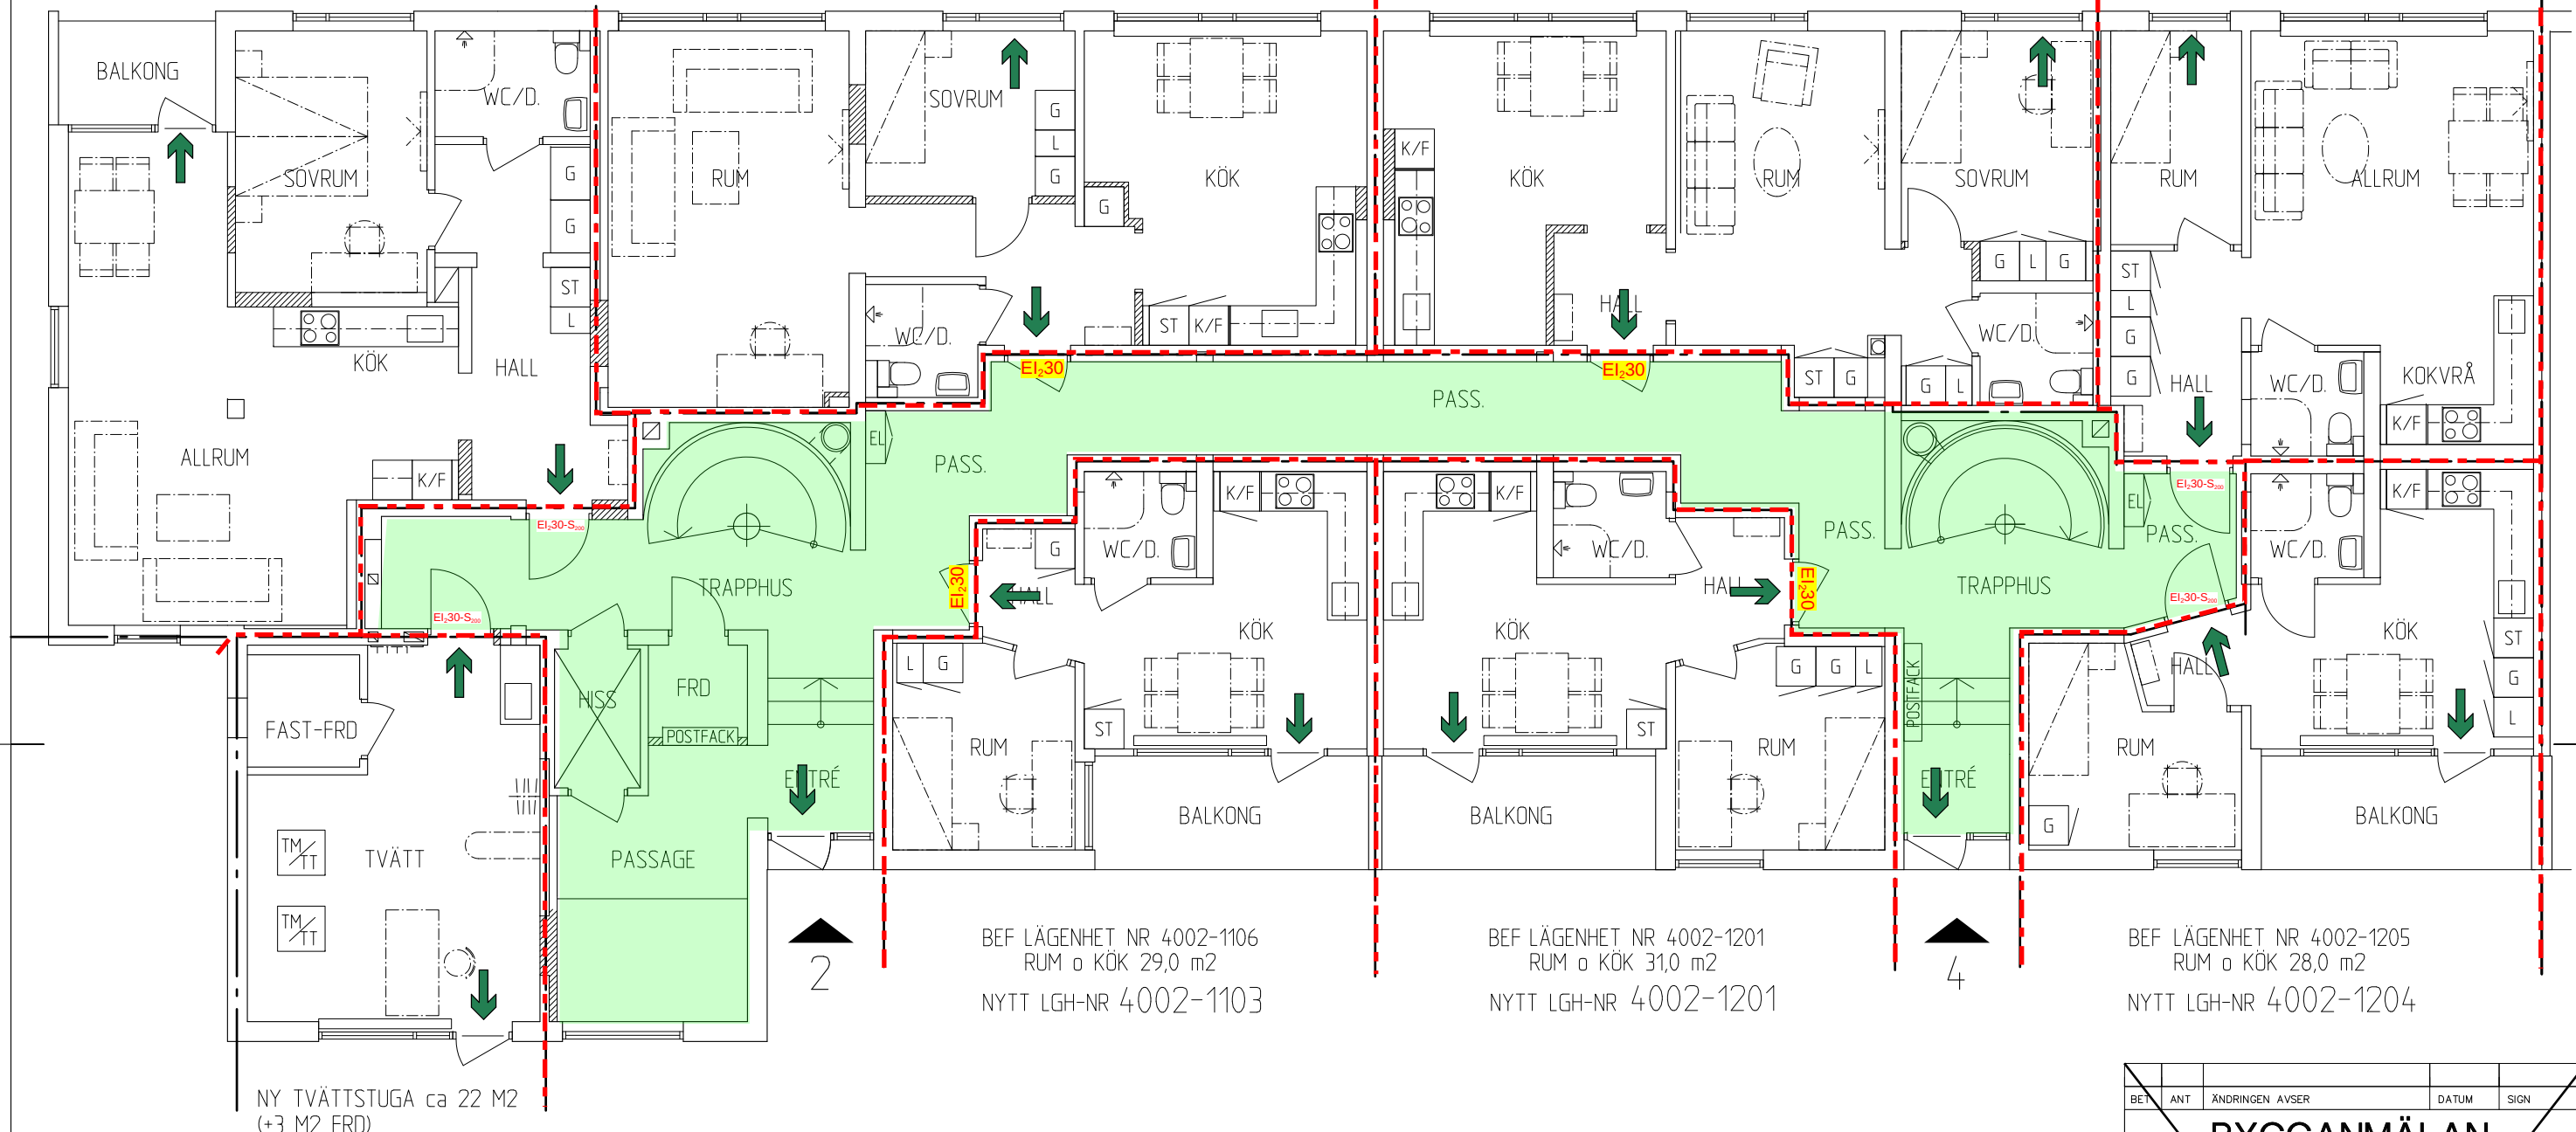

NY TVÄTTSTUGA ca 22 M2
(+3 M2 FRD)

BEF LÄGENHET NR 4002-1106
RUM o KÖK 29,0 m2
NYTT LGH-NR 4002-1103

BEF LÄGENHET NR 4002-1201
RUM o KÖK 31,0 m2
NYTT LGH-NR 4002-1201

BEF LÄGENHET NR 4002-1205
RUM o KÖK 28,0 m2
NYTT LGH-NR 4002-1204

FÖRKLARINGAR

-  Utrymningskoncept
-  Utrymningsväg, trapphus/korridor
-  Brandcellsgräns EI 60
-  Befintlig dörr, brandklass
-  Ny dörr, brandklass



2025-02-10

AR: SE RITNING NR A40.0-10

METER



BET	ANT	ÄNDRINGEN AVSER	DATUM	SIGN
BYGGANMÄLAN 2025-01-20				
		AB Gavlegårdarna Utanvindsvägen 1, Box 456, 801 06 Gävle Tel: 026-17 27 00 www.gavlegardarna.se		
UPPRÄTTAD AV		CW Bygghälsan AB Garnlevägen 94, 18 96 Hedesunda Tel. 070-232 09 38 / 070-367 16 86 e-mail: cwbygg@telia.com		
UPPDRAG NR	RITAD/KONSTR AV	HANDLÄGGARE		
1370	lw	lw		
DATUM	ANSVARIG			
2025-01-20	I. Waller			
SÄTRA 584, Pinnmovägen 2 o 4 OMBYGGNAD 2025 BOTTENPLAN med möbleringsalternativ men utan visande rivning				
SKALA	NUMMER			BET
1:100 (A3)	A40.1-10			


LGH NR 4002-1114
NY LÄGENHET 2 RoK ca 48 m2

LGH NR 4002-1111
NYTT PERSONALRUM 2 RoK ca

LGH NR 4002-1213
NY LÄGENHET 2 RoK ca 54 m2

LGH NR 4002-1211
BEF LÄGENHET 2 RoK 40 m2

Dörr ska kompletteras med
dörrstängare. Ev värdering om
det ska installeras med s.k.
free-swing.

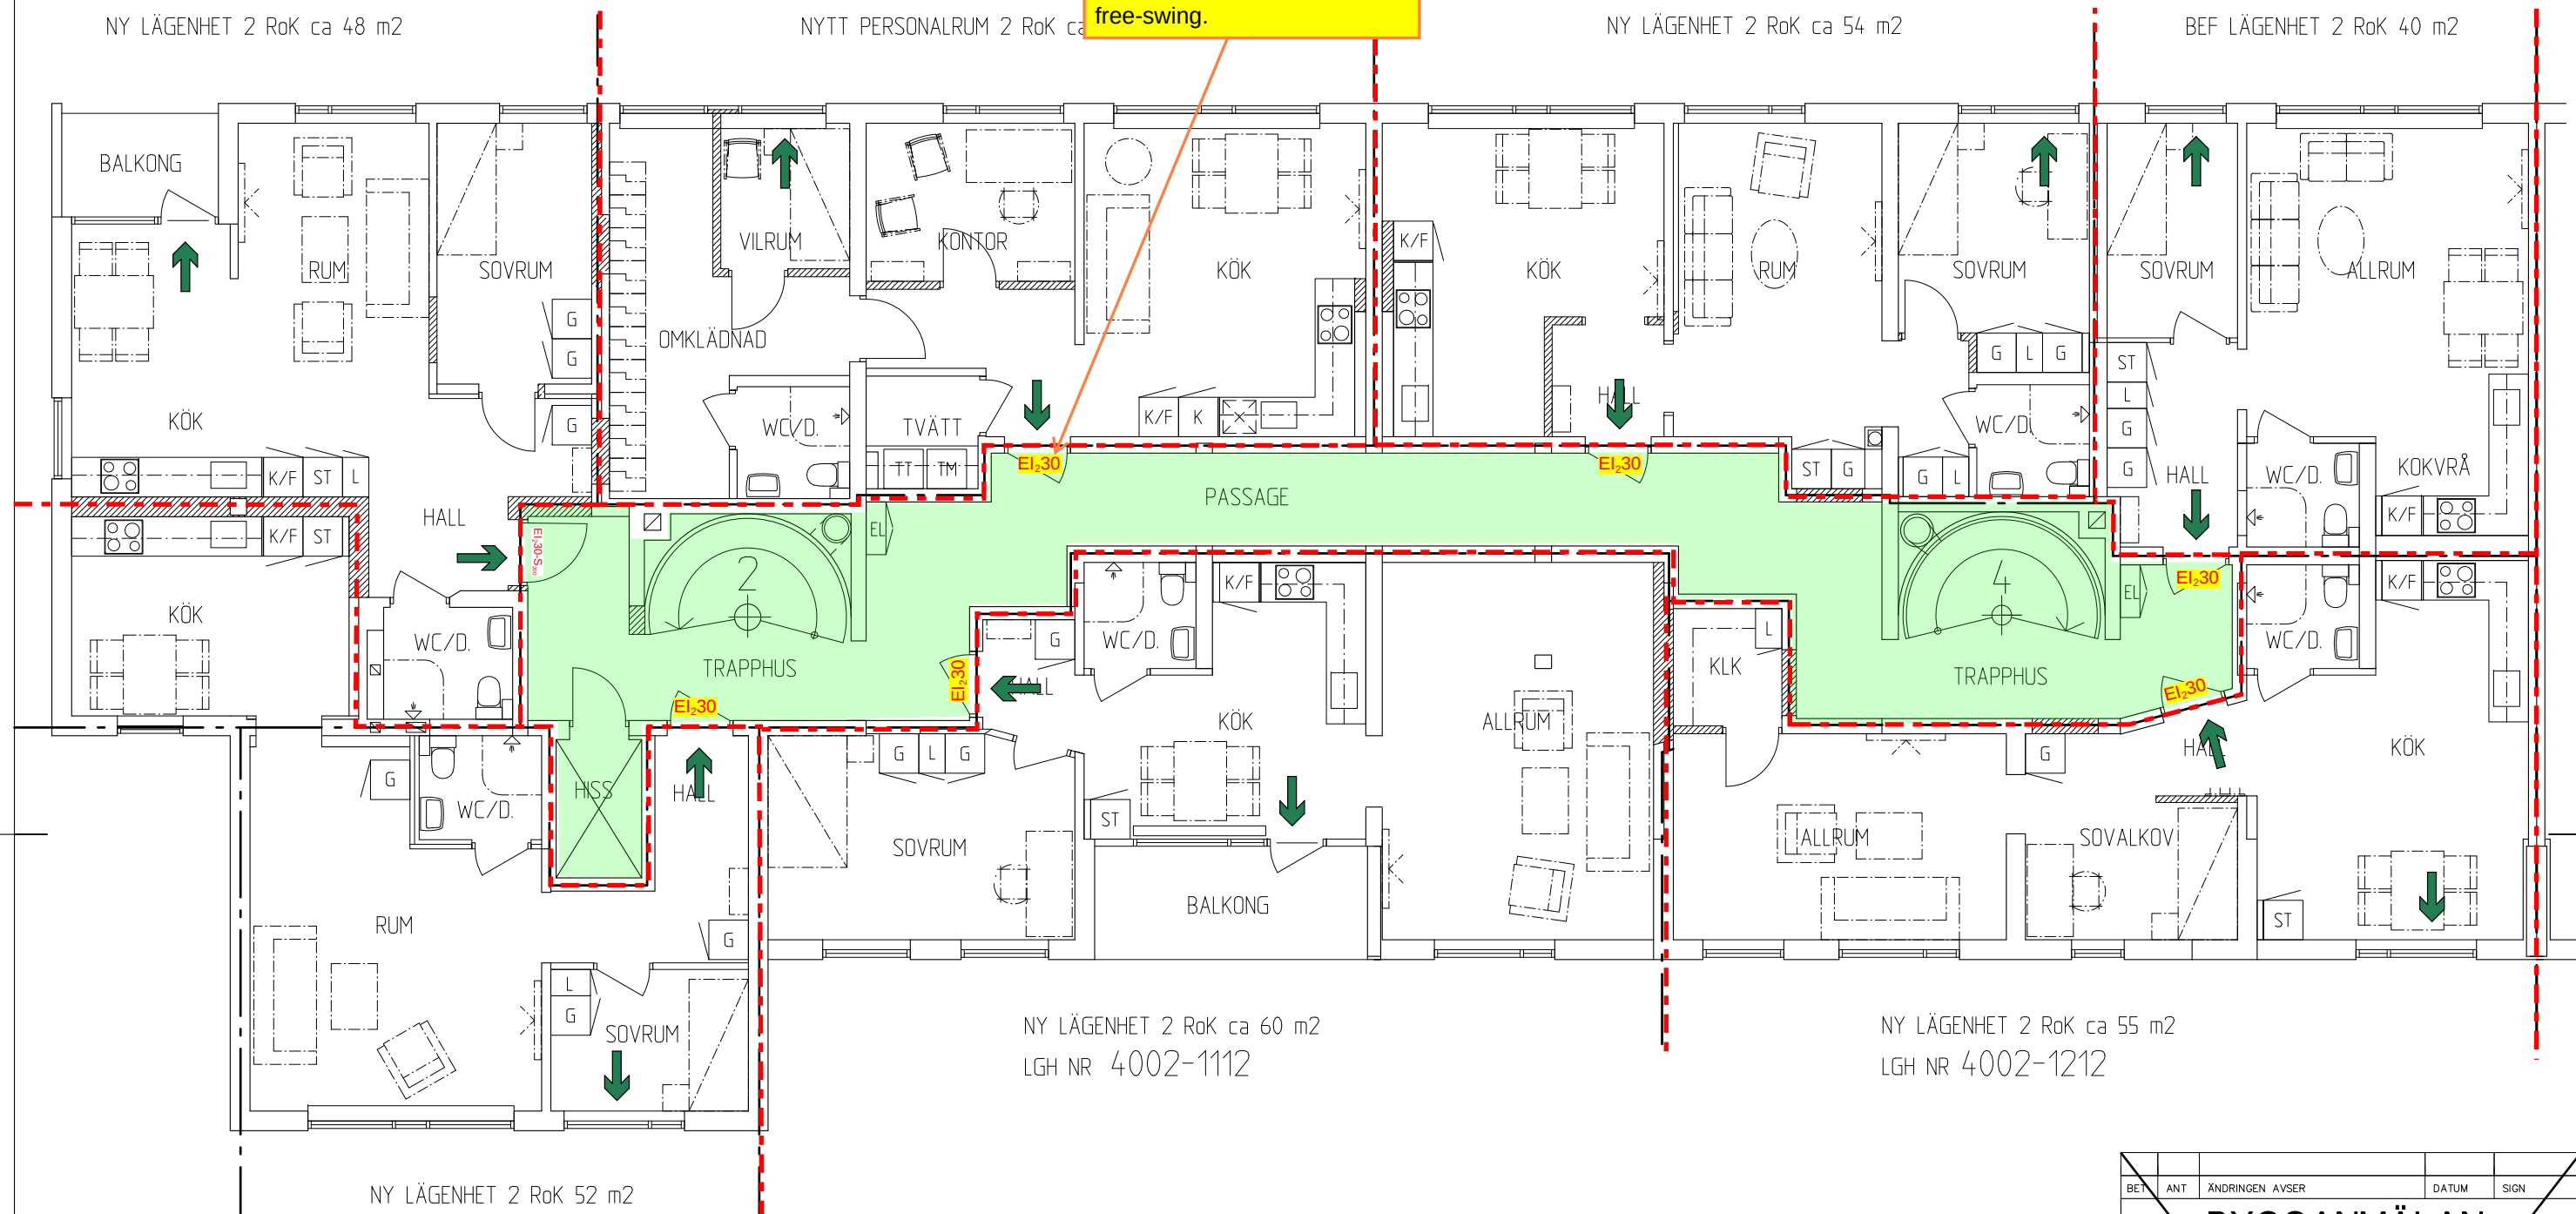


NY LÄGENHET 2 RoK 52 m2
LGH NR 4002-1113

NY LÄGENHET 2 RoK ca 60 m2
LGH NR 4002-1112



NY LÄGENHET 2 RoK ca 55 m2
LGH NR 4002-1212



FÖRKLARINGAR: SE RITNING NR A40.0-10

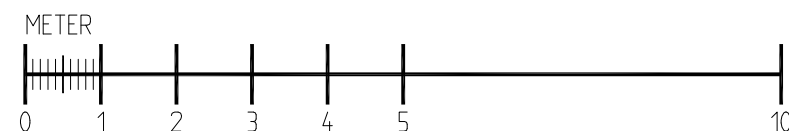

BET	ANT	ÄNDRINGEN AVSER	DATUM	SIGN
BYGGANMÄLAN 2025-01-20				
		AB Gavlegårdarna Utanvindsvägen 1, Box 456, 801 06 Gävle Tel: 026-17 27 00 www.gavlegardarna.se		
UPPRÄTTAD AV		CW Byggkonsult AB Gamlevägen 94, 18 96 Hedesunda Tel. 070-232 09 38 / 070-367 16 86 e-mail: cwbygg@telia.com		
UPPDRAG NR 1370	RITAD/KONSTR AV lw	HANDLÄGGARE lw	ANSVARIG 1. Waller	
DATUM 2025-01-20	SÄTRA 584, Pinnmovägen 2 o 4 OMBYGGNAD 2025			
PLAN VÄNING 1 TR med möbleringsalternativ men ej visande ritning				
SKALA 1:100 (A3)	NUMMER	A40.1-11		

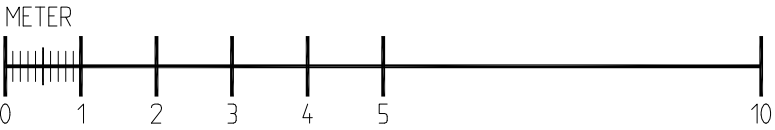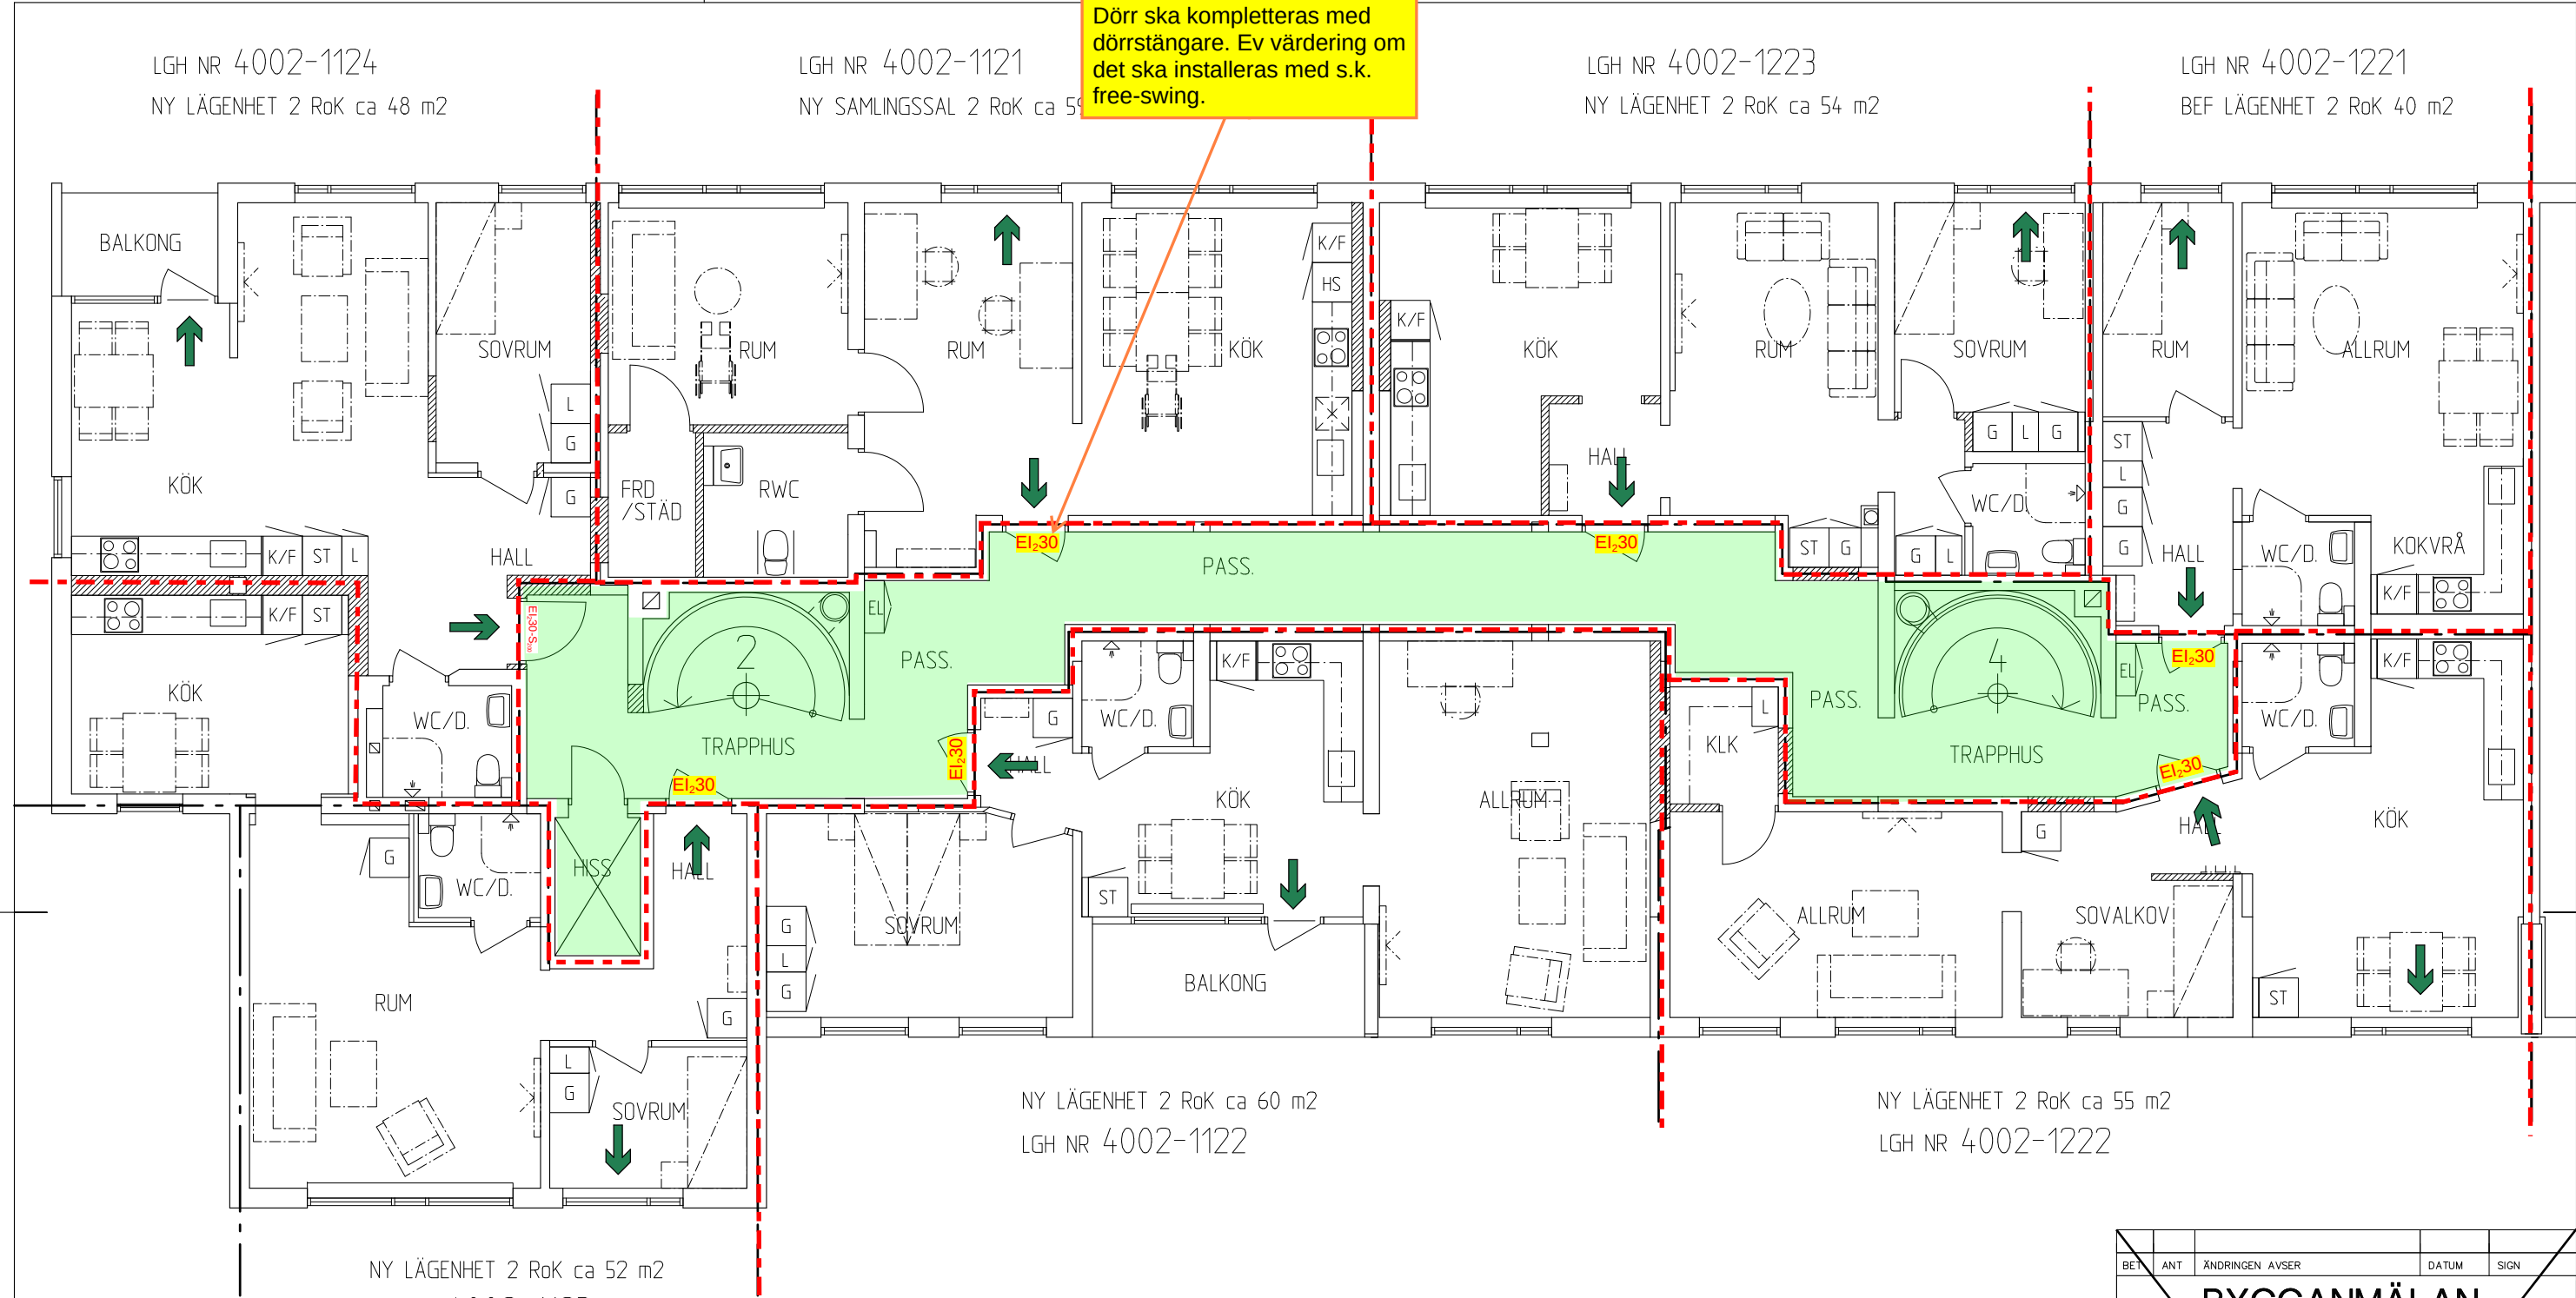

FÖRKLARINGAR: SE RITNING NR A40.0-10



BET		ANT	ÄNDRINGEN AVSER	DATUM	SIGN
BYGGANMÄLAN 2025-01-20					
			AB Gavlegårdarna Utanvindsvägen 1, Box 456, 801 06 Gävle Tel: 026-17 27 00 www.gavlegardarna.se		
UPPRÄTTAD AV			CW Bygghälsö AB Gamlevägen 94, 18 96 Hedesunda Tel. 070-232 09 38 / 070-367 16 86 e-mail: cwbygg@telia.com		
UPPDRAG NR 1370		RITAD/KONSTR AV iw		HANDLÄGGARE iw	
DATUM 2025-01-20		ANSVARIG 1 Waller			
SÄTRA 584, Pinnmovägen 2 o 4 OMBYGGNAD 2025 PLAN VÄNING 2 TR med möbleringsalternativ men ej visande ritning					
SKALA 1:100 (A3)		NUMMER A40.1-12			BET

UTFÖRANDESPECIFIKATION BRANDLARM

1. Allmänt

☒ Ny anläggning ☐ Ändring/utökning	Referensnummer eller dylikt:	Regelverk/utgåva: SBF 110:8
Anläggningen utförd med krav ställda från: ☒ BBR ☐ Försäkringskrav ☐ Egen ambition ☐ AFS	Beskrivning: Pinnmovägen 2 och 4, Gävle	Användare Kompletteras senare
Anläggningens namn och adress: Kompletteras senare		Anläggningsägare och adress: Kompletteras senare

2. Övervakningsområde

☐ Klass A – Övervakning av hela byggnaden	Beskrivning:
☐ Klass B – Fullständig övervakning av brandcell	Beskrivning:
☐ Klass C – Begränsad övervakning av utrymnings- och kommunikationsvägar	Beskrivning:
☒ Klass D – Begränsad övervakning av vissa utrymmen	Beskrivning: Övervakade ytor enligt skiss.
☐ Klass E – Endast manuell aktivering	Beskrivning:

3. Manuell aktivering

☐ Samtliga personer ska kunna aktivera brandlarmet manuellt ☒ Endast särskilt utsedd personal ska kunna aktivera brandlarmet manuellt	Beskrivning av placering av larmknappar: Larmknappar ska finnas vid brandförsvarstablå (i skåp) samt inom personalrum samt samlingssal.
---	--

4. Aktivering av brandlarm från andra brandskyddssystem

☐ Gasläcksystem	Beskrivning:
☐ Vattensprinklersystem	Beskrivning:
☐ Andra typer av brandskyddssystem	Beskrivning av typ av system:

5. Särskilda risker

☐ EI- och elektronikutrymmen med hög luftfuktighet eller hög luftomsättning	Beskrivning:
☐ Höglager	Beskrivning:
☐ Fasadövervakning	Beskrivning:
☐ Andra risker att ta hänsyn till	Beskrivning:

6. Larmsignalering

☐ Se bilaga nr:

☐ Larm för intern insats	Var och hur ska larmsignal avges:
☐ Larm för uppmärksamhet	Var och hur ska larmsignal avges:
☒ Utrymningslarm ☒ Flera täckningsområden finns och redovisas i bilaga:	Täckningsområde: Utrymningslarm ska säkerställas i samtliga utrymmen där personer vistas mer än tillfälligt. Vilka ytor som ska utföras med krav på hörbarhet om minst 65 dBA (75 dBA gäller inom boendesovrum) framgår av bifogade skisser.
Signaltyp: ☒ Sirén ☐ Larmklocka ☐ Optisk ☐ Talat meddelande (se separat utförandespecifikation enligt SBF 502)	

7. Selektion av utrymningslarm

☐ Se bilaga nr:

☒ Larm ska avges i hela byggnaden/anläggningen samtidigt	
☐ Larm ska selekteras enligt följande	Beskrivning: Ev selektion av larm utreds tillsammans med verksamheten.

8. Larmlagring

Inom vilka delar: Ev önskemål om larmlagring (under de tider personal är på plats) ska utredas med verksamhet.
Inom vilka tider på dygnet:
Kvitteringstid:
Undersökningstid:
Placering av larmlagringstablåer:

9. Förutsättning för strömförsörjning för reservdrift

☒ 24 timmars drift i normaläge enligt 6.8.5
☐ 5 timmars drift i normaläge enligt 6.8.6 a)
☐ 2 timmars drift i normaläge enligt 6.8.6 b)

10. Styrning och aktivering av andra brandskyddssystem

Typ av styrutgång (alternativ 1 gäller om inte annat anges specifikt) Alternativ 1 – Styrutgång utan krav på indikering Alternativ 2 – Styrutgång med indikering i centralutrustning av att styrsignal har aktiverats Alternativ 3 – Styrutgång med indikering i centralutrustning av att styrsignal har mottagit styrsignalen (kvittens)	Utrustning för kvittens från styrd funktion finns i: ☐ Styrd funktion ☐ Centralutrustning
☐ Gassläcksystem ☐ Styrutgång alternativ 2 ☐ Styrutgång alternativ 3 ☐ Typ 1 – Automatisk aktivering via separat kontroll- och fördröjningsanordning ☐ Typ 2 – Automatisk aktivering med integrerad kontroll- och fördröjningsanordning	
☐ Vattensprinklersystem ☐ Styrutgång alternativ 2 ☐ Styrutgång alternativ 3 ☐ Automatisk aktivering via separat styrcentral ☐ Automatisk aktivering direkt från brandlarmanläggningen	
☐ Andra typer av släcksystem ☐ Styrutgång alternativ 2 ☐ Styrutgång alternativ 3 Typ av system: ☐ Automatisk aktivering via separat styrcentral ☐ Automatisk aktivering direkt från brandlarmanläggningen	
☐ Brandgasventilation ☐ Styrutgång alternativ 2 ☐ Styrutgång alternativ 3 Beskrivning:	
☐ Ventilationsstyrning ☐ Styrutgång alternativ 2 ☐ Styrutgång alternativ 3 ☐ Flera ventilationssystem som ska styras finns och redovisas i bilaga: System: Funktionsbeskrivning:	
☒ Branddörrar ☐ Styrutgång alternativ 2 ☐ Styrutgång alternativ 3 Beskrivning: Eventuell dörrstängarordning mot personalrum och samlingssal (free-swing). Utreds med verksamhet. ☐ Alternativ 1: Dörrar stängs vid frånställning av styrande sektion/larmadress ☐ Alternativ 2: Dörrar fungerar lokalt av frånställd styrande sektion/larmadress	

☐ Hissar ☐ Styrutgång alternativ 2 ☐ Styrutgång alternativ 3		
☐ Flera hissar som ska styras finns och redovisas i bilaga:		
Styrd hiss nr:	Stannplan:	Alternativt stannplan:
Övrigt:		
Övrigt: ☐ Brandgardin/brandjalusi ☐ Nödbelysning ☐ Eislutbleck ☐ Musikanläggning ☐ Rulltrappor ☐ Annan styrning	☐ Styrutgång alternativ 2 ☐ Styrutgång alternativ 2 ☐ Styrutgång alternativ 2 ☐ Styrutgång alternativ 2 ☐ Styrutgång alternativ 2 ☐ Styrutgång alternativ 2	☐ Styrutgång alternativ 3 ☐ Styrutgång alternativ 3 ☐ Styrutgång alternativ 3 ☐ Styrutgång alternativ 3 ☐ Styrutgång alternativ 3 ☐ Styrutgång alternativ 3
Beskrivning:		
Övrig information styrningar: Om trygghetslarm installeras i senare skede så ska signal kunna lämnas från brandlarm för vidarebefordran till trygghetslarmssystem.		

11. Larmöverföring

Larmöverföring sker via: ☐ Fast larlnät ☒ Radio/mobilöverföring ☒ Ip-nät	Mottagare av brandsignal och kontaktuppgifter: SOSAB/Räddningstjänst Åtgärd:	Mottagare av felsignal och kontaktuppgifter: Utredds med fastighetsägare Åtgärd:
--	--	--

12. Skötsel och underhåll

Specifika krav på skötsel och underhåll utöver minimikraven

Beskrivning:

13. Medgivna avvikelser

Anläggningen utförs enligt SBF 110 med följande medgivna avvikelser

Beskrivning:
Avsteg utreds i vidare projektering och ska godkännas av sakkunig brand/beställare.

14. Övrig information

Beskrivning:

15. Upprättande av utförandespecifikation

Specifikation har upprättats av (namn och företag): Stina Dufva, Briab	Företag: Briab Brand och Riskingenjörerna AB
Underskrift:	Ort och datum: Gävle 2025-02-10

REDOVISNING TÄCKNINGSSOMRÅDEN

Täckningsområde:	
Se skisser.	
Signaltyp: ☒ Utrymningslarm ☒ Sirén ☐ Larmklocka ☐ Optisk ☐ Talat meddelande (se separat utförandespecifikation enligt SBF 502)	

Täckningsområde:	
Signaltyp: ☐ Utrymningslarm ☐ Sirén ☐ Larmklocka ☐ Optisk ☐ Talat meddelande (se separat utförandespecifikation enligt SBF 502)	

Täckningsområde:	
Signaltyp: ☐ Utrymningslarm ☐ Sirén ☐ Larmklocka ☐ Optisk ☐ Talat meddelande (se separat utförandespecifikation enligt SBF 502)	


Täckningsområde:	
Signaltyp: ☐ Utrymningslarm ☐ Sirén ☐ Larmklocka ☐ Optisk ☐ Talat meddelande (se separat utförandespecifikation enligt SBF 502)	

Styrning av ventilationssystem

System:	Funktionsbeskrivning:

Styrning av hissar

Styrd hiss nr:	Stannplan:	Alternativt stannplan:

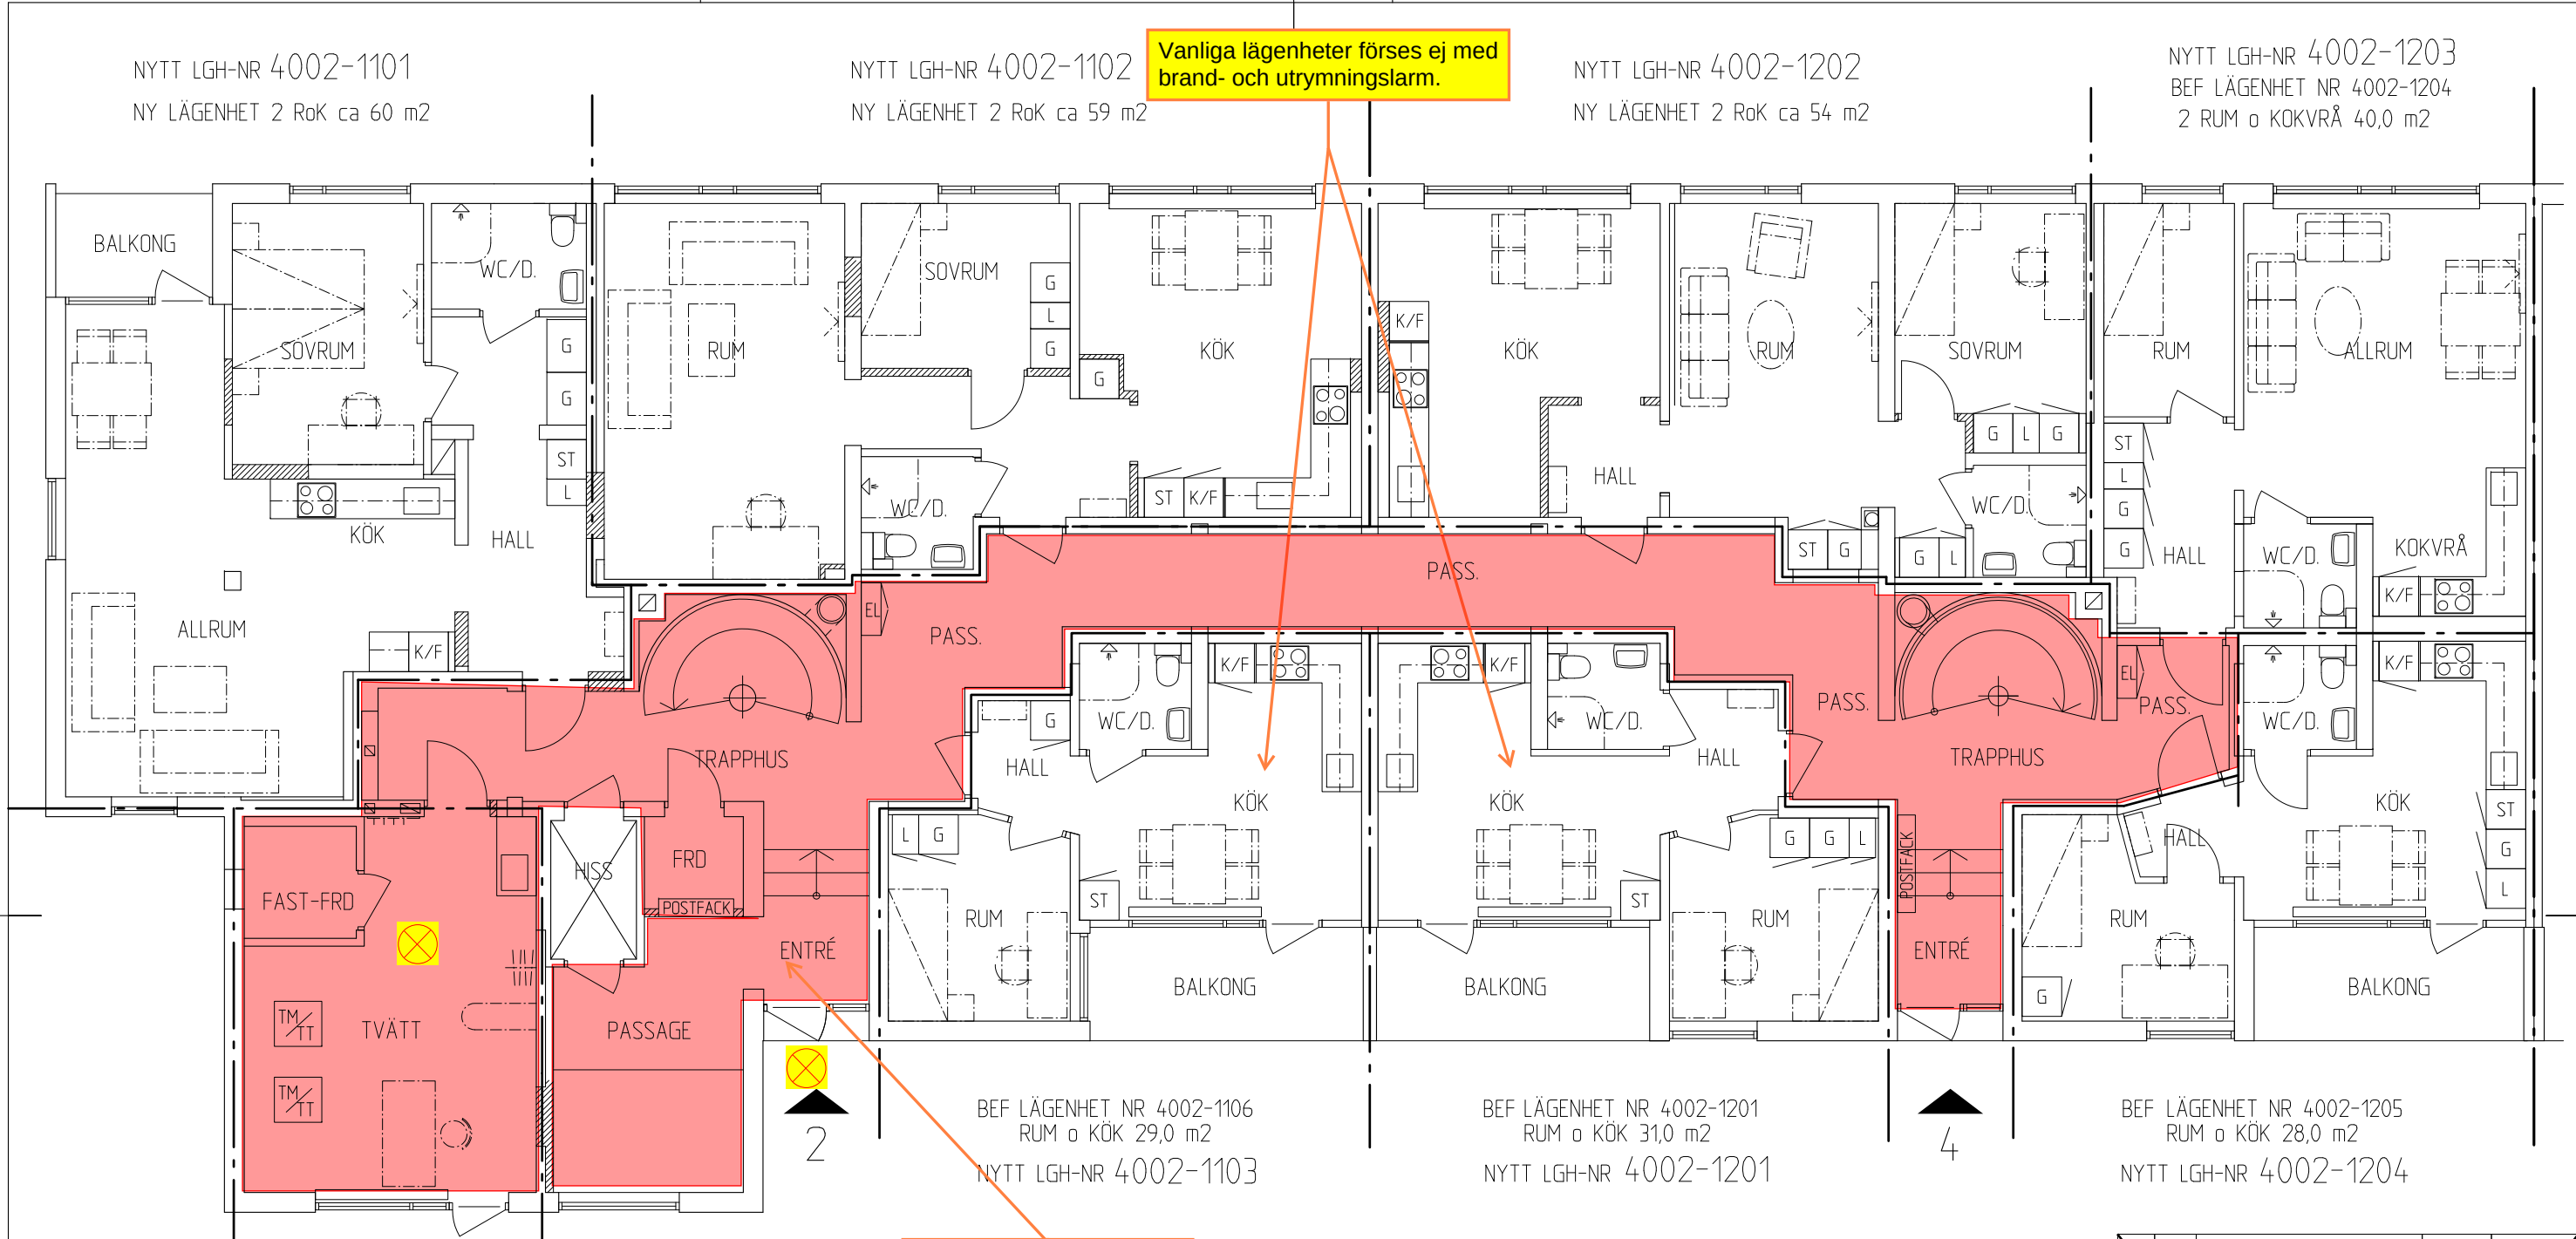

Vanliga lägenheter förses ej med brand- och utrymningslarm.

BFT/CA placeras i anslutning till entré Pinnmovägen 2. Exakt placering i samråd med byggherre.

FÖRKLARINGAR

- Yta övervakad av brandlarm (schematiskt)
- Utrymningslarm (schematiskt redovisat)
- Optiskt larmdon (schematiskt redovisat)



2025-02-10
Brandlarm

FÖRKLARINGAR: SE RITNING NR A40.0-10




BET		ANT	ÄNDRINGEN AVSER	DATUM	SIGN
BYGGANMÄLAN 2025-01-20					
			AB Gavlegårdarna Utanvindsvägen 1, Box 456, 801 06 Gävle Tel: 026-17 27 00 www.gavlegardarna.se		
UPPRÄTTAD AV			CW Bygghälsö AB		
Gamlevägen 94, 18 96 Hedesunda Tel. 070-232 09 38 / 070-367 16 86 e-mail: cwbygg@telia.com					
UPPDRAG NR 1370		RITAD/KONSTR AV lw		HANDLÄGGARE lw	
DATUM 2025-01-20		ANSVARIG 1 Waller			
SÄTRA 584, Pinnmovägen 2 o 4 OMBYGGNAD 2025 BOTTEPLAN med möbleringsalternativ men utan visande rivning					
SKALA 1:100 (A3)		NUMMER A40.1-10			BET

LGH NR 4002-1114
NY LÄGENHET 2 RoK ca 48 m2

LGH NR 4002-1111
NYTT PERSONALRUM 2 RoK ca 59 m2

LGH NR 4002-1213
NY LÄGENHET 2 RoK ca 54 m2

LGH NR 4002-1211
BEF LÄGENHET 2 RoK 40 m2

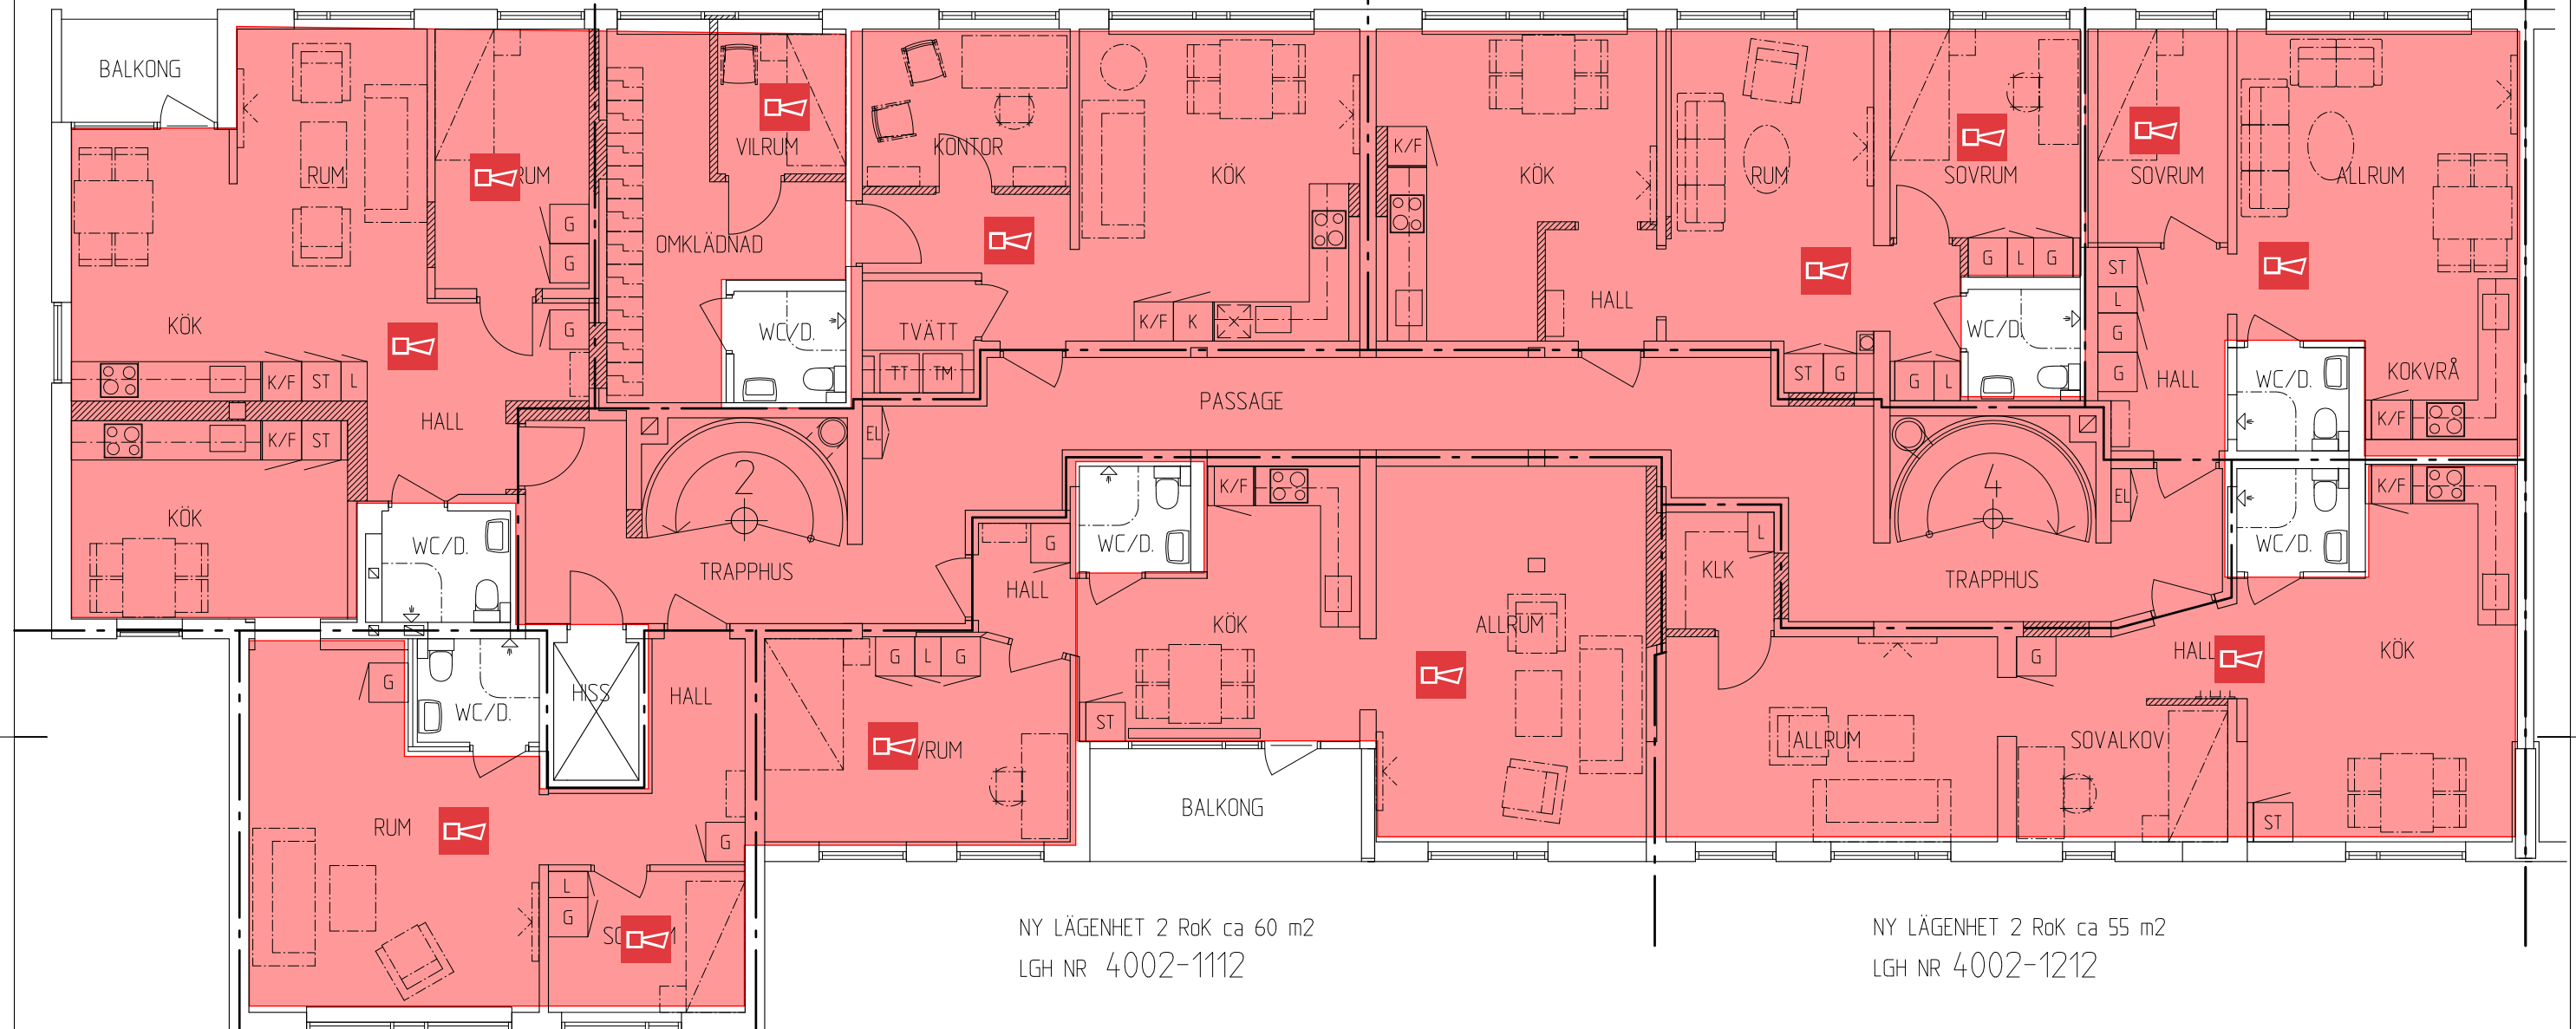


NY LÄGENHET 2 RoK 52 m2
LGH NR 4002-1113

NY LÄGENHET 2 RoK ca 60 m2
LGH NR 4002-1112

NY LÄGENHET 2 RoK ca 55 m2
LGH NR 4002-1212



FÖRKLARINGAR: SE RITNING NR A40.0-10

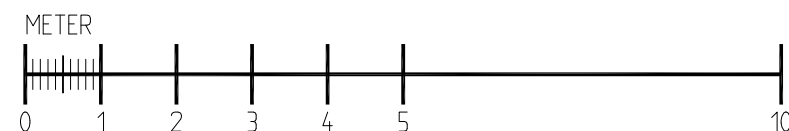


BET	ANT	ÄNDRINGEN AVSER	DATUM	SIGN
BYGGANMÄLAN 2025-01-20				
		AB Gavlegårdarna Utanvindsvägen 1, Box 456, 801 06 Gävle Tel: 026-17 27 00 www.gavlegardarna.se		
UPPRÄTTAD AV		CW Bygghälsö AB Gamlevägen 94, 18 96 Hedesunda Tel. 070-232 09 38 / 070-367 16 86 e-mail: cwbygg@telia.com		
UPPDRAG NR	RITAD/KONSTR AV	HANDLÄGGARE		
1370	lw	lw		
DATUM	ANSVARIG			
2025-01-20	I. Waller			
SÄTRA 584, Pinnmovägen 2 o 4 OMBYGGNAD 2025 PLAN VÅNING 1 TR med möbleringsalternativ men ej visande ritning				
SKALA	NUMMER			BET
1:100 (A3)	A40.1-11			

LGH NR 4002-1124
NY LÄGENHET 2 RoK ca 48 m2

LGH NR 4002-1121
NY SAMLINGSSAL 2 RoK ca 59 m2

LGH NR 4002-1223
NY LÄGENHET 2 RoK ca 54 m2

LGH NR 4002-1221
BEF LÄGENHET 2 RoK 40 m2

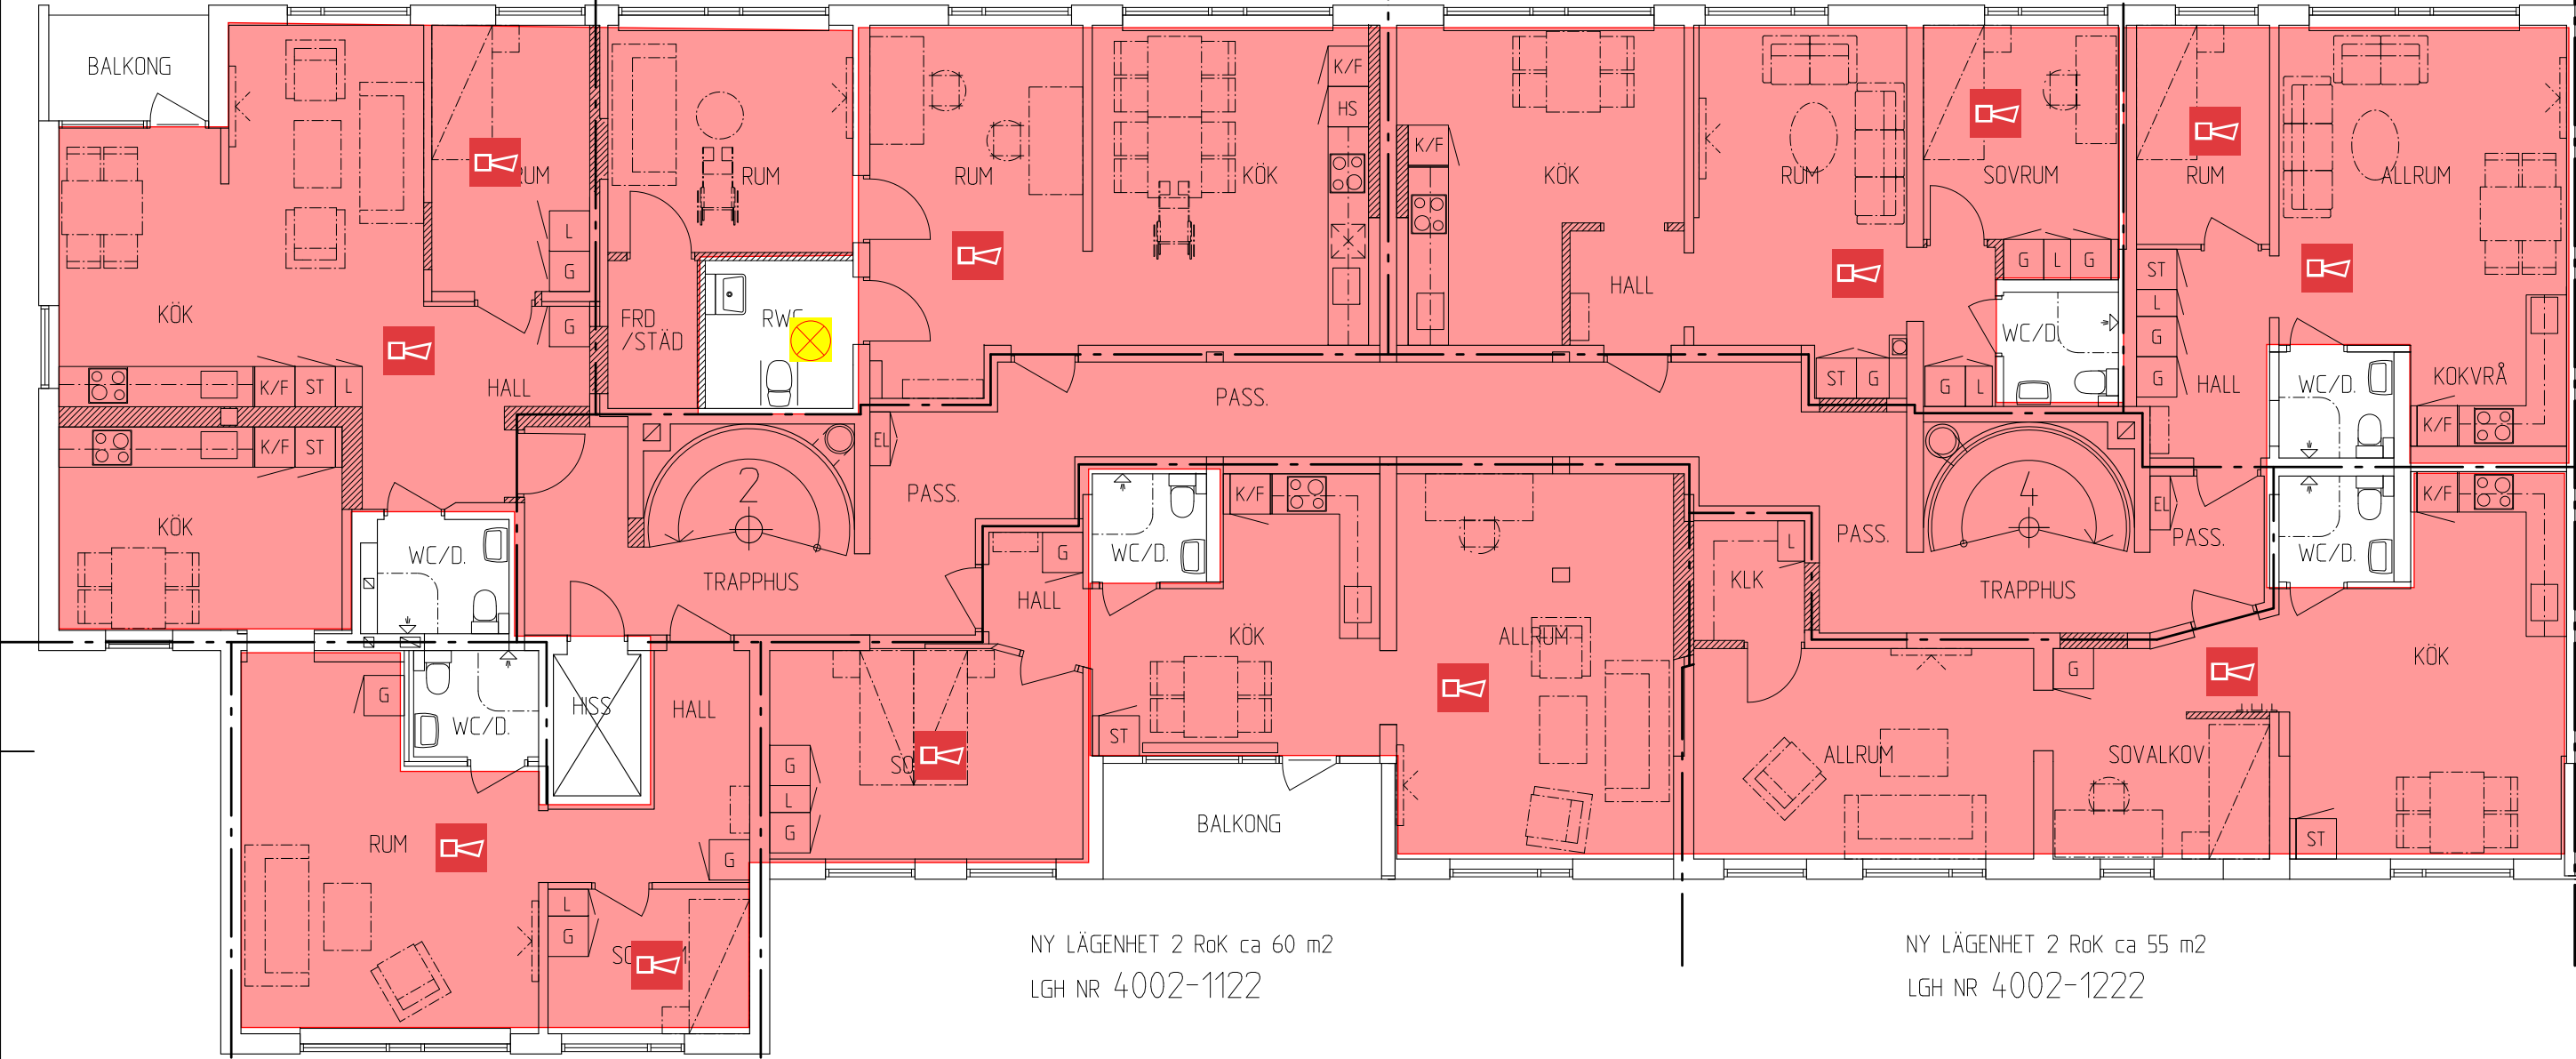


NY LÄGENHET 2 RoK ca 52 m2
LGH NR 4002-1123

NY LÄGENHET 2 RoK ca 60 m2
LGH NR 4002-1122

NY LÄGENHET 2 RoK ca 55 m2
LGH NR 4002-1222



FÖRKLARINGAR: SE RITNING NR A40.0-10

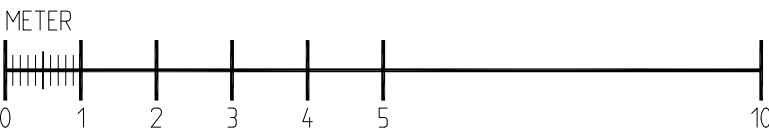

BET		ANT	ÄNDRINGEN AVSER	DATUM	SIGN
BYGGANMÄLAN 2025-01-20					
			AB Gavlegårdarna Utanvindsvägen 1, Box 456, 801 06 Gävle Tel: 026-17 27 00 www.gavlegardarna.se		
UPPRÄTTAD AV			CW Bygghälsö AB Gamlevägen 94, 18 96 Hedesunda Tel. 070-232 09 38 / 070-367 16 86 e-mail: cwbygg@telia.com		
UPPDRAG NR 1370		RITAD/KONSTR AV lw		HANDLÄGGARE lw	
DATUM 2025-01-20		ANSVARIG 1 Waller			
SÄTRA 584, Pinnmovägen 2 o 4 OMBYGGNAD 2025 PLAN VÄNING 2 TR med möbleringsalternativ men ej visande ritning					
SKALA 1:100 (A3)		NUMMER A40.1-12			BET