



GAVLEGÅRDARNA

AB GAVLEGÅRDARNA**Sätra 58:4, Pinnmovägen 2 o 4
Ombyggnad 2025****06-2.1
RITNINGSFÖRTECKNING A-ritningar****Projektnummer: 4002-240312****FÖRFRÅGNINGSUNDERLAG
2025-01-28**


Ritn nr	Rev	Status	Benämning	Skala	Datum	Rev dat.
A40.1-110		FU	Bottenplan	1:100	2025-01-28	
A40.1-111		FU	Plan våning 1 tr	1:100	2025-01-28	
A40.1-112		FU	Plan våning 2 tr	1:100	2025-01-28	
A40.1-101		FU	Källarplan del 2-4	1:100	2025-01-28	
A40.1-201		FU	Källarplan del 6-8	1:100	2025-01-28	
A40.1-301		FU	Källarplan del 8-10	1:100	2025-01-28	
A40.1-401		FU	Källarplan del 12-14	1:100	2025-01-28	
A40.2-101		FU	Sektioner	1:100	2025-01-28	
A40.3-101		FU	Fasader mot V, N o S	1:100	2025-01-28	
A40.3-102		FU	Fasad mot Öster	1:100	2025-01-28	

LGH NR 4002-1114
NY LÄGENHET 2 ROK ca 48 m2

LGH NR 4002-1111
NYTT PERSONALRUM 2 ROK ca 59 m2

LGH NR 4002-1213
NY LÄGENHET 2 ROK ca 54 m2

LGH NR 4002-1211
BEF LÄGENHET 2 ROK 40 m2

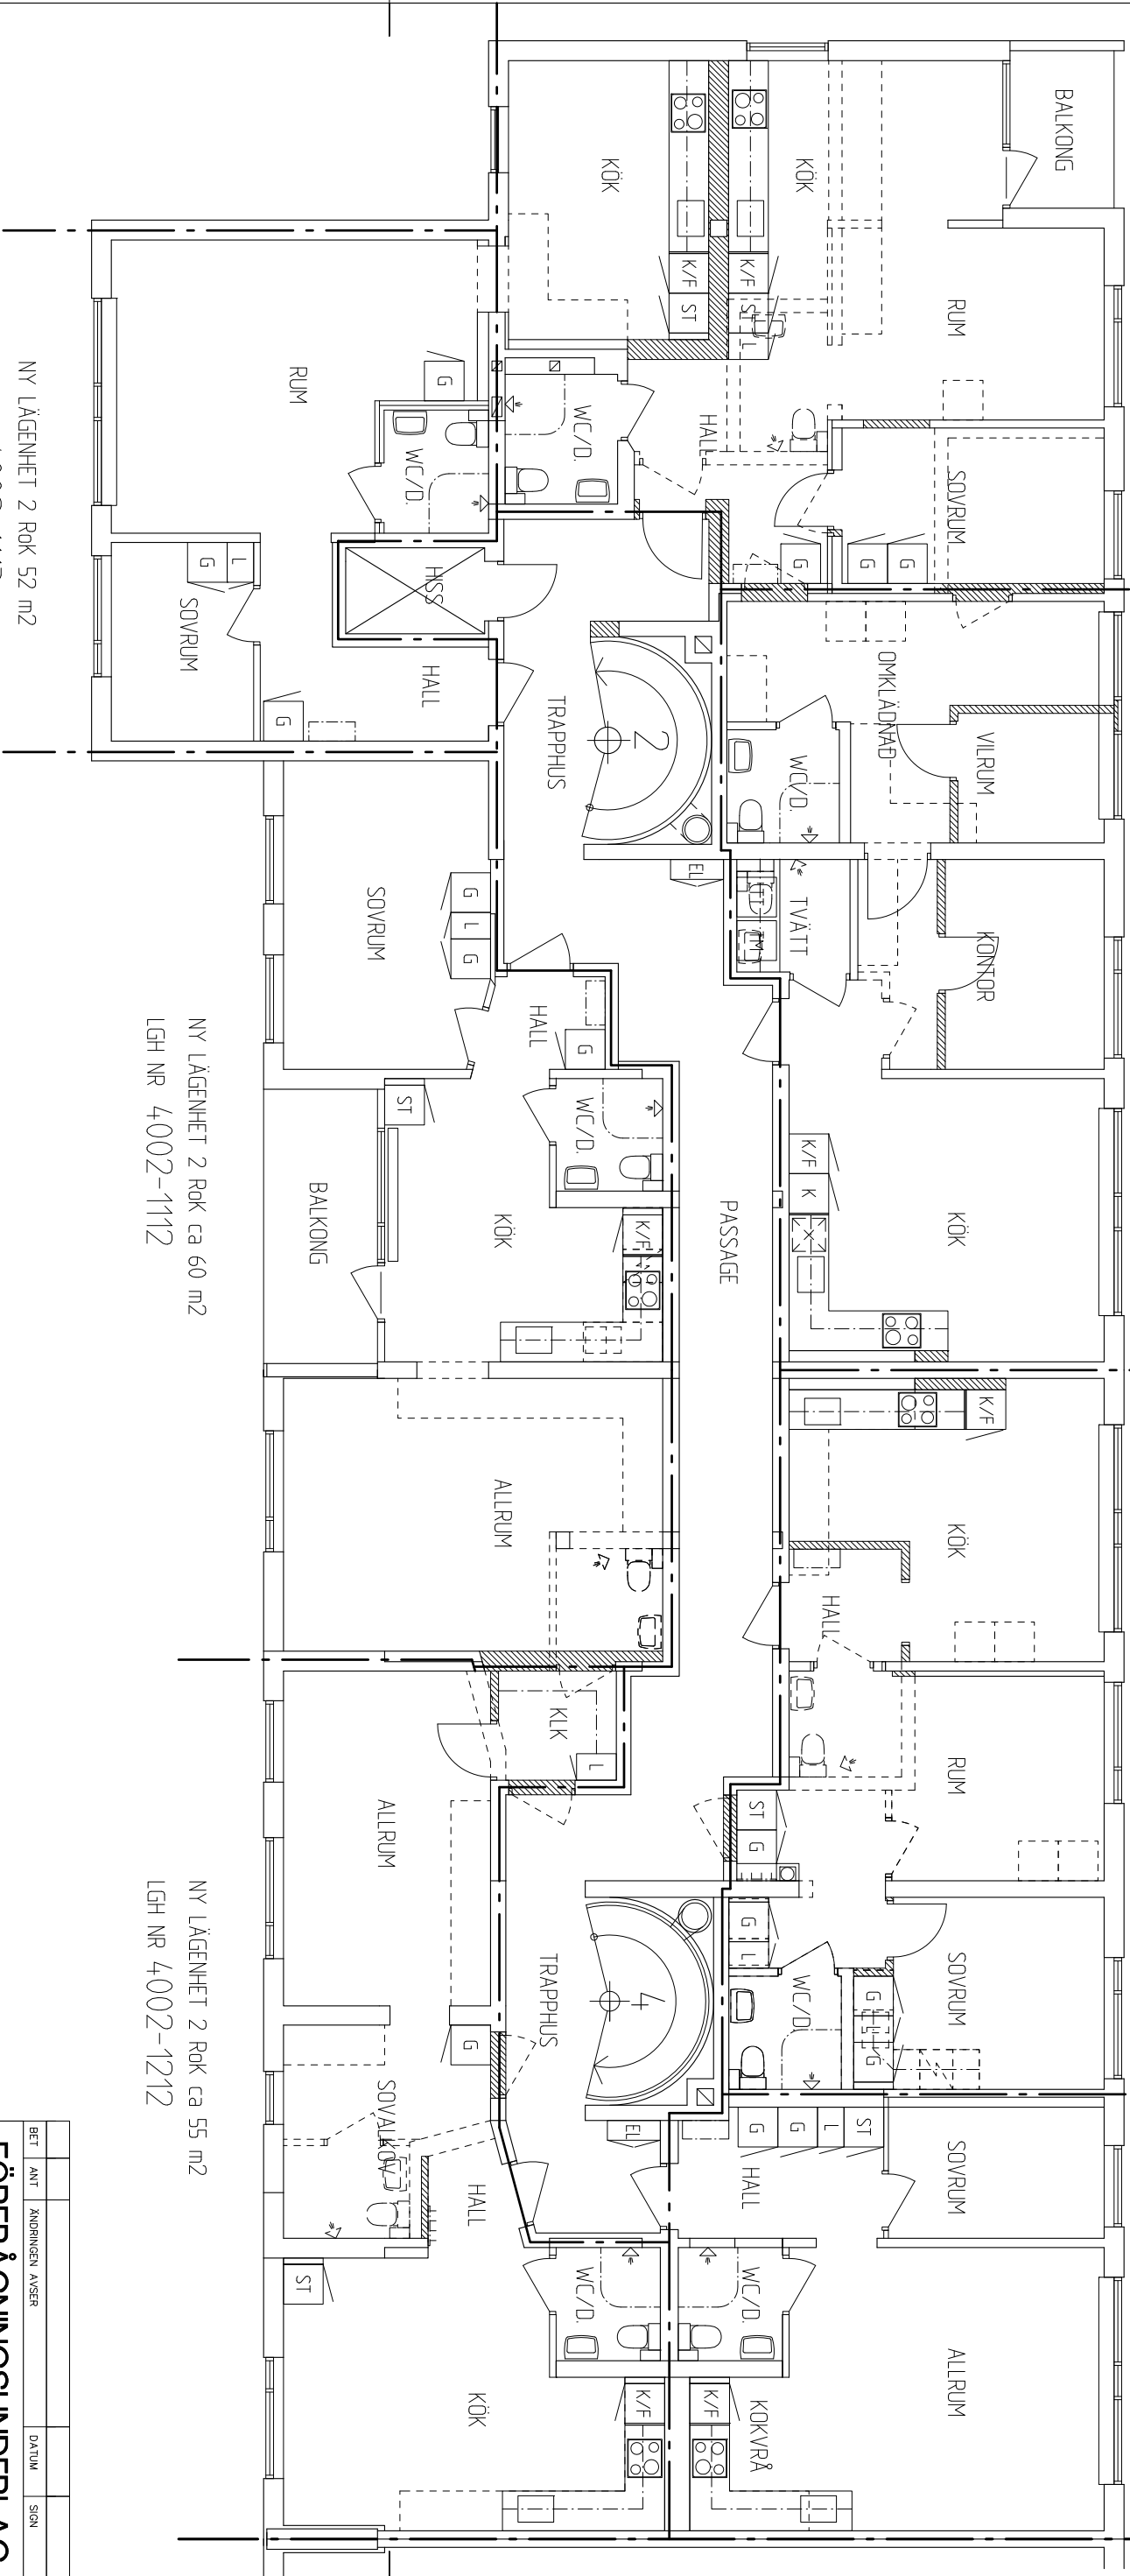


NY LÄGENHET 2 ROK 52 m2
LGH NR 4002-1113

NY LÄGENHET 2 ROK ca 60 m2
LGH NR 4002-1112

NY LÄGENHET 2 ROK ca 55 m2
LGH NR 4002-1212

FÖRKLARINGAR: SE RITNING NR A40.0-10

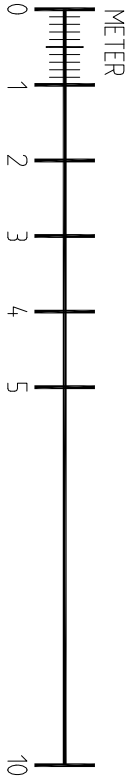


BET	ANT	ÄNDRINGEN	ANSER	DATUM	SIGN
FÖRFRÅGNINGSUNDERLAG 2025-01-28					
 AB Gavlegårdarna Utanvindsvägen 1, Box 456, 801 06 Gävle Tel: 026-17 27 00 www.gavlegardarna.se					
UPPRÄTTAD AV					
CW Byggekonsult AB Gornlevägen 94, 818 96 Hedesunda Tel: 070-232 09 33 / 070-367 16 86 e-mail: cwbygg@telia.com					
UPDRAG NR	1370	RITAD/KONSTR. AV	HANDLÄGGARE		
		IW	IW		
DATUM	ANSVARIG				
2025-01-28	I. Waller				
SÄTRA 58:4, Pinnmovägen 2 o 4					
OMBYGGNAD 2025					
PLAN VÅNING 1 TR					
SKALA	NUMMER		BET		
1:100 (A3)			A40.1-111		

LGH NR 4002-1124
NY LÄGENHET 2 ROK ca 48 m2

LGH NR 4002-1121
NY SAMLINGSSAL 2 ROK ca 59 m2

LGH NR 4002-1223
NY LÄGENHET 2 ROK ca 54 m2

LGH NR 4002-1221
BEF LÄGENHET 2 ROK 40 m2

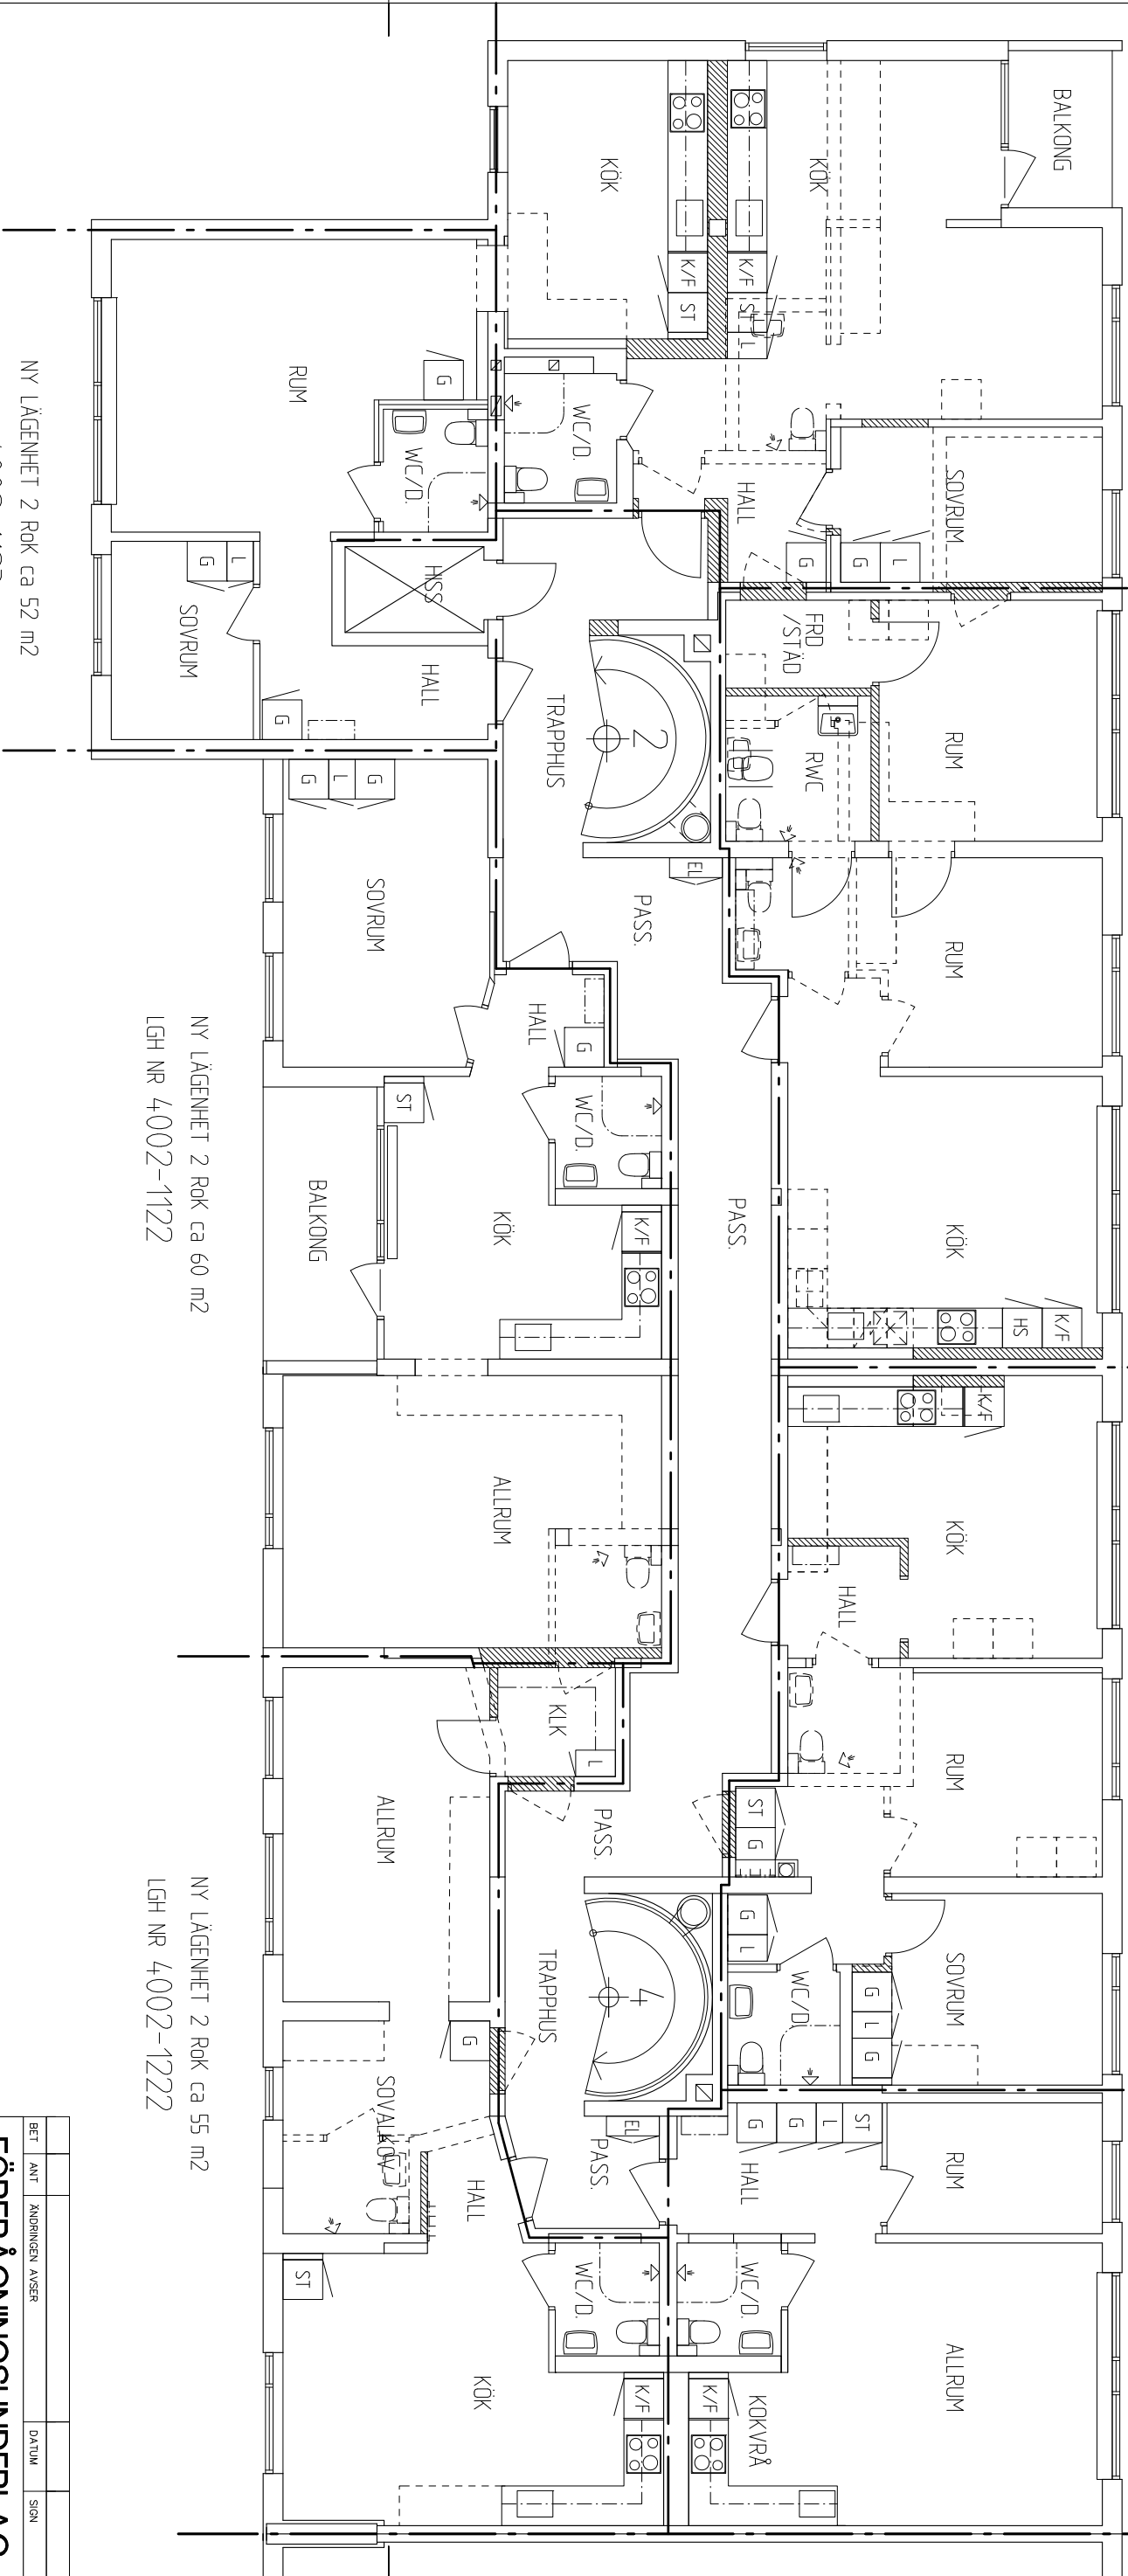


NY LÄGENHET 2 ROK ca 52 m2
LGH NR 4002-1123

NY LÄGENHET 2 ROK ca 60 m2
LGH NR 4002-1122

NY LÄGENHET 2 ROK ca 55 m2
LGH NR 4002-1222


FÖRKLARINGAR: SE RITNING NR A40.0-10

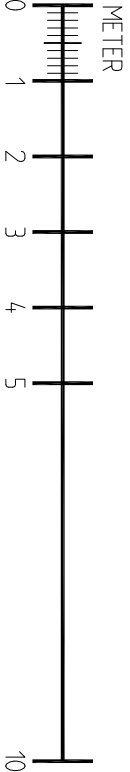

		BET		
ANT	ÄNDRINGEN ANSER	BET		
		DATUM	SIGN	
FÖRFRÅGNINGSUNDERLAG				
2025-01-28				
 AB Gavlegårdarna Utanvindsvägen 1, Box 456, 801 06 Gävle Tel: 026-17 27 00 www.gavlegardarna.se				
UPPRÄTTAD AV				
GAVLEGÅRDARNA				
CW Byggekonsult AB				
Gavlevägen 94, 818 96 Hedesunda				
Tel. 070-232 09 33 / 070-367 16 86				
e-mail: cwbygg@telia.com				
UPPRAG NR	RITAD / KONSTR. AV	ANSVARIG	HANDLÄGGARE	
1370	IW	IW	IW	
DATUM				
2025-01-28 I. Waller				
SÄTRA 58:4, Pinnmovägen 2 o 4				
OMBYGGNAD 2025				
PLAN VÅNING 2 TR				
SKALA				
1:100 (A3)				
NUMMER				
A40.1-112				
BET				

FÖRSLAG PLACERING

MARKMÄTARSKÅP I
SAMRÅD MED GÄVLE ENERGI

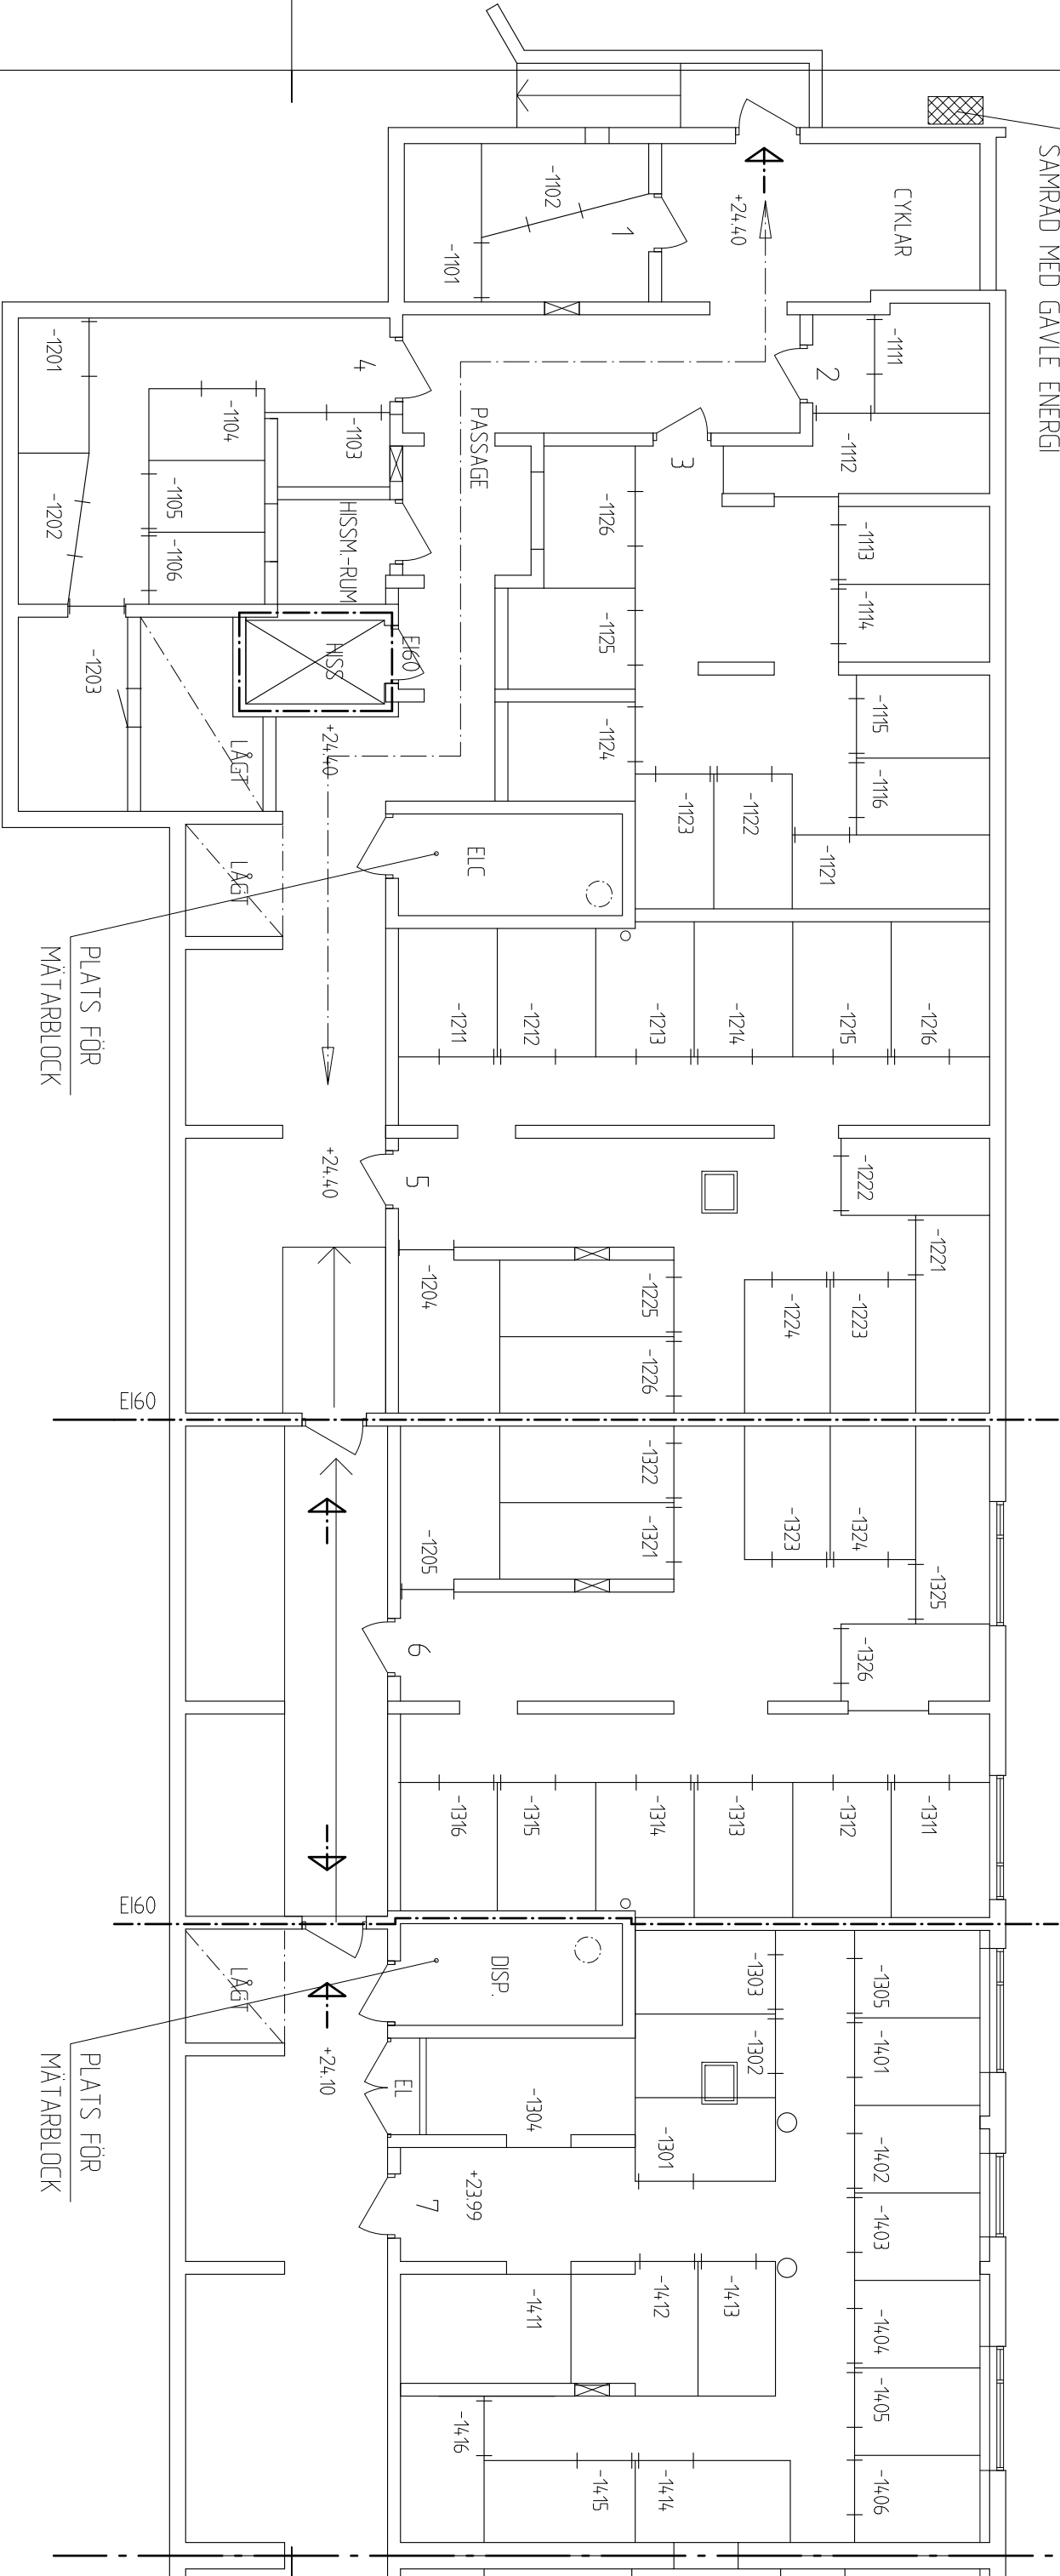

2

4

BET	ANT	ÄNDRINGEN ANSER	DATUM	SKÖT
-----	-----	-----------------	-------	------

FÖRFRÅGNINGSUNDERLAG
2025-01-28



AB Gävlegårdarna
Utanvindsvägen 1,
Box 456, 801 06 Gävle
Tel: 026-17 27 00
www.gavlegardarna.se

UPPRÄTTAD AV
CW Byggekonsult AB
Gornvägen 94, 818 96 Hedesunda
Tel: 070-232 09 33 / 070-367 16 86
e-mail: cwbygg@telia.com


UPDRAG NR
1370
RITAD/KONSTR. AV
IW
HANDLÄGGARE
IW


DATUM
2025-01-28
ANSVARIG
I. Waller

SÄTRA 58:4, Pinnmovägen 2 0 4
OMBYGGNAD 2025

KÄLLARPLAN del entré 2 0 4


SKALA	NUMMER	BET
1:100 (A3)	A40.1-101	

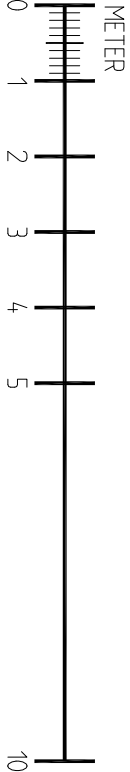

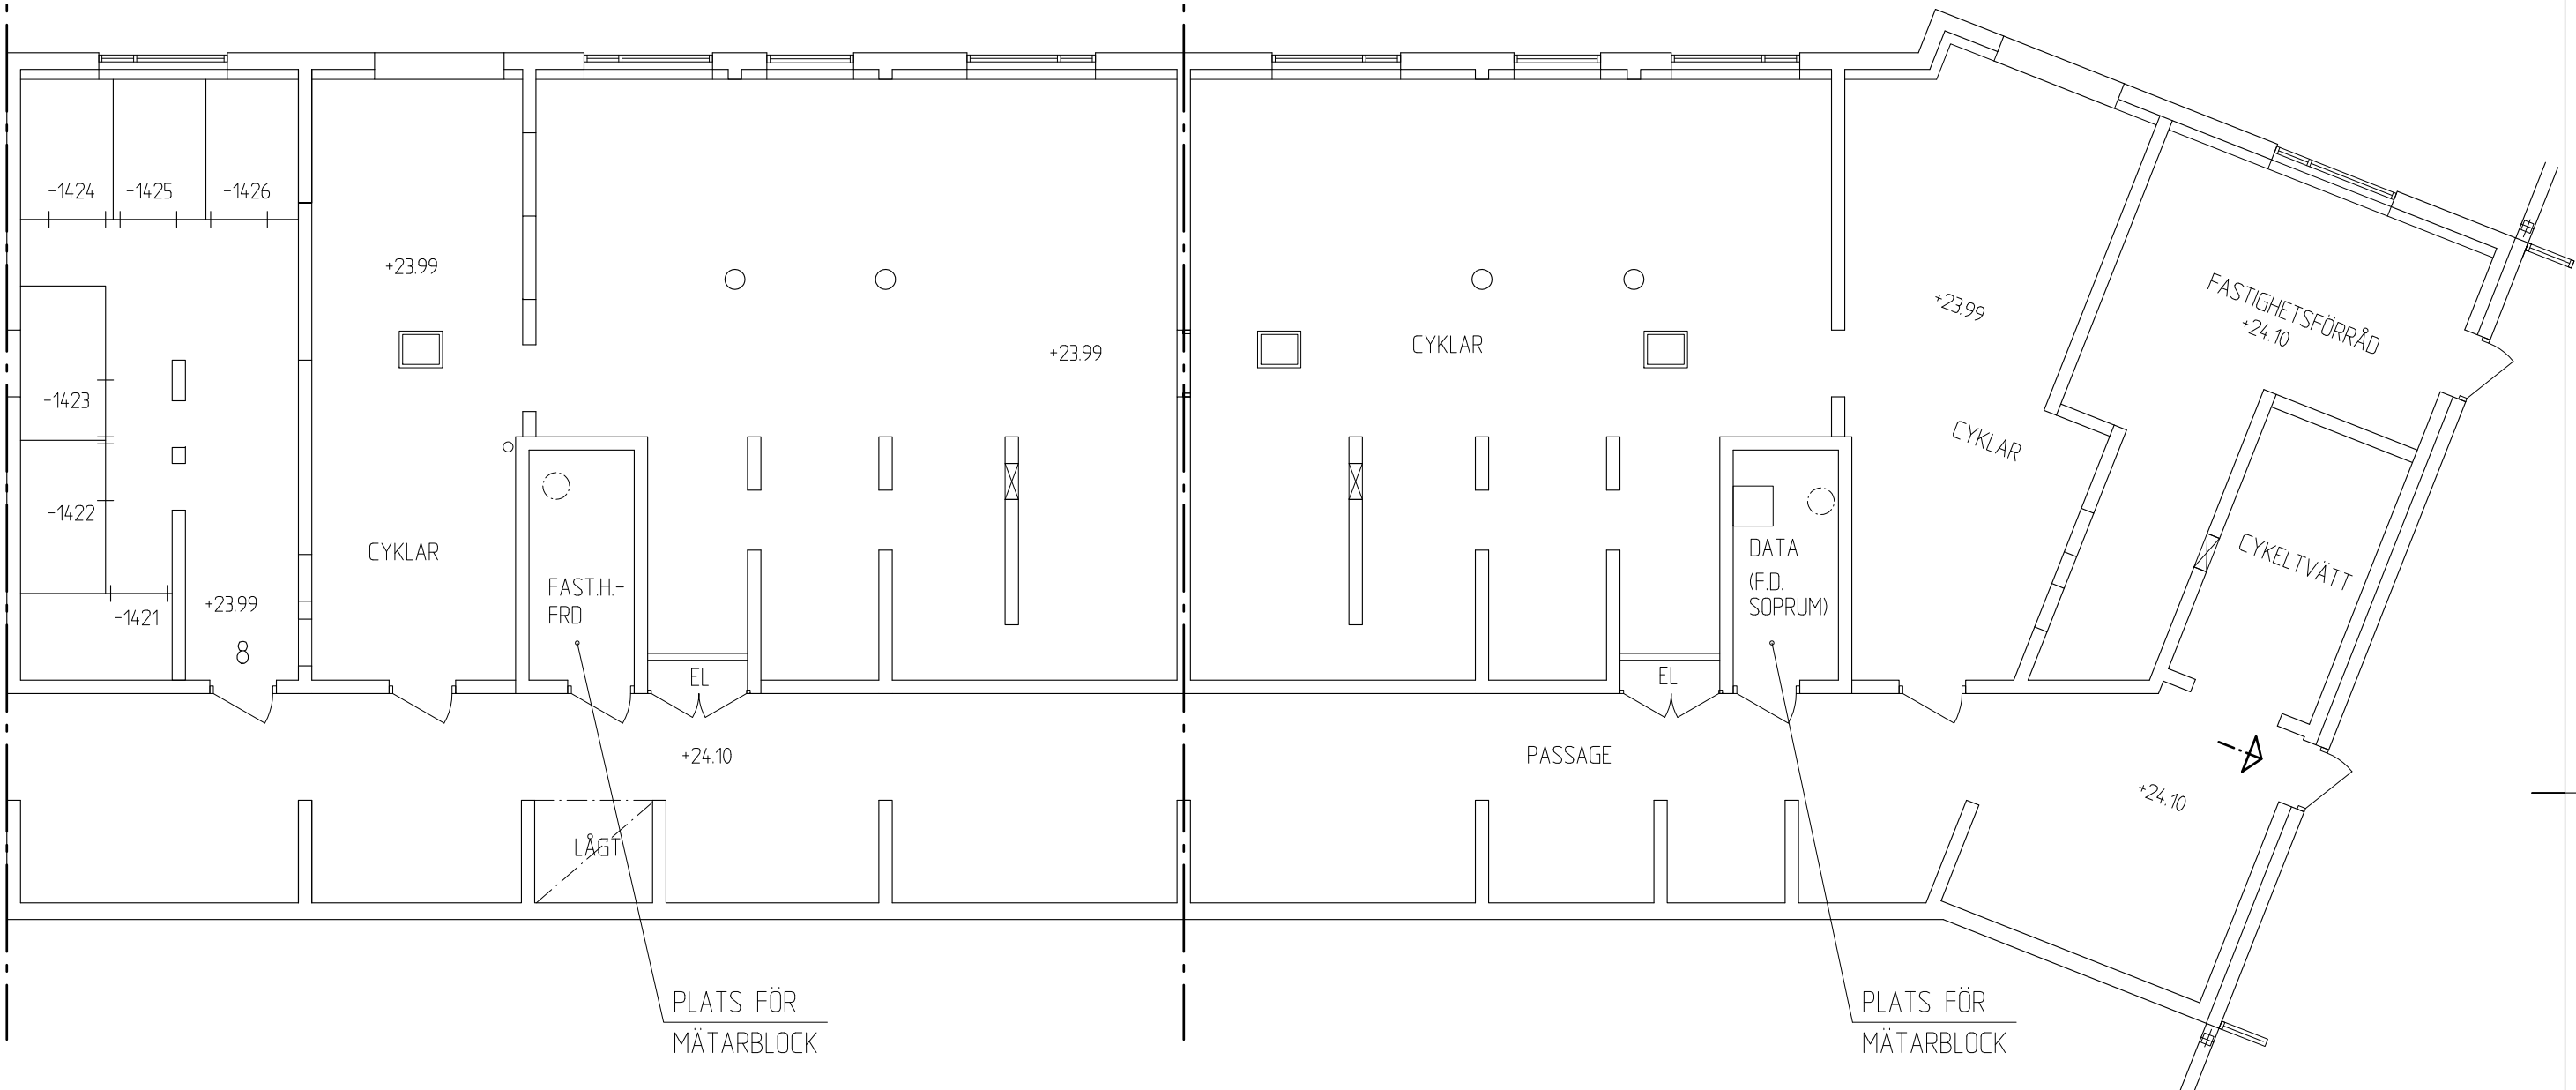


6


8

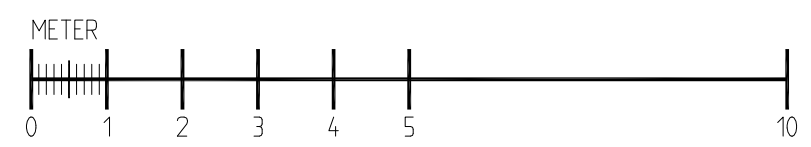

BET	ANT	ÄNDRINGEN AVSER	DATUM SIGN
FÖRFRÅGNINGSUNDERLAG 2025-01-28			
		AB Gavlegårdarna Utanvindsvägen 1, Box 456, 801 06 Gävle Tel: 026-17 27 00 www.gavlegardarna.se	
UPPRÄTTAD AV		CW Byggkonsult AB Gamlevägen 94, 818 96 Hedesunda Tel. 070-232 09 33 / 070-367 16 86 e-mail: cwbygg@telia.com	
UPPDRAG NR 1370	RITAD/KONSTR AV IW	HANDLÄGGARE IW	
DATUM 2025-01-28	ANSVARIG l. Waller		
SÄTRA 58:4, Pinnmovägen 2 o 4 OMBYGGNAD 2025			
KÄLLARPLAN del entré 6 o 8			
SKALA 1:100 (A3)	NUMMER A40.1-201		BET

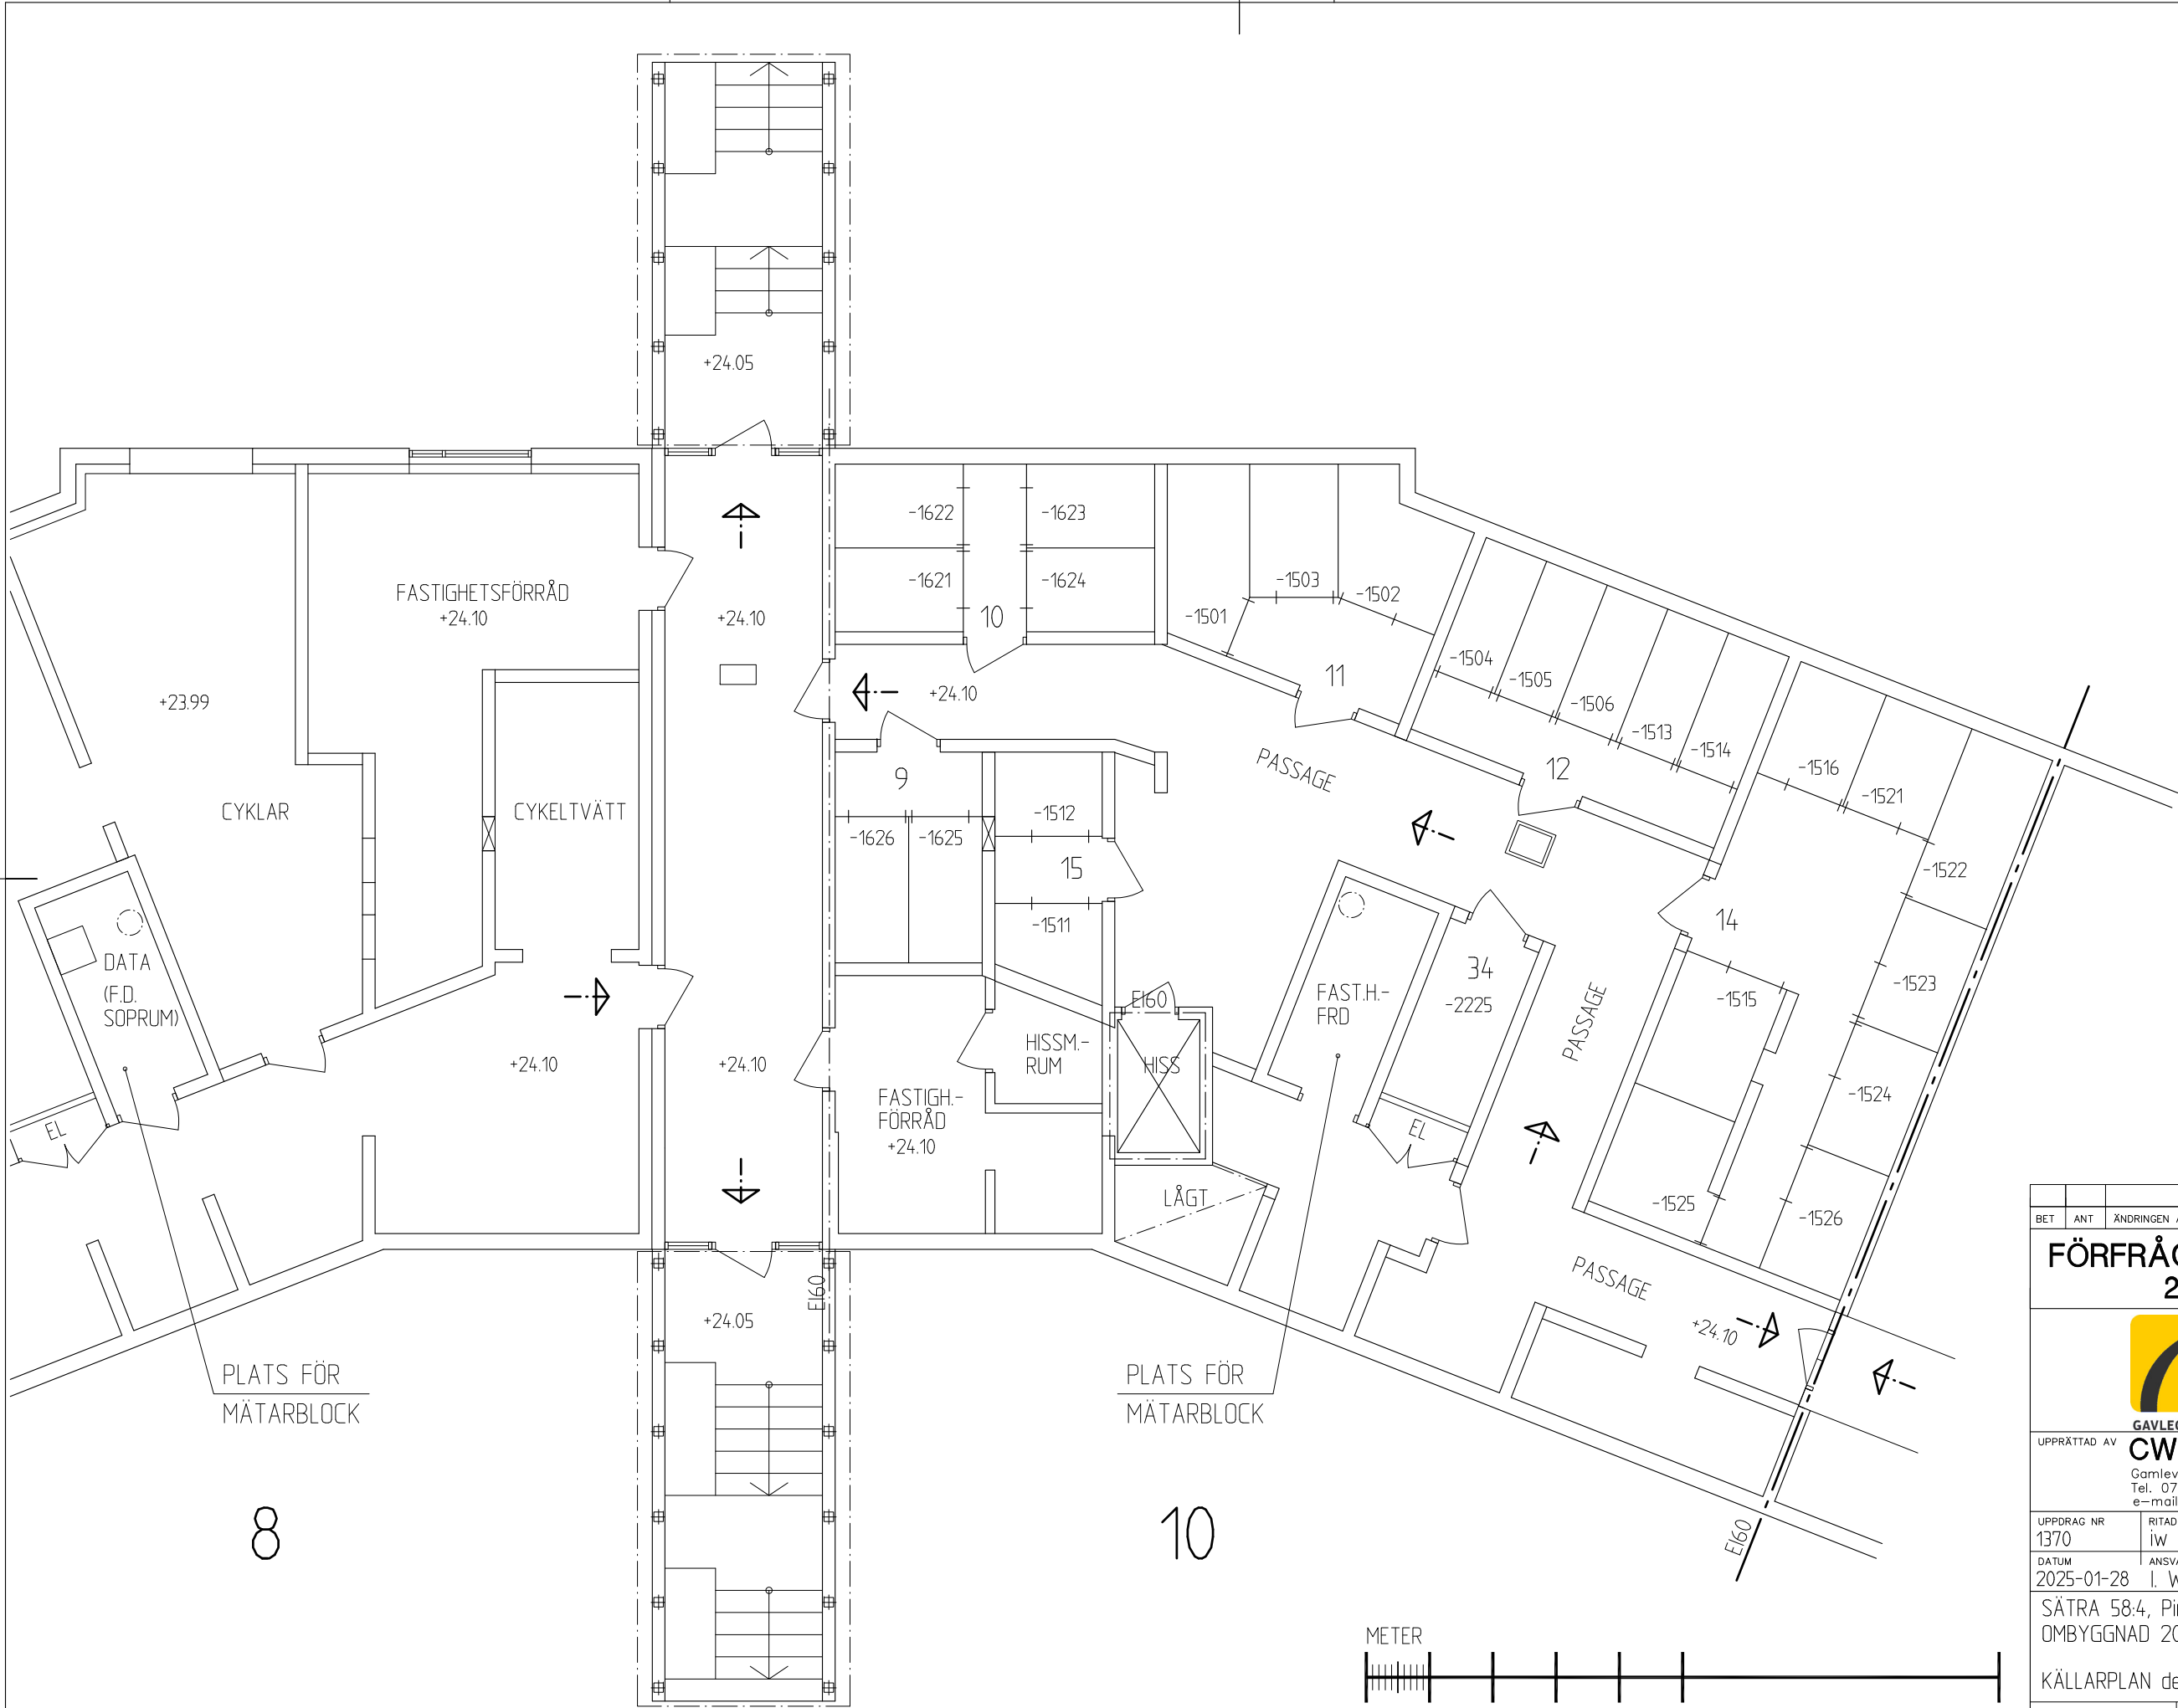

BET		ANT	ÄNDRINGEN AVSER	DATUM	SIGN
FÖRFRÅGNINGSUNDERLAG 2025-01-28					
			AB Gavlegårdarna Utanvindsvägen 1, Box 456, 801 06 Gävle Tel: 026-17 27 00 www.gavlegardarna.se		
UPPRÄTTAD AV			CW Byggkonsult AB Gamlevägen 94, 818 96 Hedesunda Tel. 070-232 09 33 / 070-367 16 86 e-mail: cwbygg@telia.com		
UPPDRAG NR 1370		RITAD/KONSTR AV iw		HANDLÄGGARE iw	
DATUM 2025-01-28		ANSVARIG l. Waller			
SÄTRA 58:4, Pinnmovägen 2 o 4 OMBYGGNAD 2025					
KÄLLARPLAN del entré 8 o 10					
SKALA 1:100 (A3)		NUMMER A40.1-301			BET

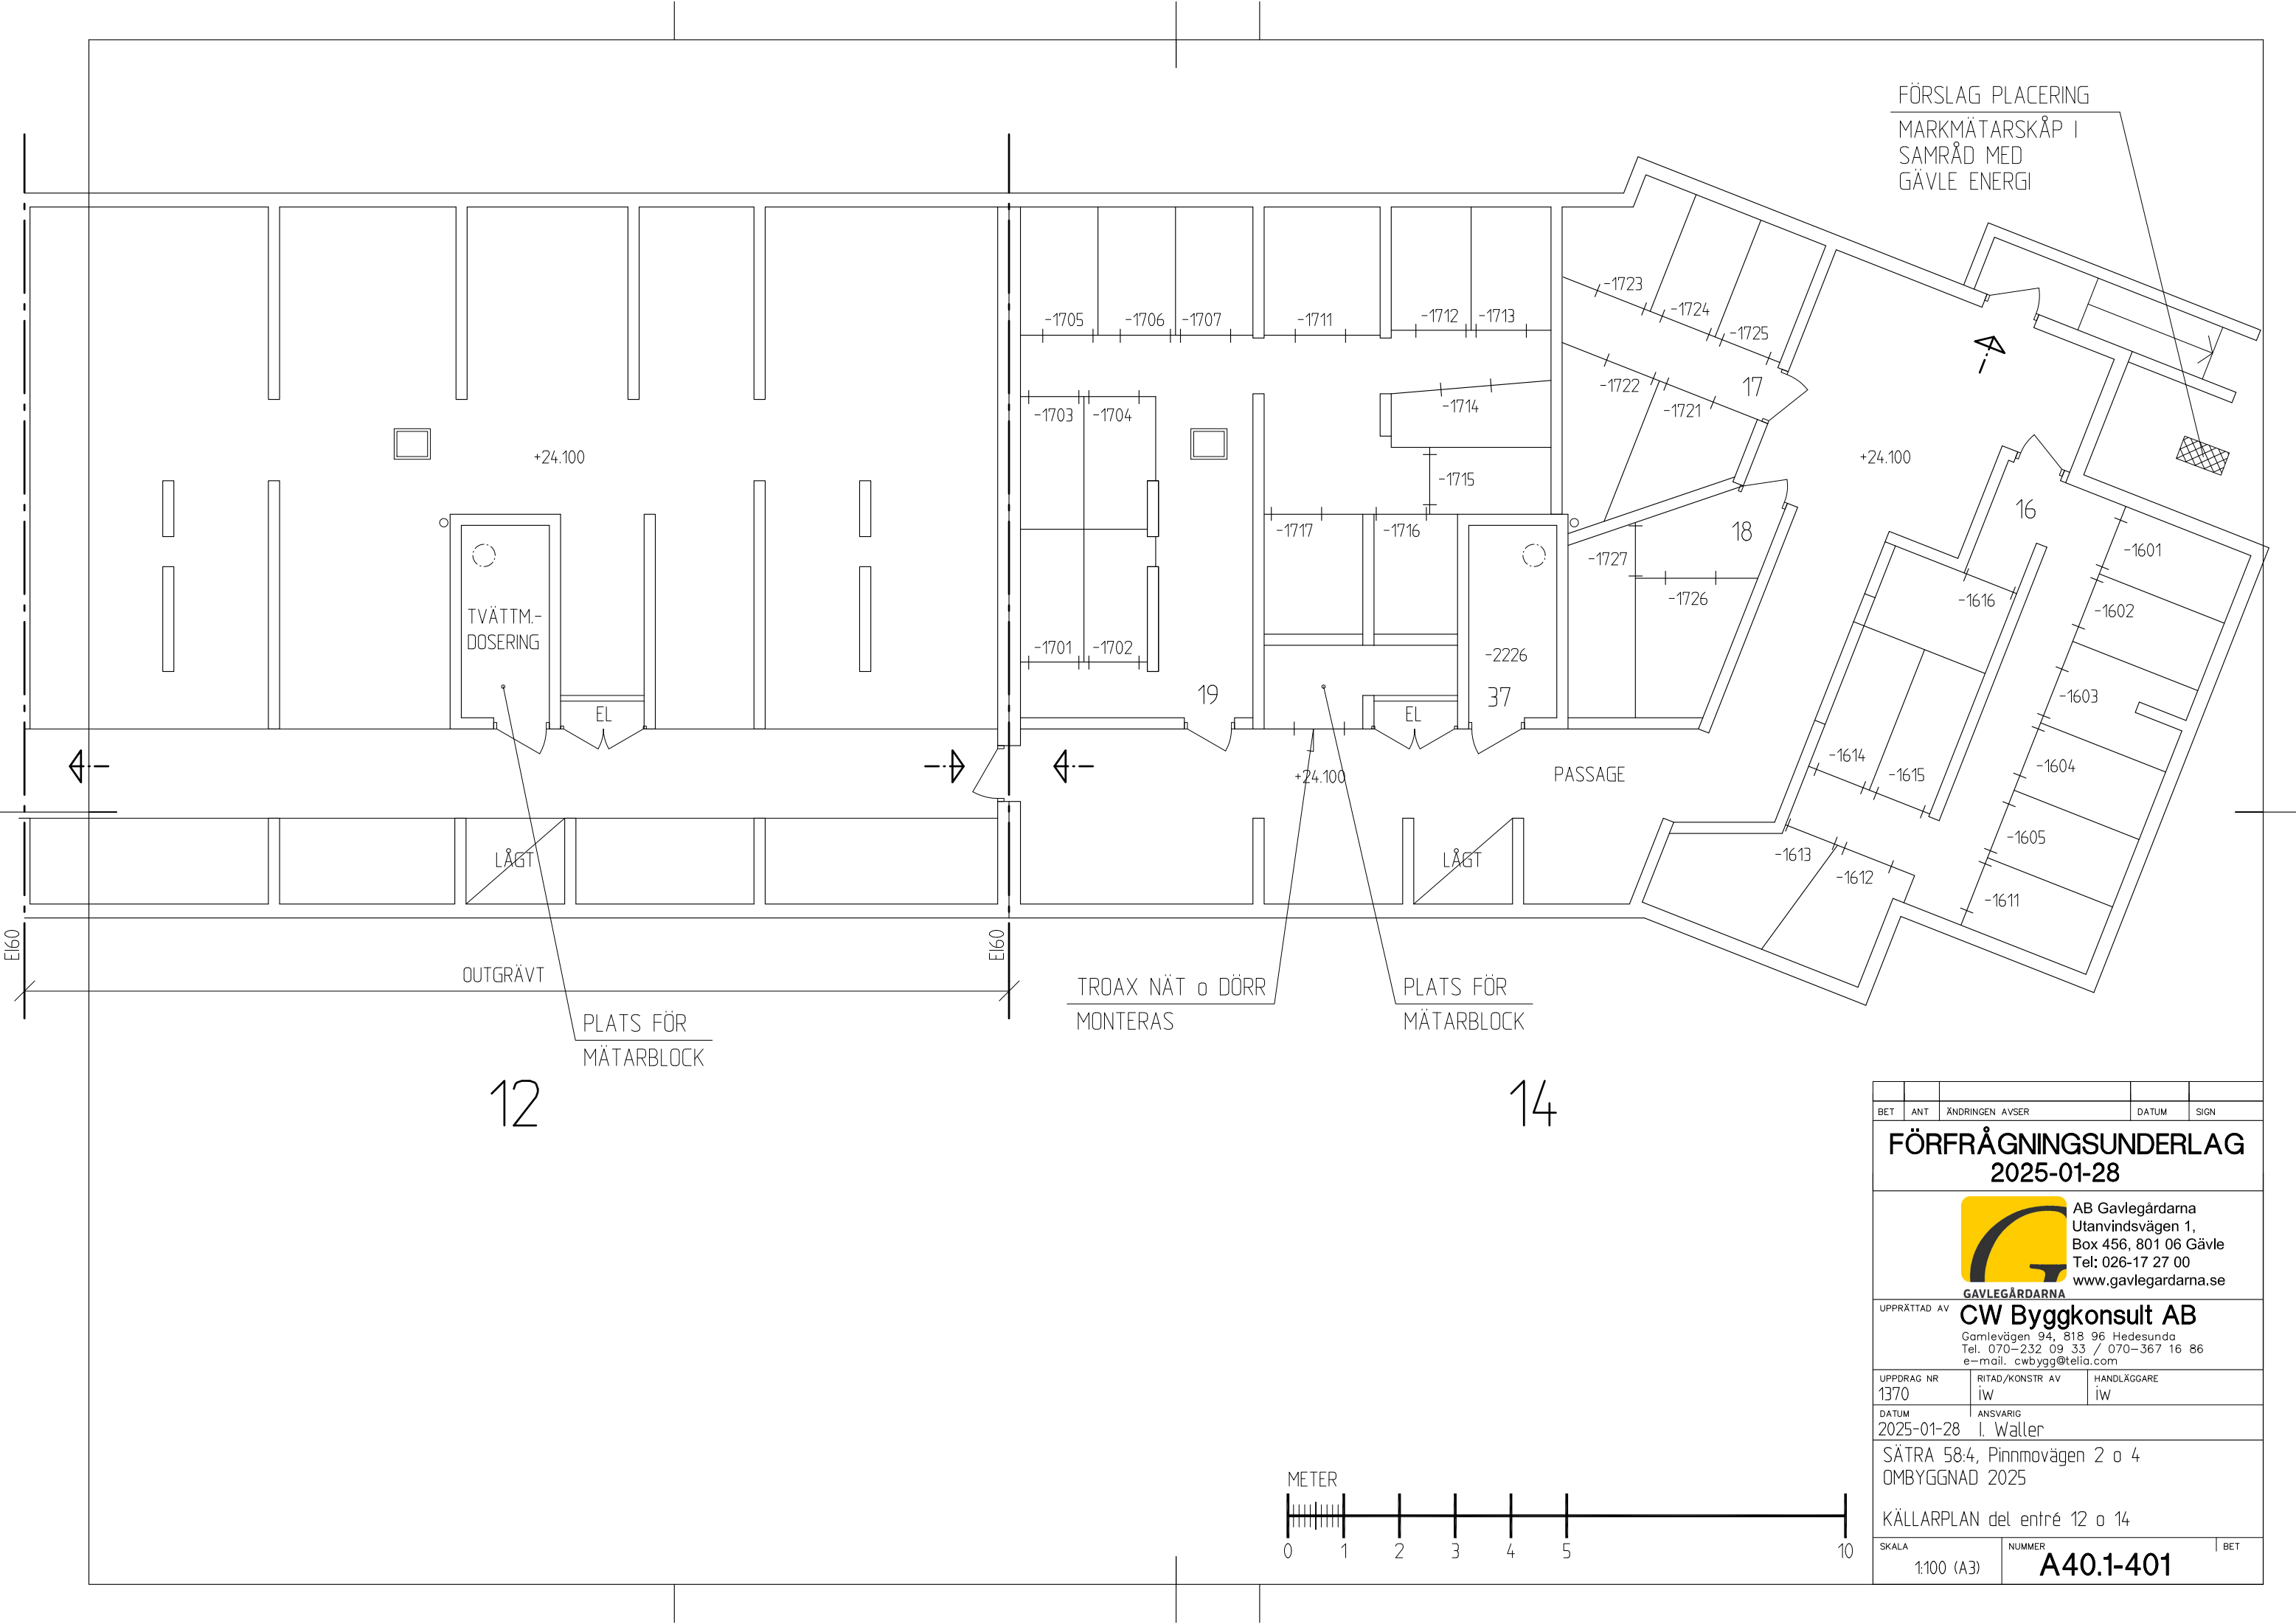

FÖRSLAG PLACERING
MARKMÄTARSKÅP I
SAMRÅD MED
GÄVLE ENERGI



+24.100

+24.100

+24.100

OUTGRÄVT

TROAX NÄT o DÖRR
MONTERAS

PLATS FÖR
MÄTARBLOCK

PLATS FÖR
MÄTARBLOCK

PASSAGE

TVÄTTM.-
DOSERING

EL

EL

LÅGT

LÅGT

-1705

-1706

-1707

-1711

-1712

-1713

-1703

-1704

-1714

-1715

-1723

-1724

-1725

-1722

-1721

17

18

-1727

-1726

-1701

-1702

-1717

-1716

-2226

37

-1601

-1602

-1603

-1604

-1605

-1611

-1614

-1615

-1613

-1612


12

14


METER




BET	ANT	ÄNDRINGEN AVSER	DATUM	SIGN
FÖRFRÅGNINGSUNDERLAG 2025-01-28				
		AB Gavlegårdarna Utanvindsvägen 1, Box 456, 801 06 Gävle Tel: 026-17 27 00 www.gavlegardarna.se		
UPPRÄTTAD AV		CW Byggkonsult AB Gamlevägen 94, 818 96 Hedesunda Tel. 070-232 09 33 / 070-367 16 86 e-mail. cwbygg@telia.com		
UPPDRAG NR 1370	RITAD/KONSTR AV iW	HANDLÄGGARE iW		
DATUM 2025-01-28	ANSVARIG I. Waller			
SÄTRA 58:4, Pinnmovägen 2 o 4 OMBYGGNAD 2025				
KÄLLARPLAN del entré 12 o 14				
SKALA 1:100 (A3)		NUMMER A40.1-401		BET

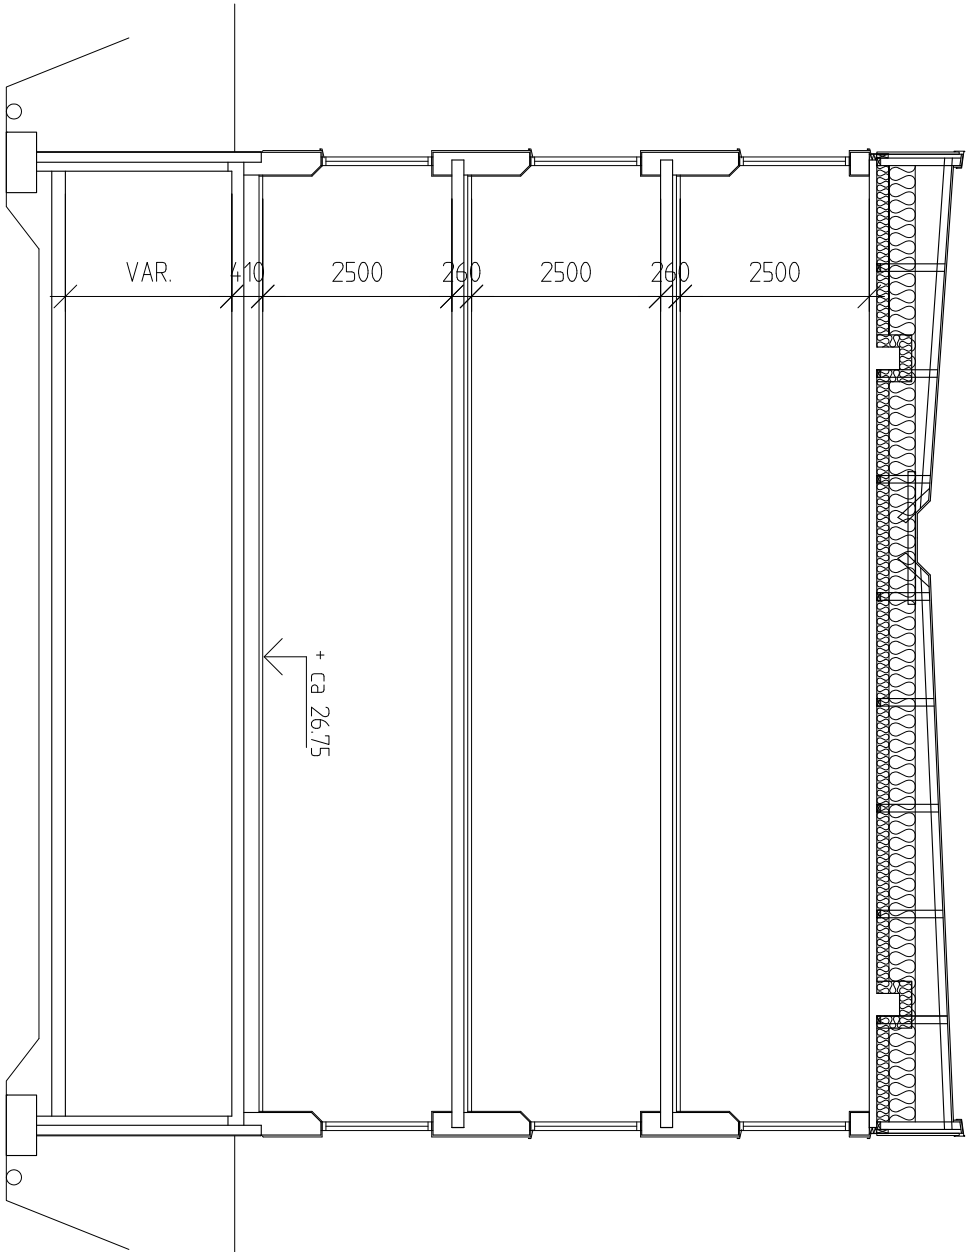

Sektion

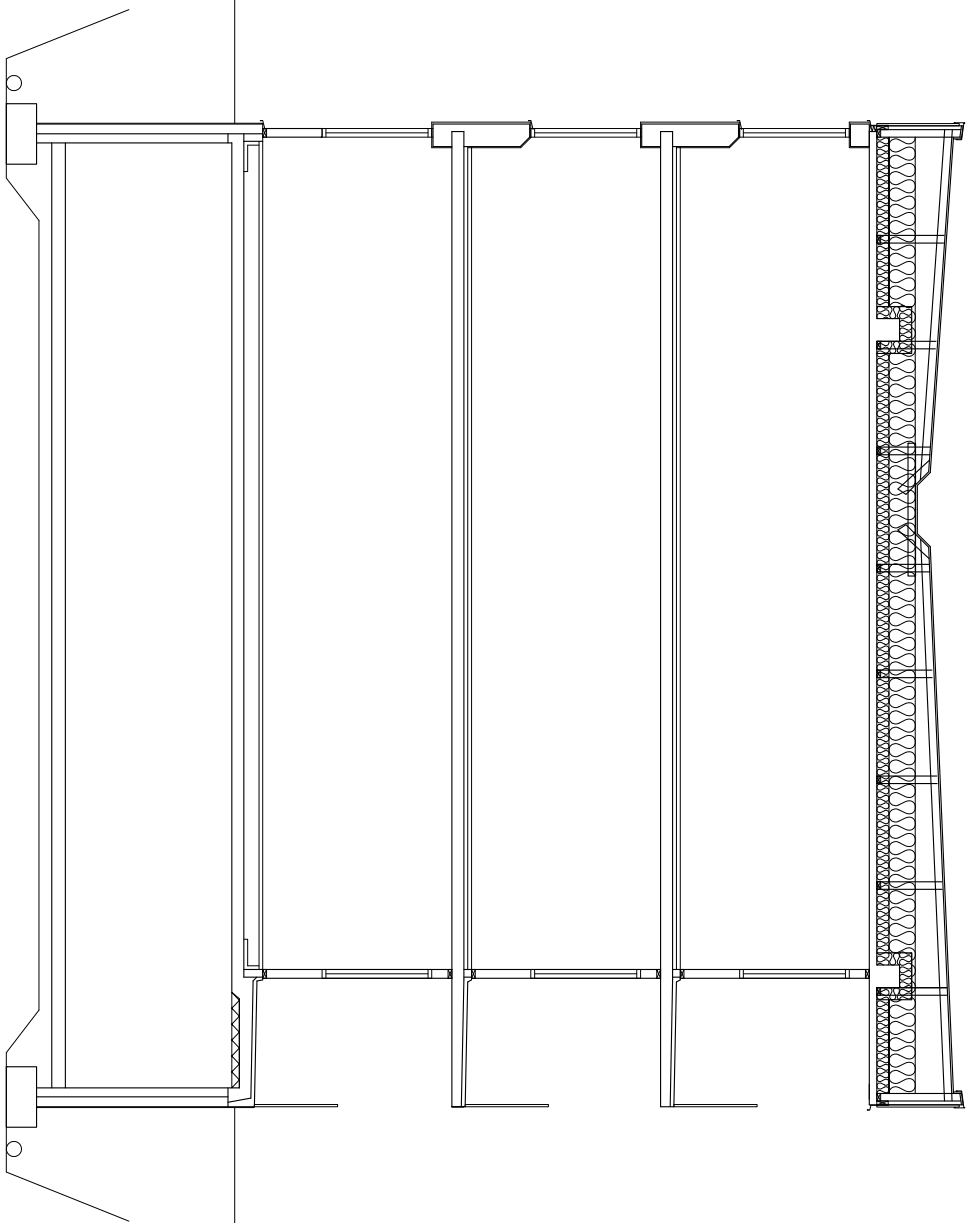

Sektion genom balkonger

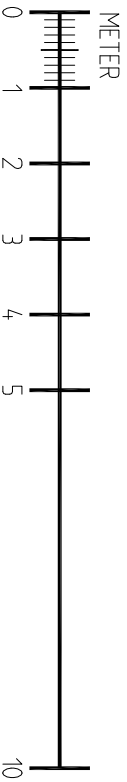

--	--	--	--	--

BET	ANT	ÄNDRINGEN ANSER	DATUM	SIGN
-----	-----	-----------------	-------	------

FÖRFRÅGNINGSUNDERLAG
2025-01-28



AB Gavlegårdarna
Utanvindsvägen 1,
Box 456, 801 06 Gävle
Tel: 026-17 27 00
www.gavlegardarna.se

UPPRÄTTAD AV	GAVLEGÅRDARNA			
	CW Byggekonsult AB			
	Gornivägen 94, 818 96 Hedesunda			
	Tel: 070-232 09 33 / 070-367 16 86			
	e-mail: cwbygg@telia.com			


UPPRAG NR	RITAD/KONSTR AV	ANSVARIG	HANDLÄGGARE
1370	IW	IW	IW

DATUM	ANSVARIG
2025-01-28	I. Waller


SÄTRA 58:4, Pinnmovägen 2 o 4
OMBYGGNAD 2025

SEKTIONER


SKALA	NUMMER	BET
1:100 (A3)	A40.2-101	

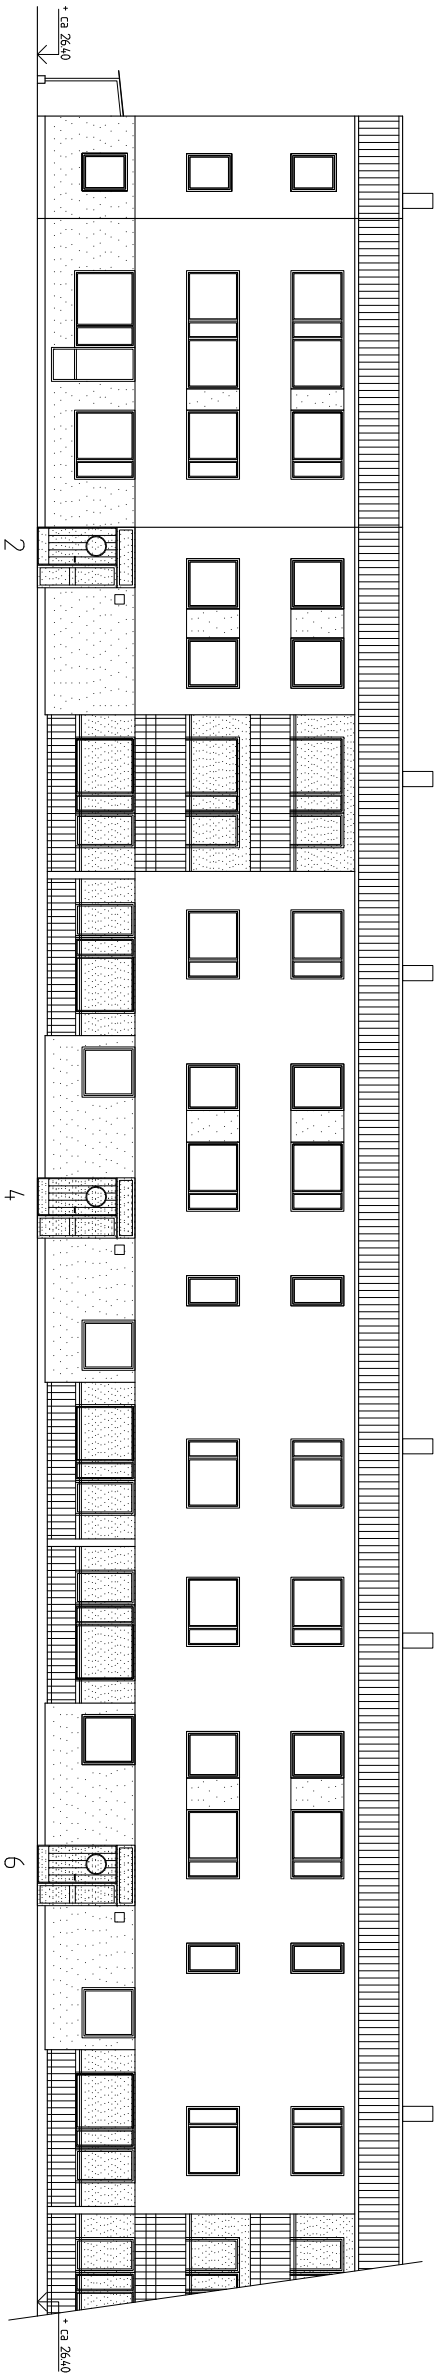


Fasad mot väster

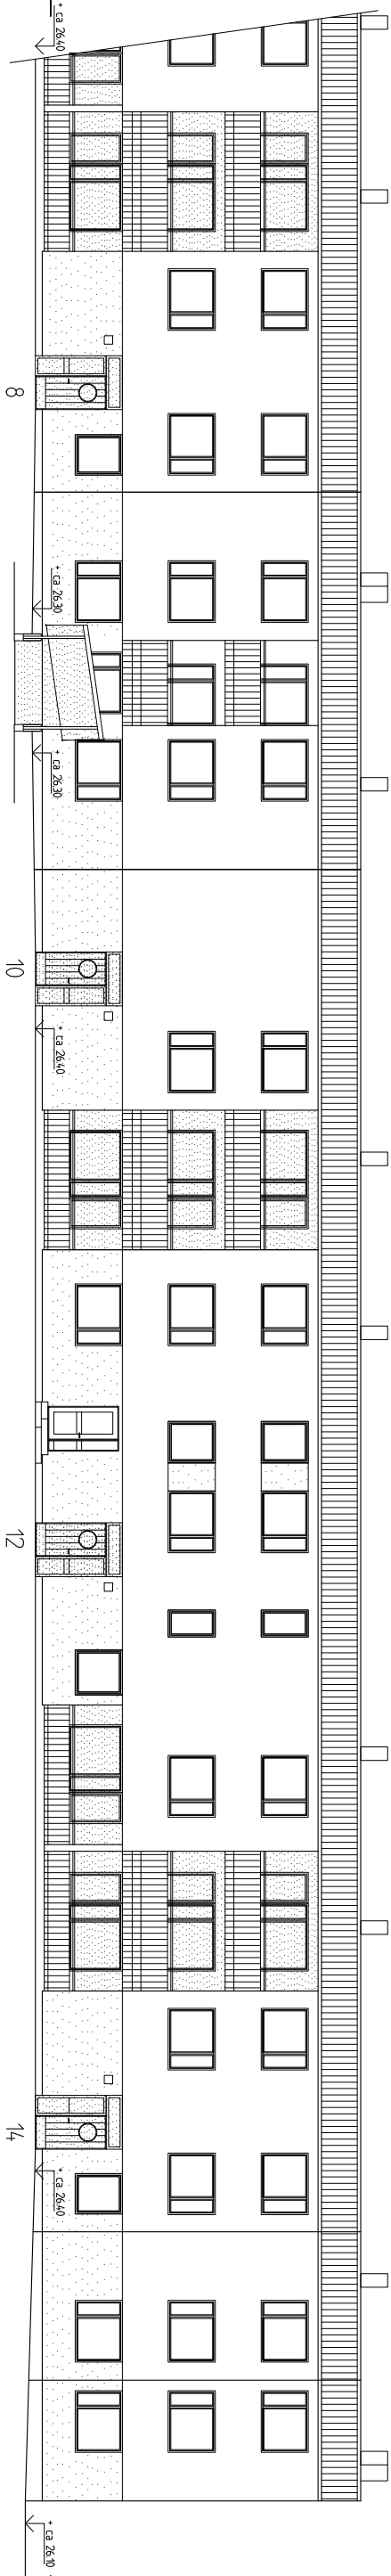


Fort. Fasad mot väster

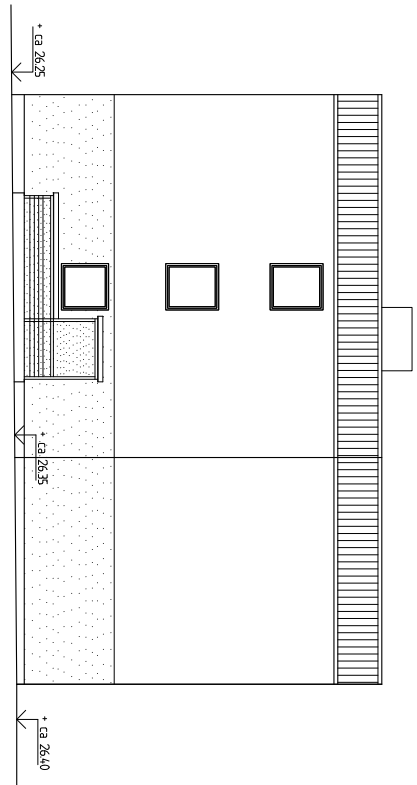


Fasad mot norr

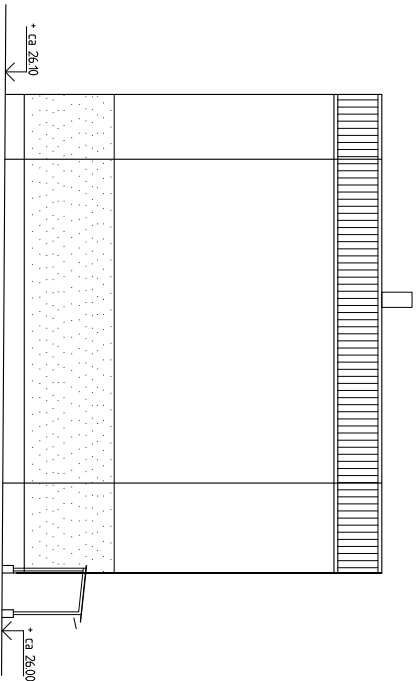


Fasad mot söder

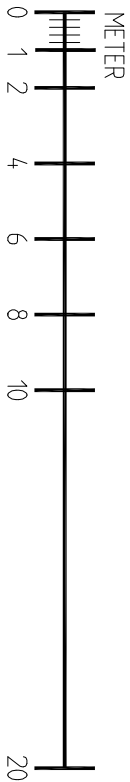

BET	ANT	ÄNDRINGEN ANSER	DATUM	SIGN	
FÖRFRÅGNINGSUNDERLAG 2025-01-28					
 AB Gavlegårdarna Utanvindsvägen 1, Box 456, 801 06 Gävle Tel: 026-17 27 00 www.gavlegardarna.se					
UPPRÄTTAD AV					
CW Byggekonsult AB Garnkvägen 94, 818 96 Hedesunda Tel: 070-232 09 33 / 070-367 16 86 e-mail: cwbygg@telia.com					
UPDRAG NR		1370	RITAD/KONSJ. AV	HANDLÄGGARE	
		iW		iW	
DATUM		ANSVARIG			
2025-01-28		I. Waller			
SÄTRA 58:4, Pinnmovägen 2 o 4					
OMBYGGNAD 2025					
FASADER MOT VÄSTER, NÖRR o SÖDER					
SKALA	NUMMER		BET		
1200 (A3)	A40.3-101				

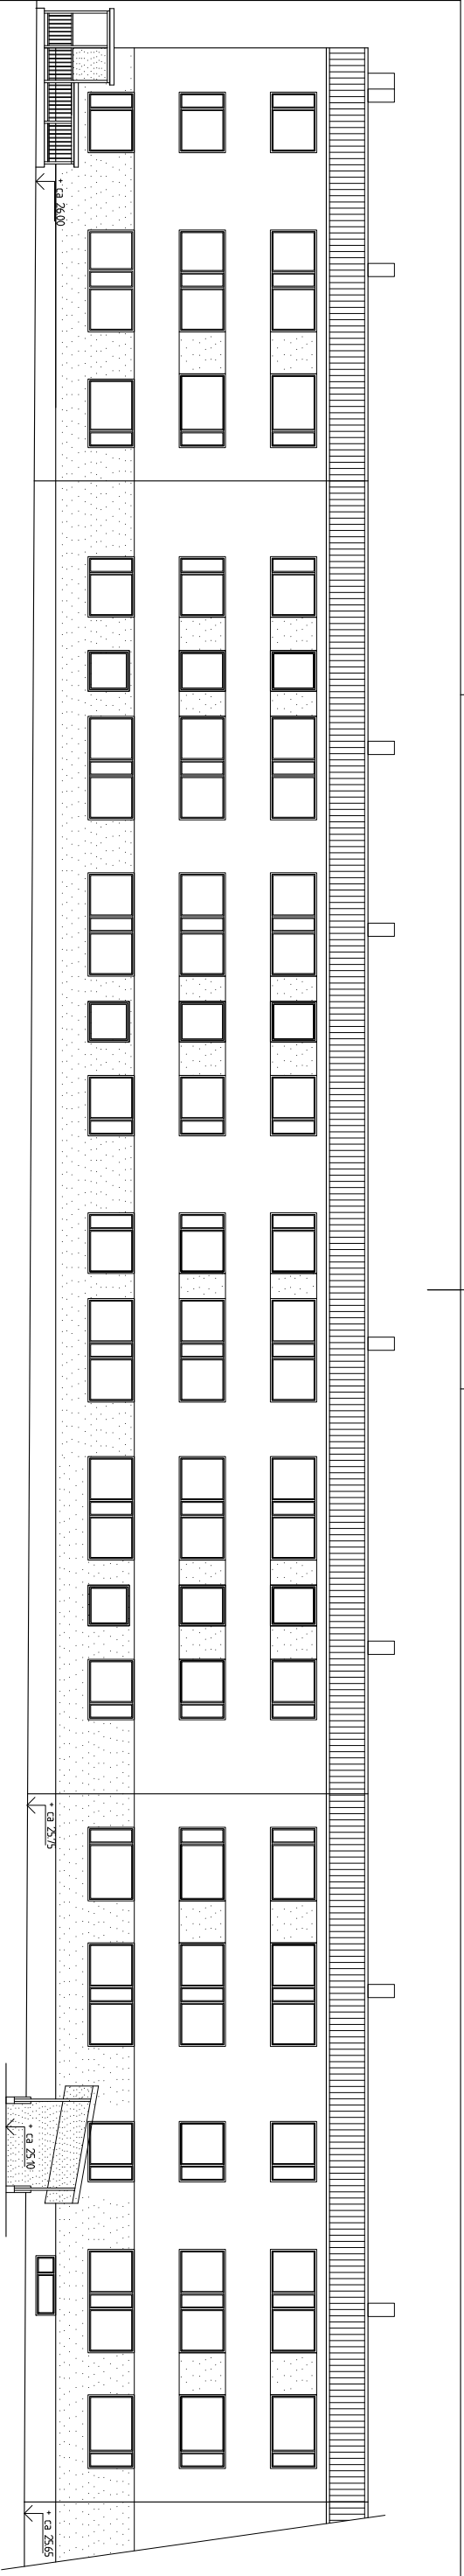

Fasad mot öster

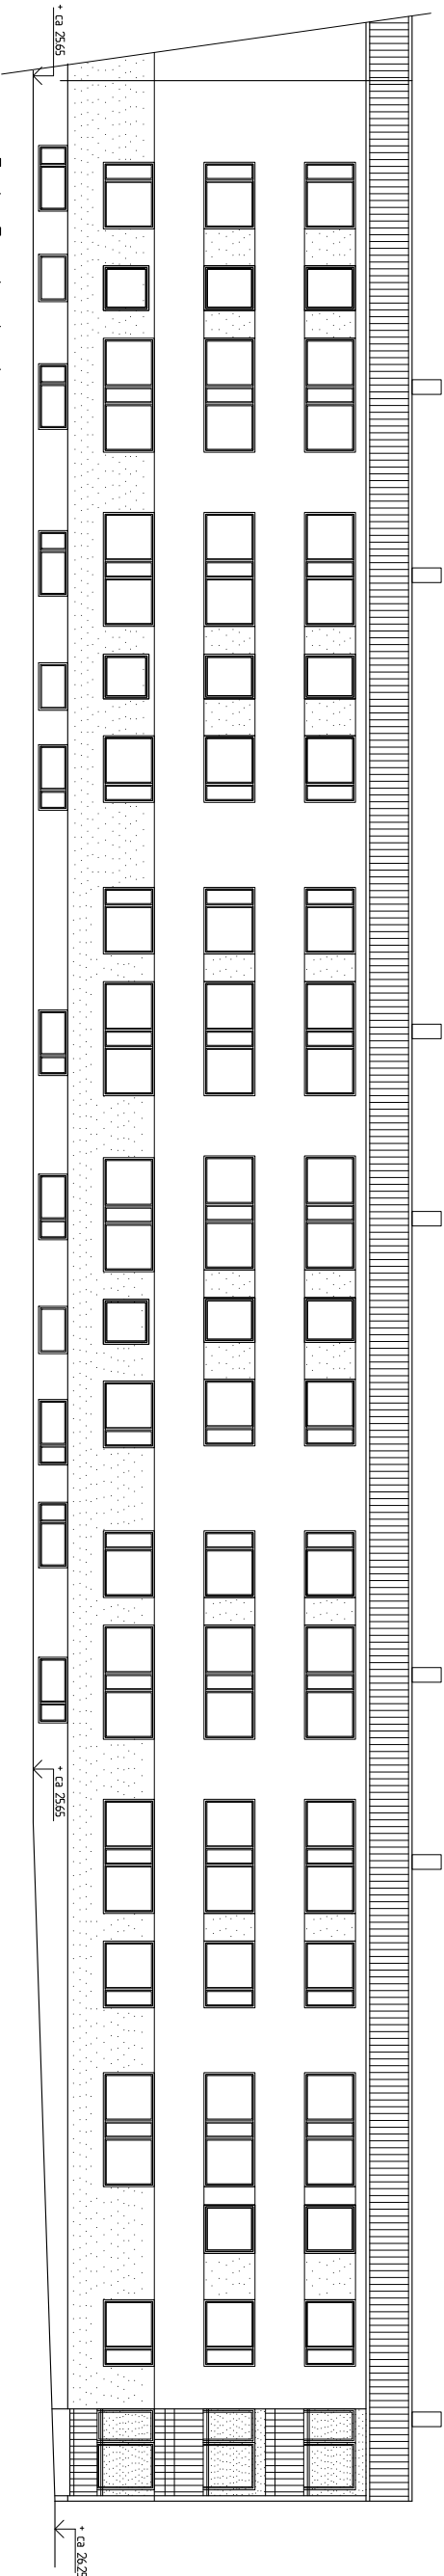

Forts. Fasad mot öster

BET	ANT	ÄNDRINGEN ANSER	DATUM	SIGN

FÖRFRÅGNINGSUNDERLAG 2025-01-28



AB Gavlegårdarna
Utanvindsvägen 1,
Box 456, 801 06 Gävle
Tel: 026-17 27 00
www.gavlegardarna.se

UPPRÄTTAD AV
CW Byggekonsult AB
Gornivägen 94, 818 96 Hedesunda
Tel: 070-232 09 33 / 070-367 16 86
e-mail: cwbygg@telia.com

UPPDRAG NR	RITAD/KONSULT AV	HANDLÄGGARE
1370	IW	IW

DATUM
2025-01-28

ANSVARIG
I. Waller

SÄTRA 58:4, Pinnmovägen 2 o 4
OMBYGGNAD 2025

SKALA	NUMMER	BET
1:200 (A3)	A40.3-102	