

HANDLINGSFÖRTECKNING

PROJEKT JÄRVA SDF KÄMPINGE 2:1 ADRESS TENSTASTRÅKET 14, TENSTA	BYGGHERR STOCKHOLMS STAD	ANSVARIG ARKITEKT M. WAHLGREN
--	-----------------------------	----------------------------------

PROJEKTNUMMER 79453	STATUS PH	UPPRÄTTAD 20250124	REVIDERAD
------------------------	--------------	-----------------------	-----------

RITNINGSNUMMER	BENÄMNING	SKALA	STATUS	DATUM	RITAD AV	REV	DATUM REV
----------------	-----------	-------	--------	-------	----------	-----	-----------

00-0 SITUATION 1:500

A-00-0-001	SITUATIONSPLAN	1:500	PH	20250124	SE/JK/AS		
------------	----------------	-------	----	----------	----------	--	--

00-1 PLANER 1:100

A-00-1-001	PLAN 09	1:200	PH	20250124	SE/JK/AS		
A-00-1-002	PLAN 10	1:200	PH	20250124	SE/JK/AS		
A-00-1-003	PLAN 11	1:200	PH	20250124	SE/JK/AS		
A-00-1-004	PLAN 12 - TAKPLAN	1:200	PH	20250124	SE/JK/AS		

00-2 SEKTIONER 1:200

A-00-2-001	SEKTIONER	1:100	PH	20250124	SE/JK/AS		
------------	-----------	-------	----	----------	----------	--	--

00-3 FASADER 1:200

A-00-3-001	FASADER	1:200	PH	20250124	SE/JK/AS		
A-00-3-002	FASADER MOT GÅRD	1:200	PH	20250124	SE/JK/AS		

01-1 SITUATION 1:500

A-01-1-001	SITUATIONSPLAN	1:500	PH	20250124	SE/JK/AS		
------------	----------------	-------	----	----------	----------	--	--

40-1 PLANER 1:200

A-40-1-001	PLAN 09	1:200	PH	20250124	SE/JK/AS		
A-40-1-002	PLAN 10	1:200	PH	20250124	SE/JK/AS		
A-40-1-003	PLAN 11	1:200	PH	20250124	SE/JK/AS		
A-40-1-004	PLAN 12	1:200	PH	20250124	SE/JK/AS		
A-40-1-005	PLAN 13 TAKPLAN	1:200	PH	20250124	SE/JK/AS		

40-2 SEKTIONER 1:200

A-40-2-001	SEKTIONER	1:100	PH	20250124	SE/JK/AS		
------------	-----------	-------	----	----------	----------	--	--



40-3 FASADER 1:200

A-40-3-001	FASADER	1:200	PH	20250124	SE/JK/AS		
A-40-3-002	FASADER MOT GÅRD	1:200	PH	20250124	SE/JK/AS		

BILAGOR

BILAGA 1	AREASAMMANSTÄLLNING - BTA	1:400	PH	20250124	SE/JK/AS		
BILAGA 2	AREASAMMANSTÄLLNING - BRA	1:400	PH	20250124	SE/JK/AS		
BILAGA 3	AREASAMMANSTÄLLNING - NTA	1:400	PH	20250124	SE/JK/AS		
BILAGA 4	GESTALTNINGSPROGRAM	-	PH	20250124	SE/JK/AS		
BILAGA 5	RUMFUNKTIONSPROGRAM	-	PH	20250124	SE/JK/AS		

TOTAL: 22

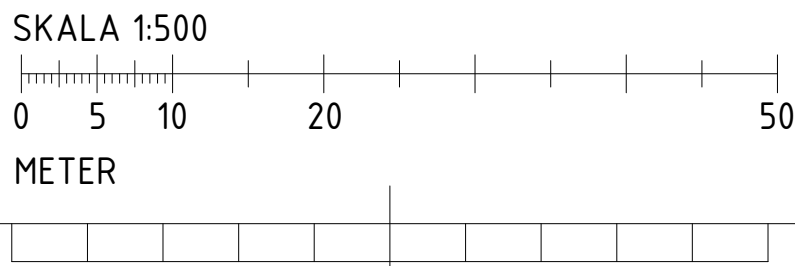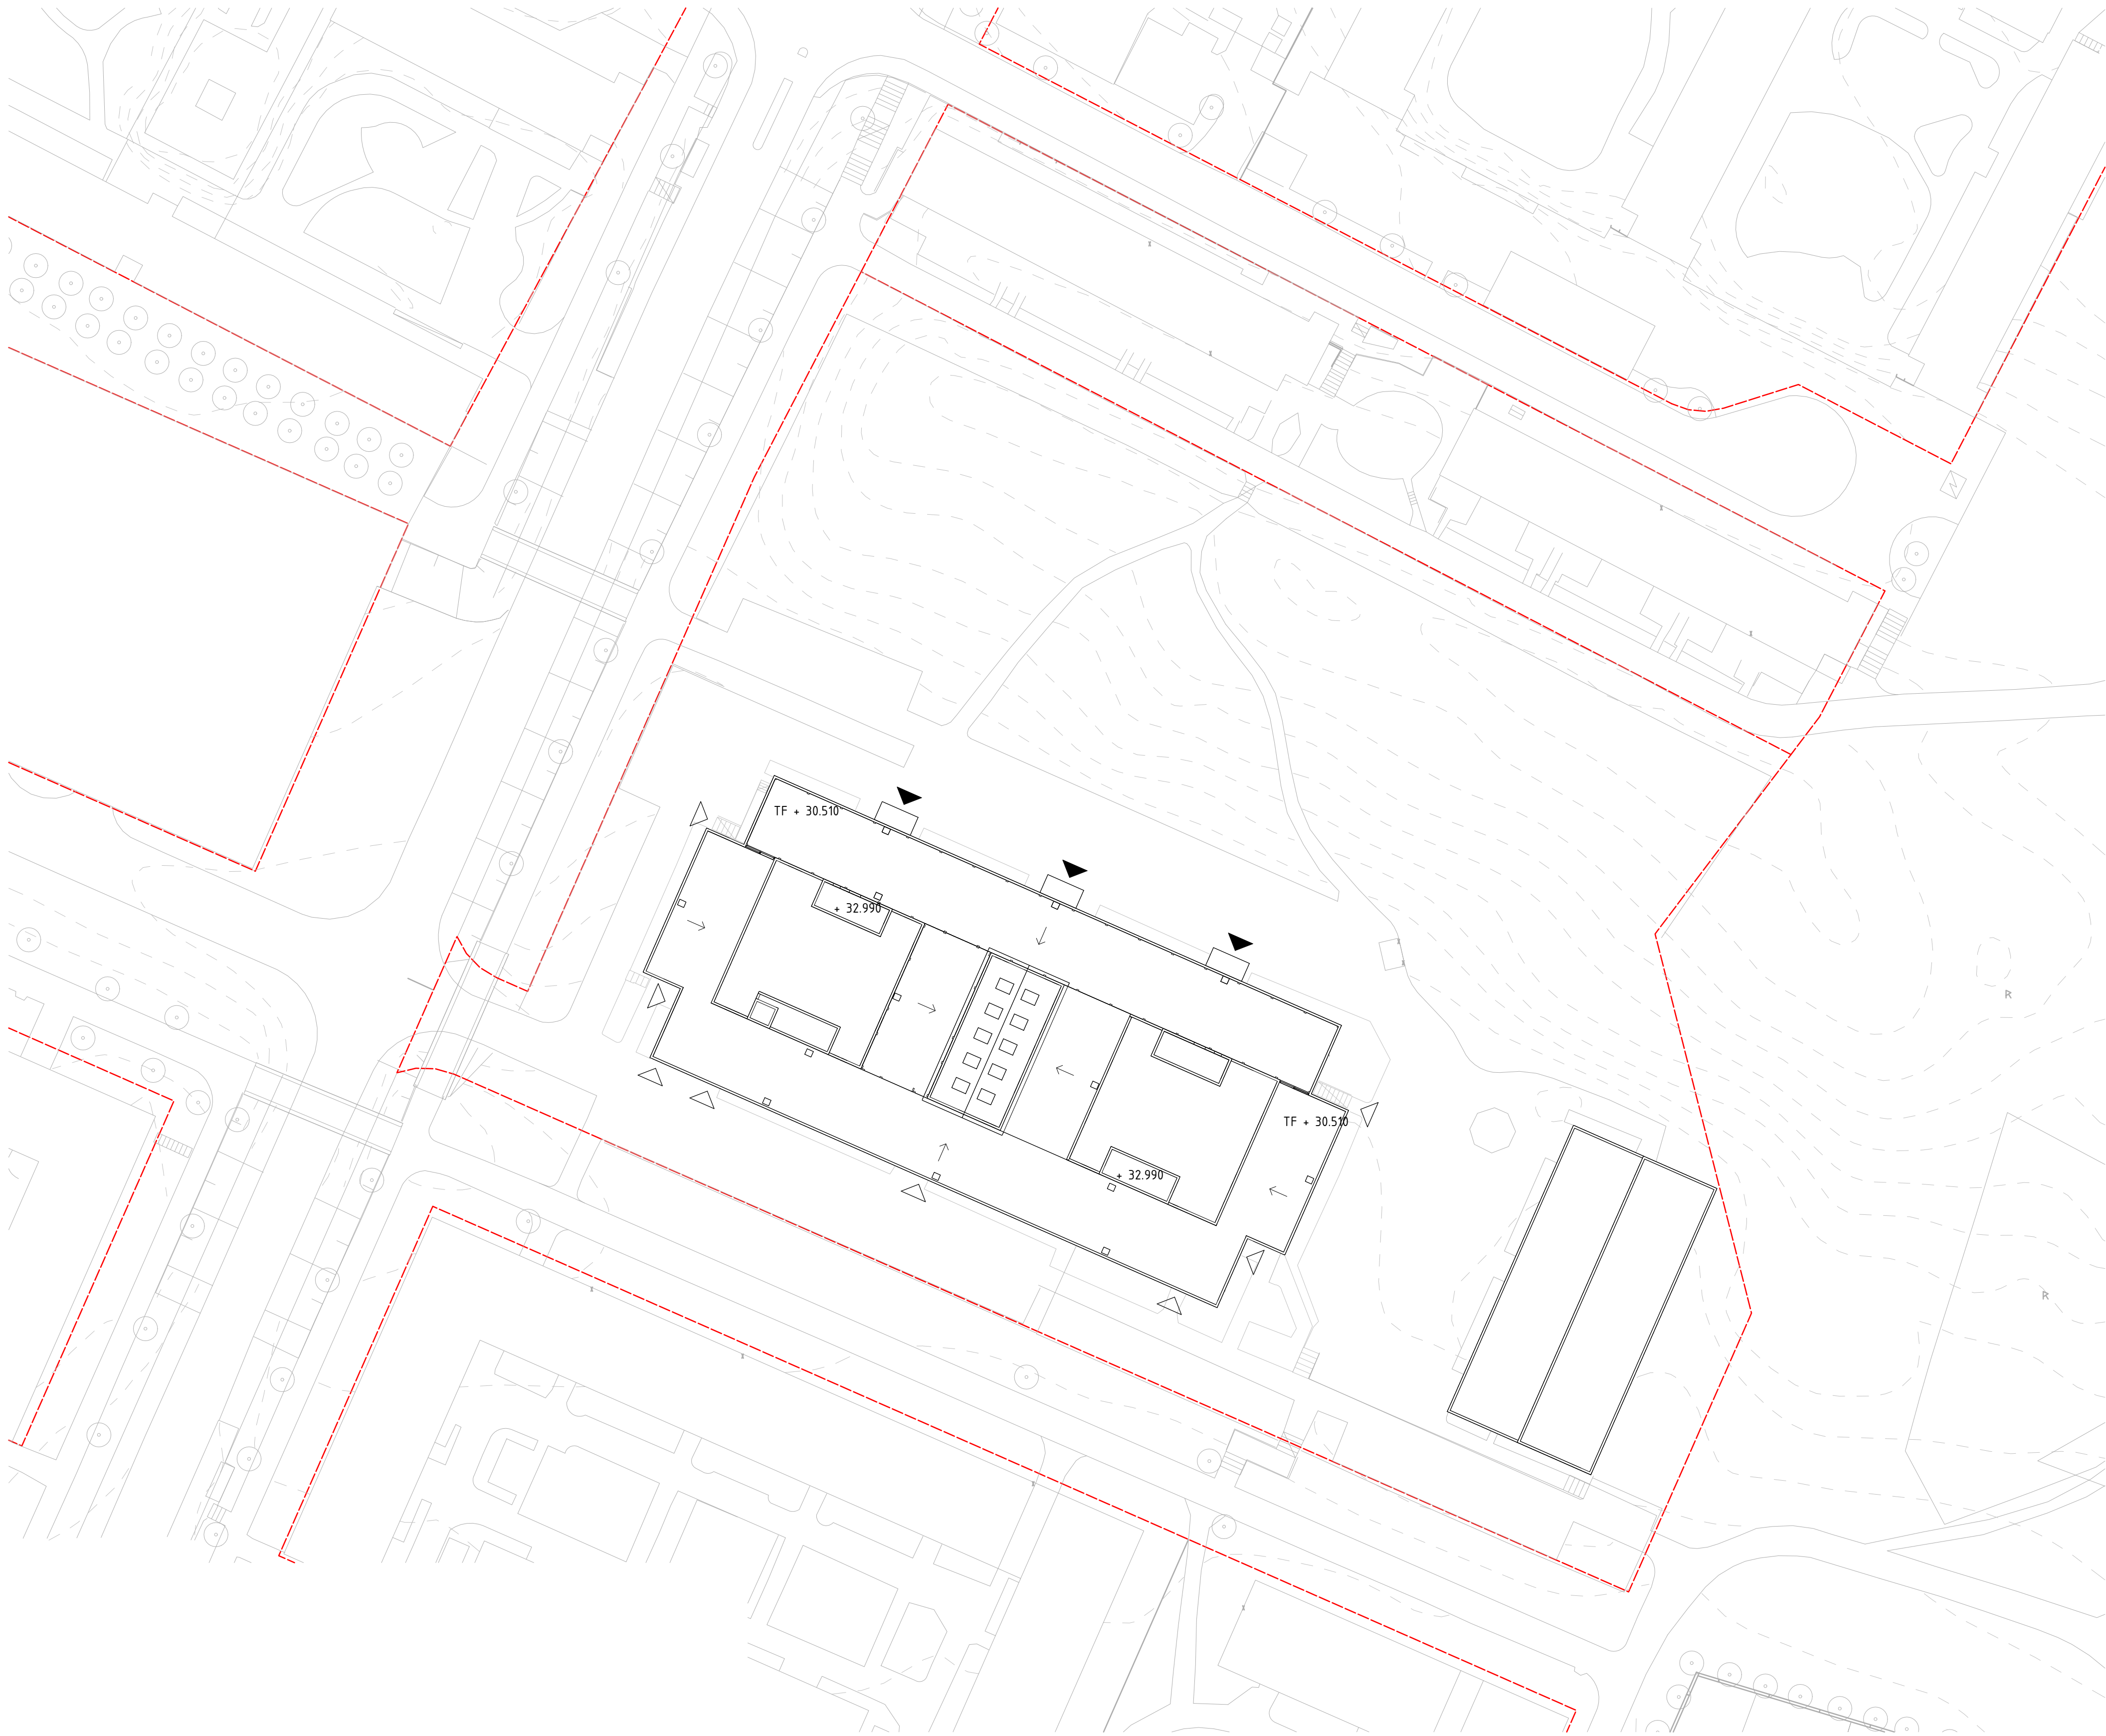

FÖRKLARINGAR


MÅTT ANGES I MILLIMETER.
PLUSHÖJDER ANGES I METER ENLIGT HÖJDSYSTEM RH2000.
RITNINGAR UPPRÄTTADE EFTER TIDIGARE UNDERLAG. BEFINTLIGA
RITNINGAR OCH RELATIONSHANDLINGAR.

- HUVUDENTRÉ
- ÖVRIGA ENTRÉER
- FASTIGHETSGRÄNS

FÖRESKRIFTER

HÄNVISNINGAR

- A-01-1-001
- A-40-X-XXX-SERIE
- A-00-1-XXX-SERIE
- A-00-2-XXX-SERIE
- A-00-3-XXX-SERIE
- SITUATIONSPLAN
- BLIVANDE UTSEENDE
- PLANER
- SEKTIONER
- FASADER

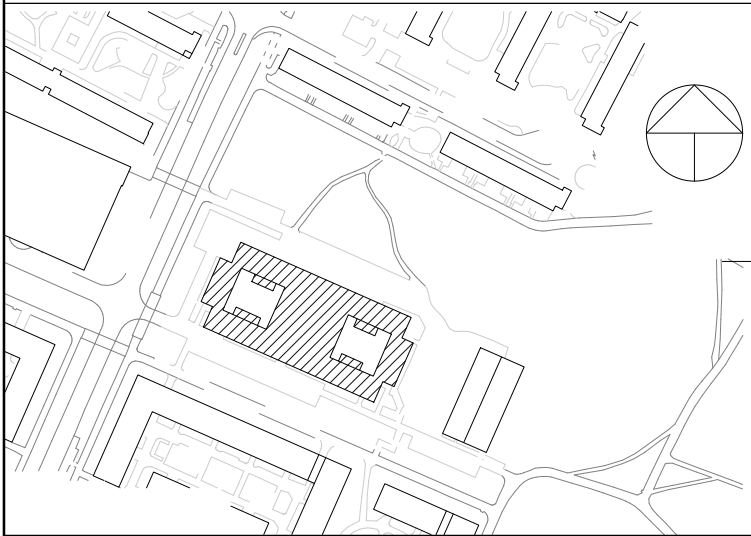

BET	ANT	ÄNDRINGEN AVSER	DATUM	SIGN
-----	-----	-----------------	-------	------

PROGRAMHANDLING

FASTIGHET: KÄMPINGE 2:1
BYGGNAD: A
HUS.NR:
PLAN: -

SEKRETESS:

Henning
Larsen





B	FASTIGHETSKONTORET	Tel: 08-508 270 00
P	WSP	Tel: 070-275 08 96
X	A HENNING LARSEN	Tel: 070-574 61 43
K	NORCONSULT	Tel: 079-142 89 57
V	SAMCONSULT	Tel: 070-278 06 29

PROJEKT NR	RITADKONSTR. AV	ANLÄGGNINGSNUMMER
74320	SE/JK/AS	0260
DATUM	ANSVARIG	DISCIPLIN
20250124	M. WAHLGREN	A

JÄRVA SDF
BEFINTLIGT UTSEENDE
SITUATIONSPLAN

SKALA	RITNINGSNAMN	BET
A1 1:500 A3 1:1000	A-00-0-001	

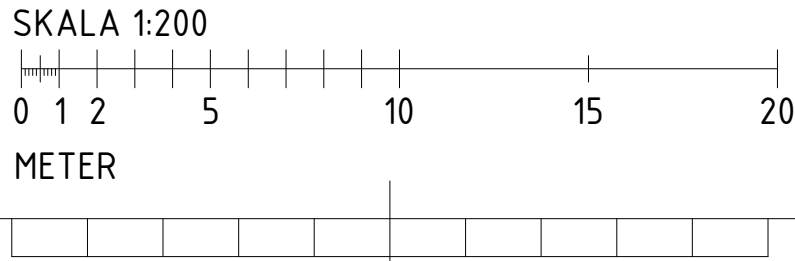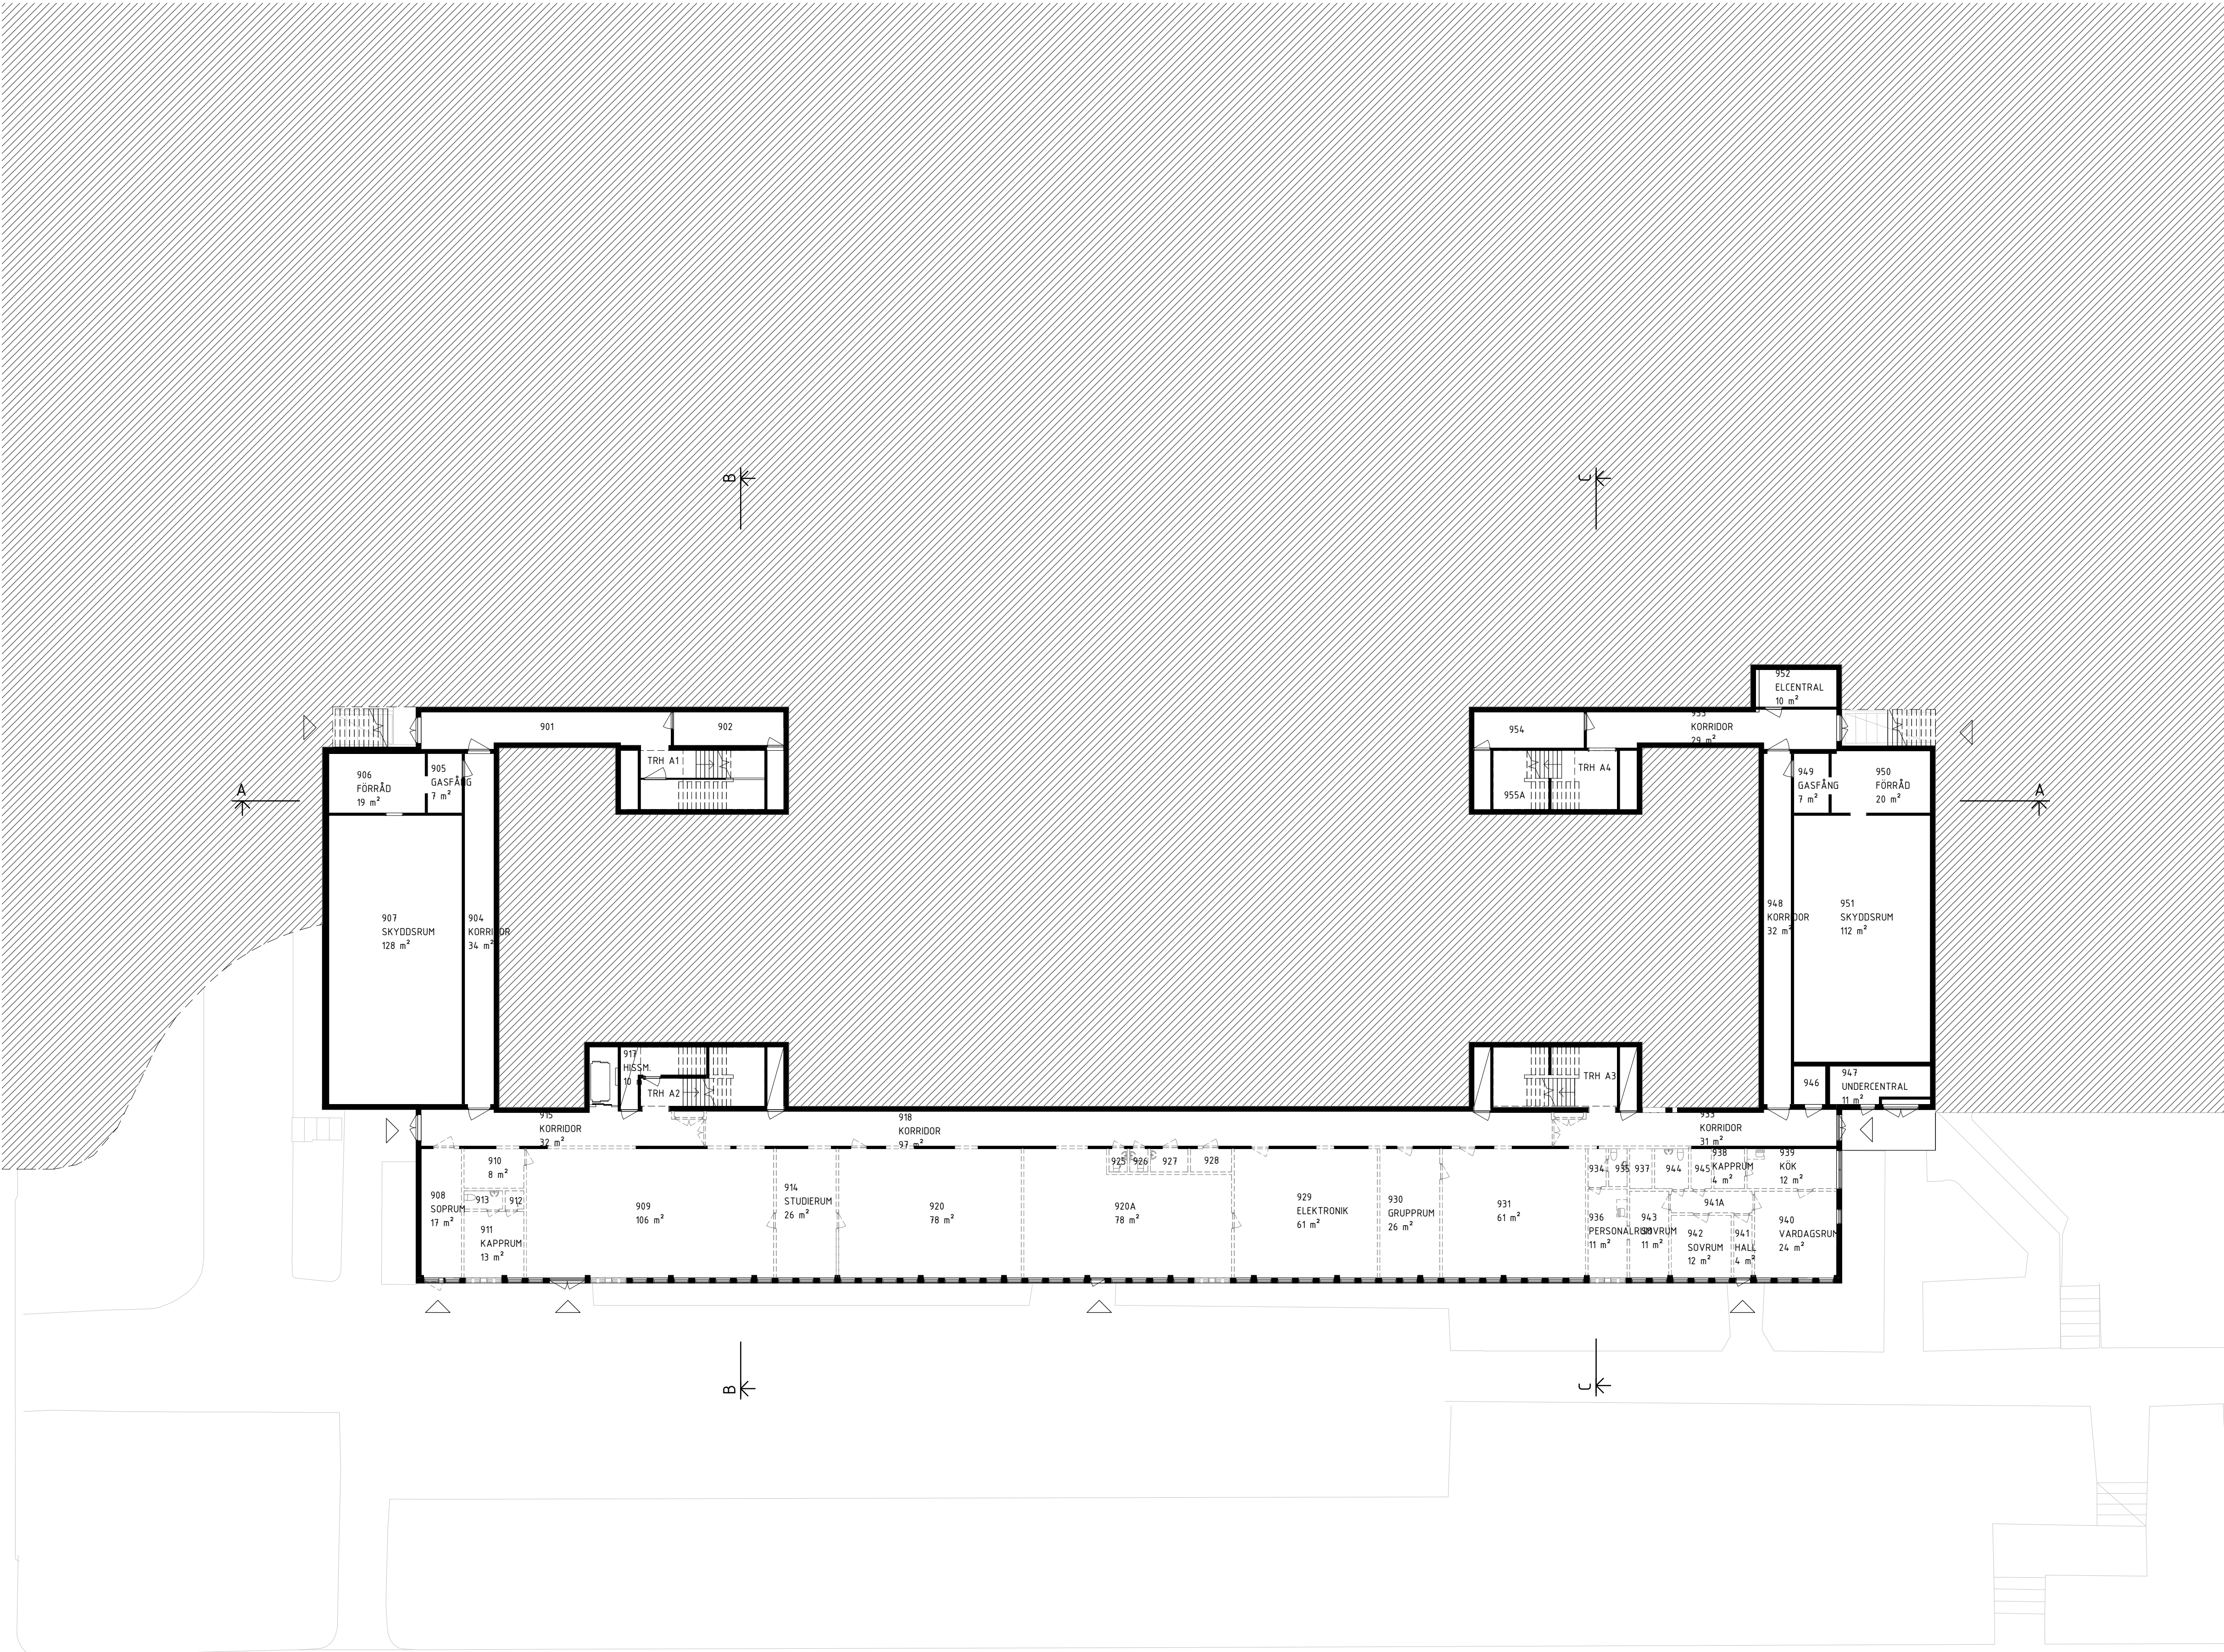

FÖRKLARINGAR

MÅTT ANGES I MILLIMETER.
PLUSHÖJDER ANGES I METER ENLIGT HÖJDSYSTEM RH2000.

RITNINGAR UPPRÄTTADE EFTER TIOGÅRE UNDERLAG. BEFINTLIGA
RITNINGAR OCH RELATIONSHANDLINGAR.


- HUVUDENTRÉ
- ÖVRIGA ENTRÉER
- BEFINTLIGA BYGGDELAR
- BYGGDELAR SOM RIVS

FÖRESKRIFTER

-

HÄNVISNINGAR

- | | |
|------------------|-------------------|
| A-01-1-001 | SITUATIONSPLAN |
| A-40-X-XXX-SERIE | BLIVANDE UTSEENDE |
| A-00-2-XXX-SERIE | SEKTIONER |
| A-00-3-XXX-SERIE | FASADER |

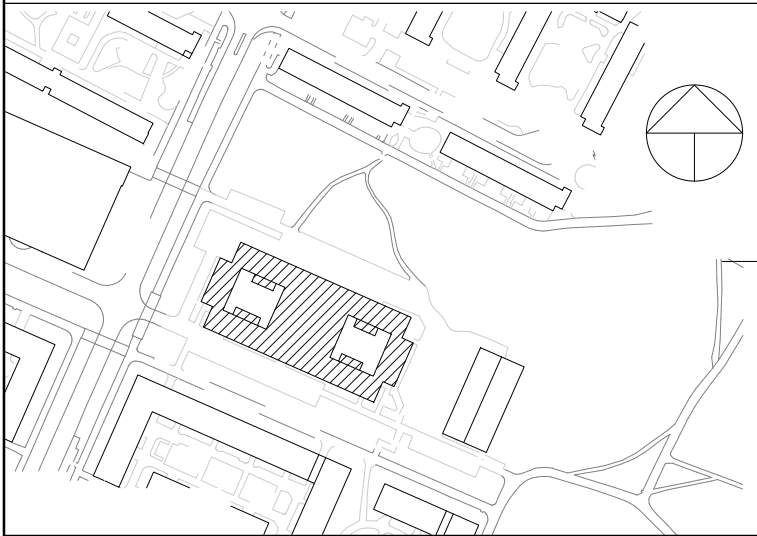


BET	ANT	ANDRINGEN AVSER		DATUM	SIGN
PROGRAMHANDLING					
FASTIGHET: KÄMPINGE 2:1					
BYGGNAD: A					
HUS.NR: -					
PLAN: 09		SEKRETESS:			
 Henning Larsen —					
 Stockholms stad					
B FASTIGHETSKONTORET		Tel: 08-508 270 00			
P WSP		Tel: 070-275 08 96			
A HENNING LARSEN		Tel: 070-574 61 43			
K NORCONSULT		Tel: 079-142 89 57			
V SAMKONSULT		Tel: 070-278 06 29			
PROJEKT NR 74320		RITADKONSTR. AV SE/JK/AS		ANLÄGGNINGSNUMMER 0260	
DATUM 20250124		ANSVARIG M. WAHLGREN			DISCIPLIN A
JÄRVA SDF					
BEFINTLIGT UTSEENDE					
PLAN 09					
SKALA A1 1:200 A3 1:400		RITNINGSNAMN A-00-1-001			BET

SE A-00-1-001

SE A-00-1-001

SE A-00-1-001


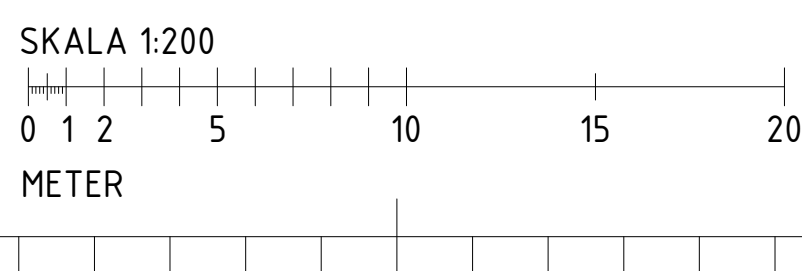


FASTIGHET: KÄMPINGE 2:1	
BYGGNAD: A	
HUS.NR: -	
PLAN: 10	SEKRETESS:



PROJEKT.NR 74320	RITAD/KONSTR. AV SE/JK/AS	ANLÄGGNINGSNUMMER 0260
DATUM 20250124	ANSVARIG M. WAHLGREN	DISCIPLIN A

SKALA	RITNINGSNAMN	BET
A1 1:200	A-00-1-002	
A3 1:400		

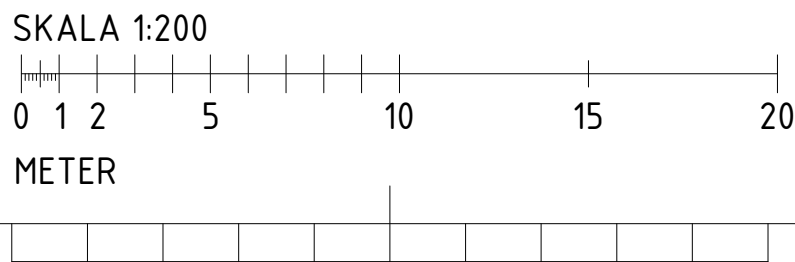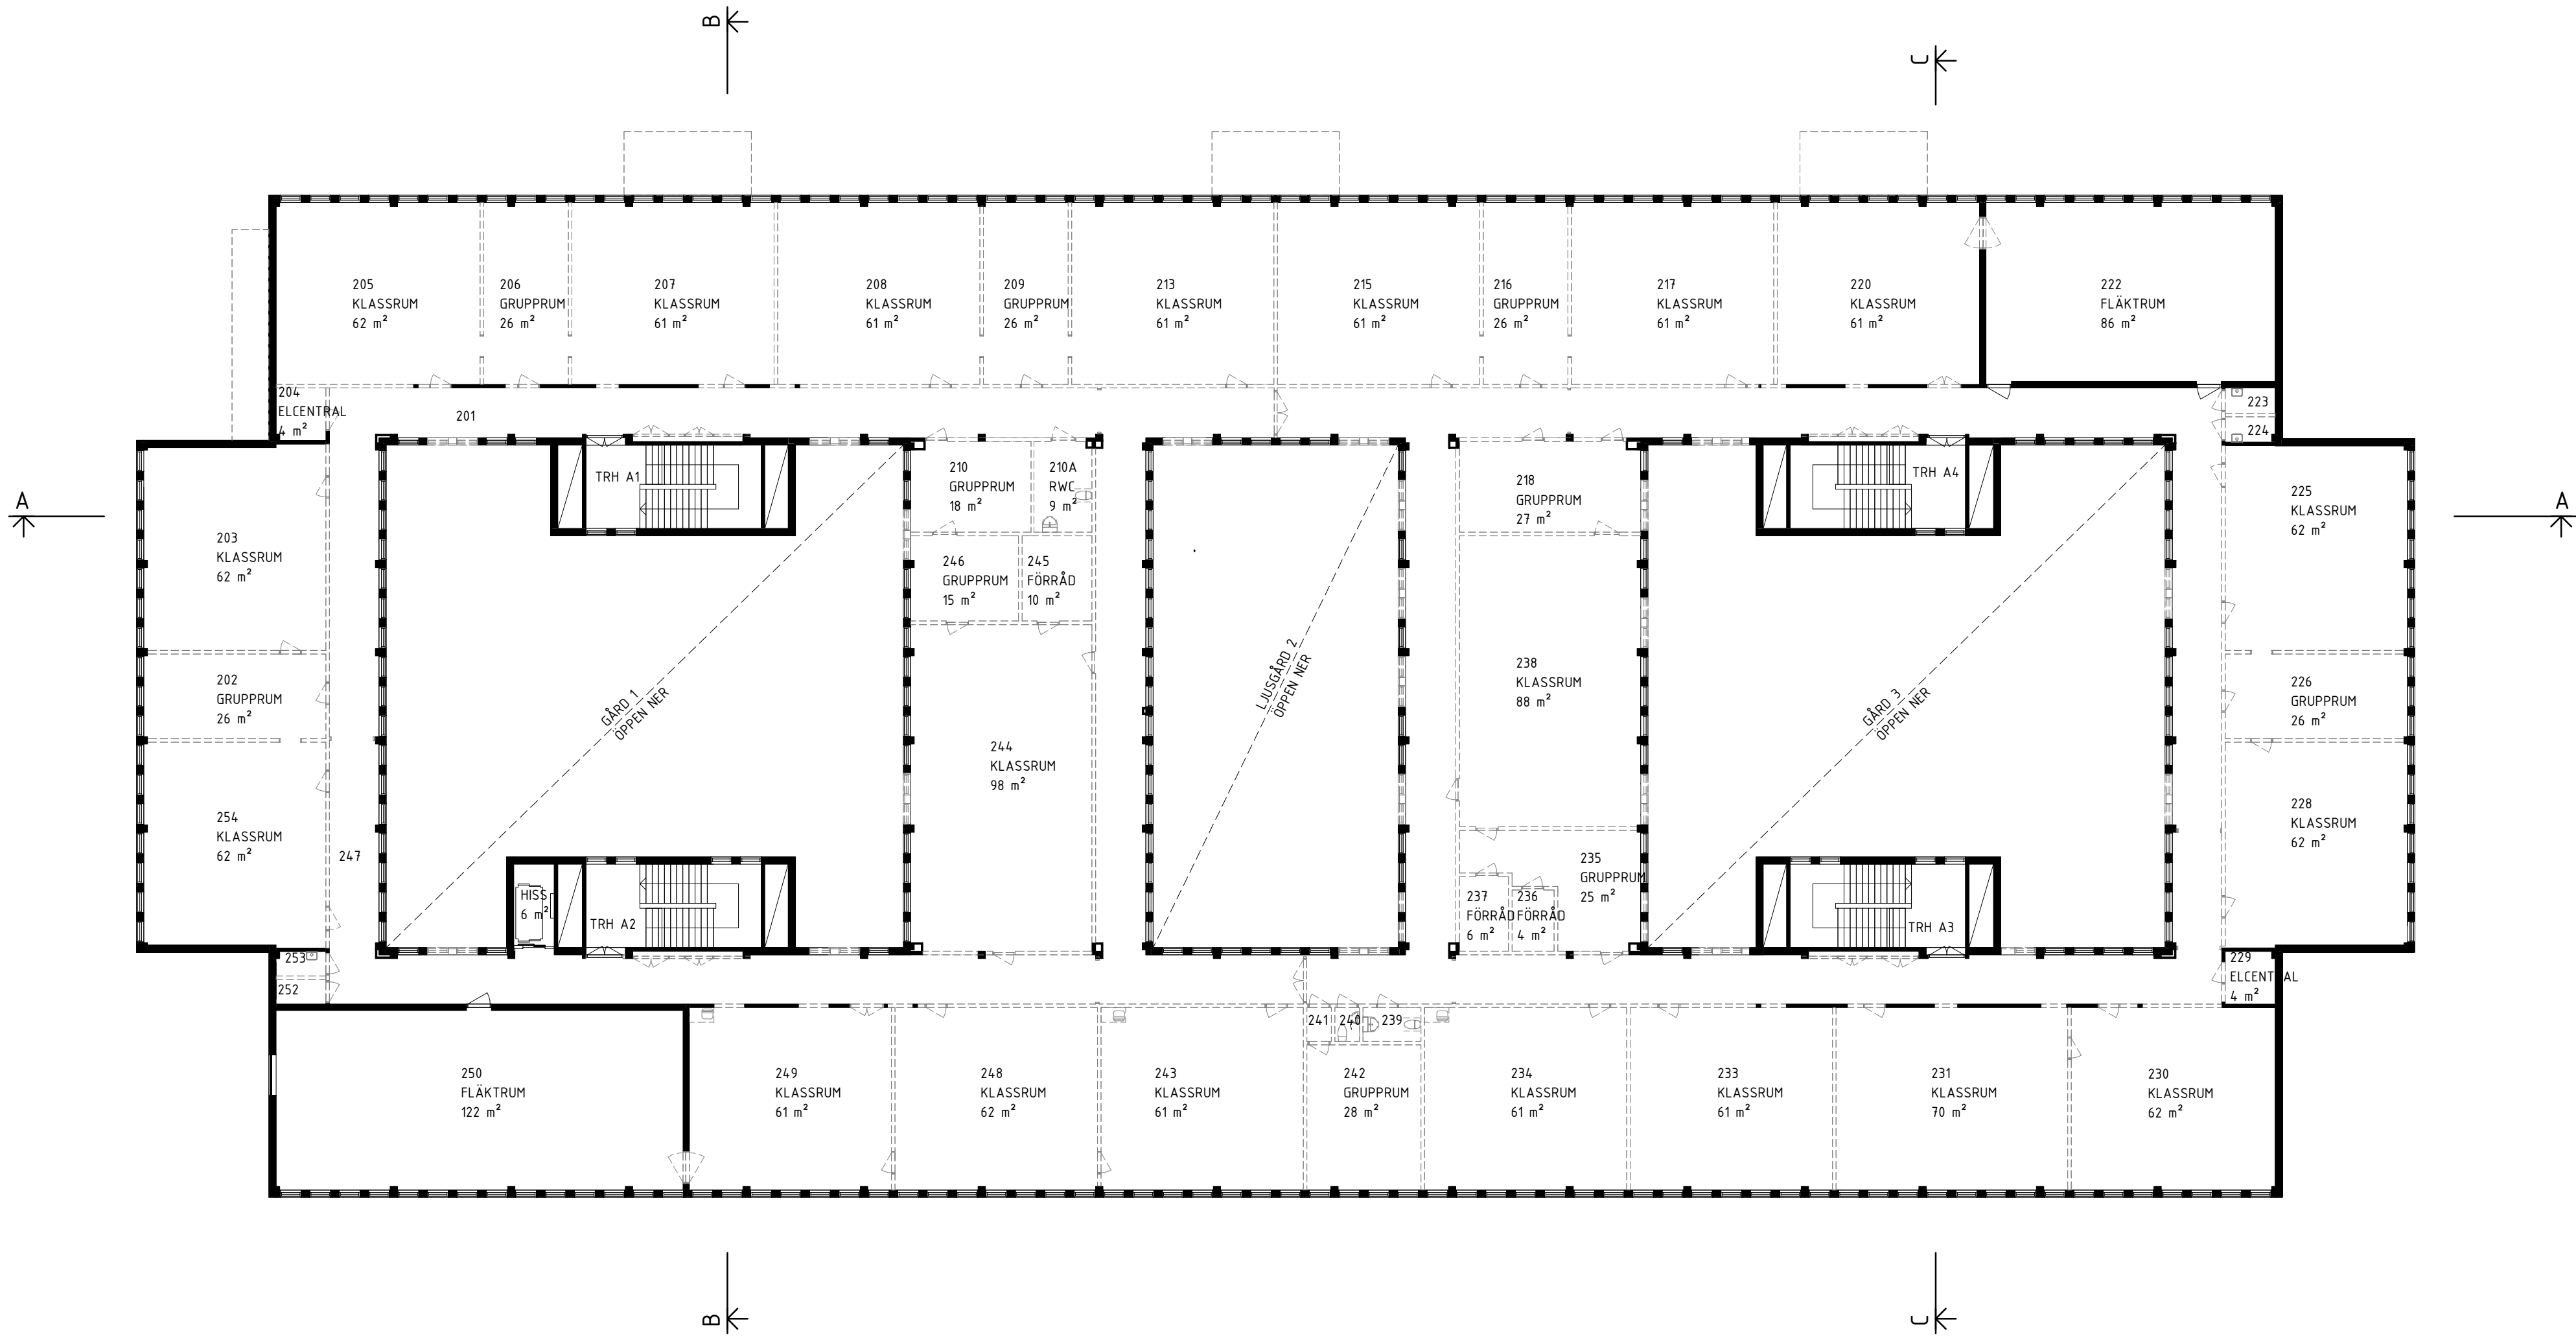

FÖRKLARINGAR


SE A-00-1-001

FÖRESKRIFTER

SE A-00-1-001

HÄNVISNINGAR

SE A-00-1-001

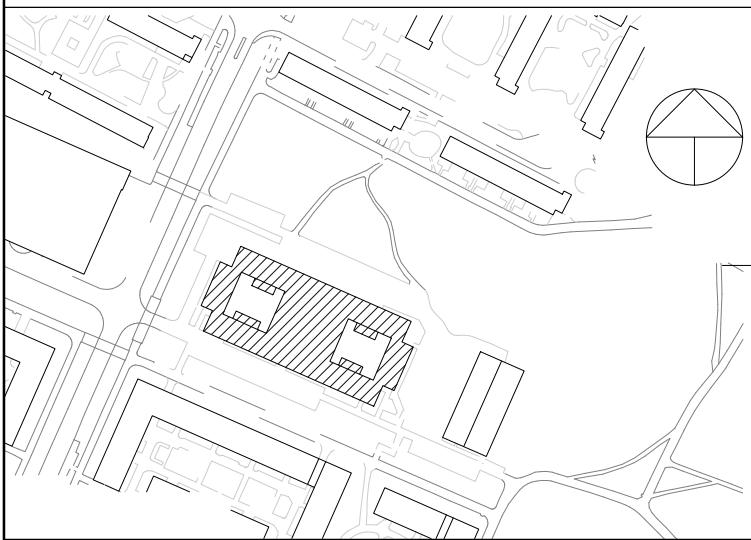

BET	ANT	ÄNDRINGEN AVSER	DATUM	SIGN
-----	-----	-----------------	-------	------

PROGRAMHANDLING

FASTIGHET: KÄMPINGE 2:1

BYGGNAD: A

HUS.NR: -

PLAN: 11

SEKRETESS:

**Henning
Larsen**





**Stockholms
stad**

B	FASTIGHETSKONTORET	Tel: 08-508 270 00
P	WSP	Tel: 070-275 08 96
X	A HENNING LARSEN	Tel: 070-574 61 43
K	NORCONSULT	Tel: 079-142 89 57
V	SAMKONSULT	Tel: 070-278 06 29

PROJEKT NR	RITADYKONSTR. AV	ANLÄGGNINGSNUMMER
74320	SE/JK/AS	0260
DATUM	ANSVARIG	DISCIPLIN
20250124	M. WAHLGREN	A

JÄRVA SDF
BEFINTLIGT UTSEENDE
PLAN 11

SKALA	RITNINGSNAMN	BET
A1 1:200 A3 1:400	A-00-1-003	

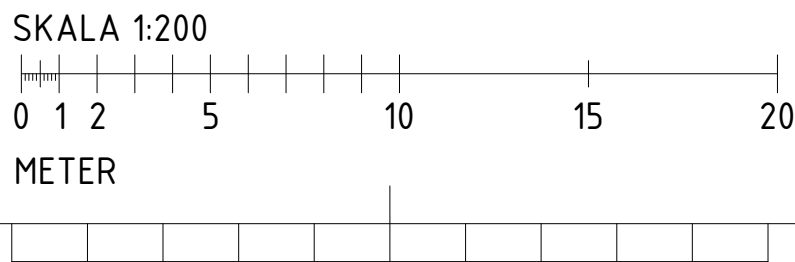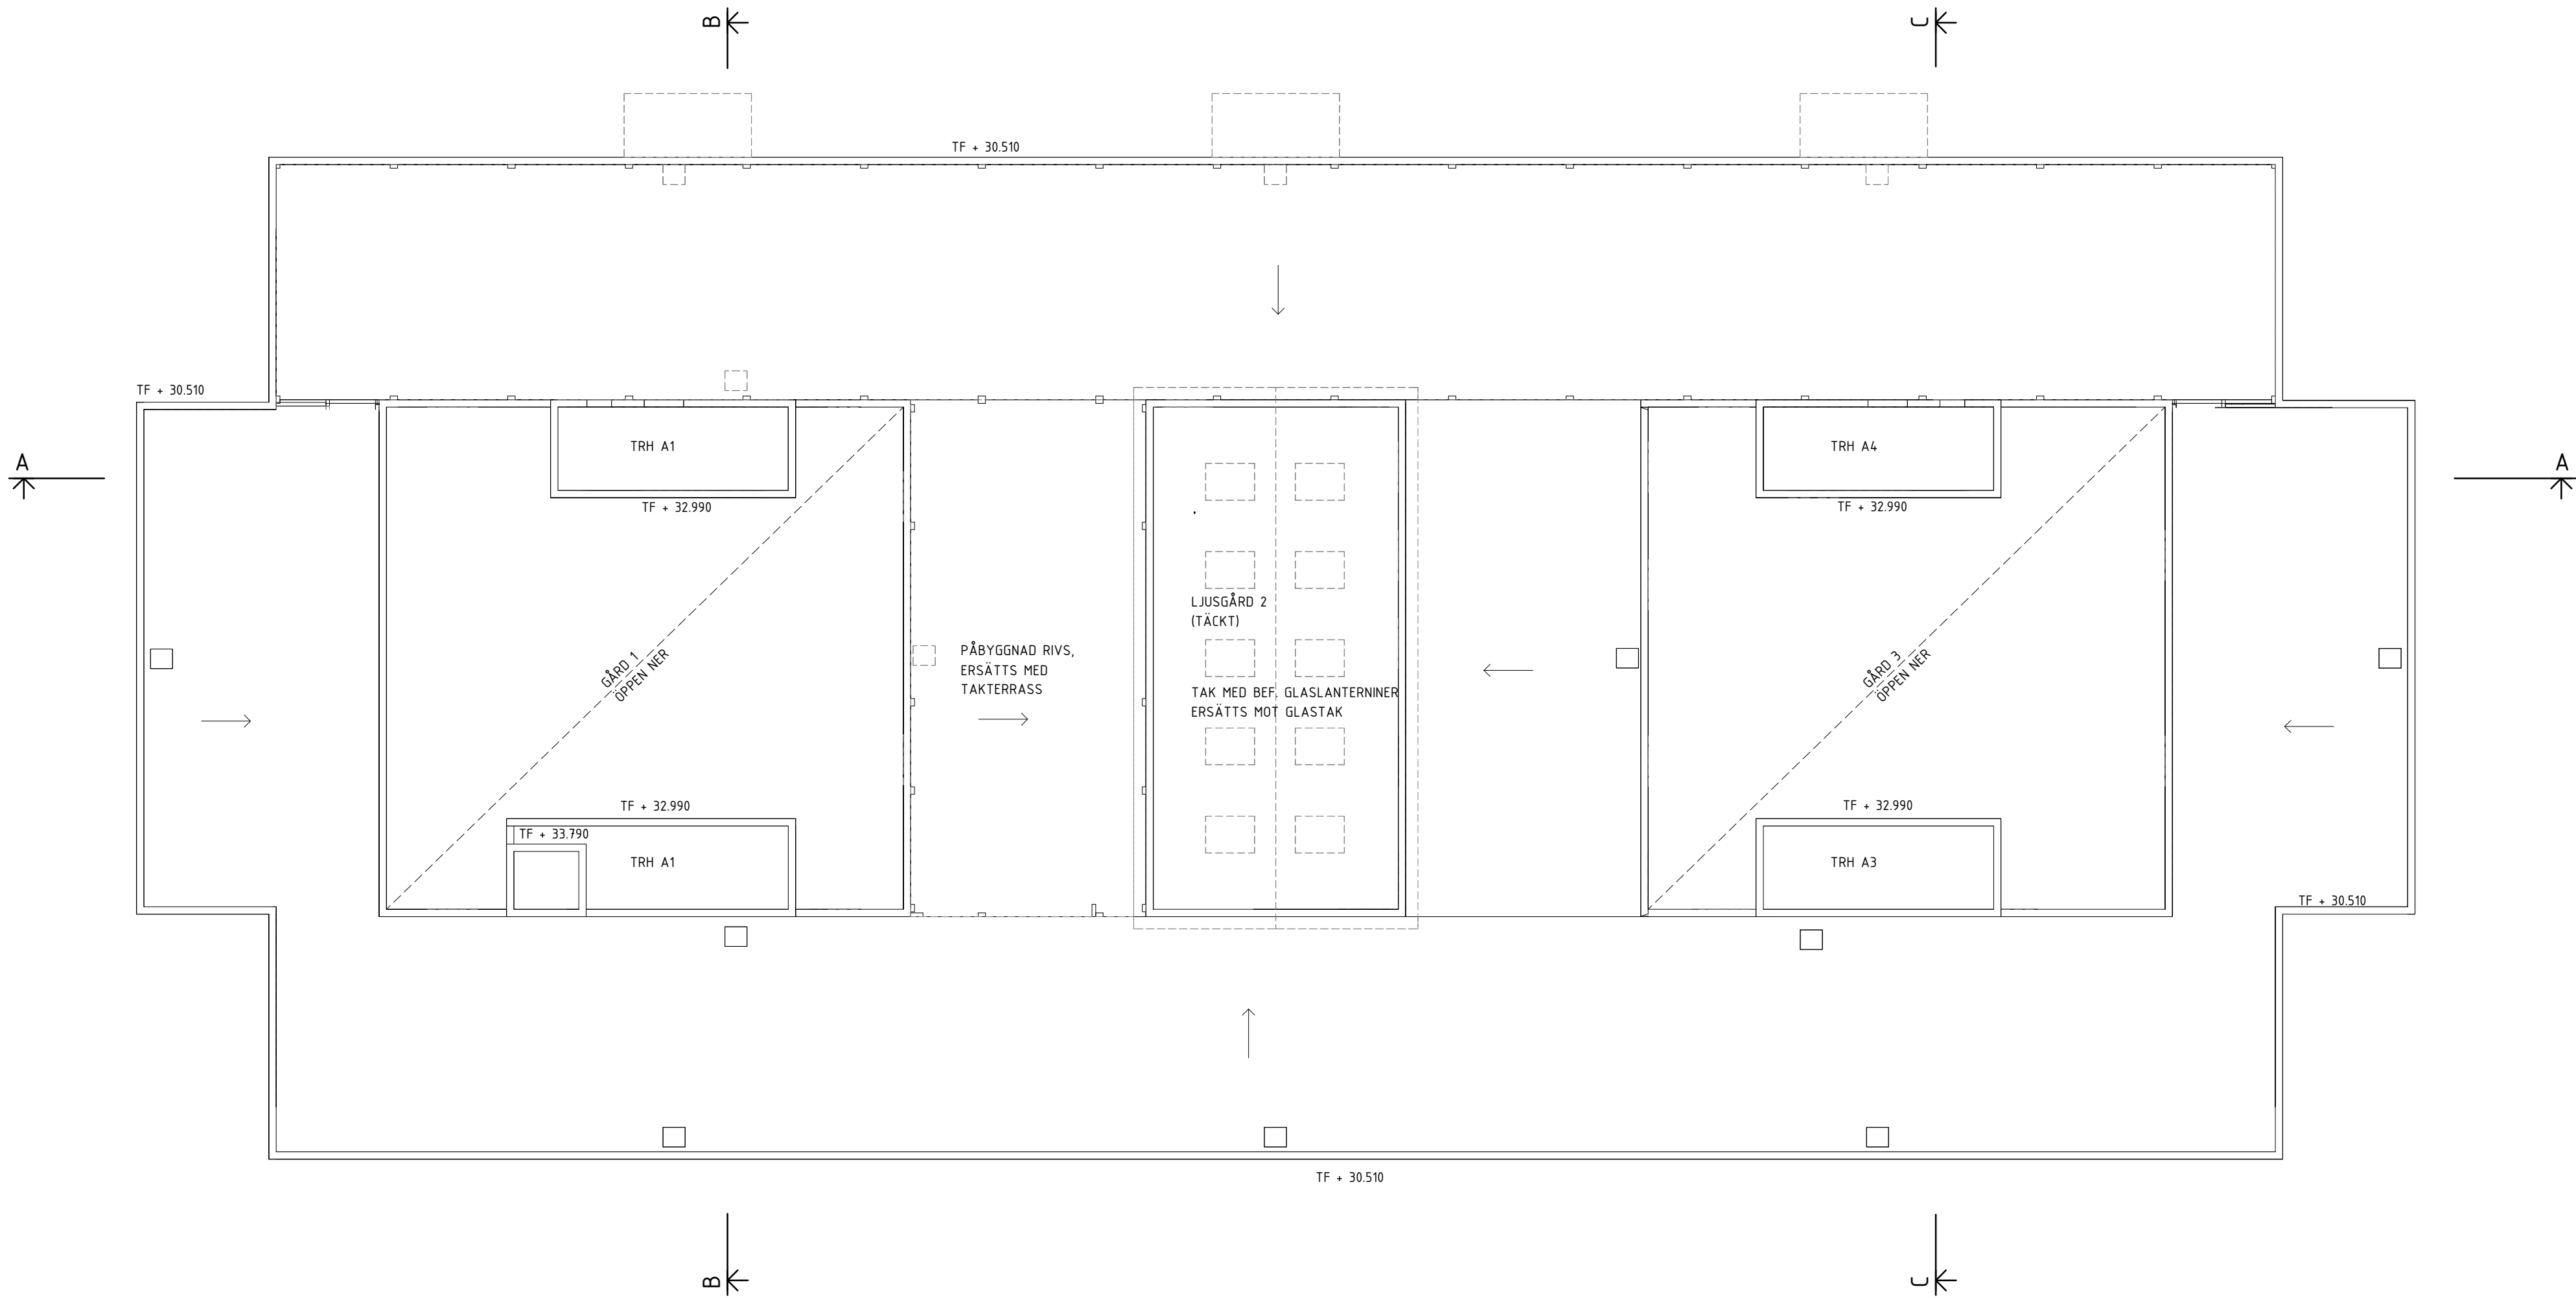

FÖRKLARINGAR


SE A-00-1-001

FÖRESKRIFTER

SE A-00-1-001

HÄNVISNINGAR

SE A-00-1-001

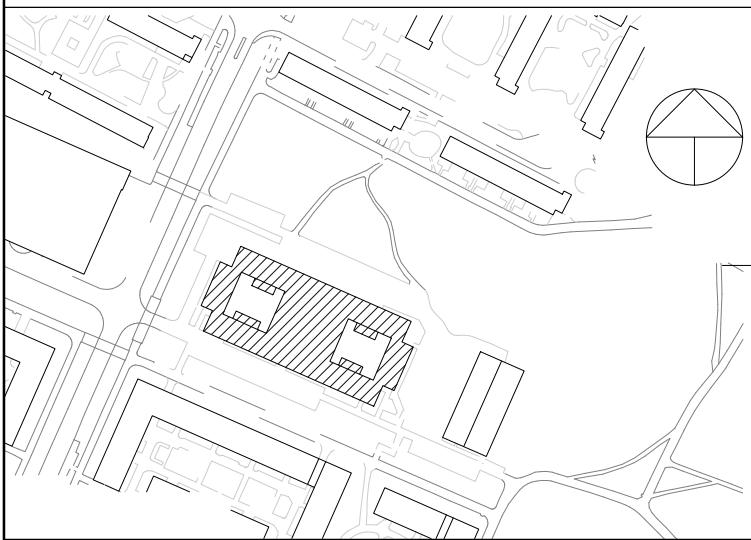

BET	ANT	ÄNDRINGEN AVSER	DATUM	SIGN
-----	-----	-----------------	-------	------

PROGRAMHANDLING

FASTIGHET: KÄMPINGE 2:1
BYGGNAD: A
HUS.NR: -
PLAN: 12

SEKRETESS:

**Henning
Larsen**




B	FASTIGHETSKONTORET	Tel: 08-508 270 00
P	WSP	Tel: 070-275 08 96
X	A HENNING LARSEN	Tel: 070-574 61 43
K	NORCONSULT	Tel: 079-142 89 57
V	SAMKONSULT	Tel: 070-278 06 29


PROJEKT NR	RITADYKONSTR. AV	ANLÄGGNINGSNUMMER
74320	SE/JK/AS	0260
DATUM	ANSVARIG	DISCIPLIN
20250124	M. WAHLGREN	A

JÄRVA SDF
SAMMANSATT REDOVISNING
PLAN 12 - TAKPLAN


SKALA	RITNINGSNAMN	BET
A1 1:200 A3 1:400	A-00-1-004	

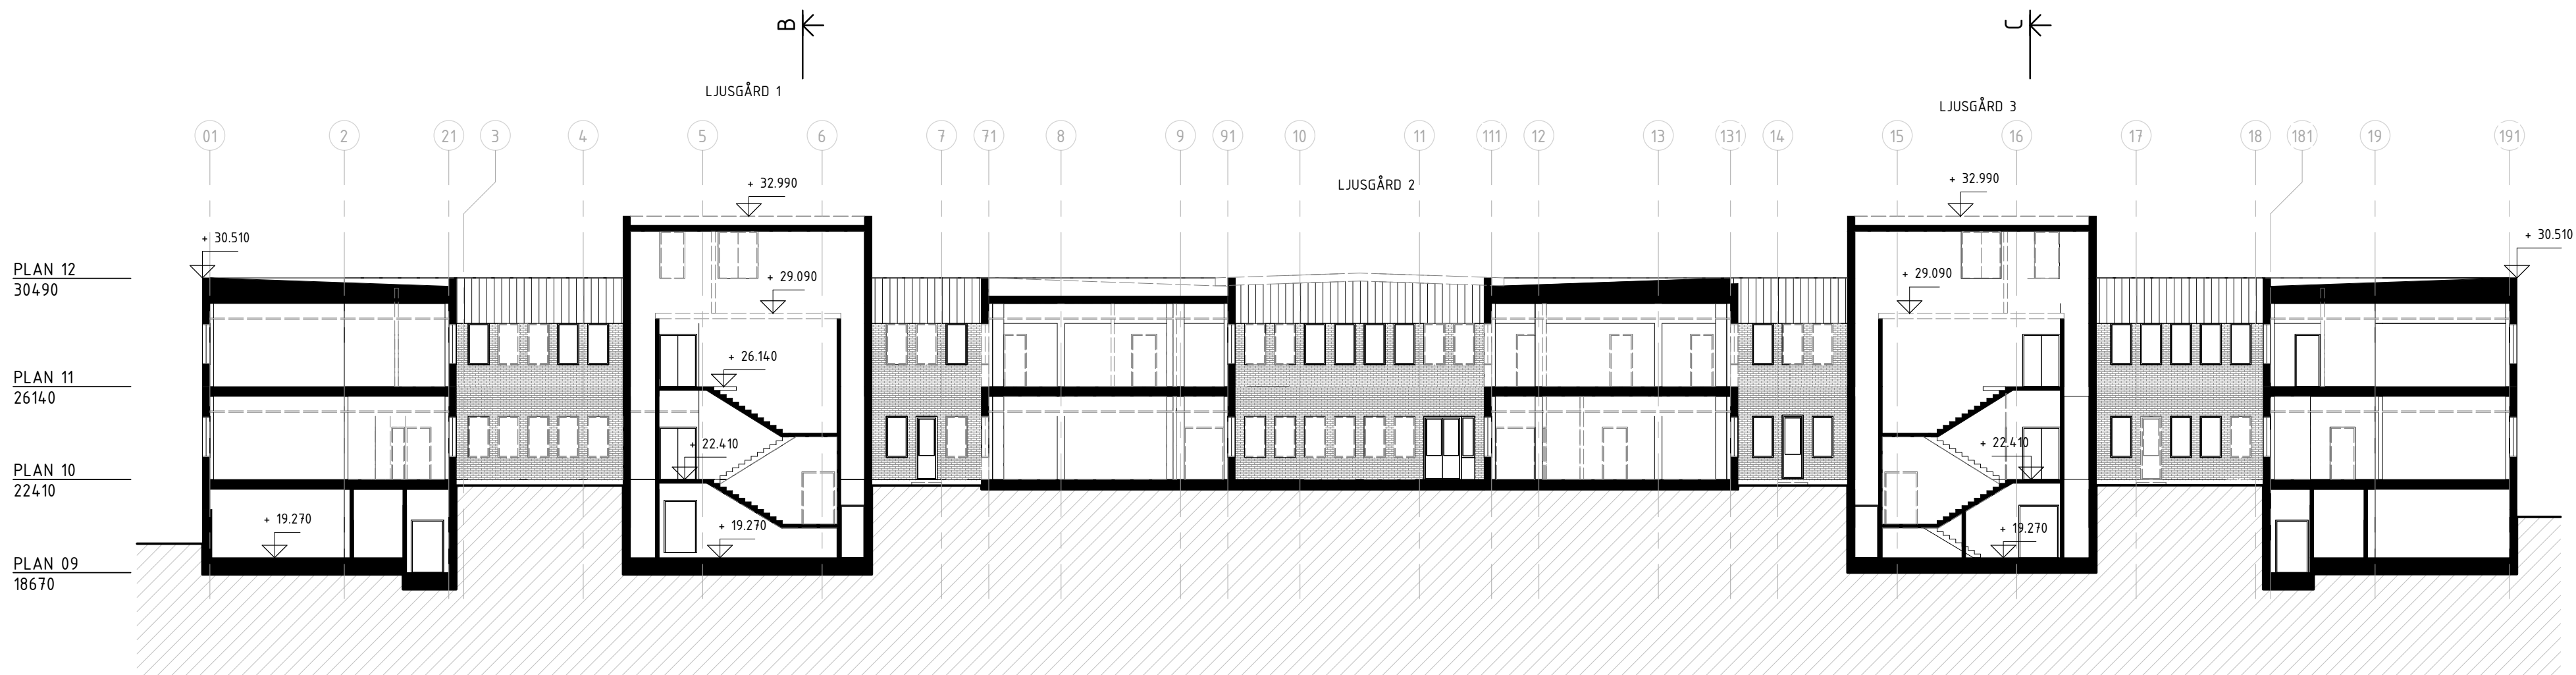


SEKTION A-A, BEFINTLIG

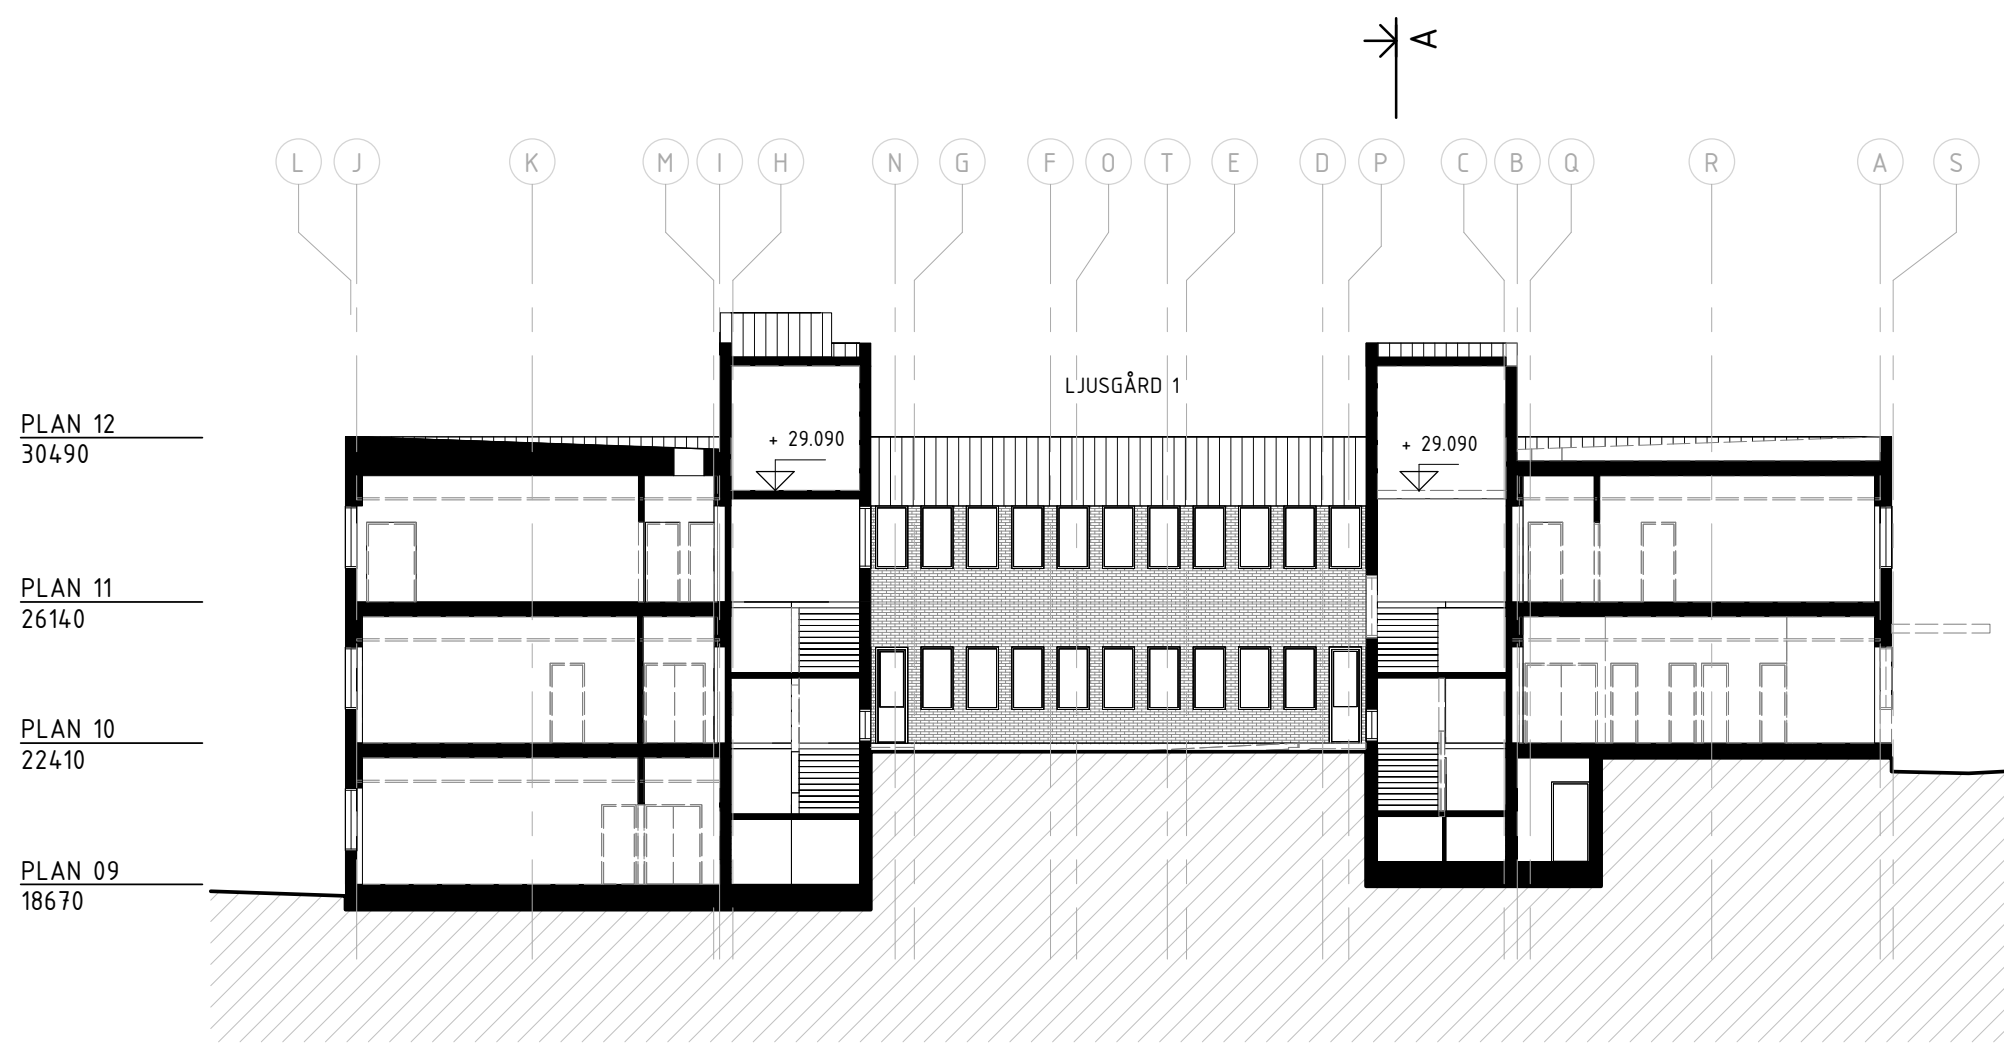

SEKTION B-B, BEFINTLIG

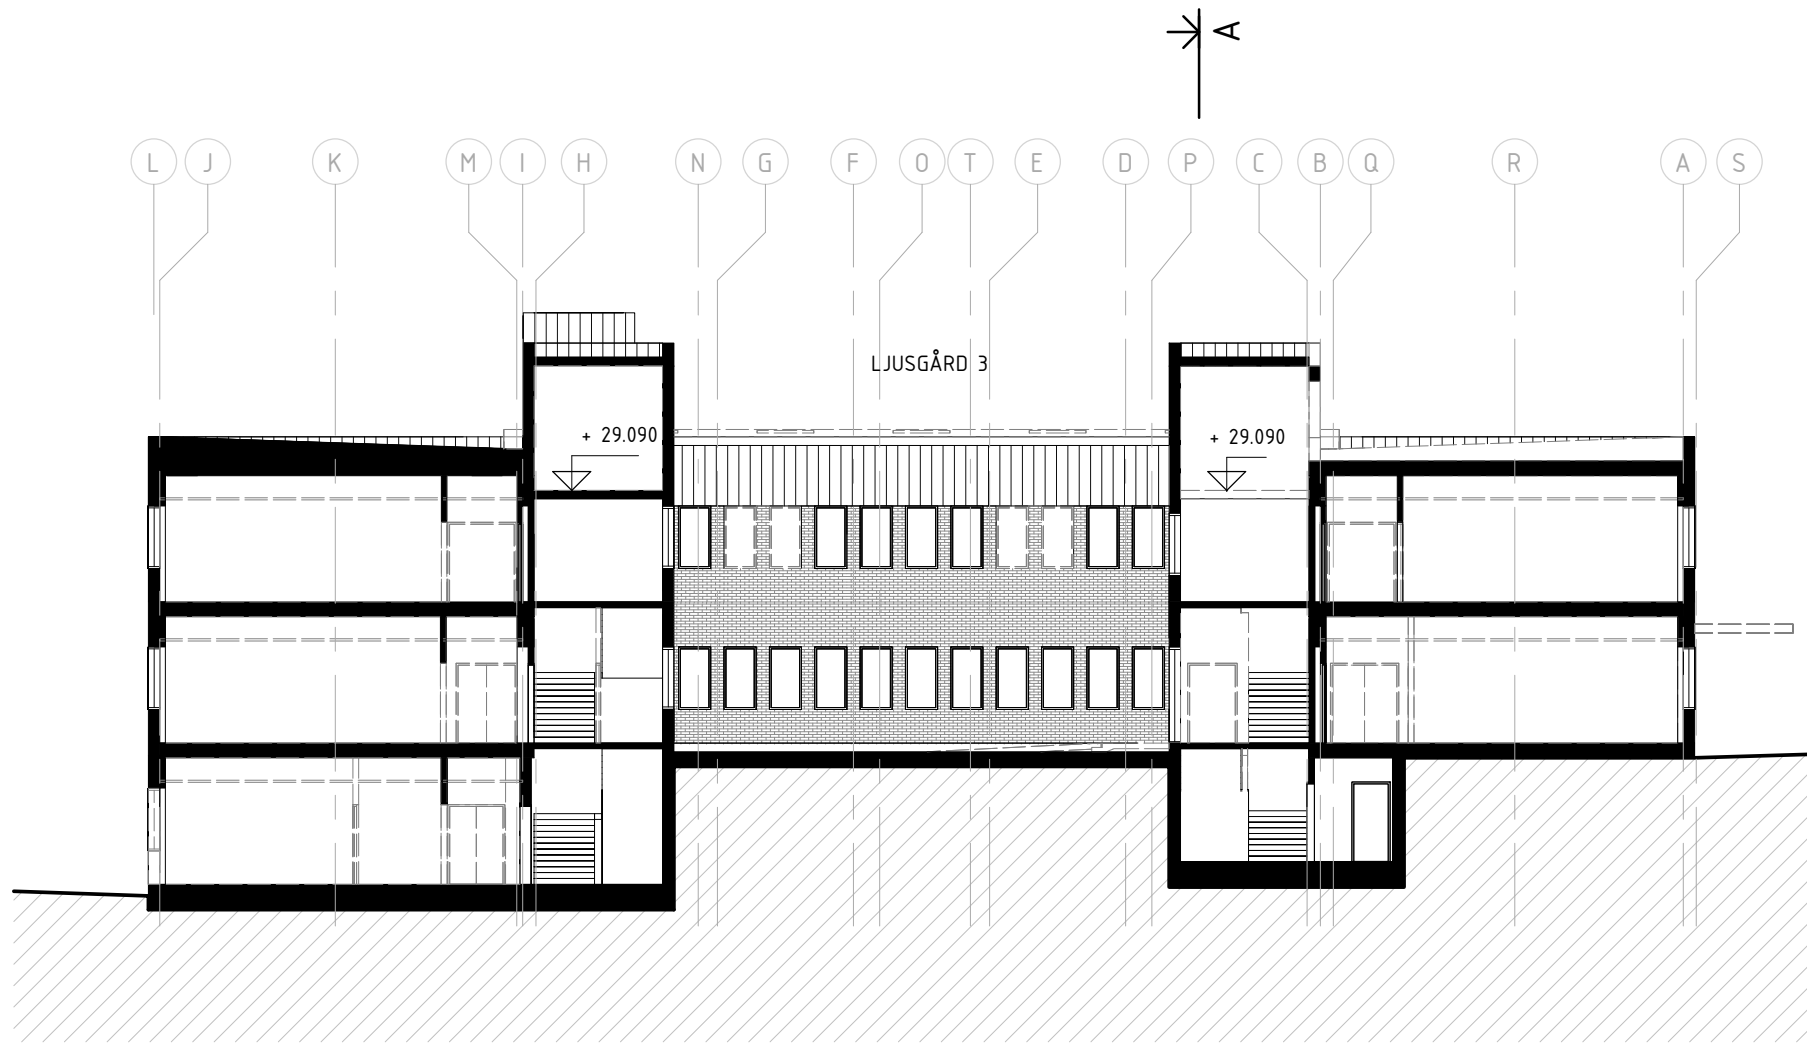

SEKTION C-C, BEFINTLIG

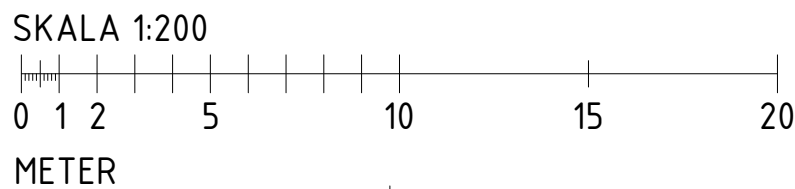

FÖRKLARINGAR


MÅTT ANGES I MILLIMETER.
PLUSHÖJDER ANGES I METER ENLIGT HÖJDSYSTEM RH2000.
RITNINGAR UPPRÄTTADE EFTER TIDIGARE UNDERLAG: BEFINTLIGA
RITNINGAR OCH RELATIONSHANDLINGAR.

— BEFINTLIG BYGGDEL
- - - - - BYGGDEL SOM RIVS

FÖRESKRIFTER

HÄNVISNINGAR

A-10-X-XXX-SERIE BLIVANDE UTSEENDE
A-00-1-XXX-SERIE PLANER
A-00-3-XXX-SERIE FASADER

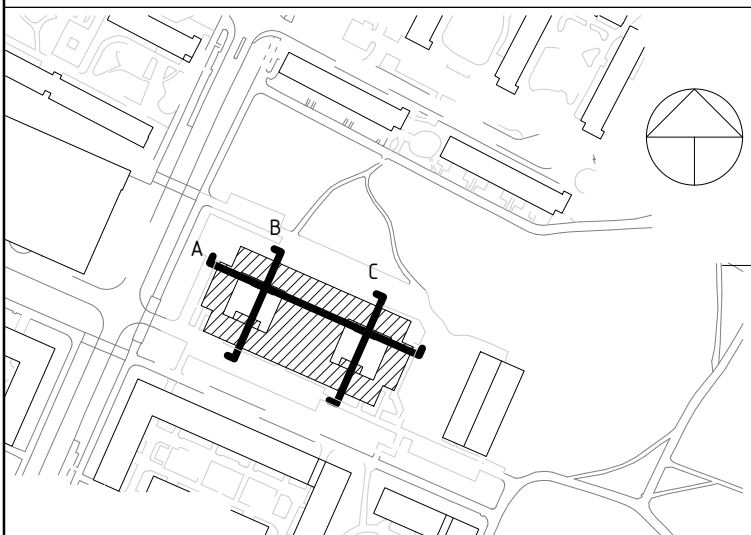

BET	ANT	ÄNDRINGEN AVSER	DATUM	SIGN
-----	-----	-----------------	-------	------

PROGRAMHANDLING

FASTIGHET: KÄMPINGE 2:1
BYGGNAD: A
HUS.NR: -
PLAN: -

SEKRETESS:

**Henning
Larsen**




B	FASTIGHETSKONTORET	Tel: 08-508 270 00
P	WSP	Tel: 070-275 08 96
X	A HENNING LARSEN	Tel: 070-574 61 43
K	NORCONSULT	Tel: 079-142 89 57
V	SAMKONSULT	Tel: 070-278 06 29

PROJEKT NR	RITADYKONSTR. AV	ANLÄGGNINGSNUMMER
74320	SE/JK/AS	0260
DATUM	ANSVARIG	DISCIPLIN
20250124	M. WAHLGREN	A


JÄRVA SDF
BEFINTLIGT UTSEENDE
SEKTIONER

SKALA	RITNINGSNAMN	BET
A1 1:100 A3 1:200	A-00-2-001	


C:\Users\JAHMSE\OneDrive - Ramboll\Documents\0260-A-4.0-V-0000_0arima.kaim.rvt
2025-01-24 15:24:17

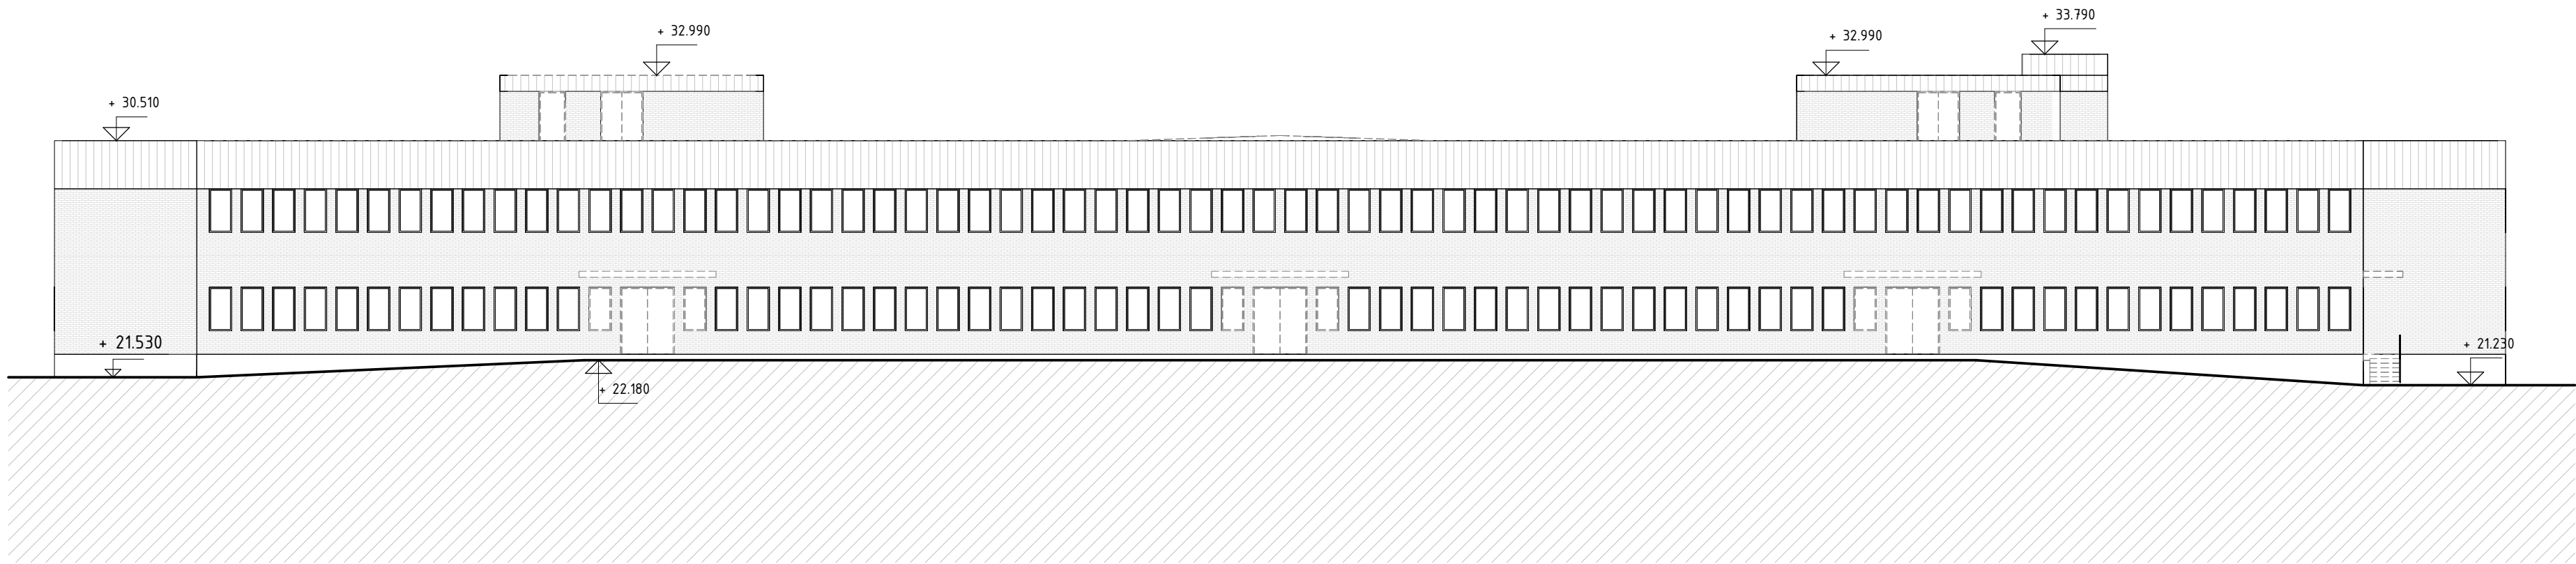


1 - FASAD MOT NORR, BEFINTLIG

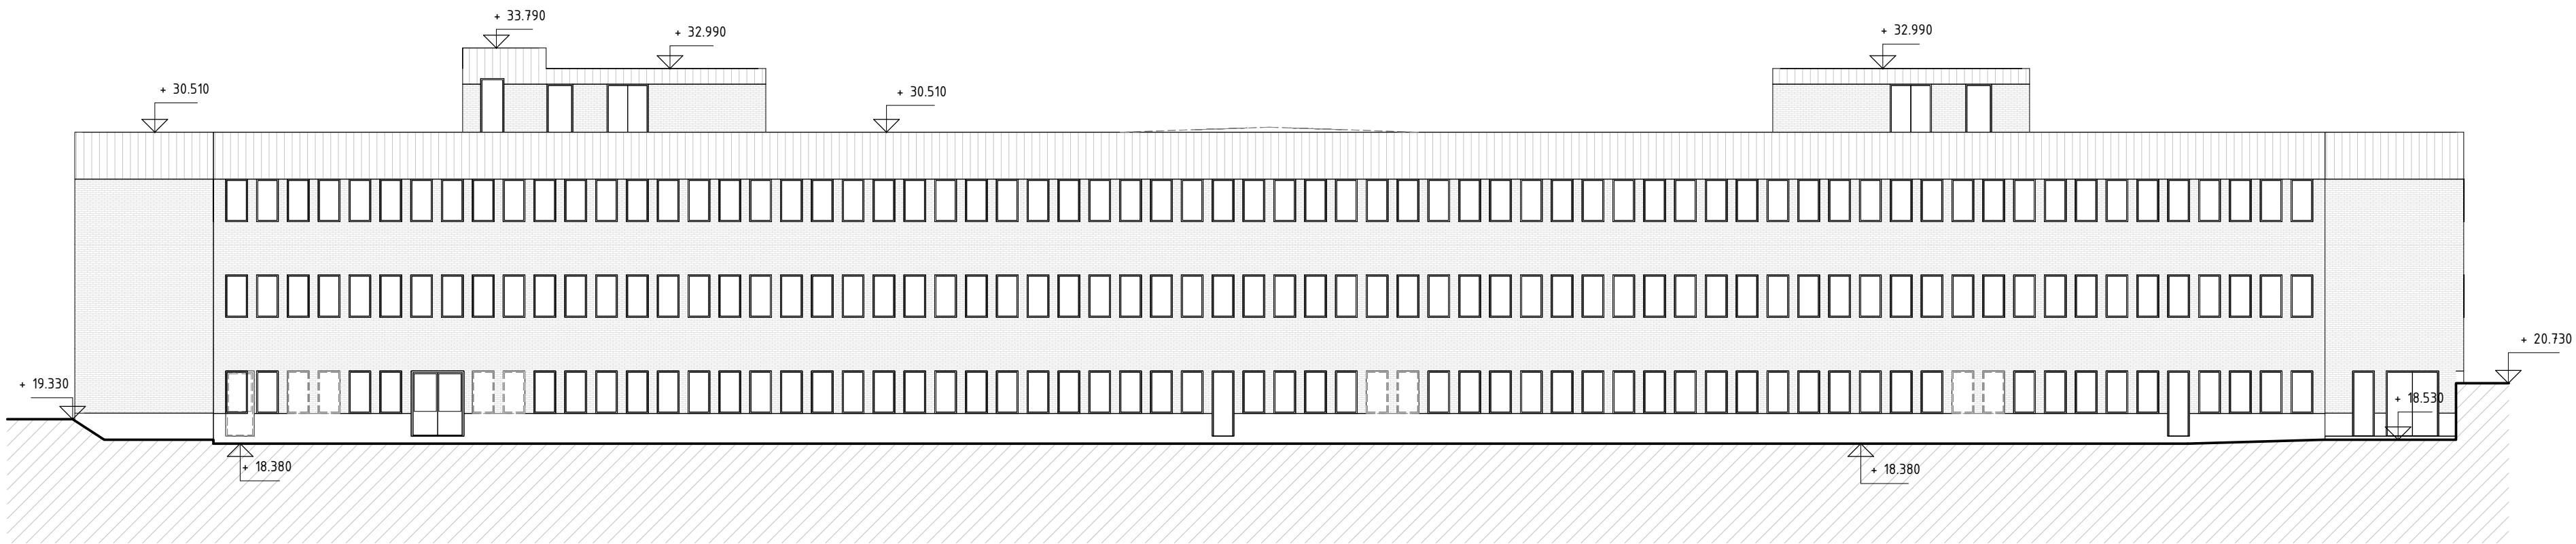


2 - FASAD MOT SÖDER, BEFINTLIG

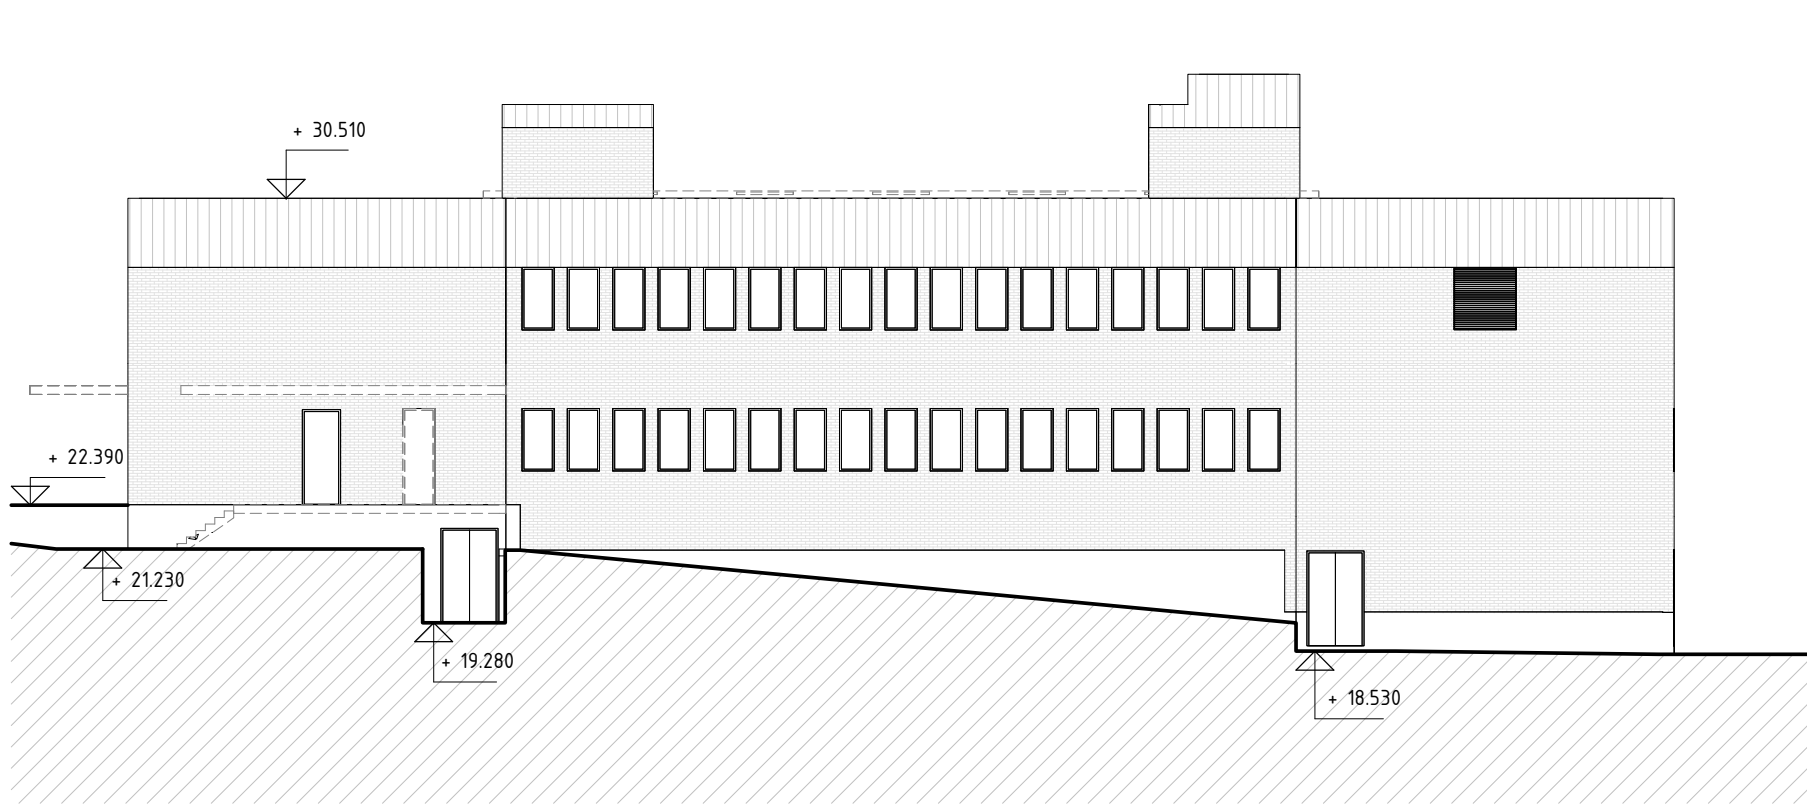

3 - FASAD MOT VÄSTER, BEFINTLIG

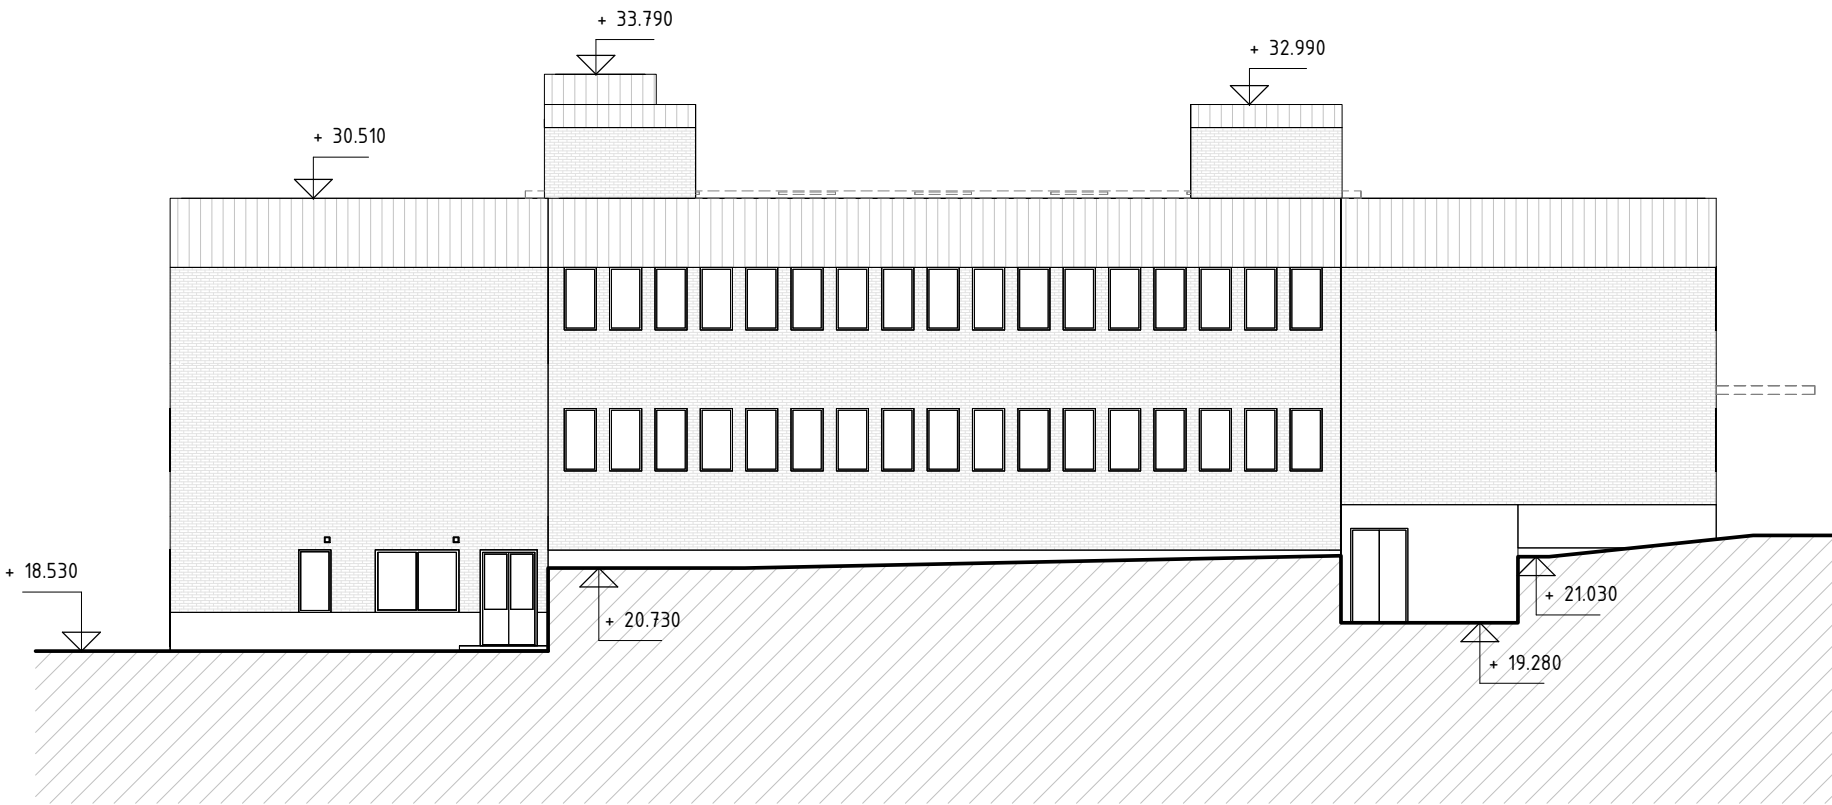

4 - FASAD MOT ÖSTER, BEFINTLIG

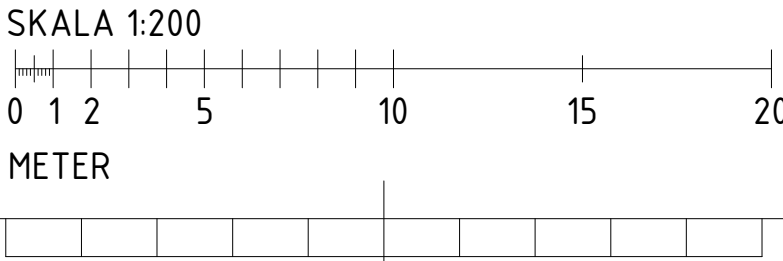

FÖRKLARINGAR

MÅTT ANGES I MILLIMETER.
PLUSHÖJDER ANGES I METER ENLIGT HÖJDSYSTEM RH2000.


RITNINGAR UPPRÄTTADE EFTER TIDIGARE UNDERLAG. BEFINTLIGA
RITNINGAR OCH RELATIONSHANDLINGAR.

FÖRESKRIFTER

-


HÄNVISNINGAR

A-40-X-XXX-SERIE BLIVANDE UTSEENDE
A-00-1-XXX-SERIE PLANER
A-00-2-XXX-SERIE SEKTIONER

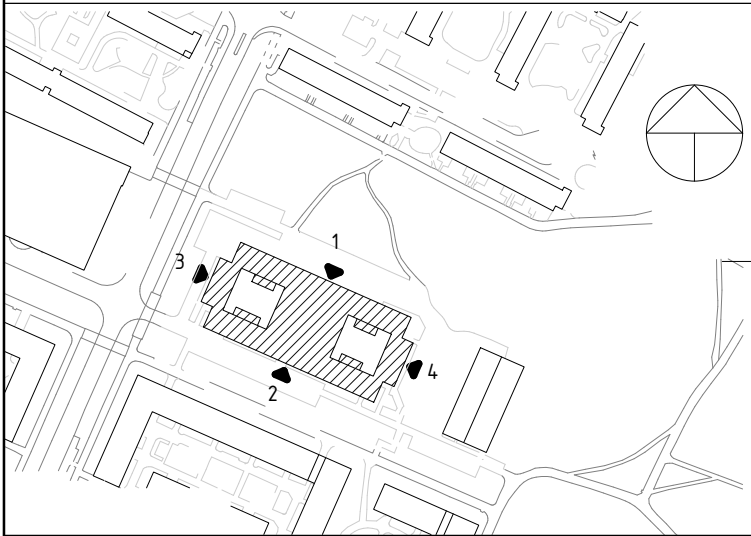


BET	ANT	ÄNDRINGEN AVSER	DATUM	SIGN
PROGRAMHANDLING				
FASTIGHET: KÄMPINGE 2:1				
BYGGNAD: A				
HUS.NR: -				
PLAN: -			SEKRETESS:	
Henning Larsen —				
 Stockholms stad				
B FASTIGHETSKONTORET			Tel: 08-508 270 00	
P WSP			Tel: 070-275 08 96	
X A HENNING LARSEN			Tel: 070-574 61 43	
K NORCONSULT			Tel: 079-142 89 57	
V SAMKONSULT			Tel: 070-278 06 29	
PROJEKT NR 74320		RITADYKONSTR. AV SE/JK/AS		ANLÄGGNINGSNUMMER 0260
DATUM 20250124		ANSVARIG M. WAHLGREN		
				DISCIPLIN A
JÄRVA SDF				
BEFINTLIGT UTSEENDE				
FASADER				
SKALA A1 1:200 A3 1:400		RITNINGSNAMN A-00-3-001		
				BET


C:\Users\JAHMSE\OneDrive - Ramboll\Documents\1760-A-4.0-V-0000_0arima Kaim.rvt
2025-01-24 15:24:39

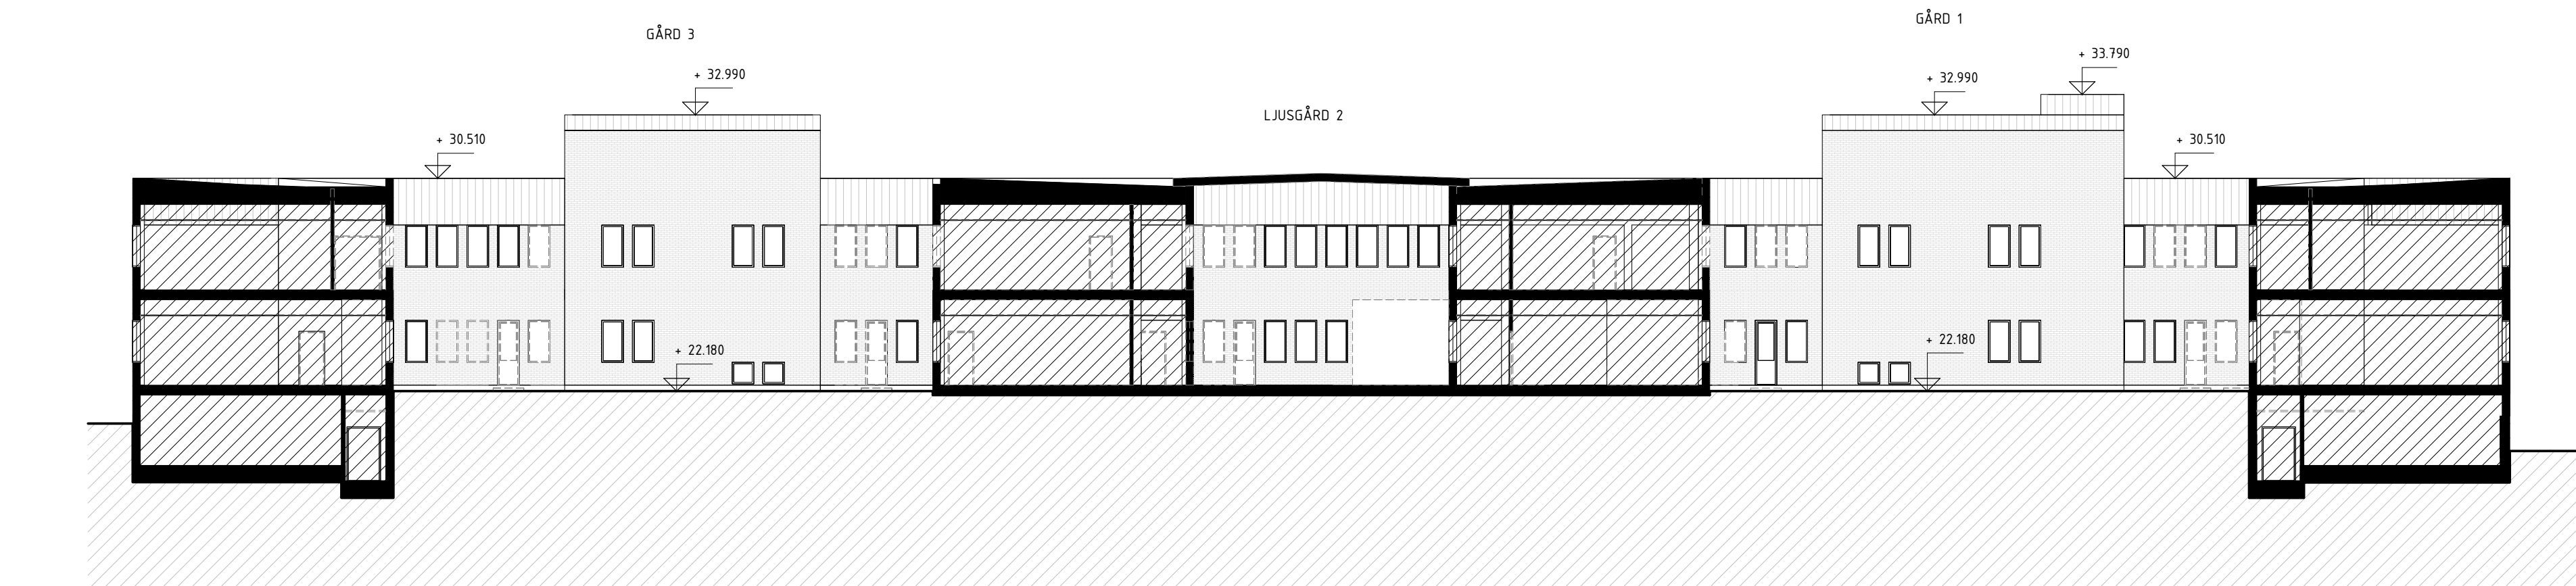


5 - FASAD MOT NORR, GÅRD 1, 2, 3. BEFINTLIG

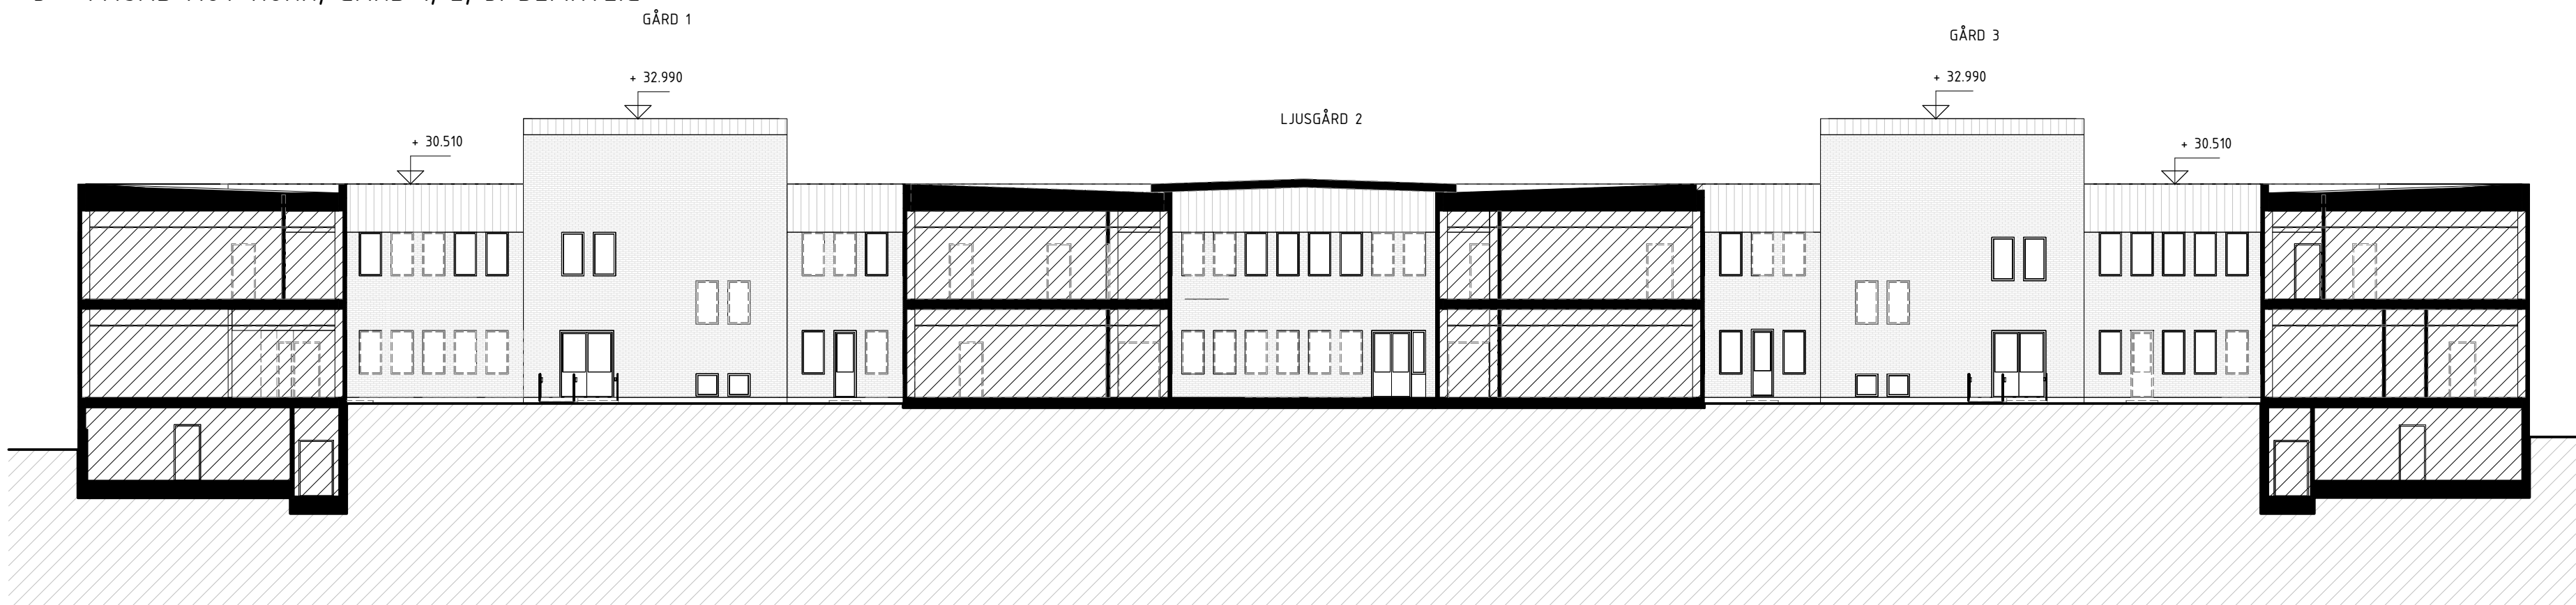


6 - FASAD MOT SÖDER, GÅRD 1, 2, 3. BEFINTLIG

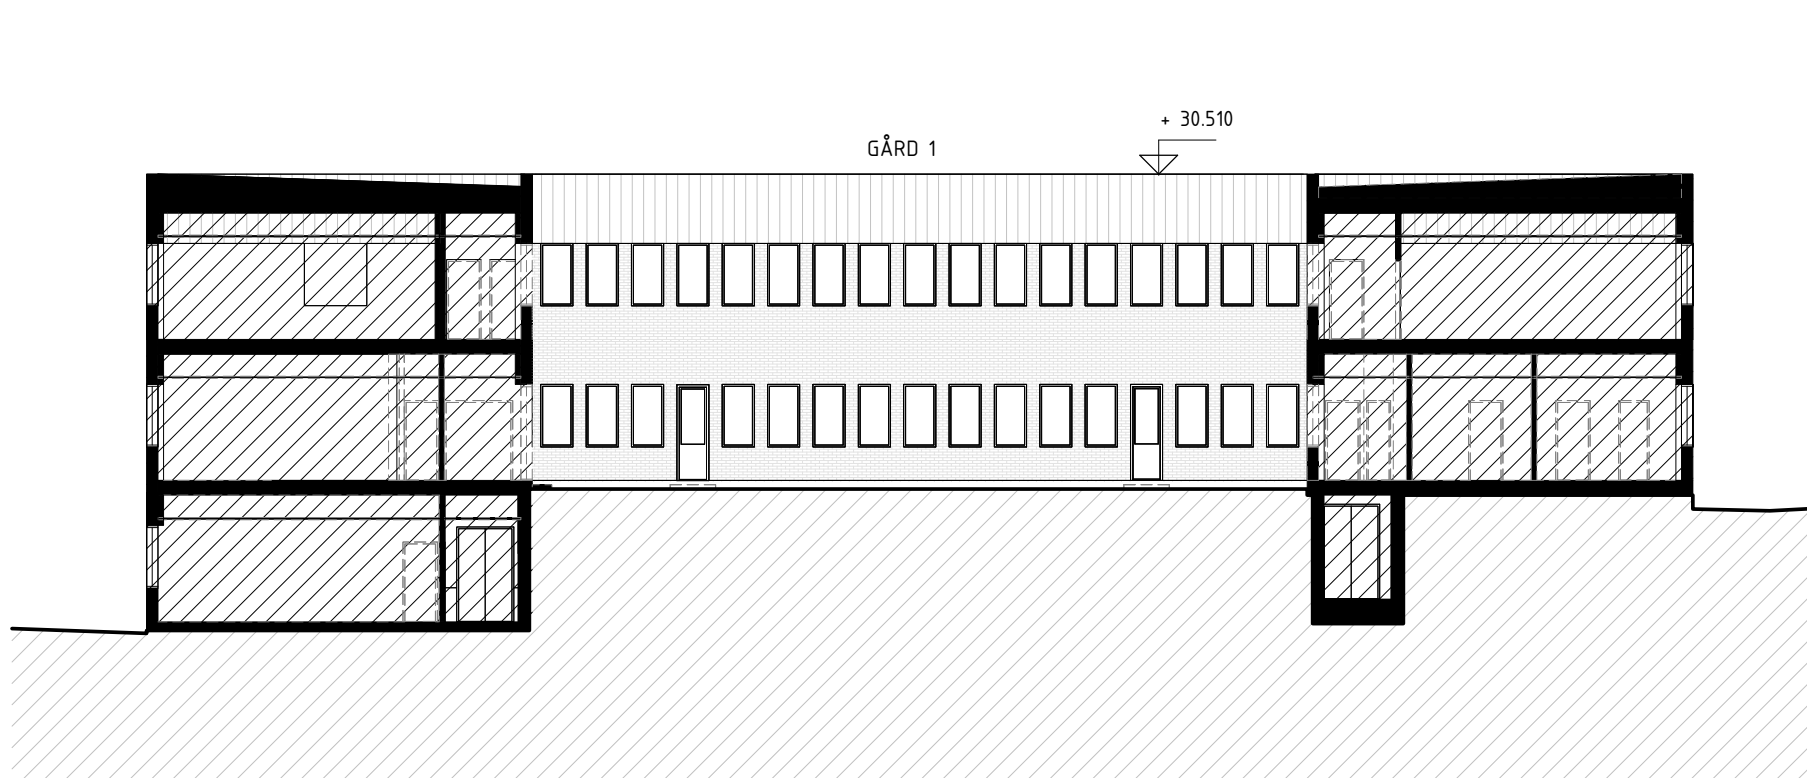


7 - FASAD MOT ÖSTER, GÅRD 1, BEFINTLIG

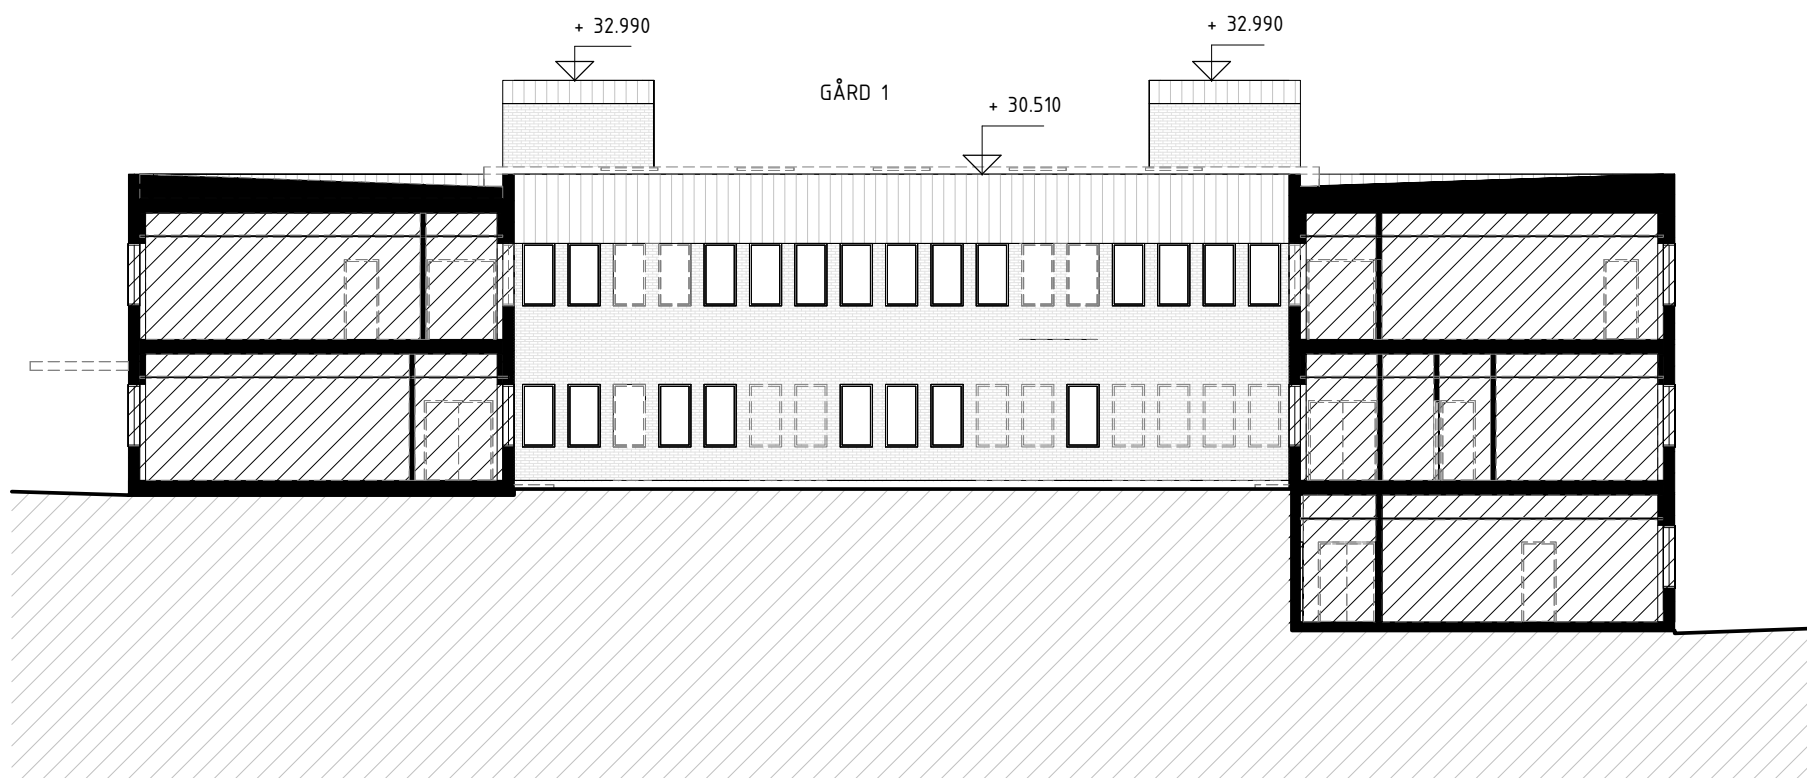


8 - FASAD MOT VÄSTER, GÅRD 1, BEFINTLIG

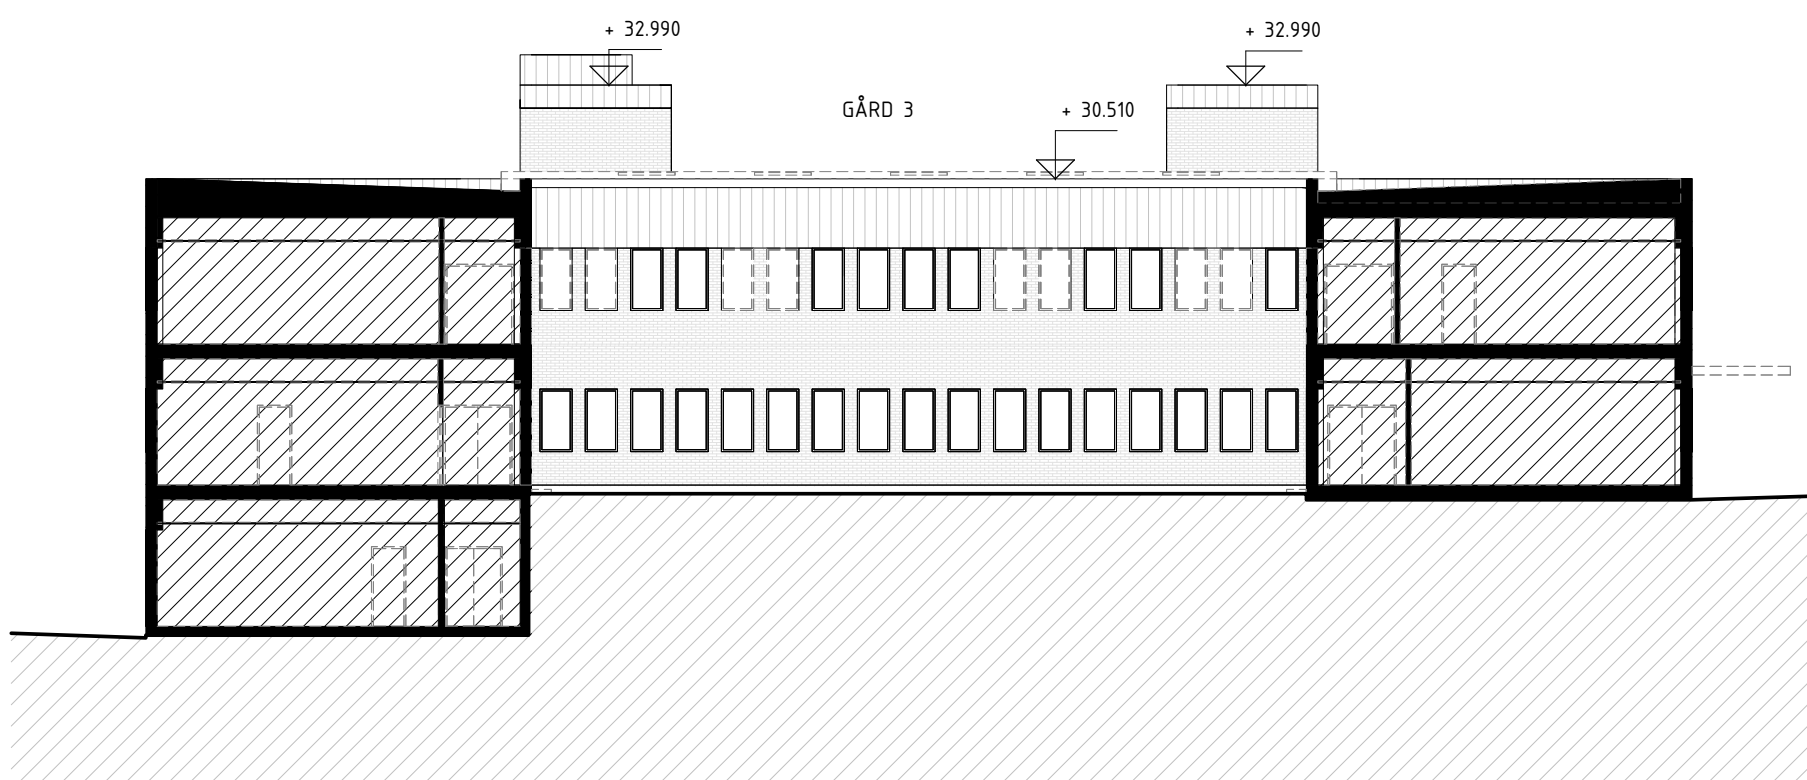

9 - FASAD MOT ÖSTER, GÅRD 3, BEFINTLIG

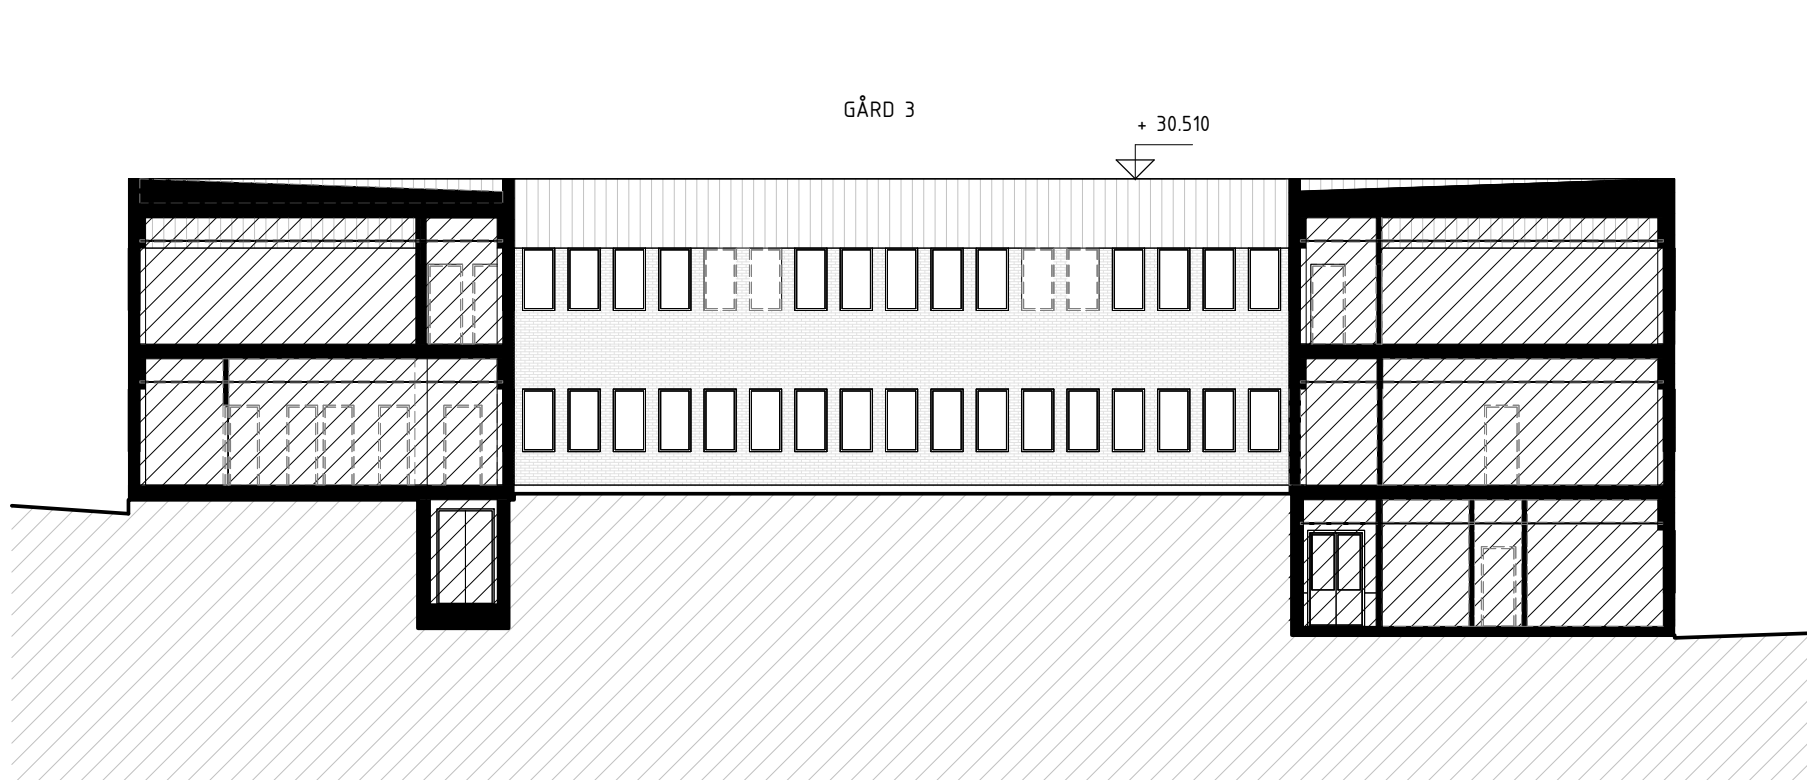

10 - FASAD MOT VÄSTER, GÅRD 3, BEFINTLIG

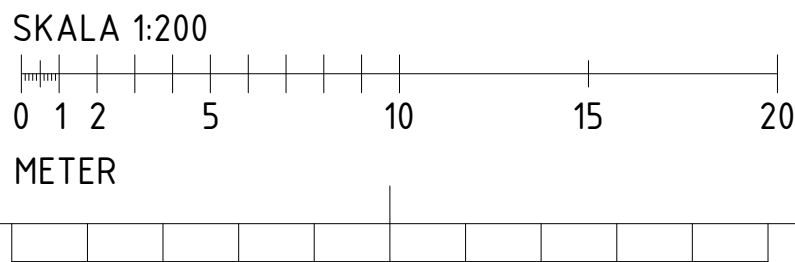

FÖRKLARINGAR


SE A-00-3-001

FÖRESKRIFTER


SE A-00-3-001

HÄNVISNINGAR

SE A-00-3-001

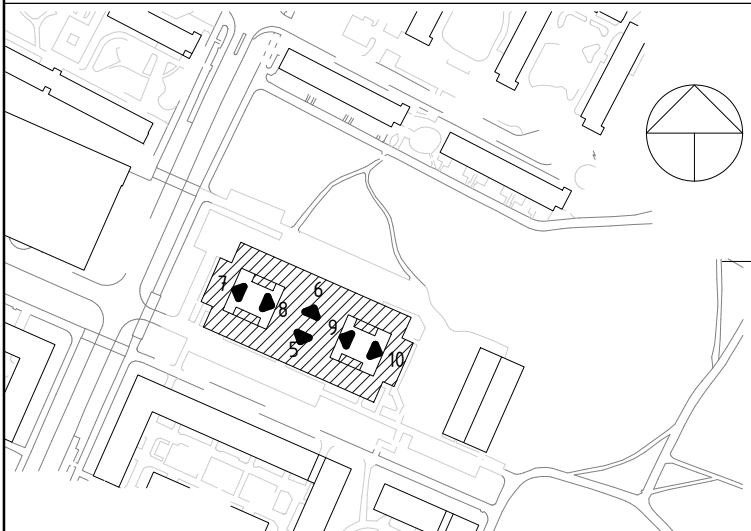

BET	ANT	ÄNDRINGEN AVSER	DATUM	SIGN
PROGRAMHANDLING				
FASTIGHET: KÄMPINGE 2:1				
BYGGNAD: A				
HUS.NR: -				
PLAN: -			SEKRETESS:	
Henning Larsen —				
 Stockholms stad				
B		FASTIGHETSKONTORET		Tel: 08-508 270 00
P		WSP		Tel: 070-275 08 96
X		A HENNING LARSEN		Tel: 070-574 61 43
K		NORCONSULT		Tel: 079-142 89 57
V		SAMKONSULT		Tel: 070-278 06 29
PROJECT NR		RITADKONSTR. AV		ANLÄGGNINGSNUMMER
74320		SE/JK/AS		0260
DATUM		ANSVARIG		DISCIPLIN
20250124		M. WAHLGREN		A
JÄRVA SDF				
BEFINTLIGT UTSEENDE				
FASADER MOT GÅRD				
SKALA		RITNINGSNAMN		
A1 1:200		A-00-3-002		
A3 1:400				

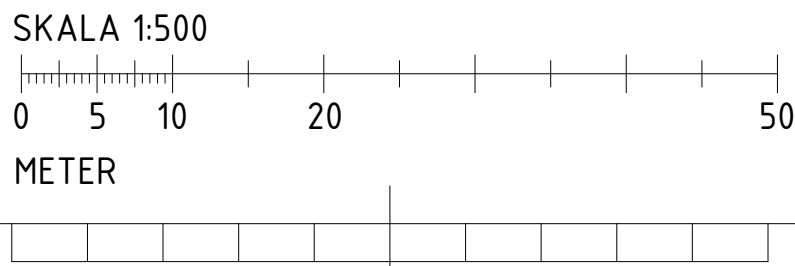

FÖRKLARINGAR

MÅTT ANGES I MILLIMETER.
PLUSHÖJDER ANGES I METER ENLIGT HÖJDSYSTEM RH2000.
RITNINGAR UPPRÄTTADE EFTER TIDIGARE UNDERLAG. BEFINTLIGA
RITNINGAR OCH RELATIONSHANDLINGAR.


LANDSKAPSSKISS ENLIGT LA.

- HUVUDENTRÉ
- ÖVRIGA ENTRÉER
- FASTIGHETSGRÄNS


FÖRESKRIFTER

HÄNVISNINGAR

A-00-X-XXX-SERIE BEFINTLIGT UTSEENDE
A-40-X-XXX-SERIE BLIVANDE UTSEENDE

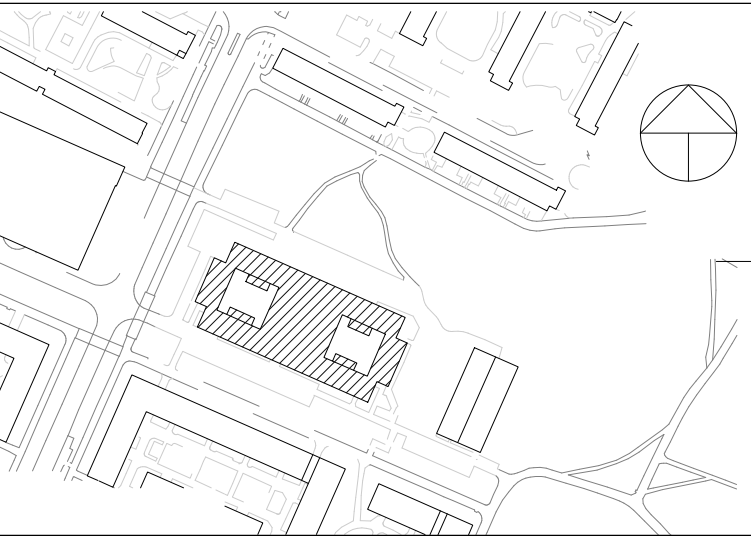

BET	ANT	ANDRINGEN AVSER		DATUM	SIGN
PROGRAMHANDLING					
FASTIGHET: KÄMPINGE 2:1					
BYGGNAD: A					
HUS.NR:					
PLAN: -		SEKRETESS:			
Henning Larsen —					
 Stockholms stad					
B FASTIGHETSKONTORET		Tel: 08-508 270 00			
P WSP		Tel: 070-275 08 96			
A HENNING LARSEN		Tel: 070-574 61 43			
K NORCONSULT		Tel: 079-142 89 57			
V SAMKONSULT		Tel: 070-278 06 29			
PROJECT NR 74320		RITADYKONSTR. AV SE/JK/AS		ANLÄGGNINGSNUMMER 0260	
DATUM 20250124		ANSVARIG M. WAHLGREN			DISCIPLIN A
JÄRVA SDF					
SAMMANSATT REDOVISNING					
SITUATIONSPLAN					
SKALA A1 1:500 A3 1:1000		RITNINGSNAMN A-01-1-001			BET

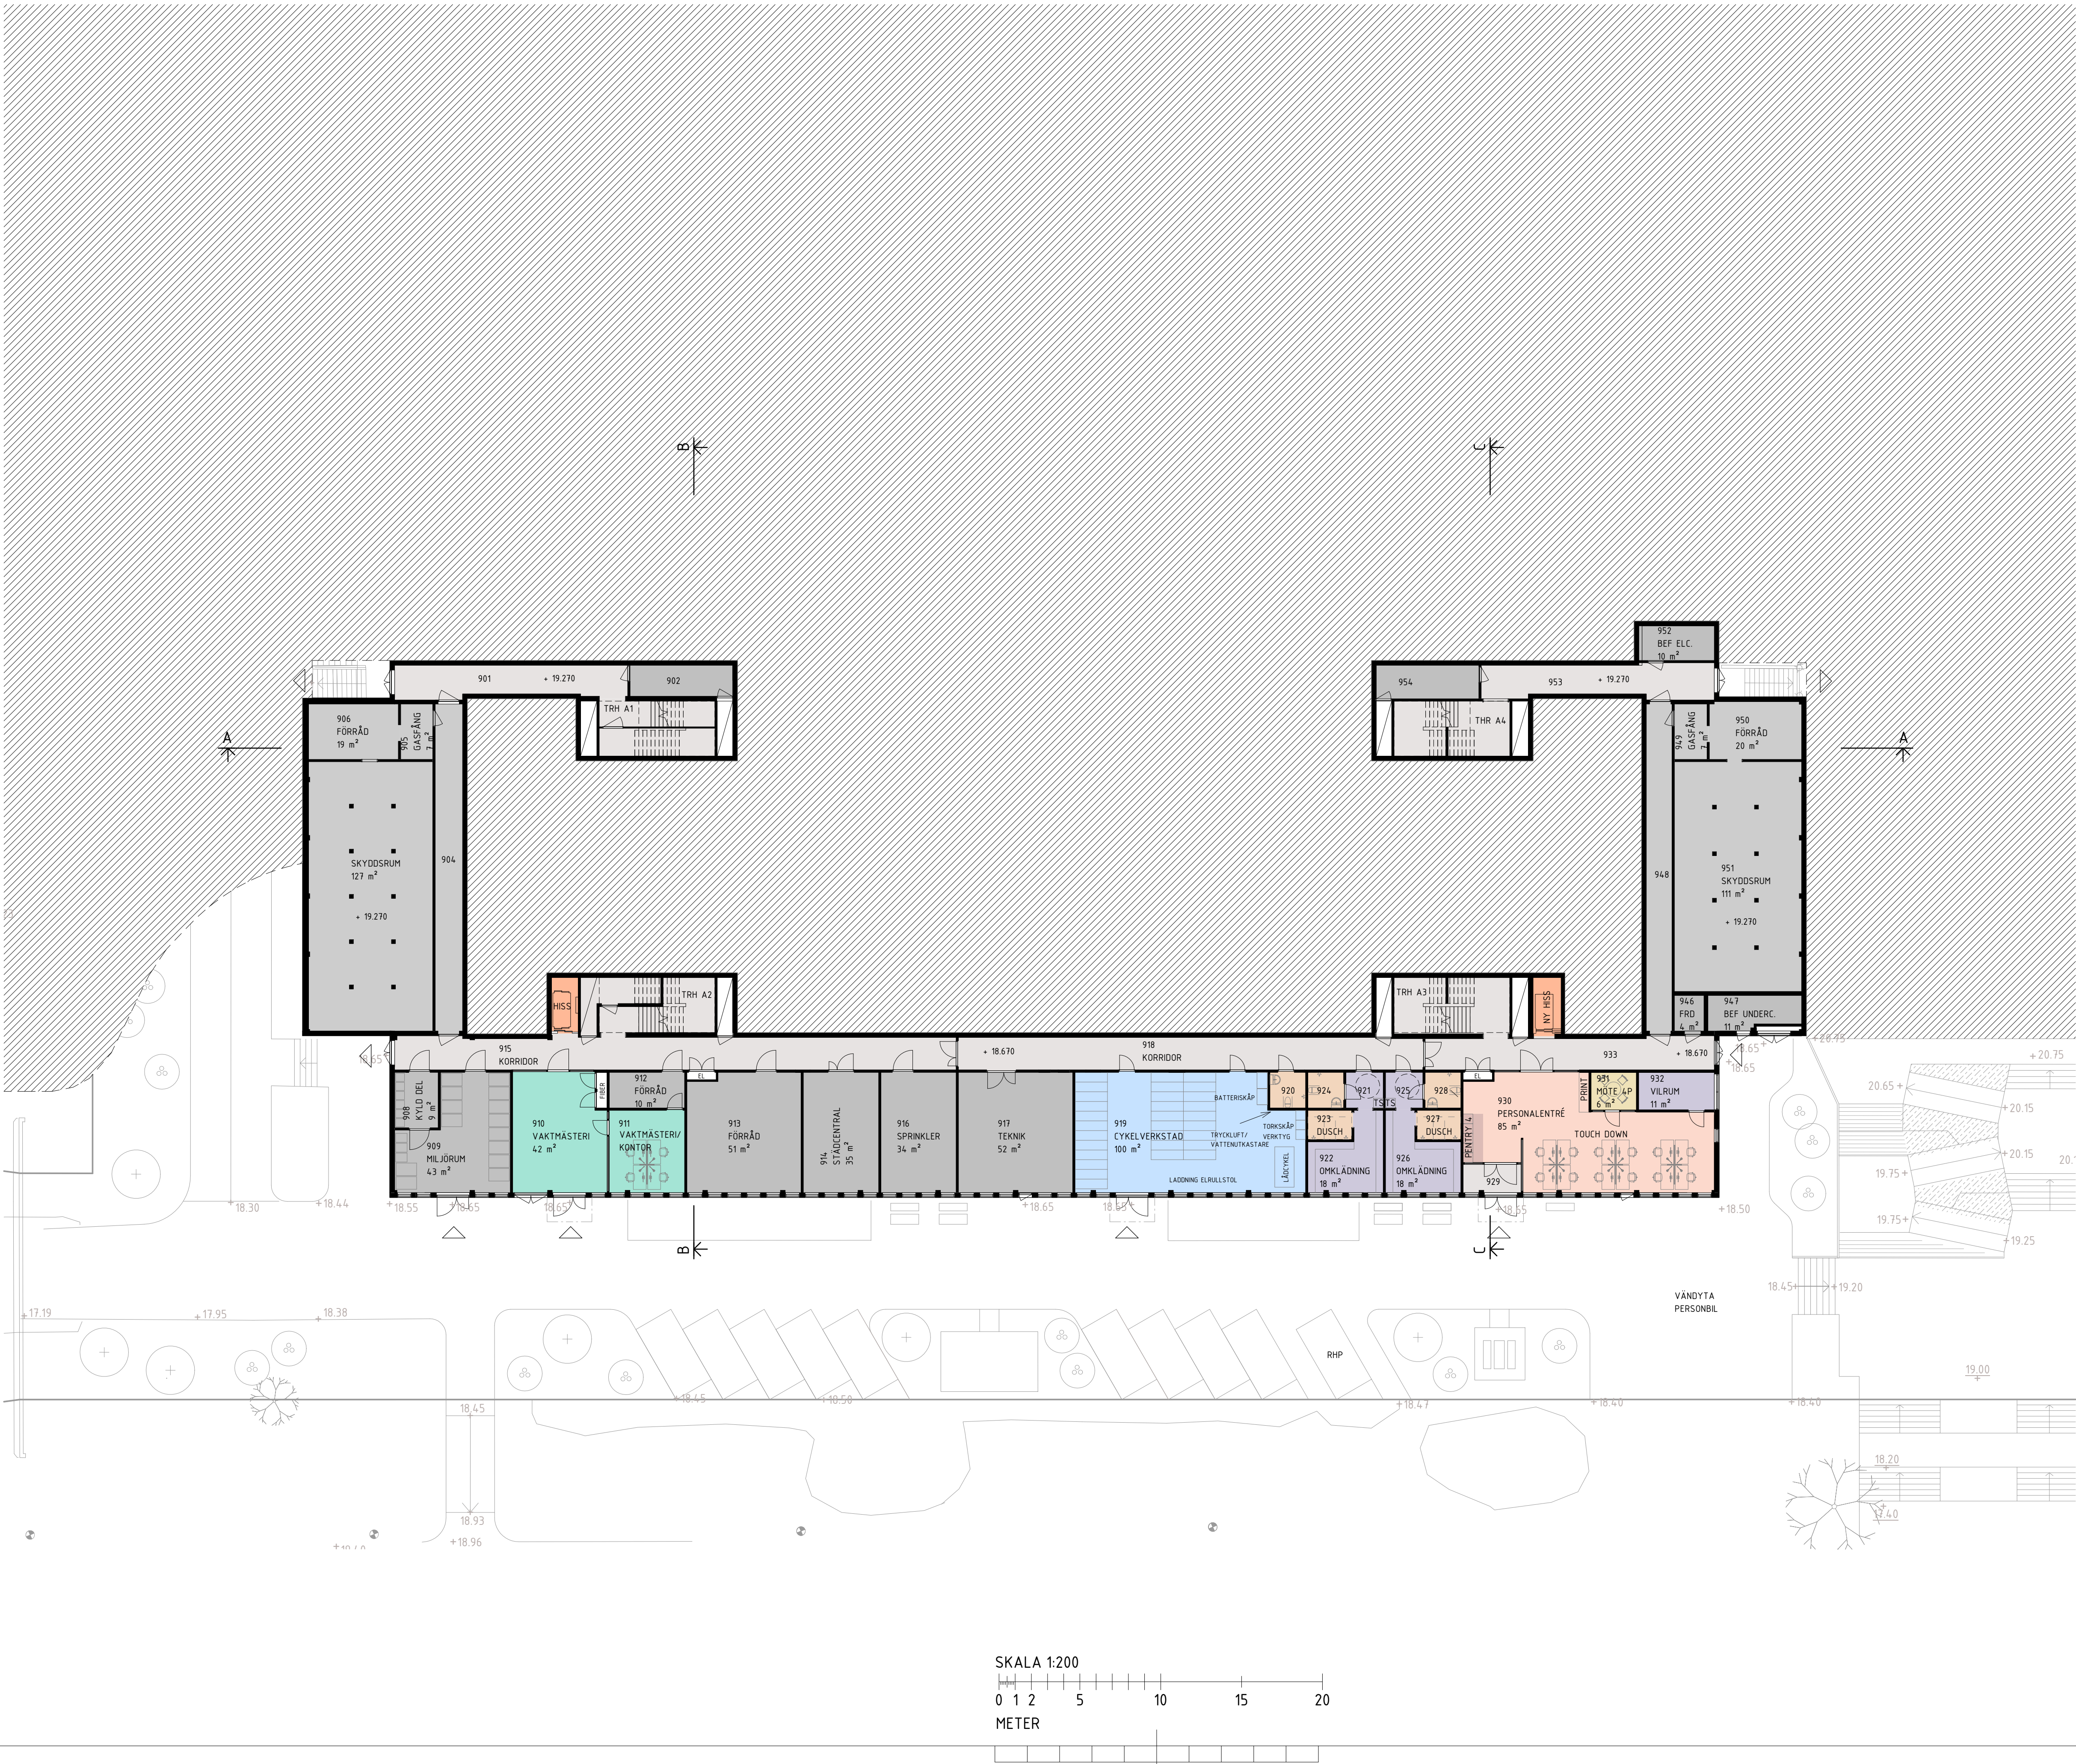

FÖRKLARINGAR

MÅTT ANGES I MILLIMETER.
PLUSHÖJDER ANGES I METER ENLIGT HÖJDSYSTEM RH2000.
RITNINGAR UPPRÄTTADE EFTER TIOGÅRE UNDERLAG. BEFINTLIGA
RITNINGAR OCH RELATIONSHANDLINGAR.
PÅ PLANER REDOVISAS EN SCHEMATISK MÖBLERING. DENNA KAN
KOMMA ATT ÄNDRAS UNDER SAMORDNING MED VERKSAMHETEN.
PELÄRE INOM BEBYGGDA GÅRDAR ENL. K. PLACERING SAMORDNAS I
NÄSTA SKEDE.
GESTALTNING AV GLASTAK TILL LJUSGÅRDAR TAS FRAM I
KOMMANDE SKEDE SH.
TILLGÄNGLIGHET TILL TAKTERRASS PLAN 12 LÖSES MED
RAMP/LYFTBORD ENLIGT TIL.


- HUVUDENTRÉ
- ÖVRIGA ENTRÉER
- BEFINTLIGA DÖRRAR
- NYA DÖRRAR
- MÖJLIG INDELNING
- TS TORKSKÅP
- K KYLSKÅP
- F FRYS
- DM DISKMASKIN

FÖRESKRIFTER

-

HÄNVISNINGAR

- A-01-1-001 SITUATIONSPLAN
- A-00-X-XXX-SERIE BEFINTLIGT UTSEENDE
- A-40-2-XXX-SERIE SEKTIONER
- A-40-3-XXX-SERIE FASADER
- RUMSFUNKTIONSPROGRAM
- GESTALTNINGSPROGRAM

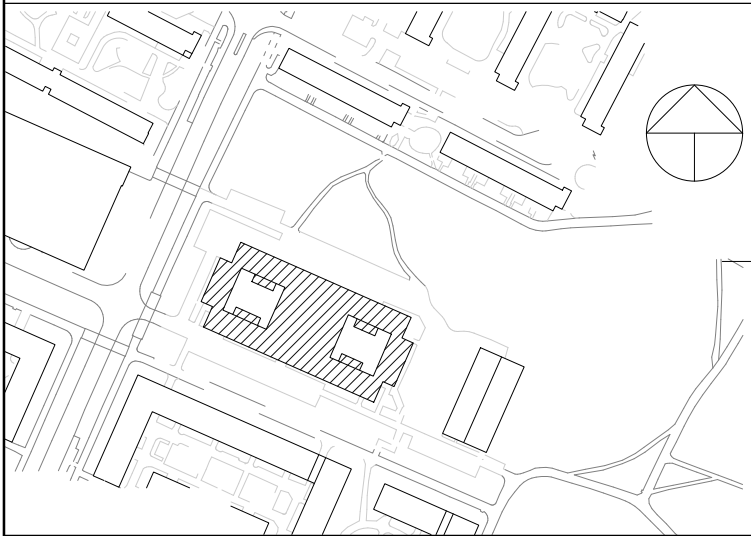

BET	ANT	ÄNDRINGEN AVSER	DATUM	SIGN
-----	-----	-----------------	-------	------

PROGRAMHANDLING

FASTIGHET: KÄMPINGE 2:1
BYGGNAD: A
HUS.NR: -
PLAN: 09

SEKRETESS:

Henning
Larsen






B	FASTIGHETSKONTORET	Tel: 08-508 270 00
P	WSP	Tel: 070-275 08 96
A	HENNING LARSEN	Tel: 070-574 61 43
K	NORCONSULT	Tel: 079-142 89 57
V	SAMKONSULT	Tel: 070-278 06 29

PROJEKT NR	RITADKONSTR. AV	ANLÄGGNINGSNUMMER
74320	SE/JK/AS	0260
DATUM	ANSVARIG	DISCIPLIN
20250124	M. WAHLGREN	A

JÄRVA SDF
SAMMANSATT REDOVISNING
PLAN 09

SKALA	RITNINGSNAMN	BET
A1 1:200 A3 1:400	A-40-1-001	

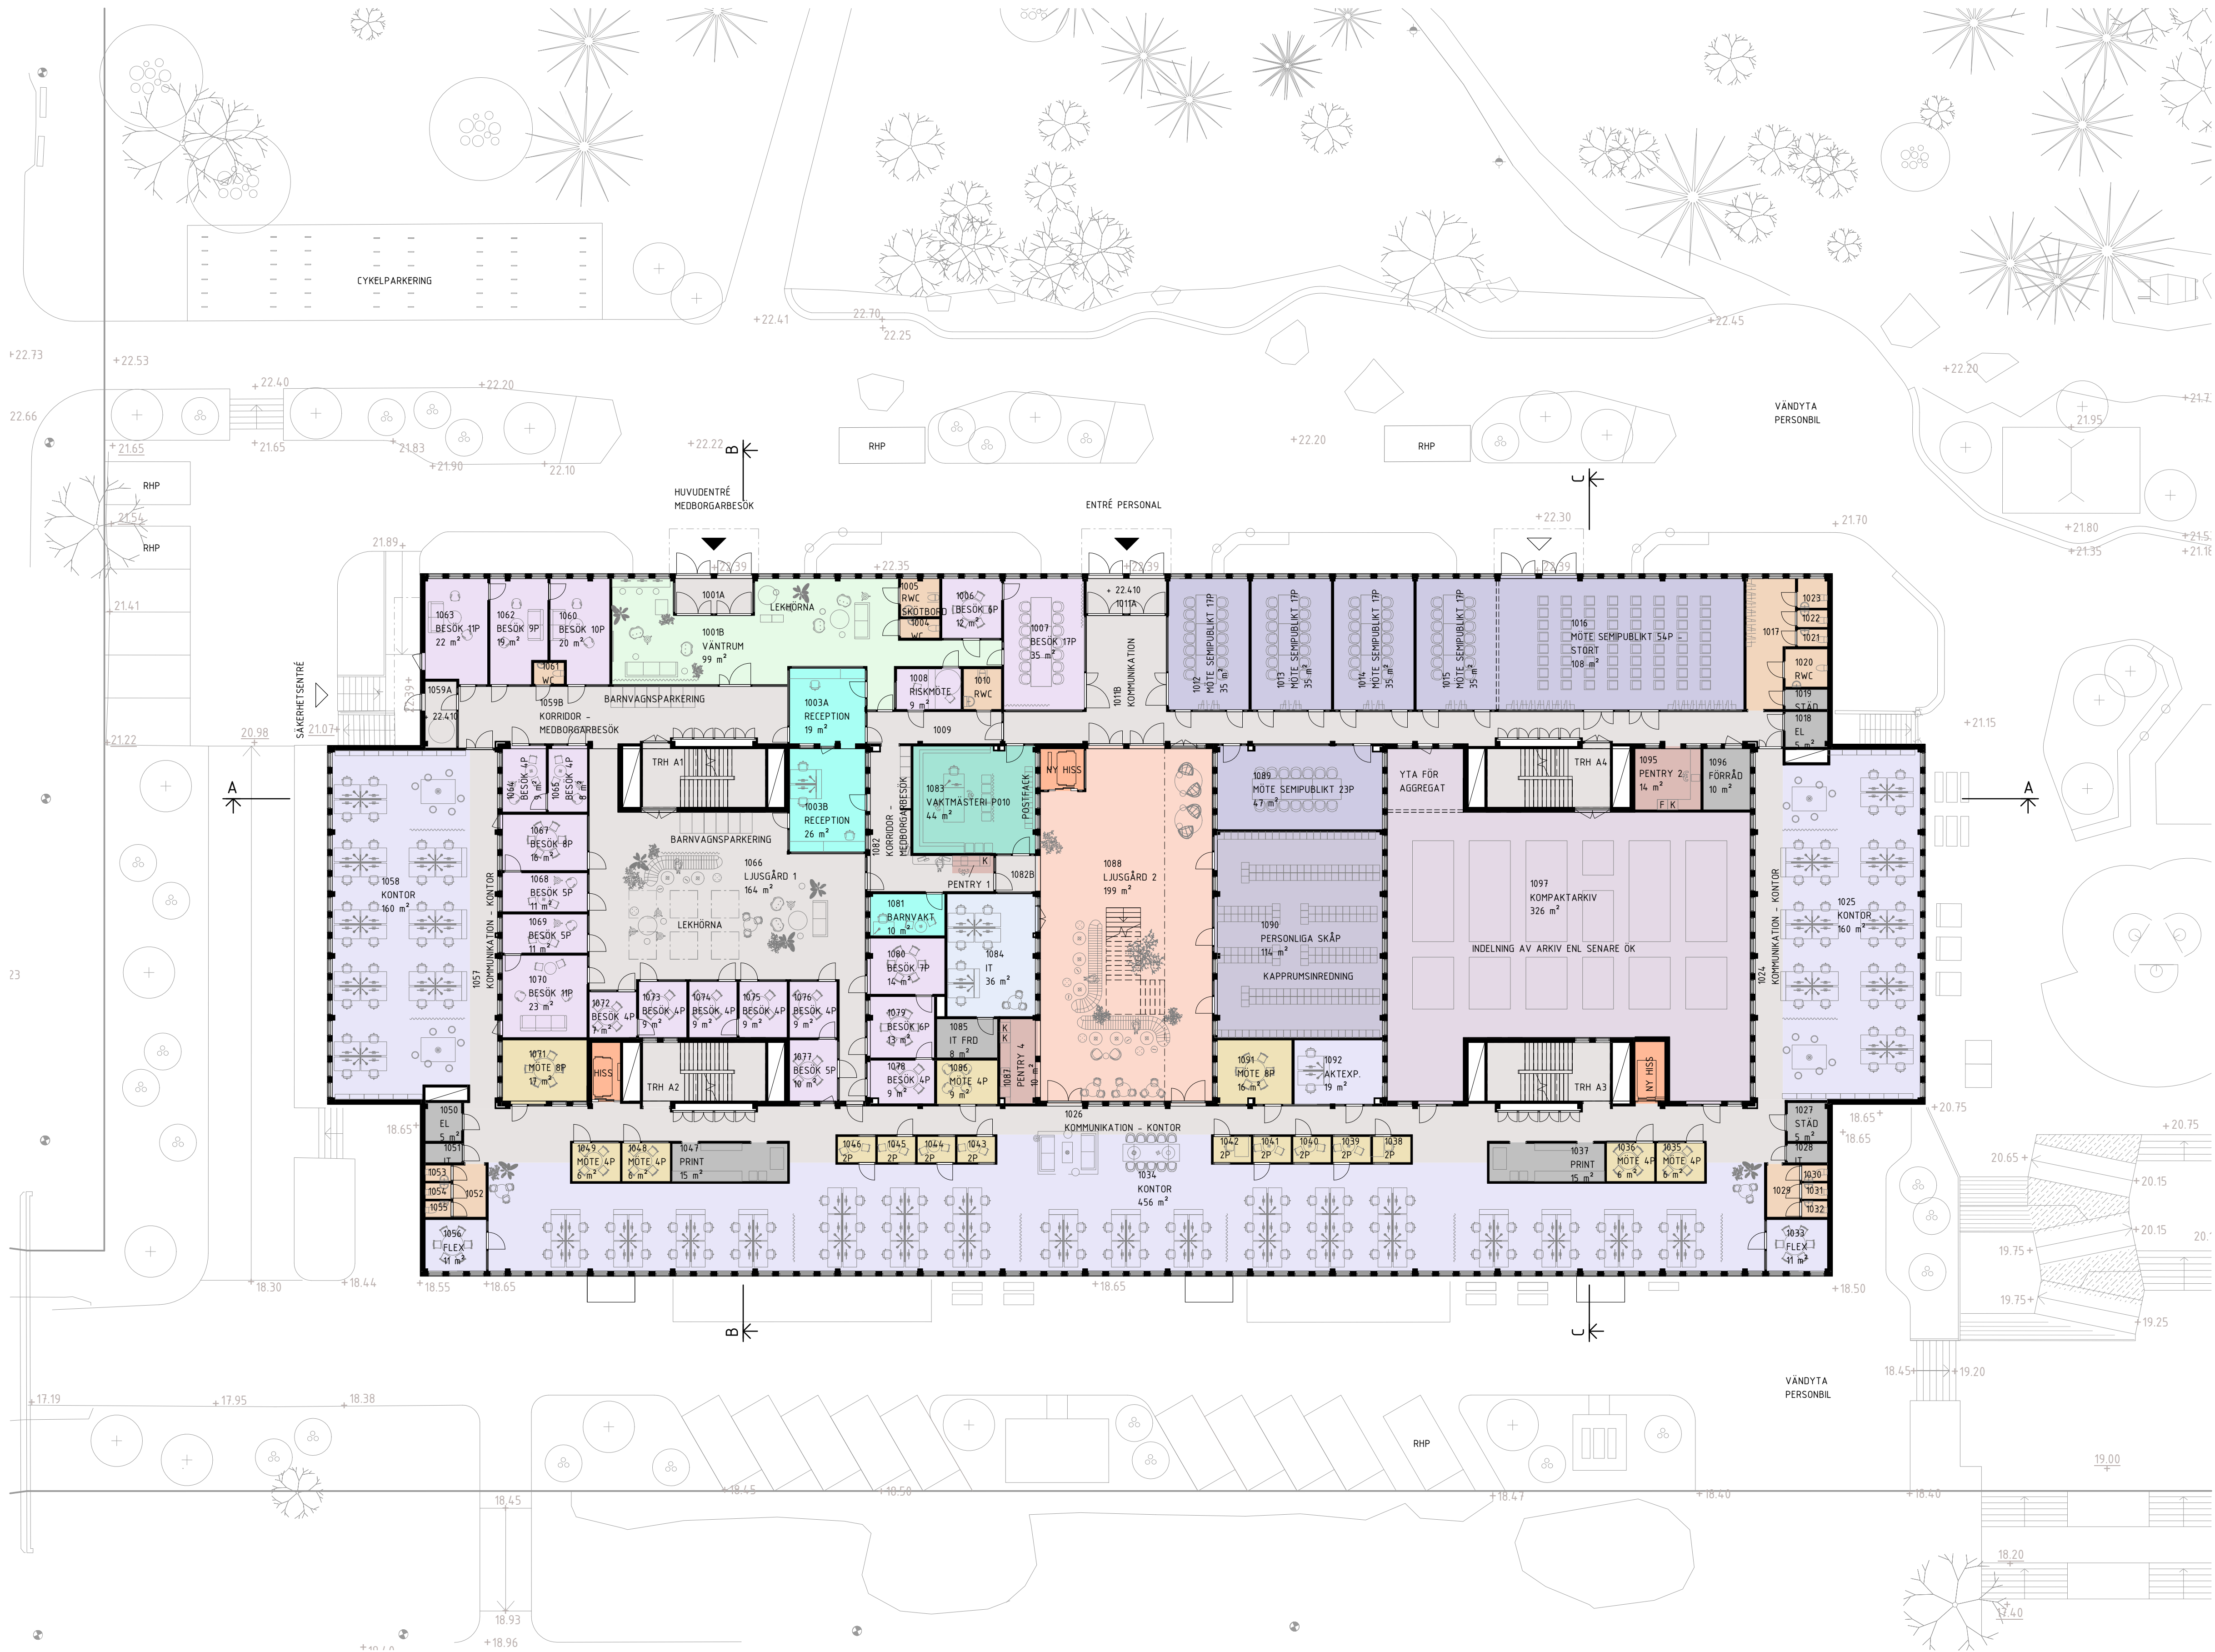

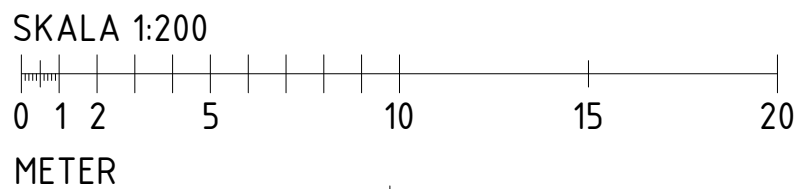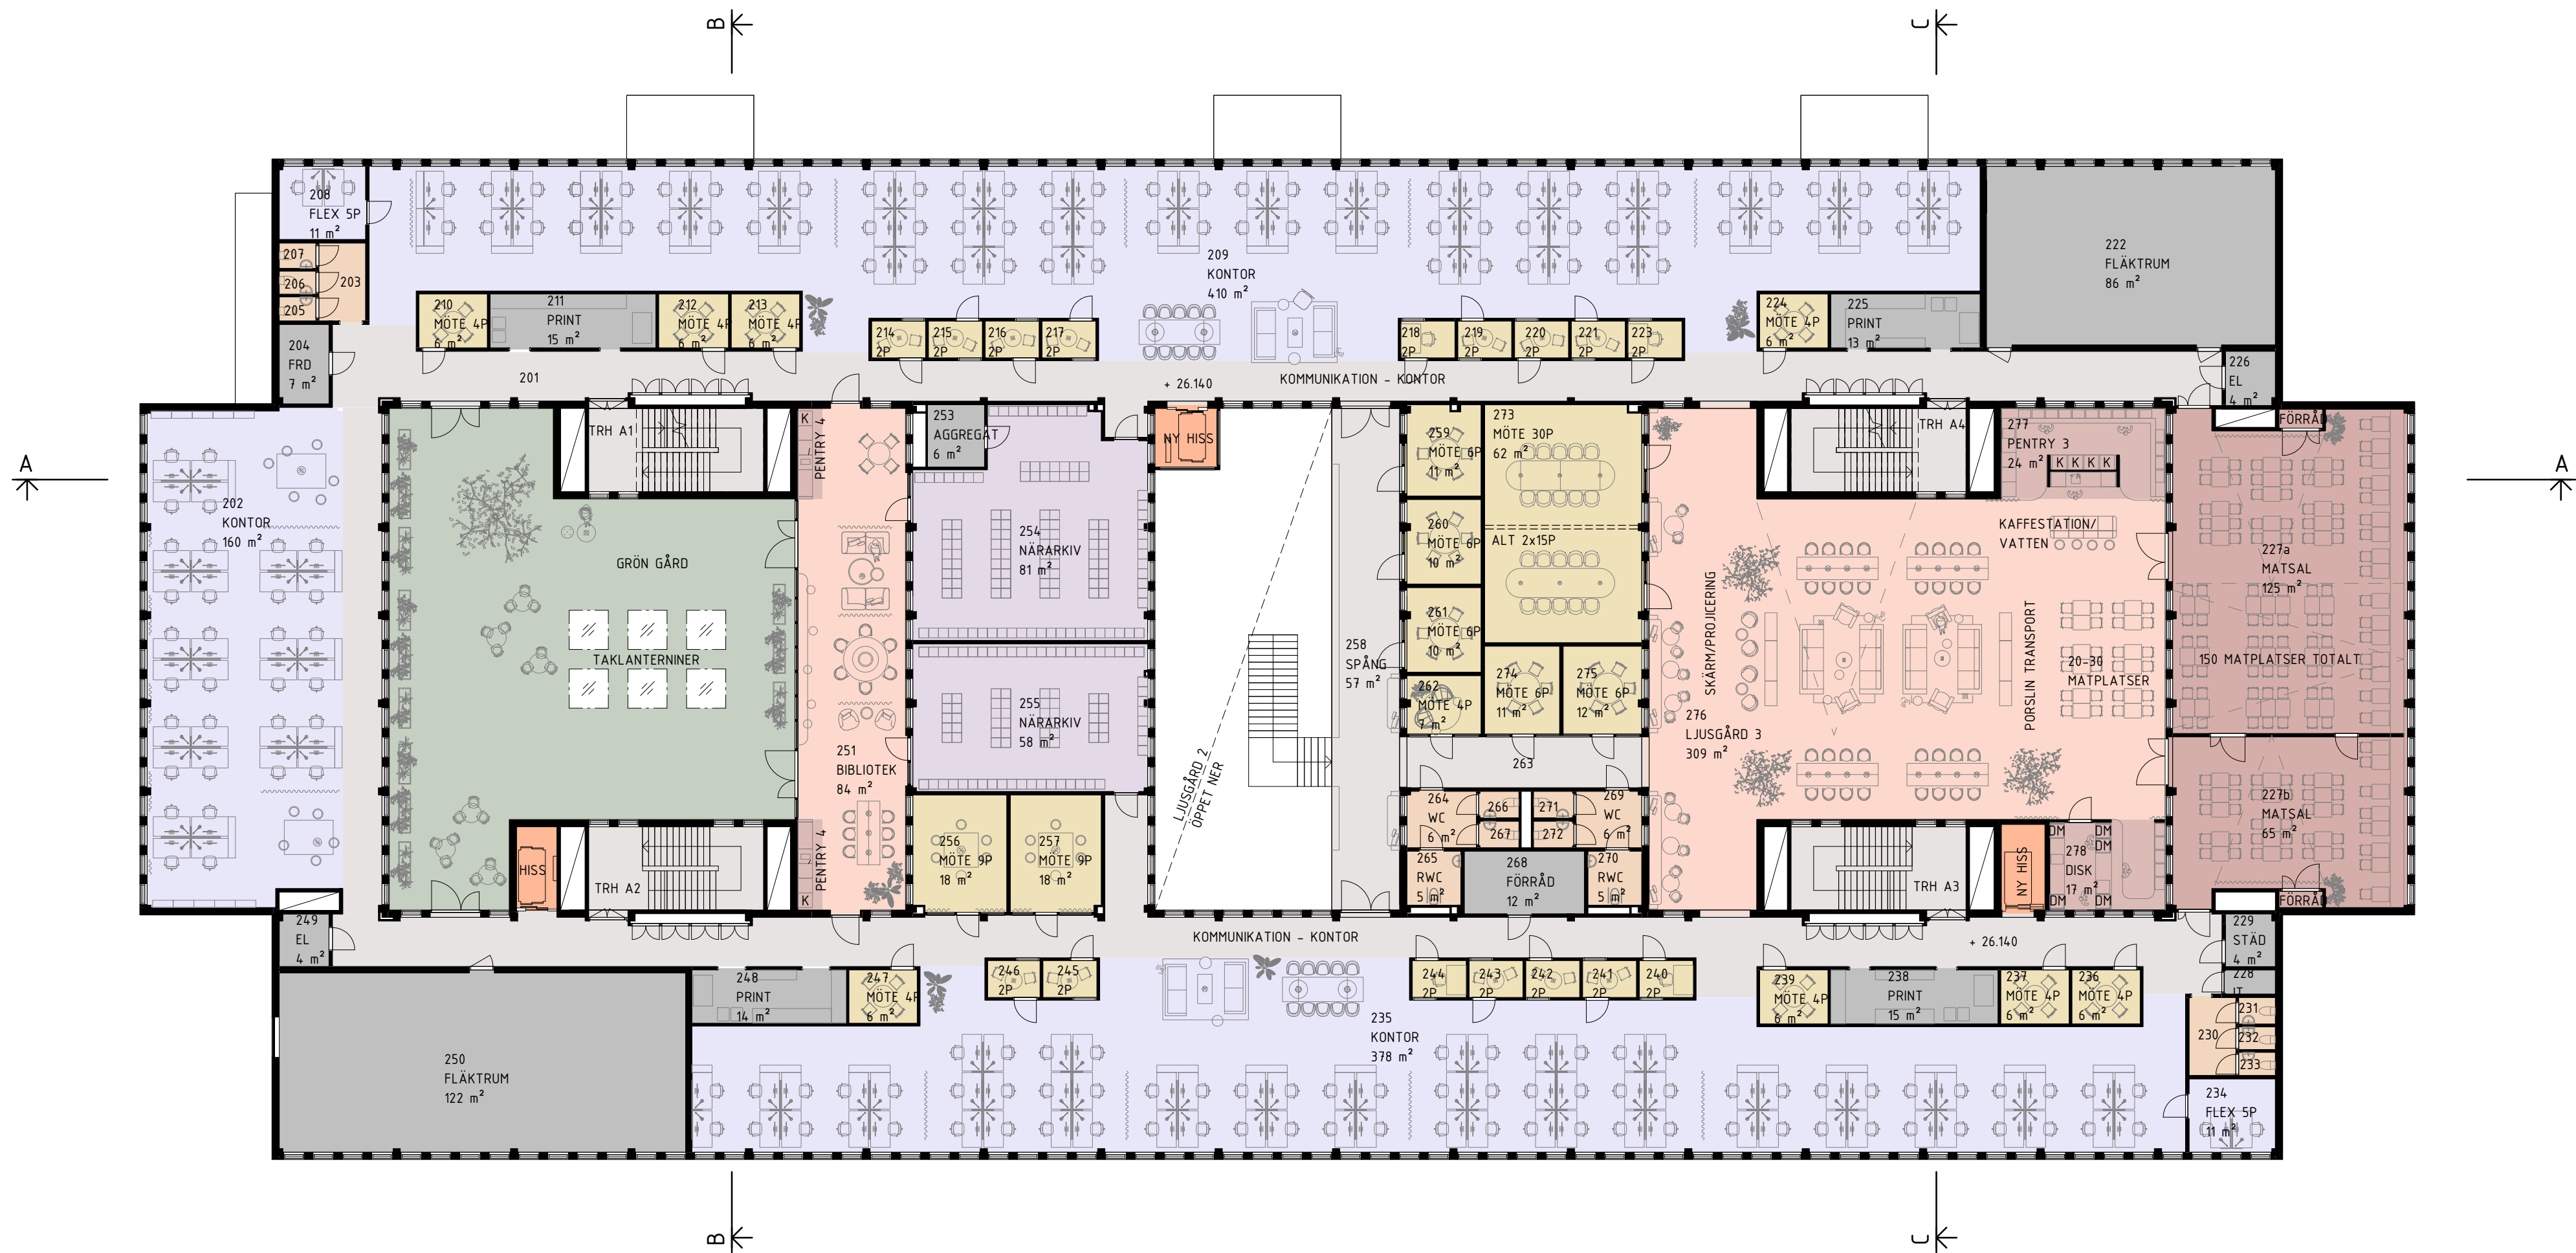

FÖRKLARINGAR


SE A-40-1-001

FÖRESKRIFTER

SE A-40-1-001

HÄNVISNINGAR

SE A-40-1-001

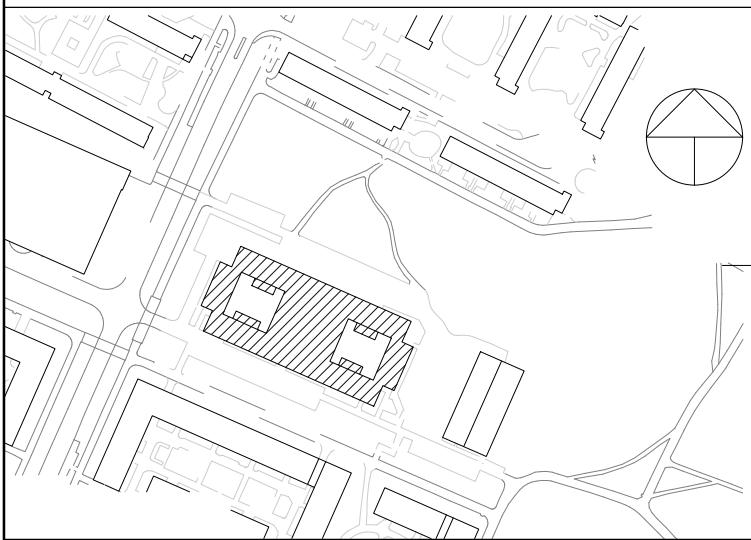

BET	ANT	ÄNDRINGEN AVSER	DATUM	SIGN
-----	-----	-----------------	-------	------

PROGRAMHANDLING

FASTIGHET: KÄMPINGE 2:1

BYGGNAD: A

HUS.NR: -

PLAN: 11

SEKRETESS:

**Henning
Larsen**





**Stockholms
stad**

B	FASTIGHETSKONTORET	Tel: 08-508 270 00
P	WSP	Tel: 070-275 08 96
☒	A HENNING LARSEN	Tel: 070-574 61 43
K	NORCONSULT	Tel: 079-142 89 57
V	SAMCONSULT	Tel: 070-278 06 29

PROJEKT NR	RITADYKONSTR. AV	ANLÄGGNINGSNUMMER
74320	SE/JK/AS	0260
DATUM	ANSVARIG	DISCIPLIN
20250124	M. WAHLGREN	A

JÄRVA SDF
SAMMANSATT REDOVISNING
PLAN 11

SKALA	RITNINGSNAMN	BET
A1 1:200 A3 1:400	A-40-1-003	

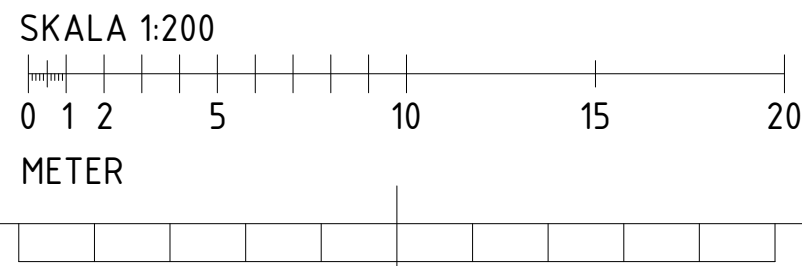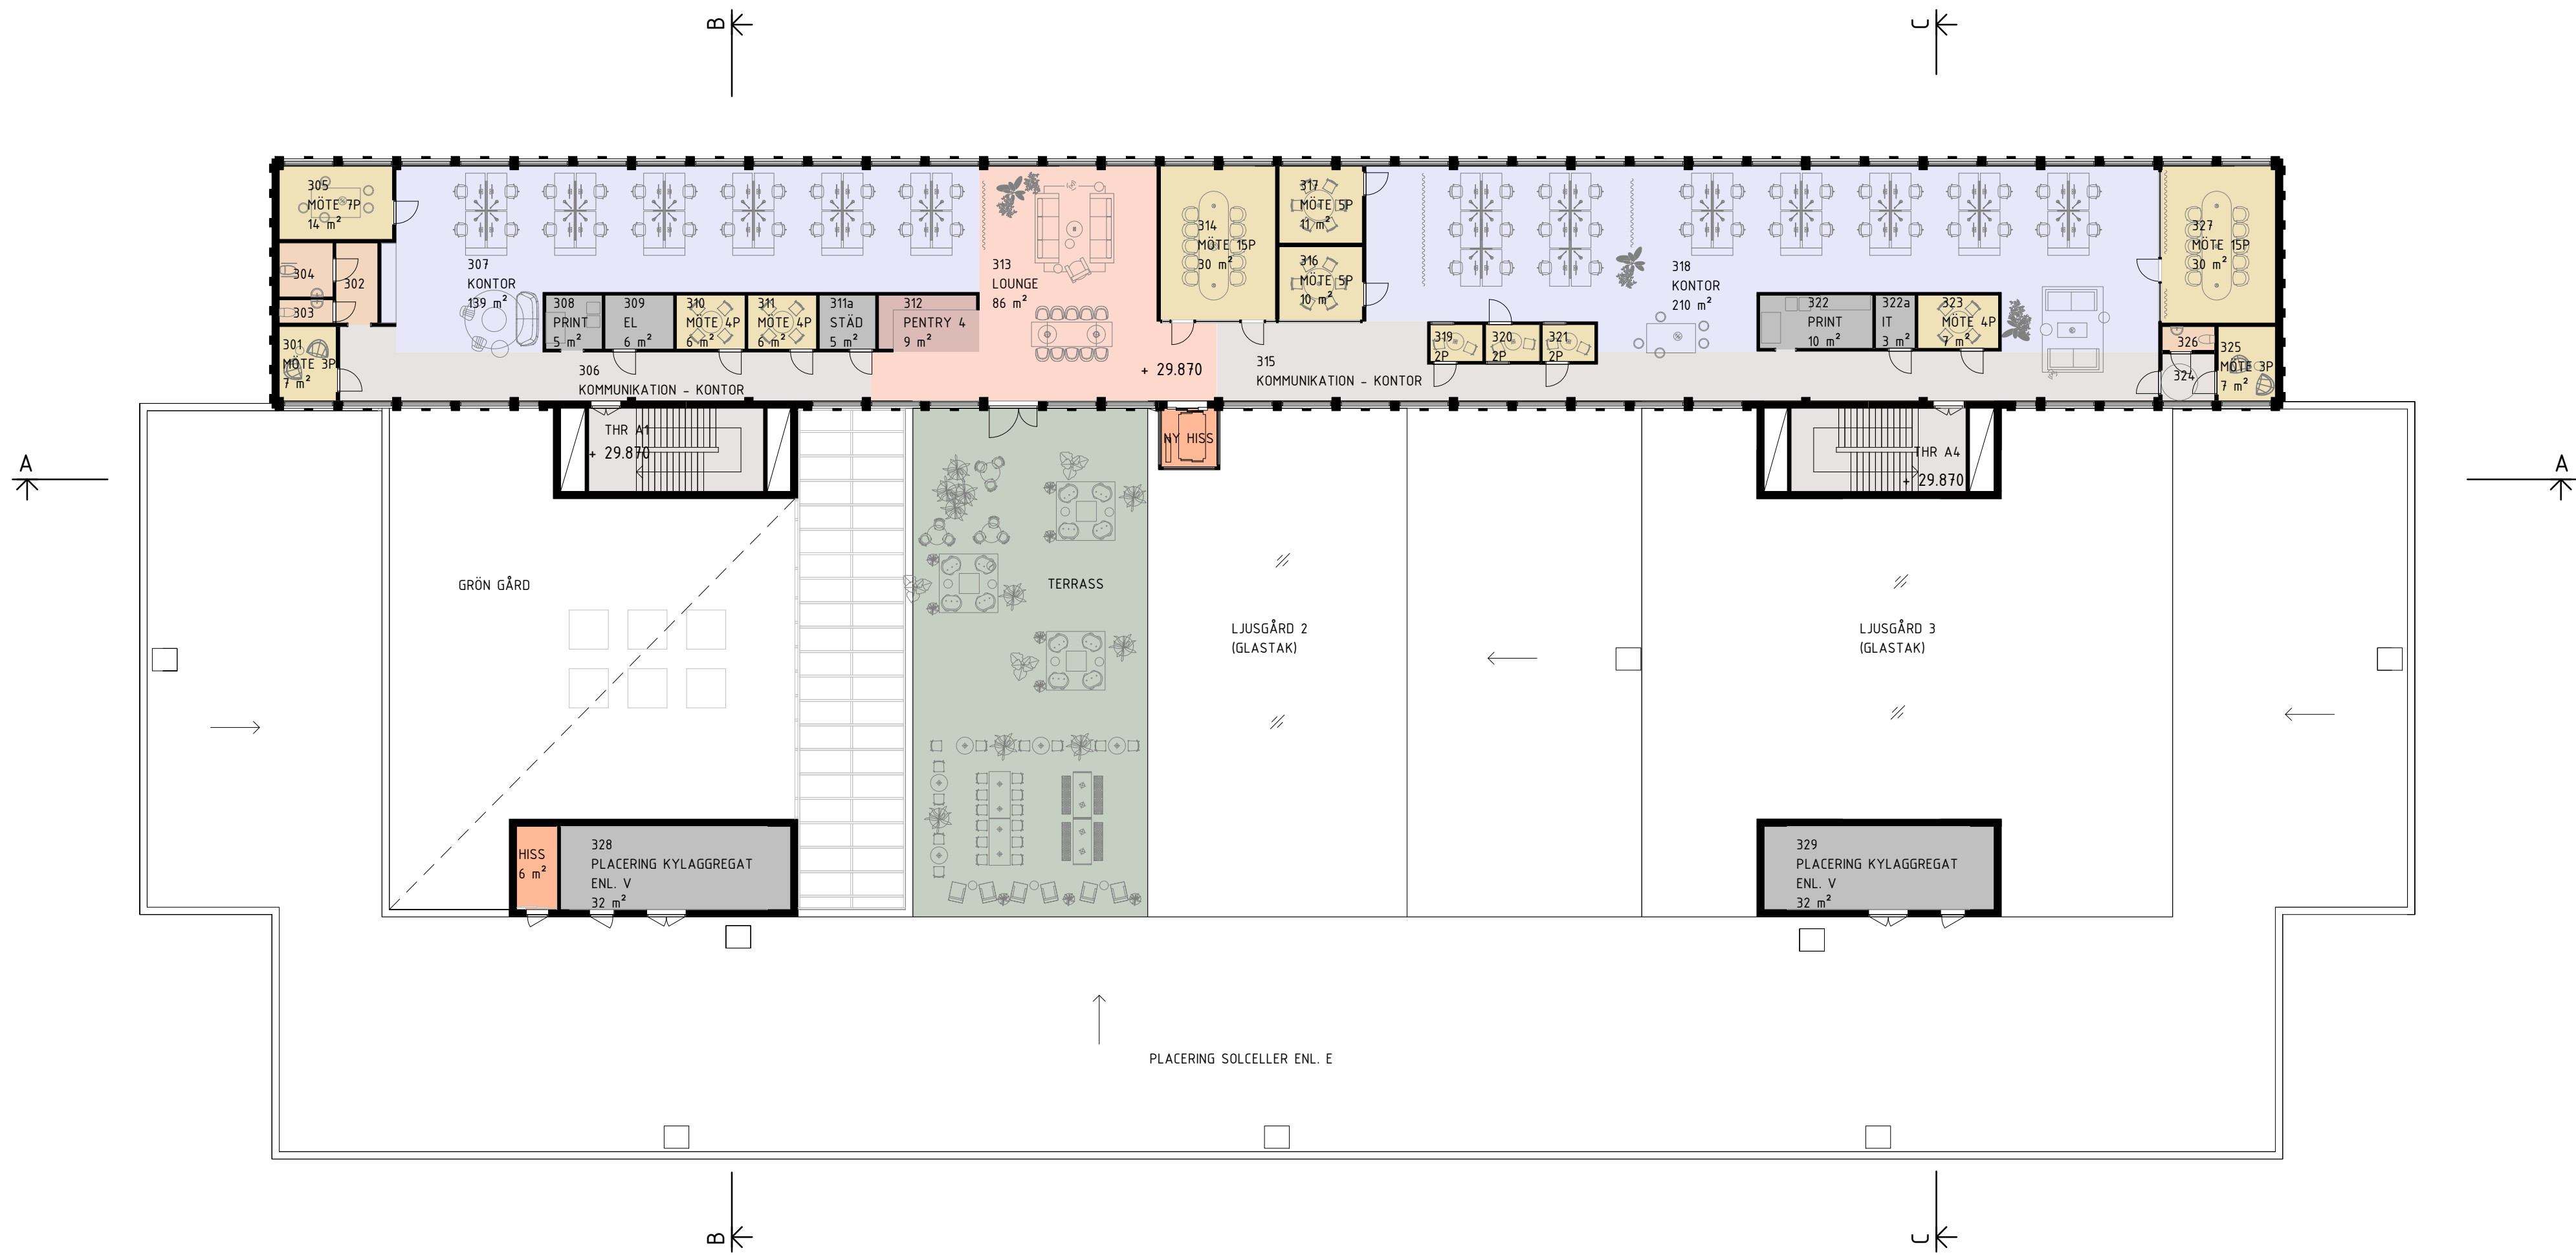

FÖRKLARINGAR


SE A-40-1-001

FÖRESKRIFTER



SE A-40-1-001

HÄNVISNINGAR

SE A-40-1-001

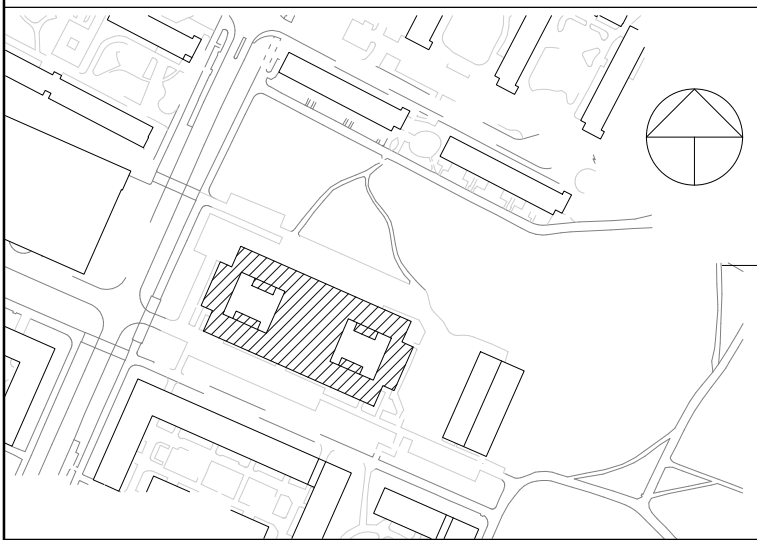

BET	ANT	ÄNDRINGEN AVSER	DATUM	SIGN
PROGRAMHANDLING				
FASTIGHET: KÄMPINGE 2:1				
BYGGNAD: A				
HUS.NR: -				
PLAN: 12		SEKRETESS:		
Henning Larsen				
 Stockholms stad				
B FASTIGHETSKONTORET		Tel: 08-508 270 00		
P WSP		Tel: 070-275 08 96		
A HENNING LARSEN		Tel: 070-574 61 43		
K NORCONSULT		Tel: 079-142 89 57		
V SAMCONSULT		Tel: 070-278 06 29		
PROJEKT NR 74320		RITADYKONSTR. AV SE/JK/AS		ANLÄGGNINGSNUMMER 0260
DATUM 20250124		ANSVARIG M. WAHLGREN		DISCIPLIN A
JÄRVA SDF				
SAMMANSATT REDOVISNING				
PLAN 12				
SKALA A1 1:200 A3 1:400		RITNINGSNAMN A-40-1-004		BET

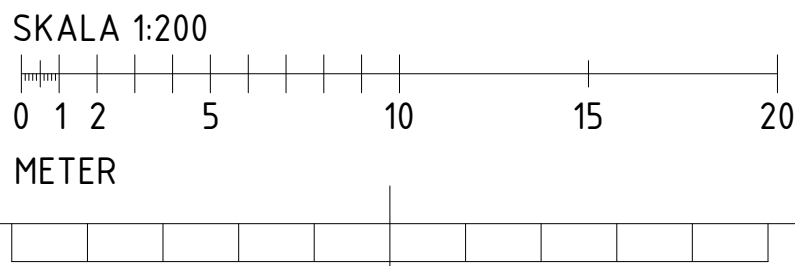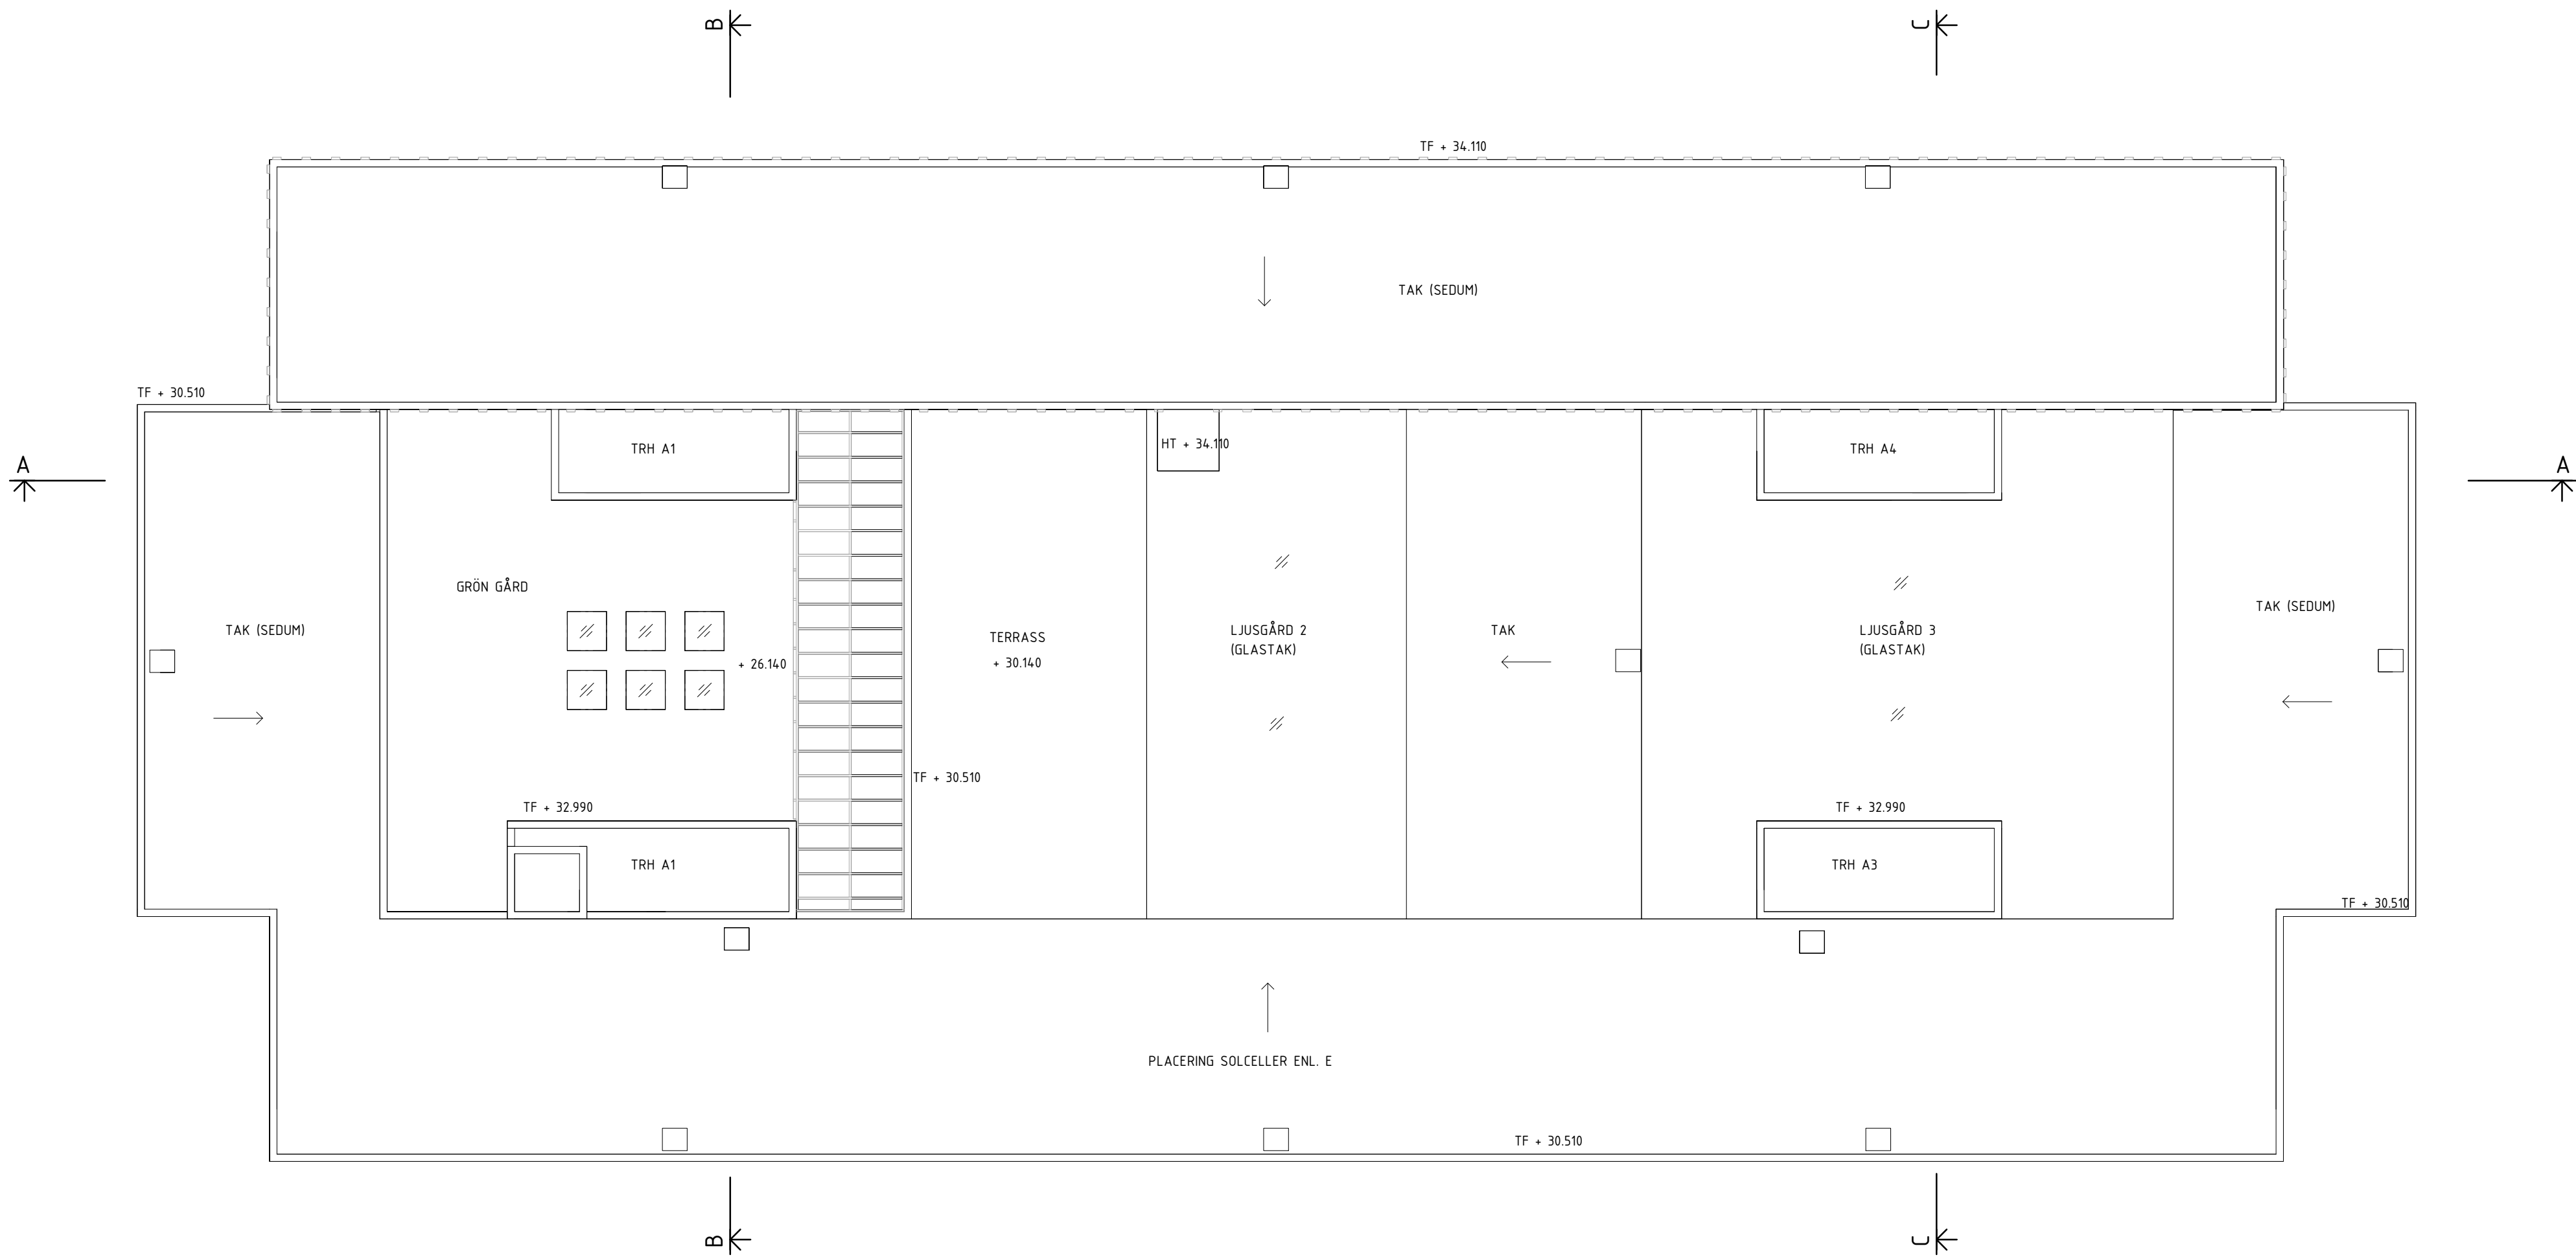

FÖRKLARINGAR


SE A-40-1-001

FÖRESKRIFTER

SE A-40-1-001

HÄNVISNINGAR

SE A-40-1-001

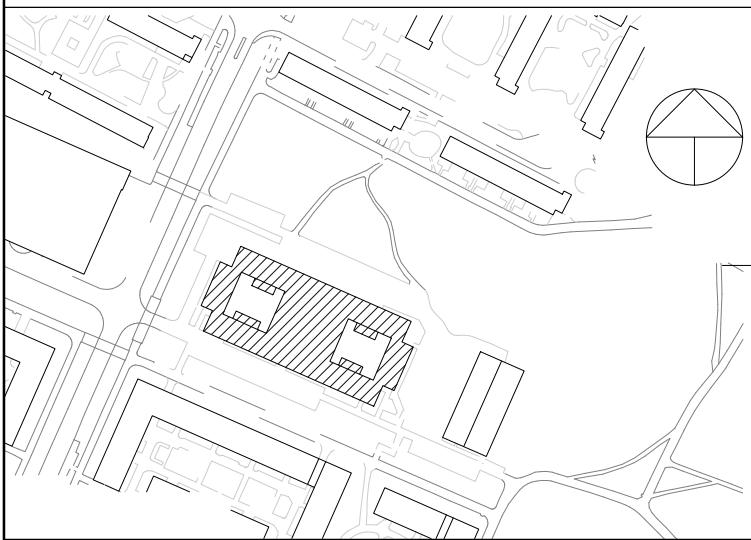

BET	ANT	ÄNDRINGEN AVSER	DATUM	SIGN
-----	-----	-----------------	-------	------

PROGRAMHANDLING

FASTIGHET: KÄMPINGE 2:1

BYGGNAD: A

HUS.NR: -

PLAN: 13

SEKRETESS:

**Henning
Larsen**




B	FASTIGHETSKONTORET	Tel: 08-508 270 00
P	WSP	Tel: 070-275 08 96
X	A HENNING LARSEN	Tel: 070-574 61 43
K	NORCONSULT	Tel: 079-142 89 57
V	SAMKONSULT	Tel: 070-278 06 29


PROJEKT NR	RITADYKONSTR. AV	ANLÄGGNINGSNUMMER
74320	SE/JK/AS	0260
DATUM	ANSVARIG	DISCIPLIN
20250124	M. WAHLGREN	A

JÄRVA SDF
SAMMANSATT REDOVISNING
PLAN 13 TAKPLAN


SKALA	RITNINGSNAMN	BET
A1 1:200 A3 1:400	A-40-1-005	

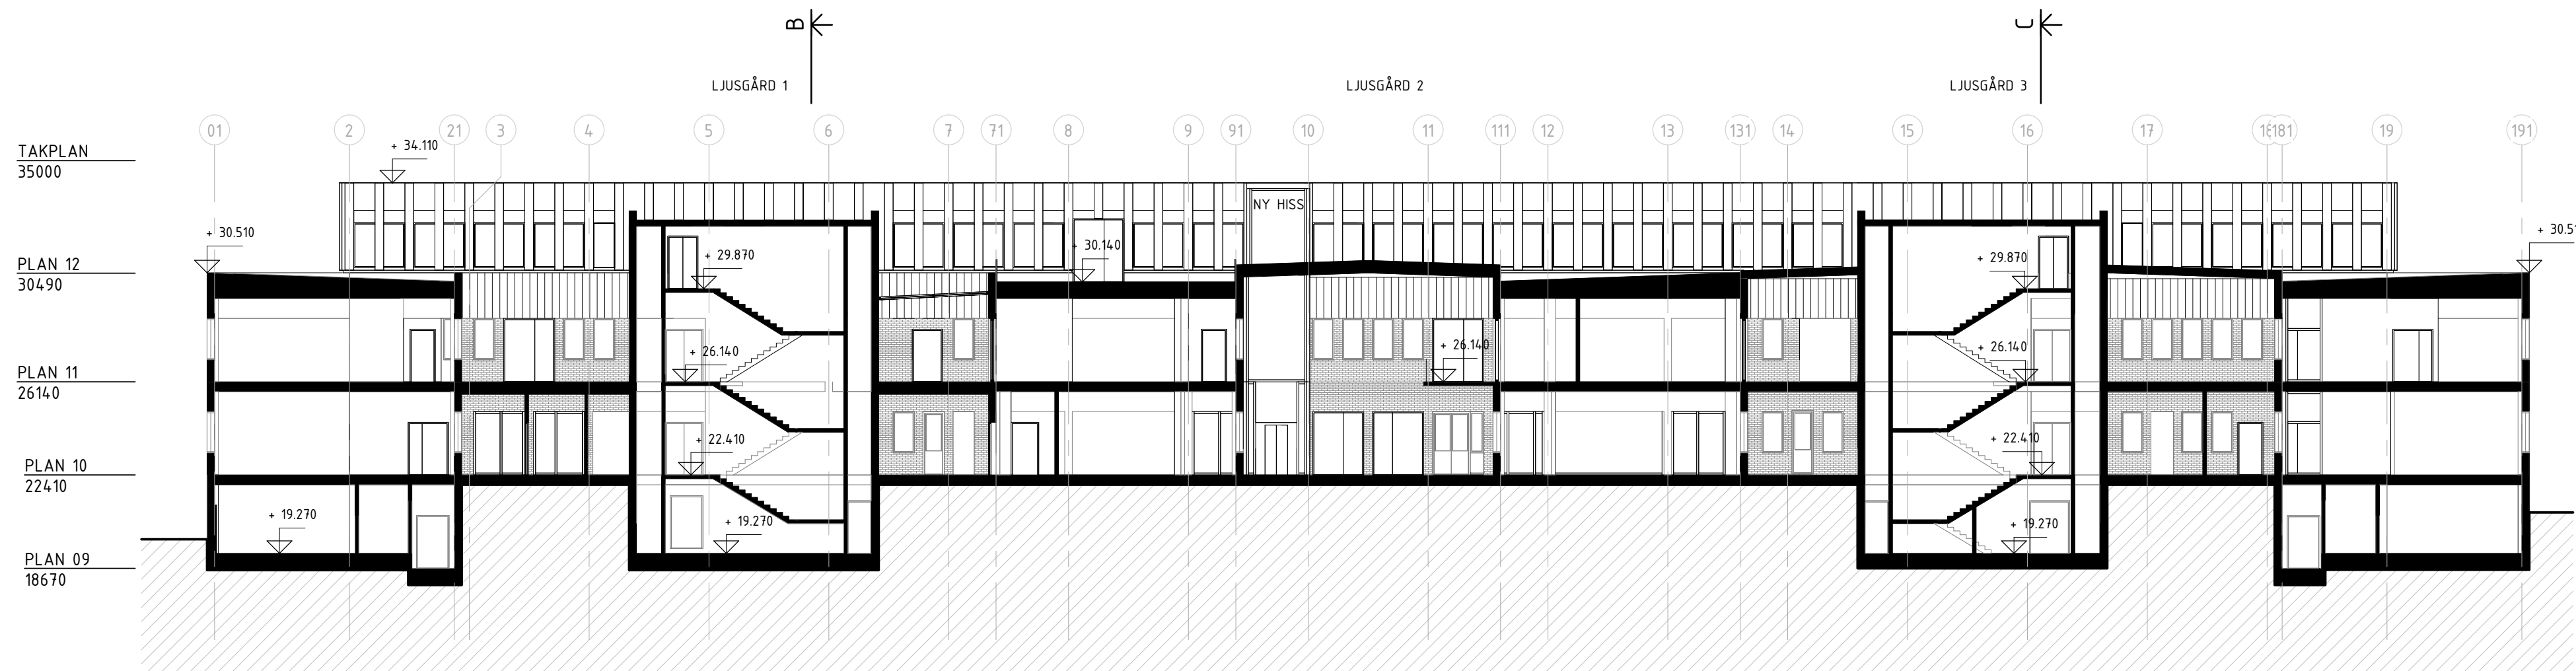


SEKTION A-A

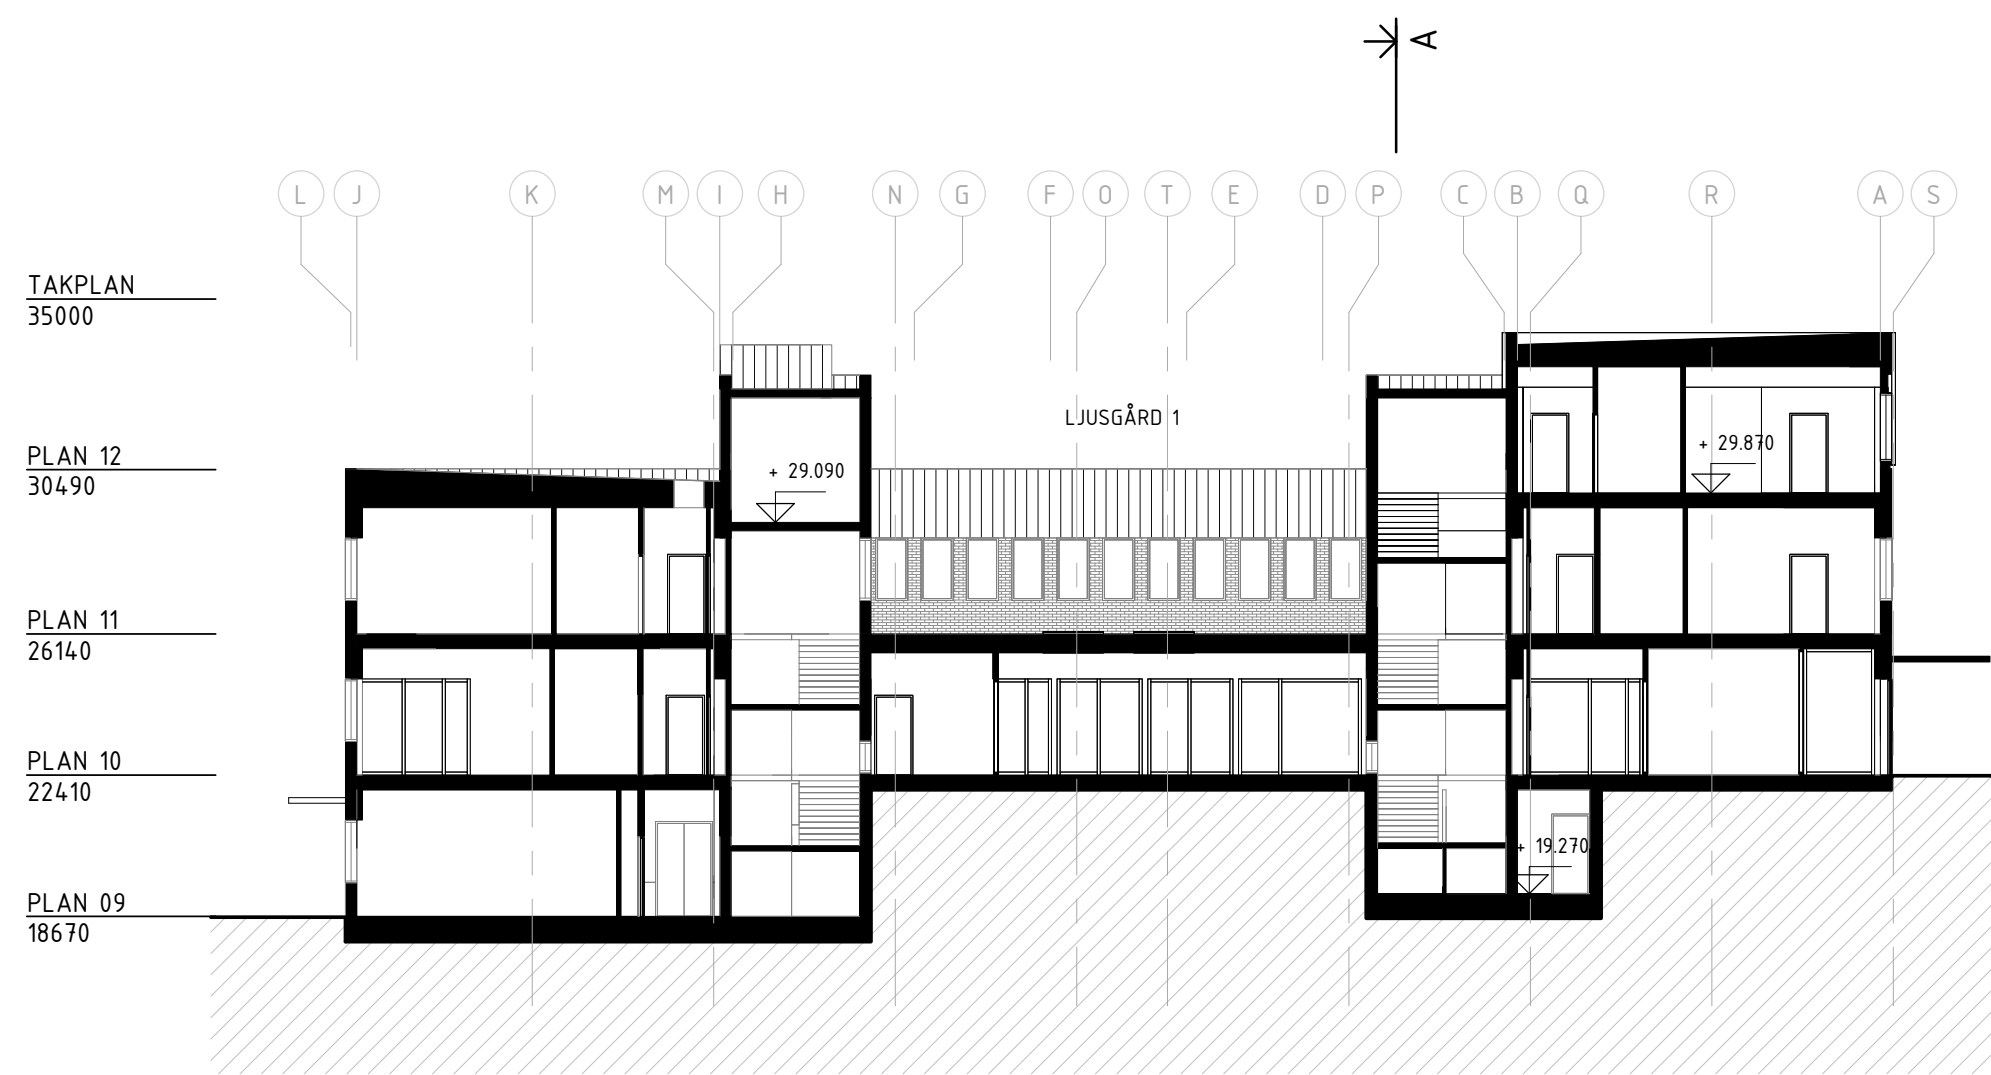

SEKTION B-B

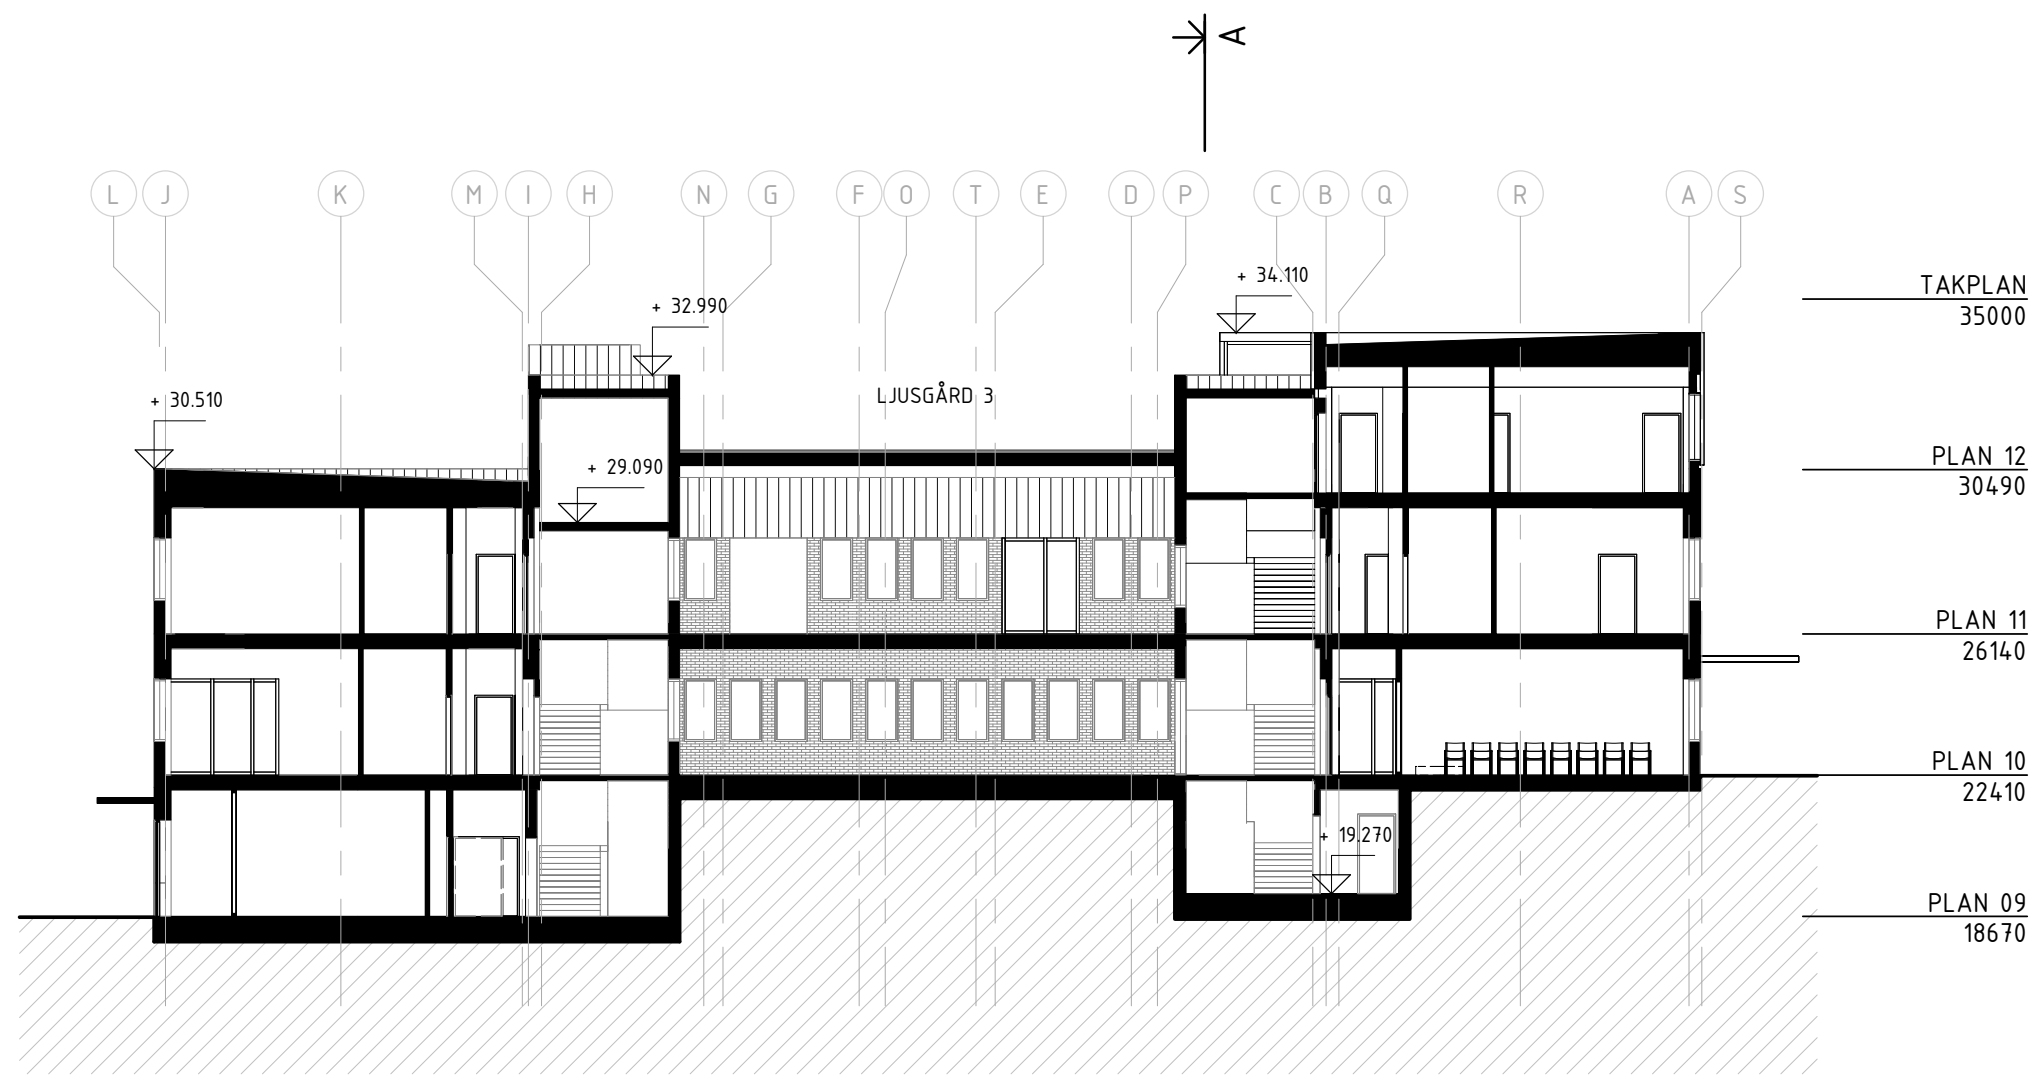

SEKTION C-C

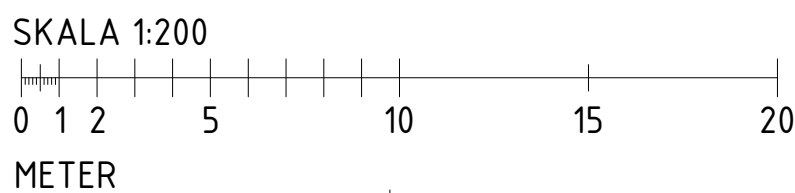

FÖRKLARINGAR

MÅTT ANGES I MILLIMETER.
PLUSHÖJDER ANGES I METER ENLIGT HÖJDSYSTEM RH2000.


RITNINGAR UPPRÄTTADE EFTER TIDIGARE UNDERLAG. BEFINTLIGA
RITNINGAR OCH RELATIONSHANDLINGAR.

FÖRESKRIFTER

-

HÄNVISNINGAR

A-00-X-XXX-SERIE BEFINTLIGT UTSEENDE
A-40-1-XXX-SERIE PLANER
A-40-3-XXX-SERIE FASADER
RUMSFUNKTIONSPROGRAM
GESTALTNINGSPROGRAM

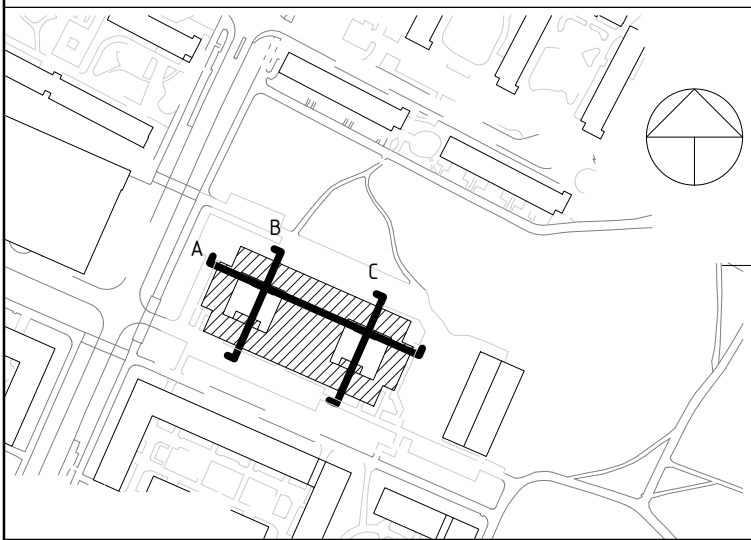

BET	ANT	ÄNDRINGEN AVSER	DATUM	SIGN
-----	-----	-----------------	-------	------

PROGRAMHANDLING

FASTIGHET: KÄMPINGE 2:1

BYGGNAD: A

HUS.NR: -

PLAN: -

SEKRETESS:

**Henning
Larsen**




B	FASTIGHETSKONTORET	Tel: 08-508 270 00
P	WSP	Tel: 070-275 08 96
X	A HENNING LARSEN	Tel: 070-574 61 43
K	NORCONSULT	Tel: 079-142 89 57
V	SAMKONSULT	Tel: 070-278 06 29

PROJEKT NR	RITADYKONSTR. AV	ANLÄGGNINGSNUMMER
74320	SE/JK/AS	0260
DATUM	ANSVARIG	DISCIPLIN
20250124	M. WAHLGREN	A


JÄRVA SDF
SAMMANSATT REDOVISNING
SEKTIONER

SKALA	RITNINGSNAMN	BET
A1 1:100 A3 1:200	A-40-2-001	


C:\Users\JAHMSE\OneDrive - Ramboll\Documents\0260-A-40-V-0000_barina_kaim.rvt
2025-01-24 15:21:51

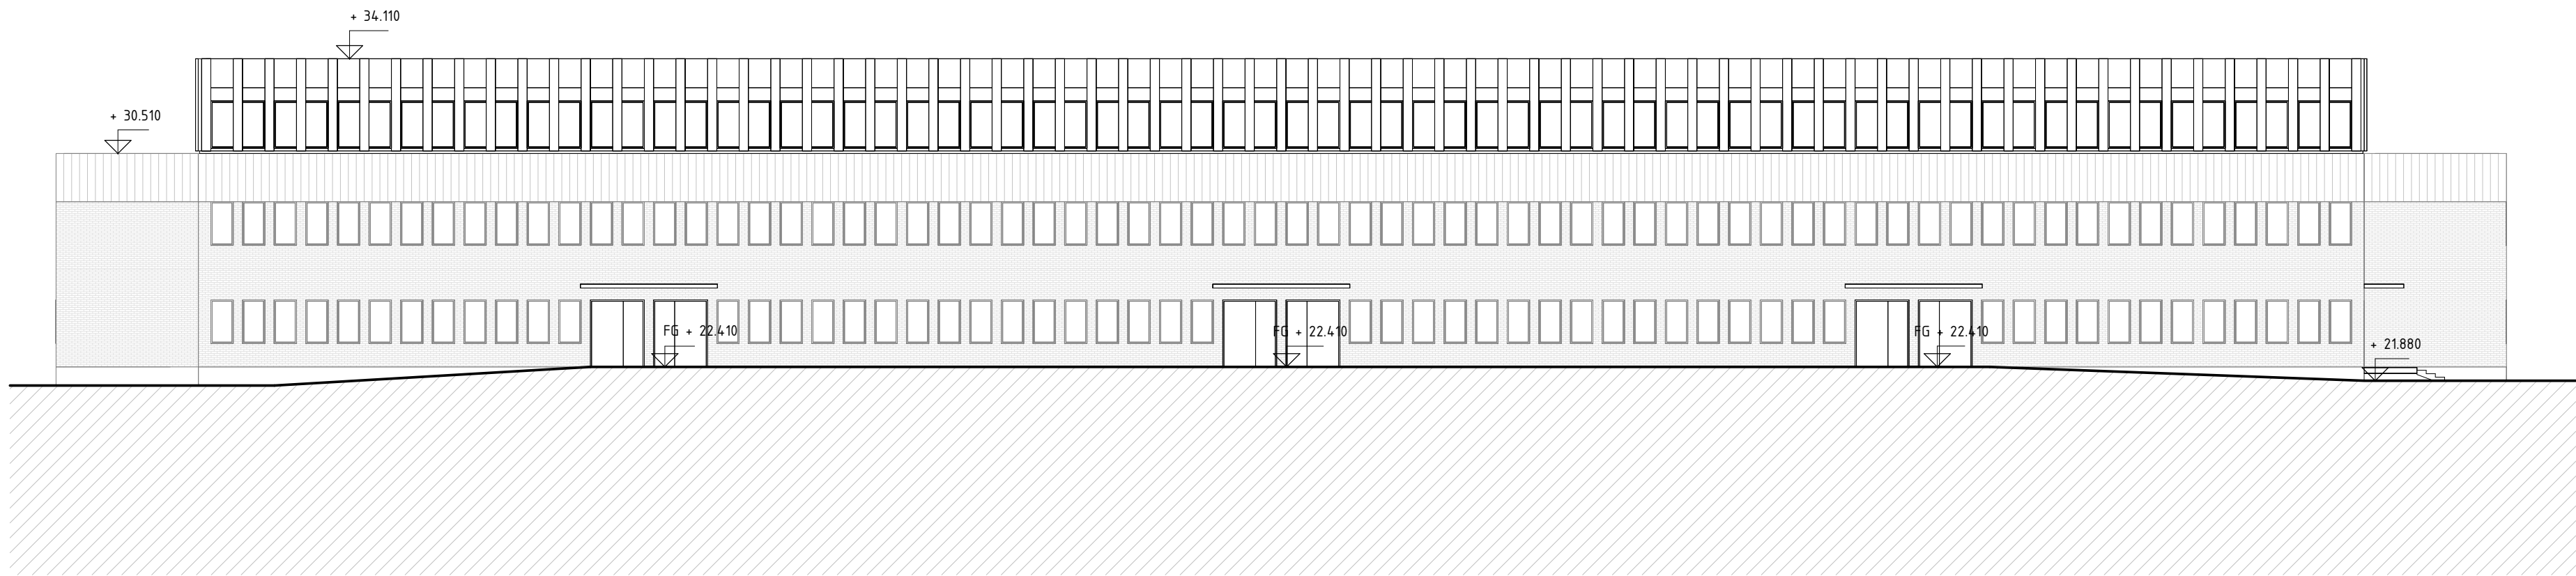


1 - FASAD MOT NORR

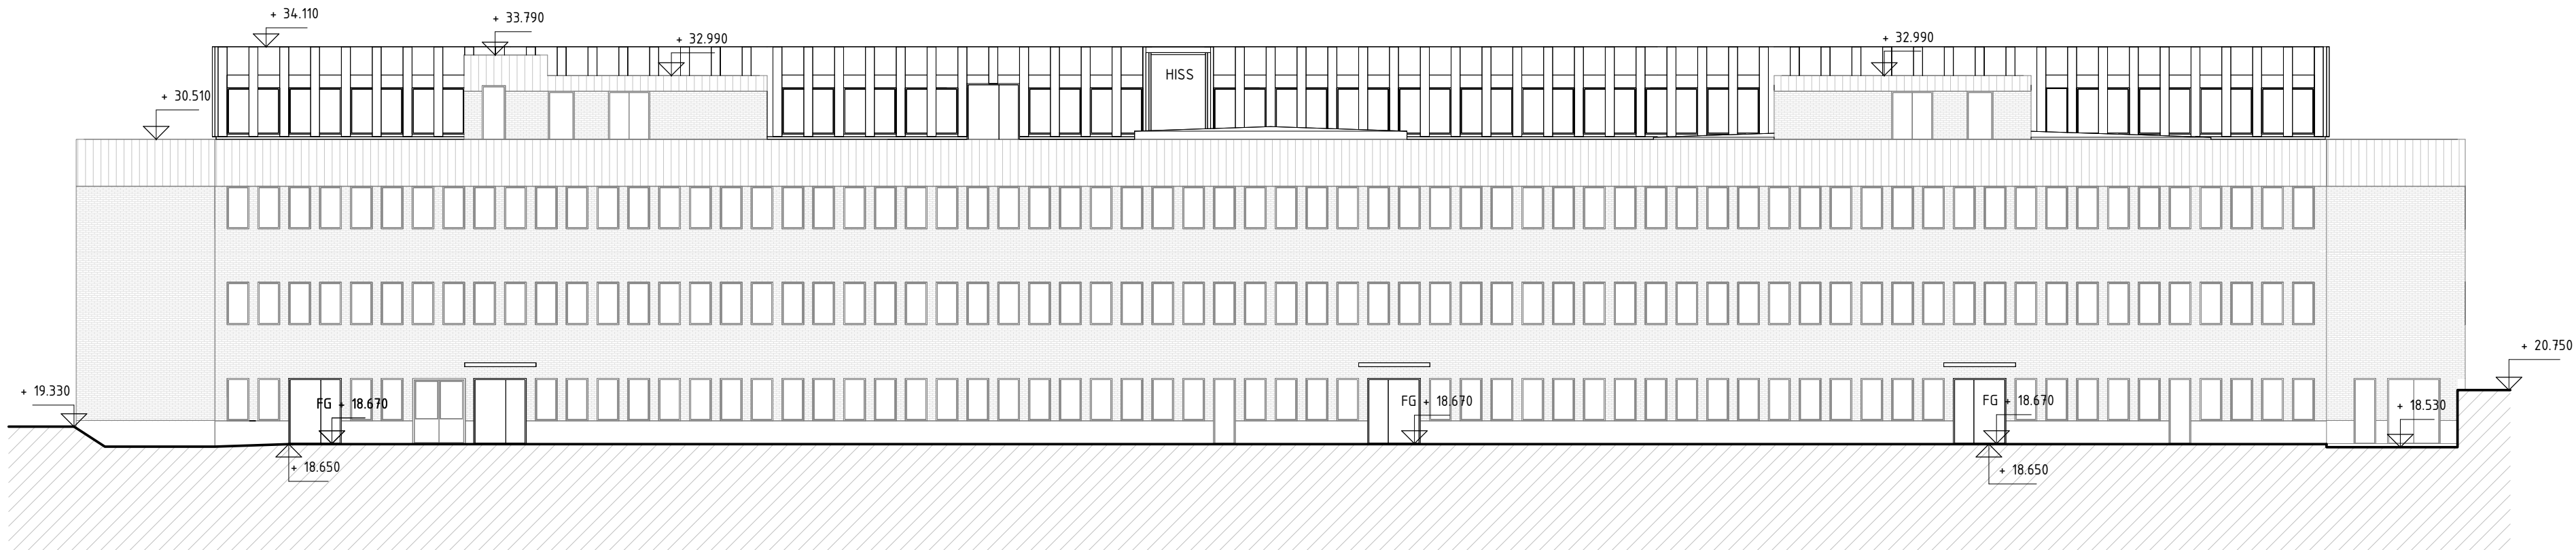


2 - FASAD MOT SÖDER

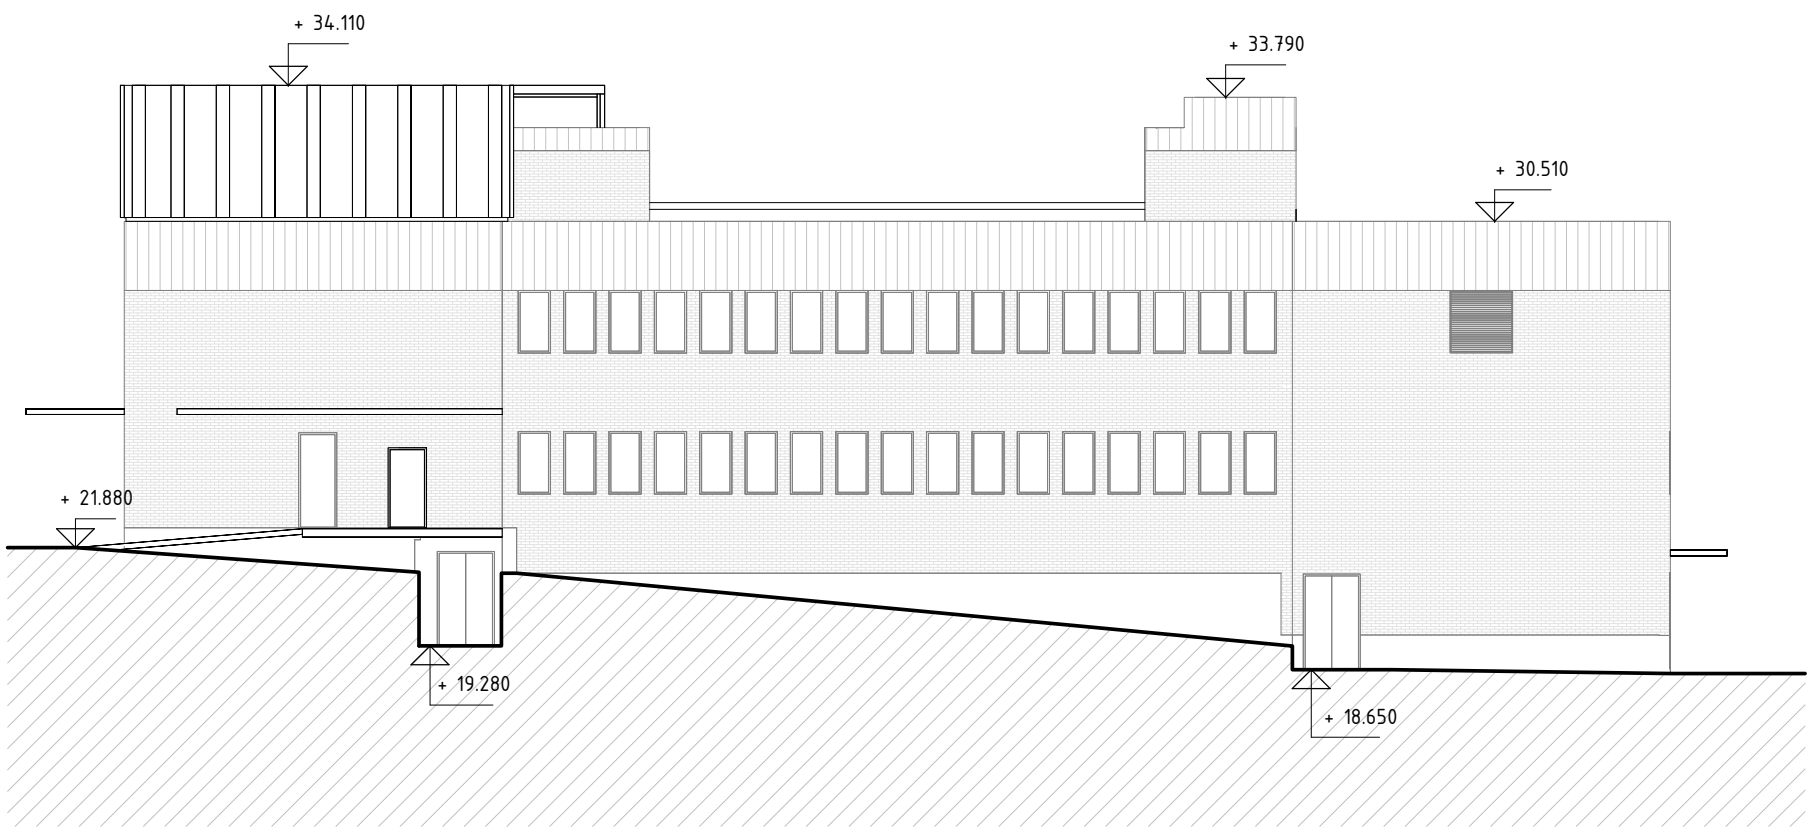

3 - FASAD MOT VÄSTER

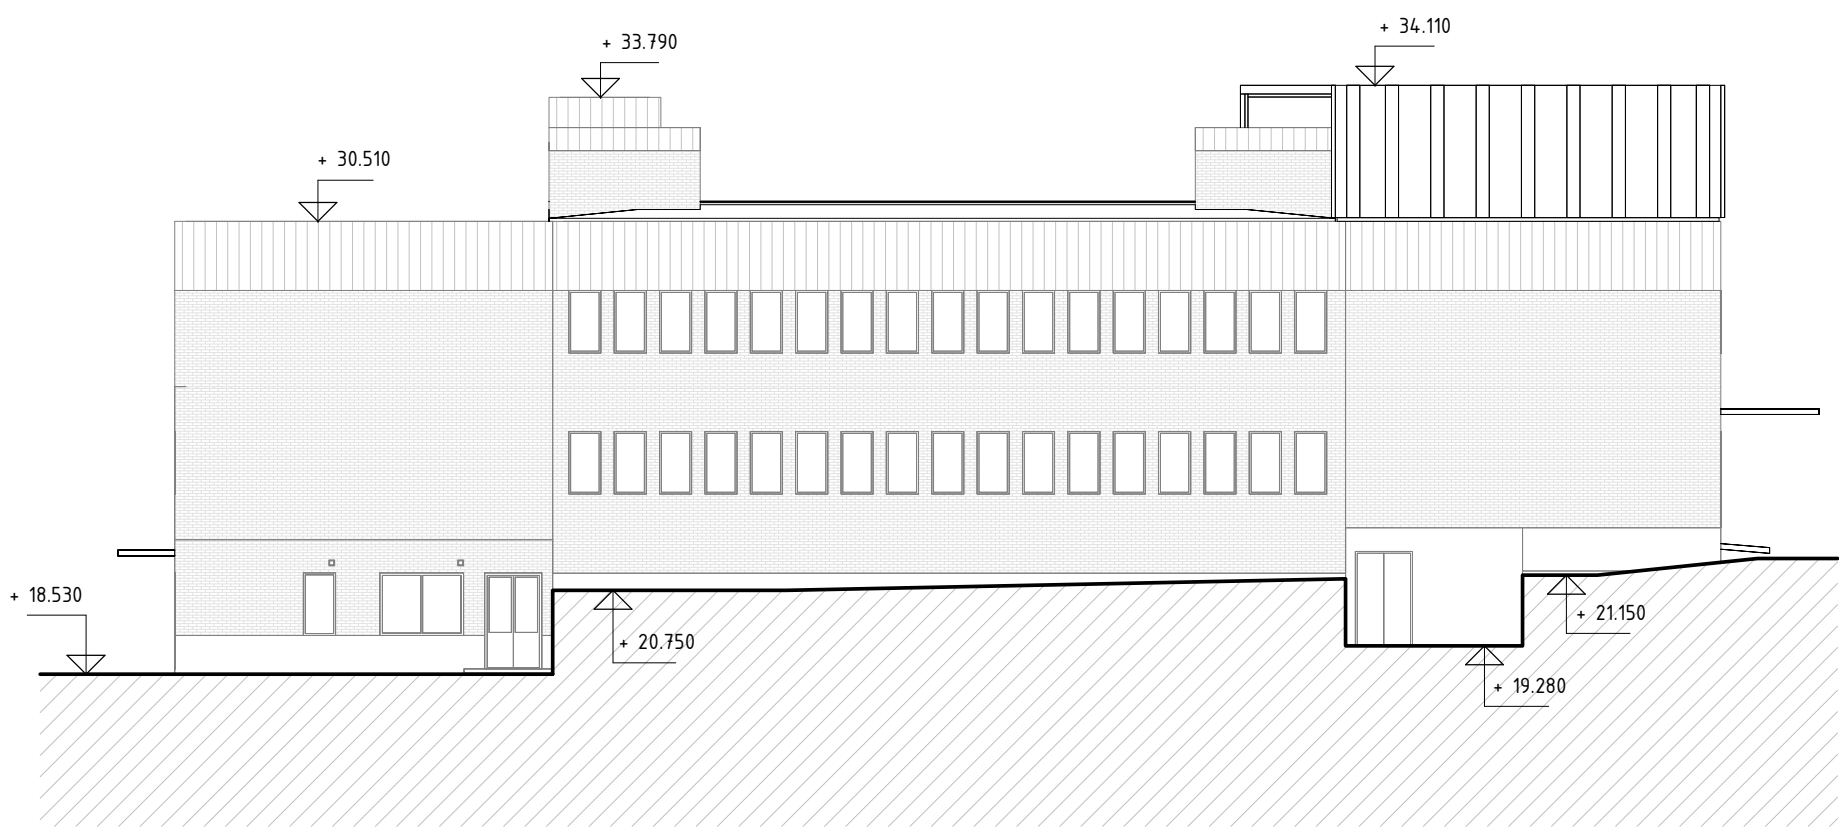

4 - FASAD MOT ÖSTER

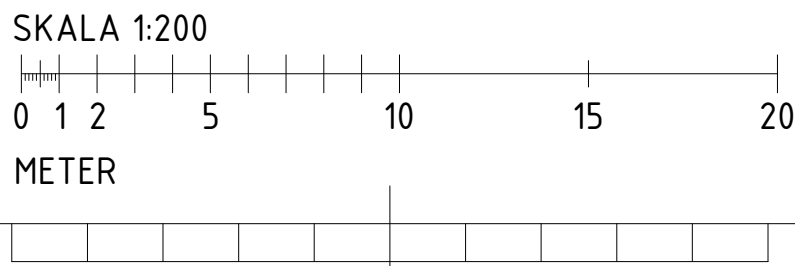


FÖRKLARINGAR

MÅTT ANGES I MILLIMETER.
PLUSHÖJDER ANGES I METER ENLIGT HÖJDSYSTEM RH2000.
RITNINGAR UPPRÄTTADE EFTER TIDIGARE UNDERLAG. BEFINTLIGA
RITNINGAR OCH RELATIONSHANDLINGAR.

FÖRESKRIFTER

HÄNVISNINGAR

A-00-X-XXX-SERIE BEFINTLIGT UTSEENDE
A-40-1-XXX-SERIE PLANER
A-40-2-XXX-SERIE SEKTIONER
RUMSFUNKTIONSPROGRAM
GESTALTNINGSPROGRAM

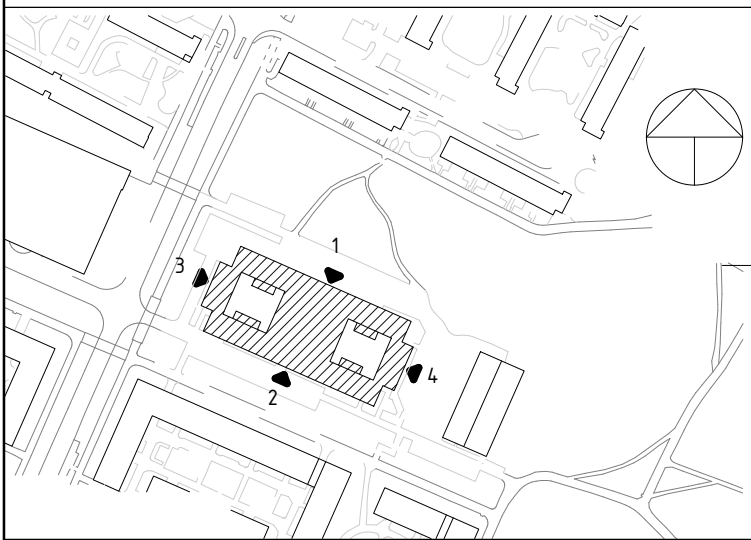

BET	ANT	ÄNDRINGEN AVSER	DATUM	SIGN
-----	-----	-----------------	-------	------

PROGRAMHANDLING

FASTIGHET: KÄMPINGE 2:1
BYGGNAD: A
HUS.NR: -
PLAN: -

SEKRETESS:

**Henning
Larsen**




**Stockholms
stad**

B	FASTIGHETSKONTORET	Tel: 08-508 270 00
P	WSP	Tel: 070-275 08 96
X	A HENNING LARSEN	Tel: 070-574 61 43
K	NORCONSULT	Tel: 079-142 89 57
V	SAMKONSULT	Tel: 070-278 06 29


PROJEKT NR	RITADYKONSTR. AV	ANLÄGGNINGSNUMMER
74320	SE/JK/AS	0260
DATUM	ANSVARIG	DISCIPLIN
20250124	M. WAHLGREN	A

JÄRVA SDF
SAMMANSATT REDOVISNING
FASADER


SKALA	RITNINGSNAMN	BET
A1 1:200 A3 1:400	A-40-3-001	

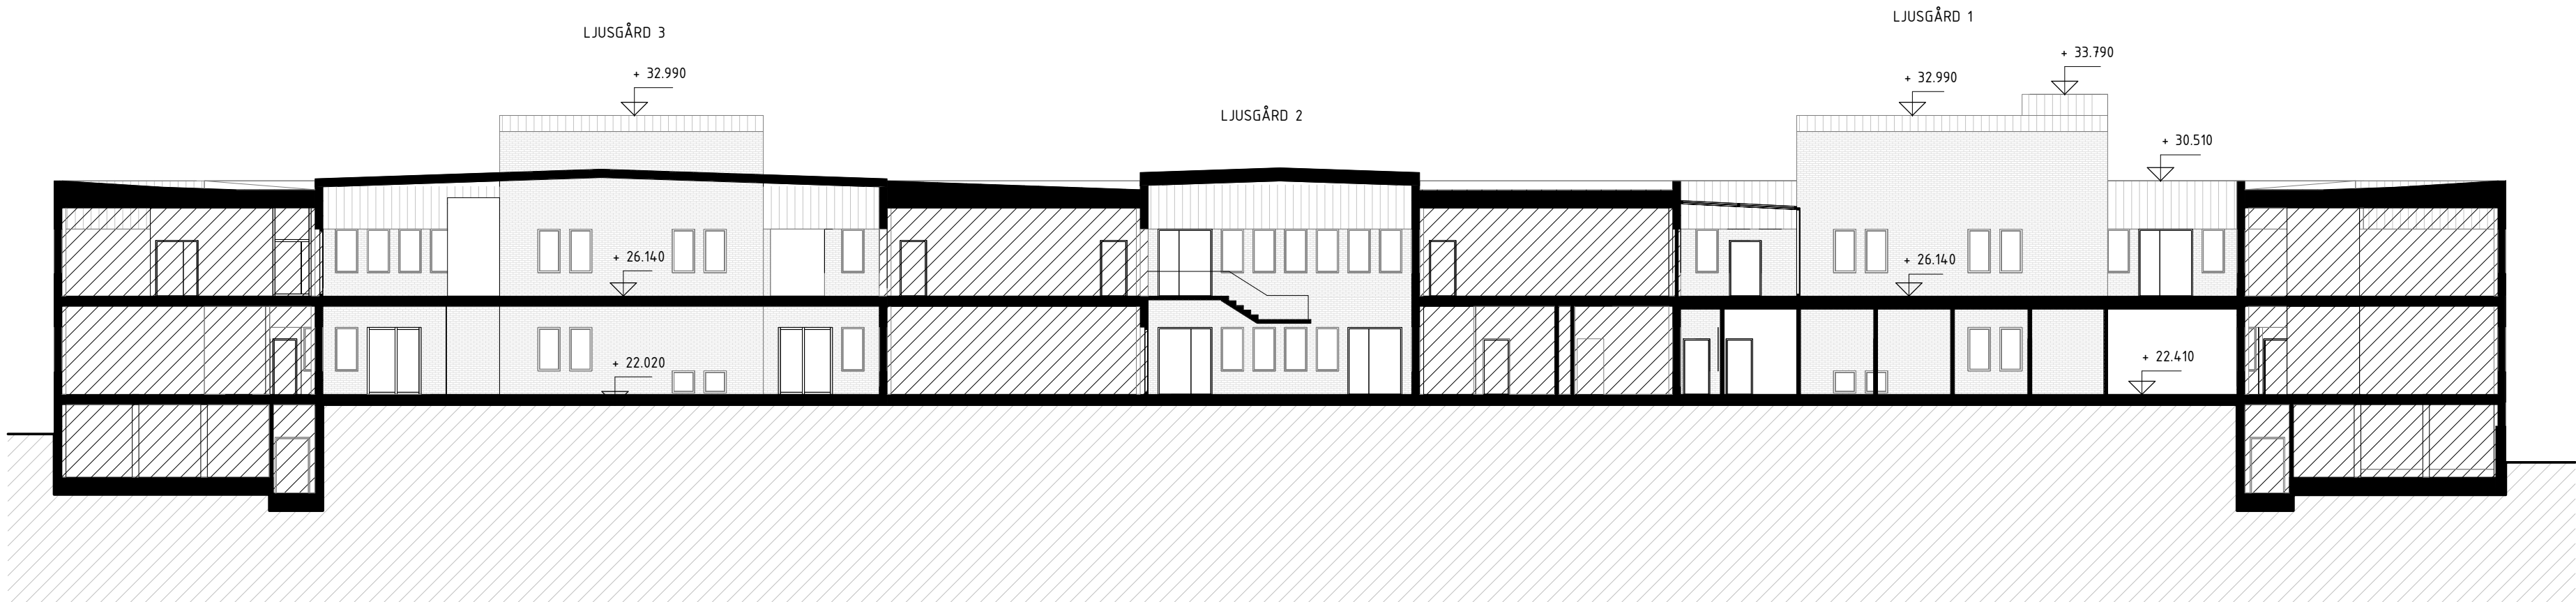


5 - FASAD MOT NORR, LJUSGÅRD 1, 2, 3

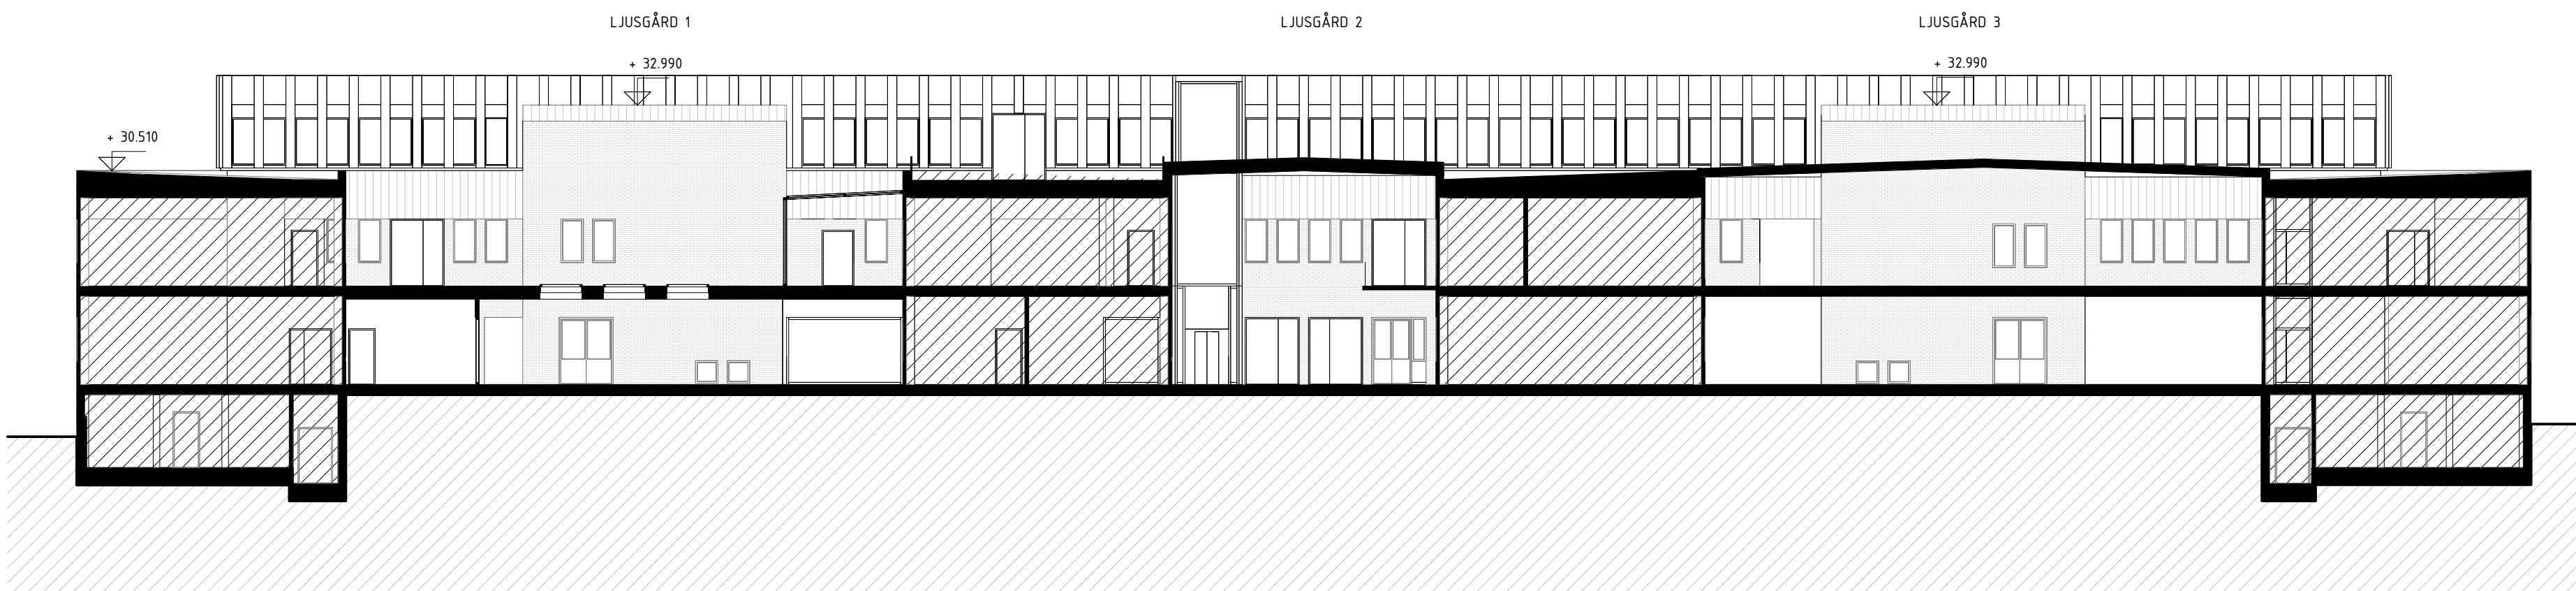


6 - FASAD MOT SÖDER, LJUSGÅRD 1, 2, 3

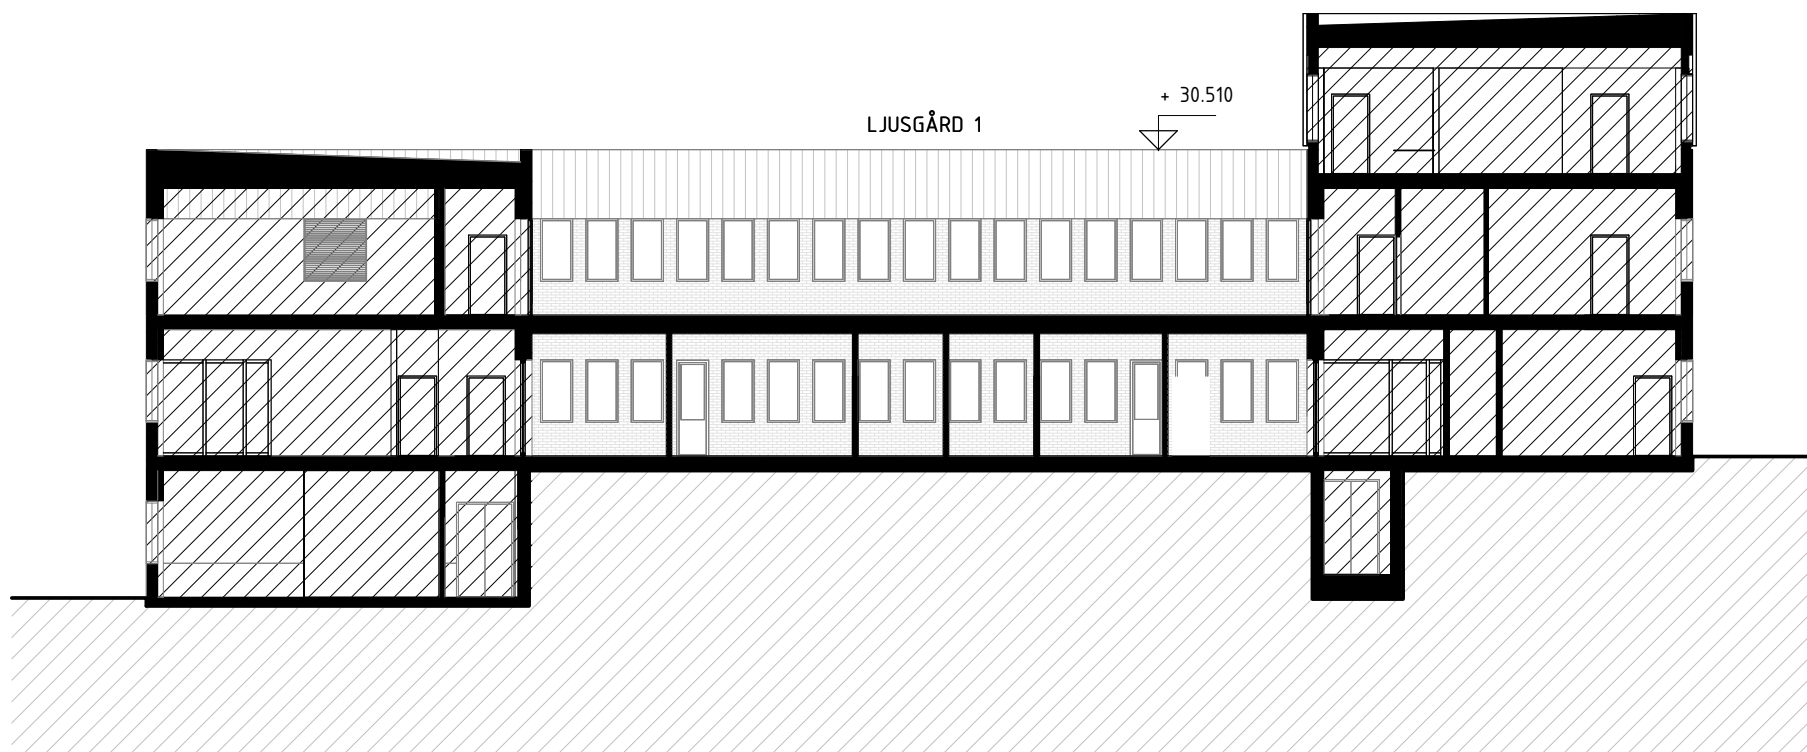


7 - FASAD MOT ÖSTER, LJUSGÅRD 1

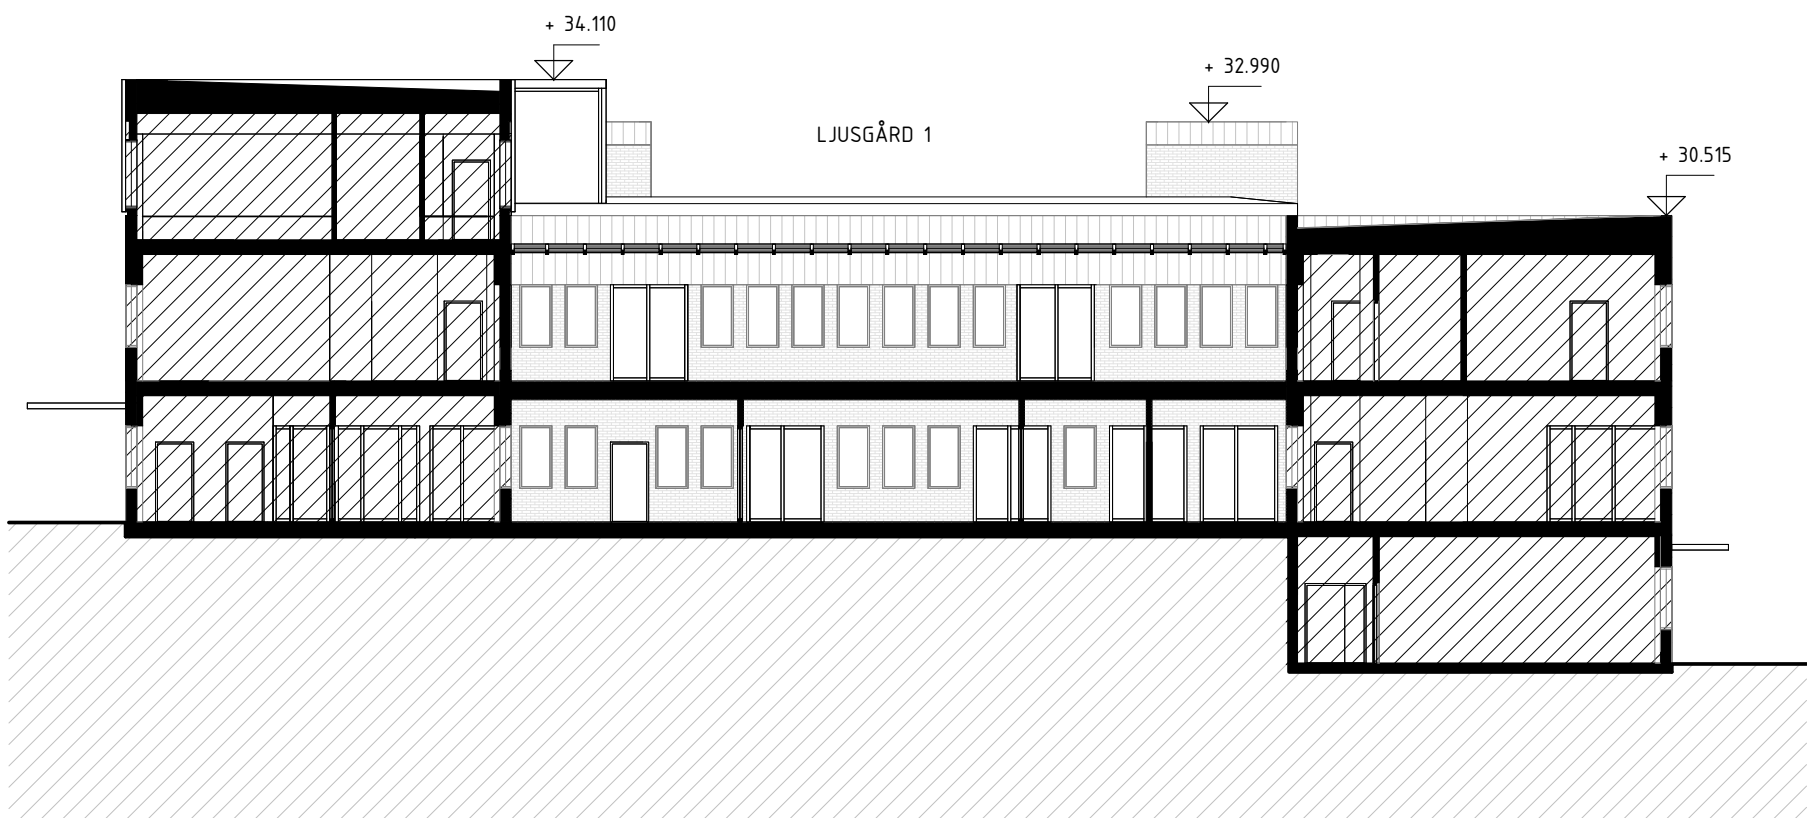


8 - FASAD MOT VÄSTER, LJUSGÅRD 1

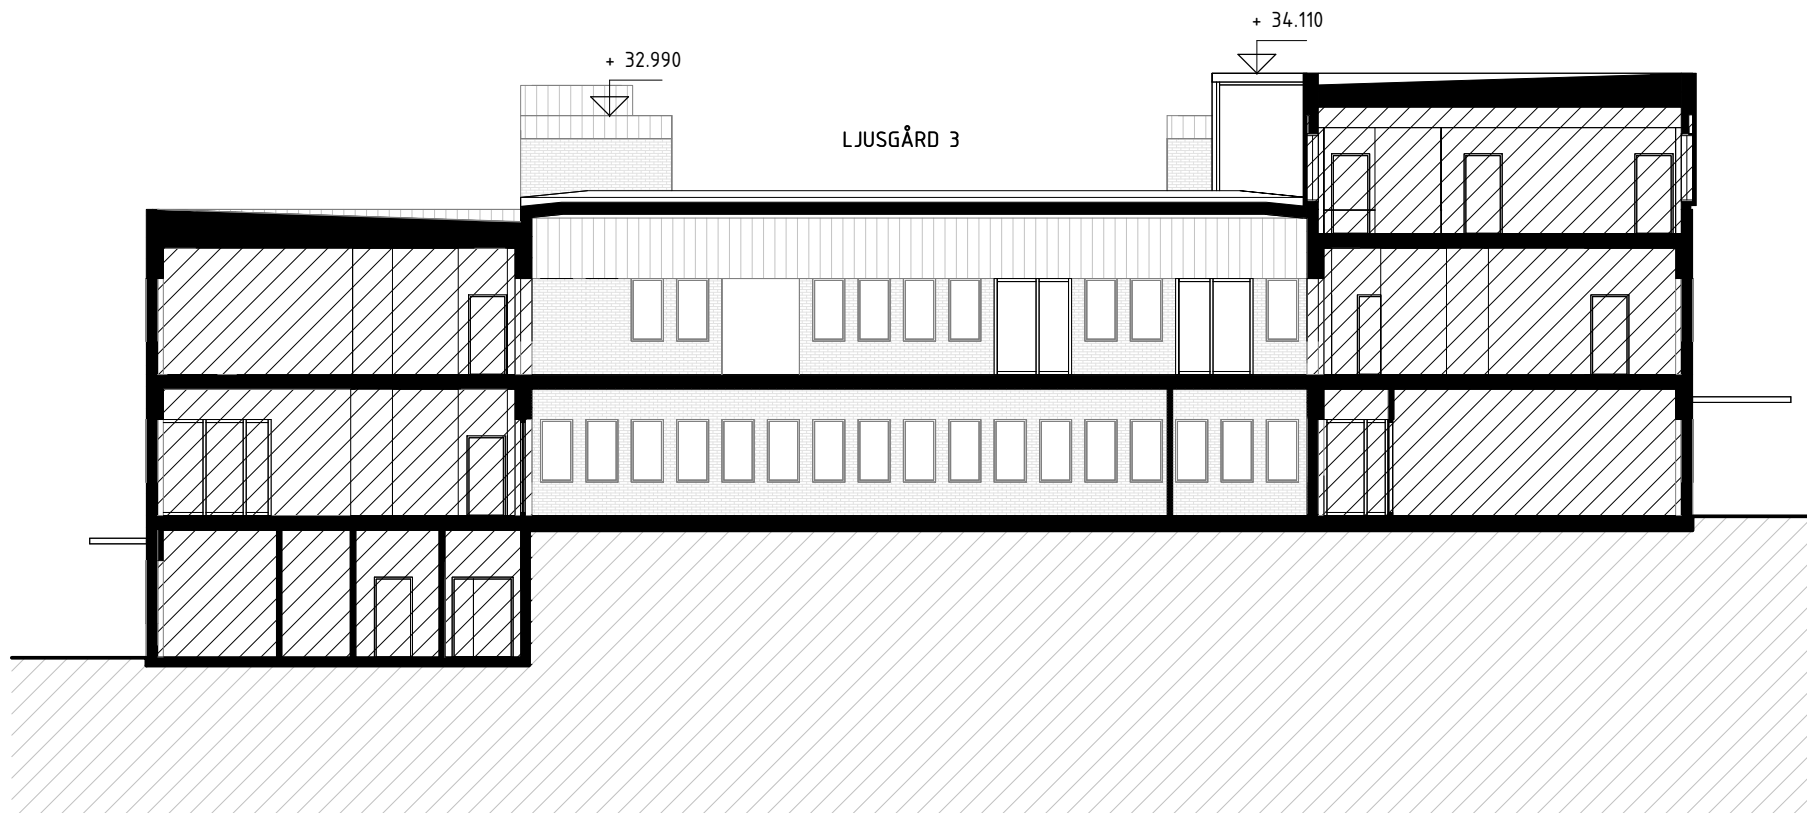

9 - FASAD MOT ÖSTER, LJUSGÅRD 3

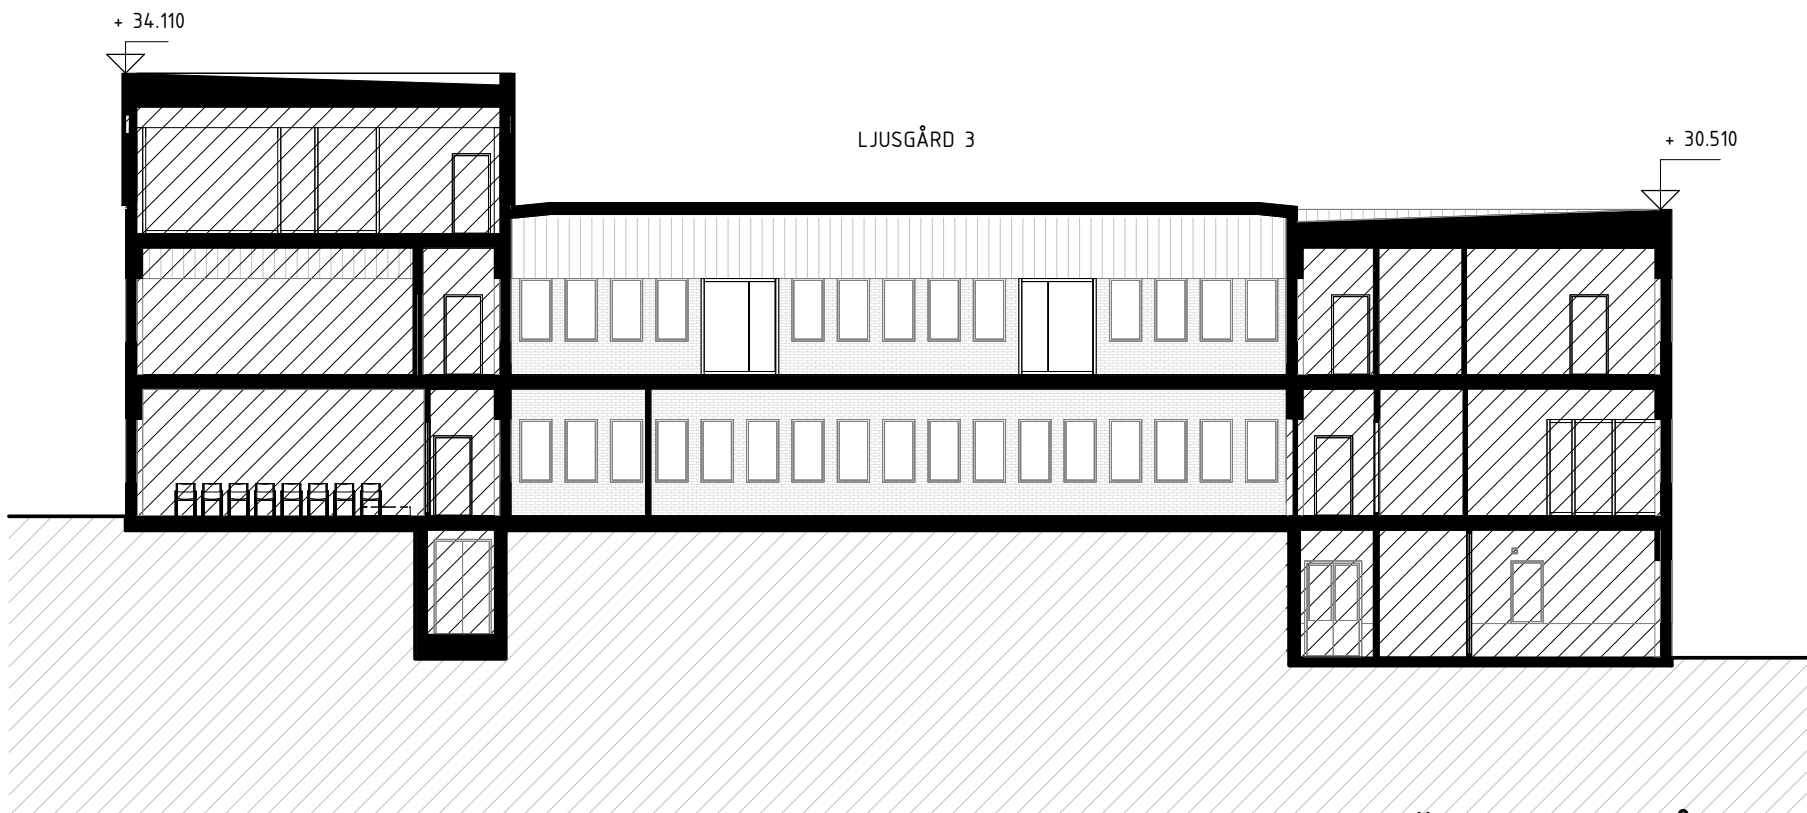

10 - FASAD MOT VÄSTER, LJUSGÅRD 3

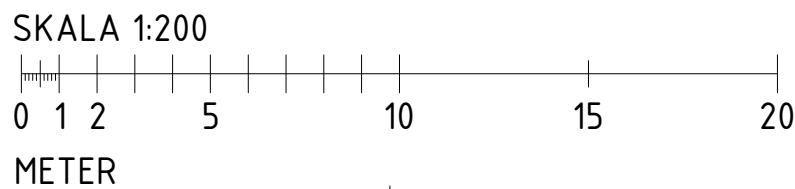

FÖRKLARINGAR


SE A-40-3-001

FÖRESKRIFTER

SE A-40-3-001

HÄNVISNINGAR

SE A-40-3-001

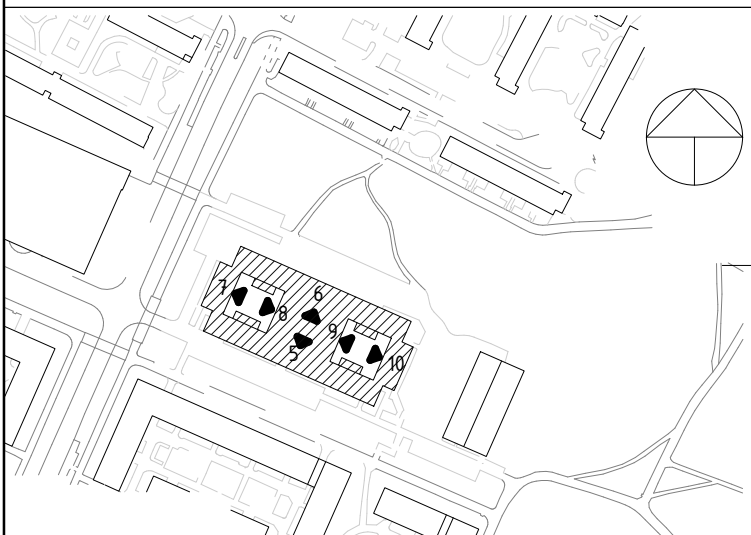

BET	ANT	ÄNDRINGEN AVSER	DATUM	SIGN
-----	-----	-----------------	-------	------

PROGRAMHANDLING

FASTIGHET: KÄMPINGE 2:1
BYGGNAD: A
HUS.NR: -
PLAN: -

SEKRETESS:

Henning
Larsen



B	FASTIGHETSKONTORET	Tel: 08-508 270 00
P	WSP	Tel: 070-275 08 96
A	HENNING LARSEN	Tel: 070-574 61 43
K	NORCONSULT	Tel: 079-142 89 57
V	SAMKONSULT	Tel: 070-278 06 29


PROJEKT NR	RITADYKONSTR. AV	ANLÄGGNINGSNUMMER
74320	SE/JK/AS	0260
DATUM	ANSVARIG	DISCIPLIN
20250124	M. WAHLGREN	A

JÄRVA SDF
SAMMANSATT REDOVISNING
FASADER MOT GÅRD


SKALA	RITNINGSNAMN	BET
A1 1:200 A3 1:400	A-40-3-002	

PRELMINÄR AREASAMMANSTÄLLNING.
KAN KOMMA ATT JUSTERAS UNDER PROJEKTERING.


AREASAMMANSTÄLLNING - BTA	
PLAN 09	1538 m ²
PLAN 10	3588 m ²
PLAN 11	3187 m ²
PLAN 12	1006 m ²
	9319 m ²

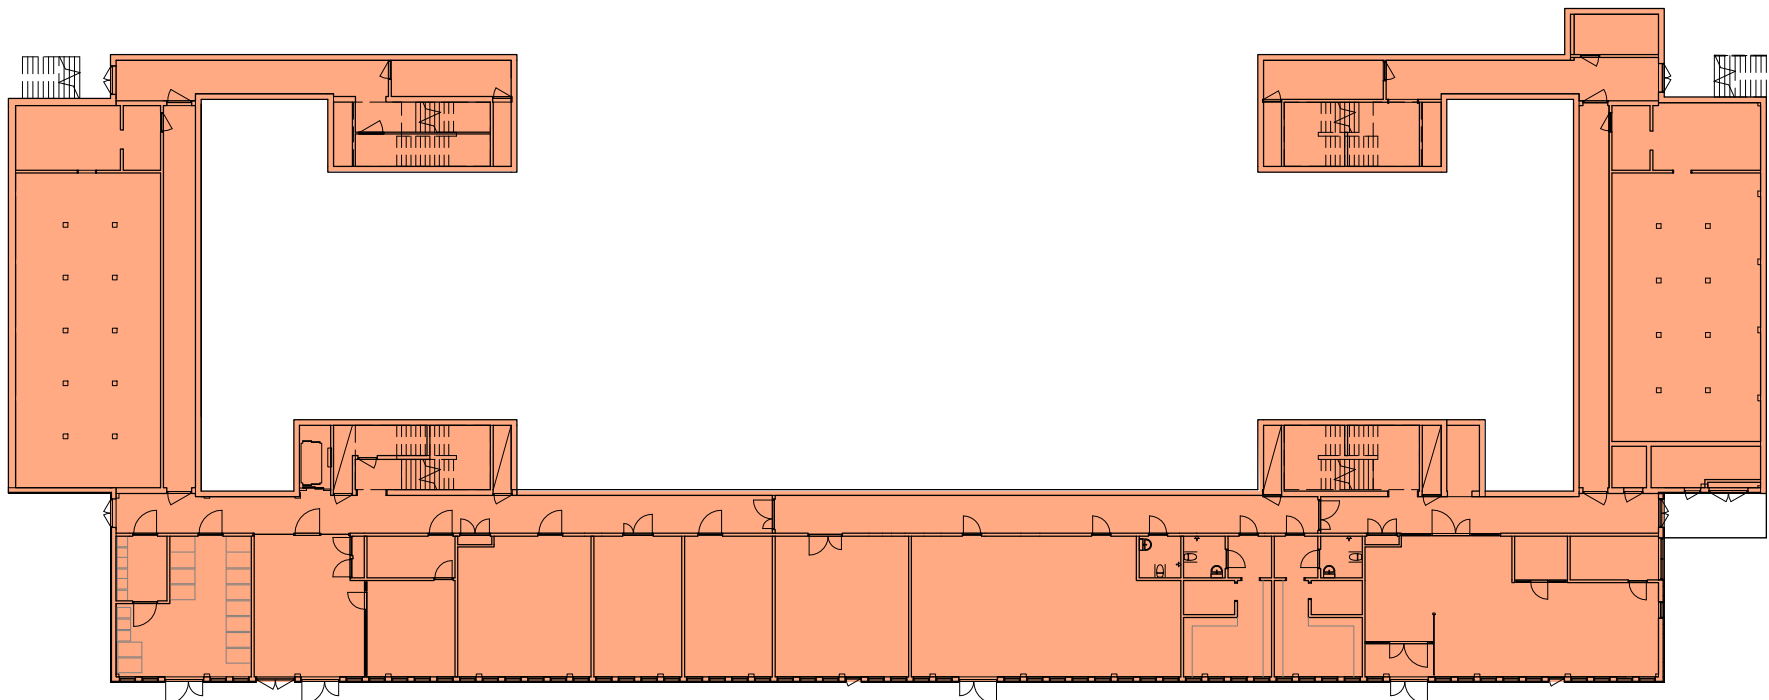


PLAN 09 BTA

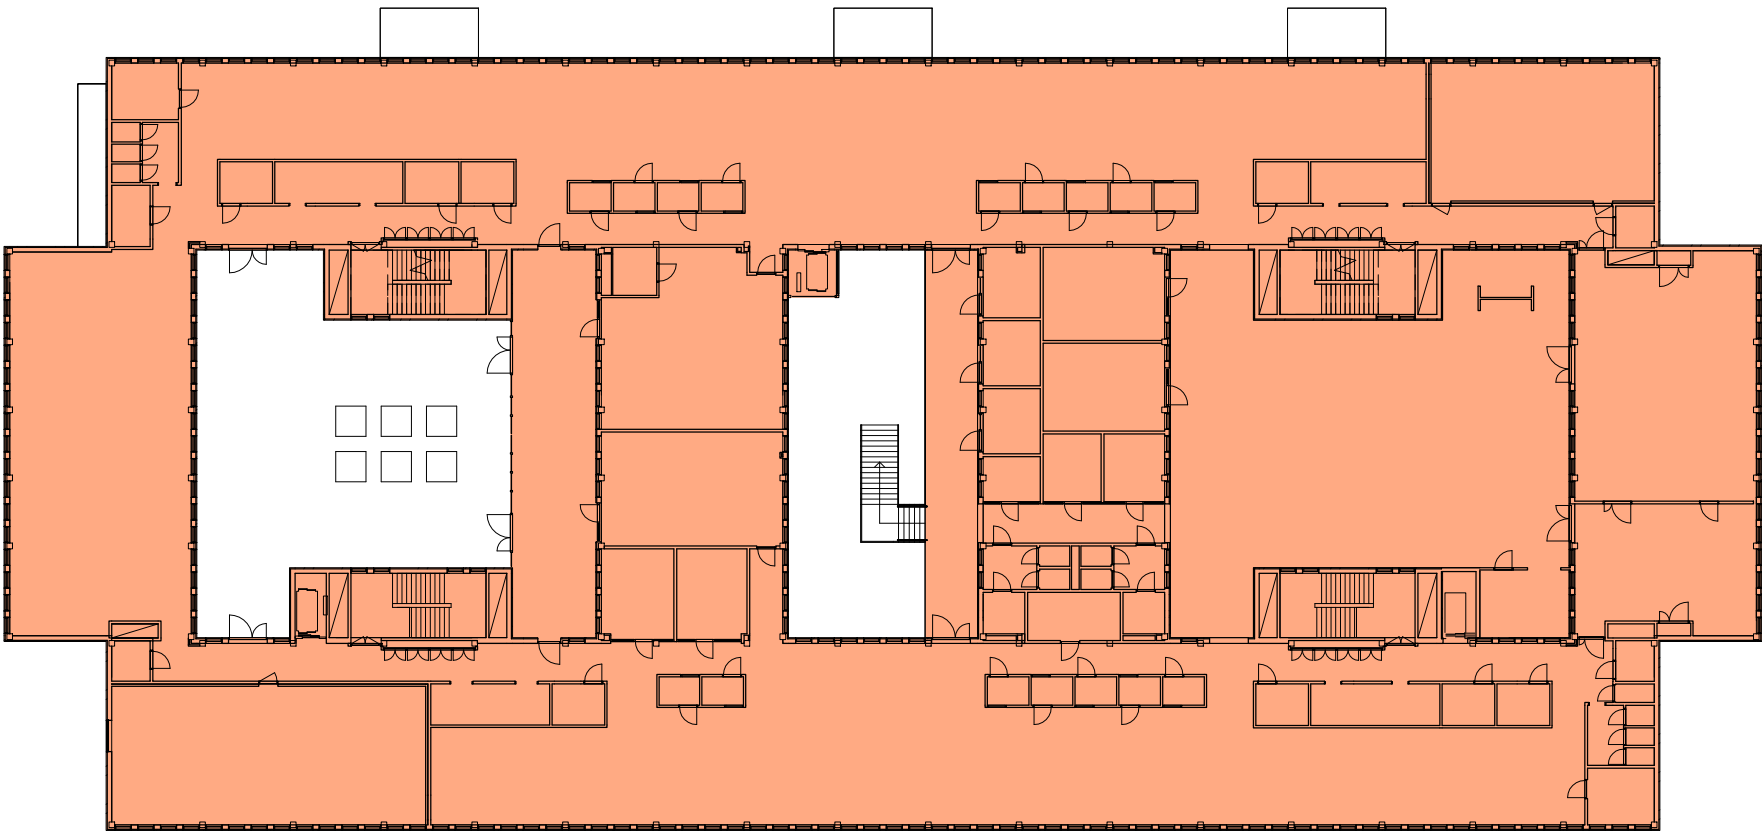



PLAN 11 BTA

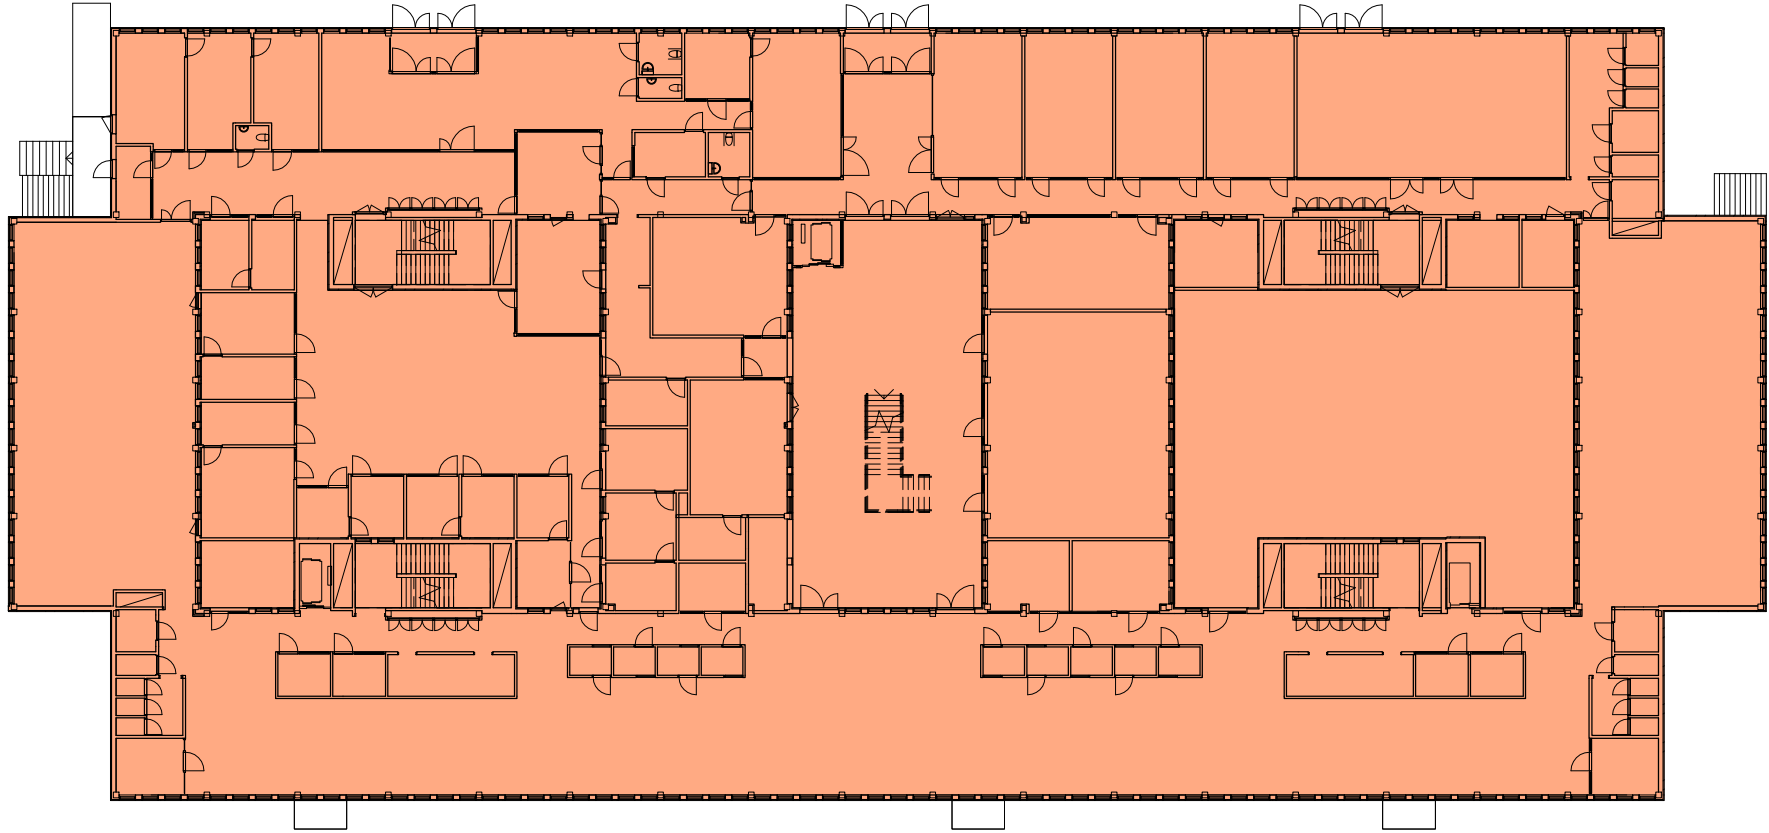

PLAN 10 BTA

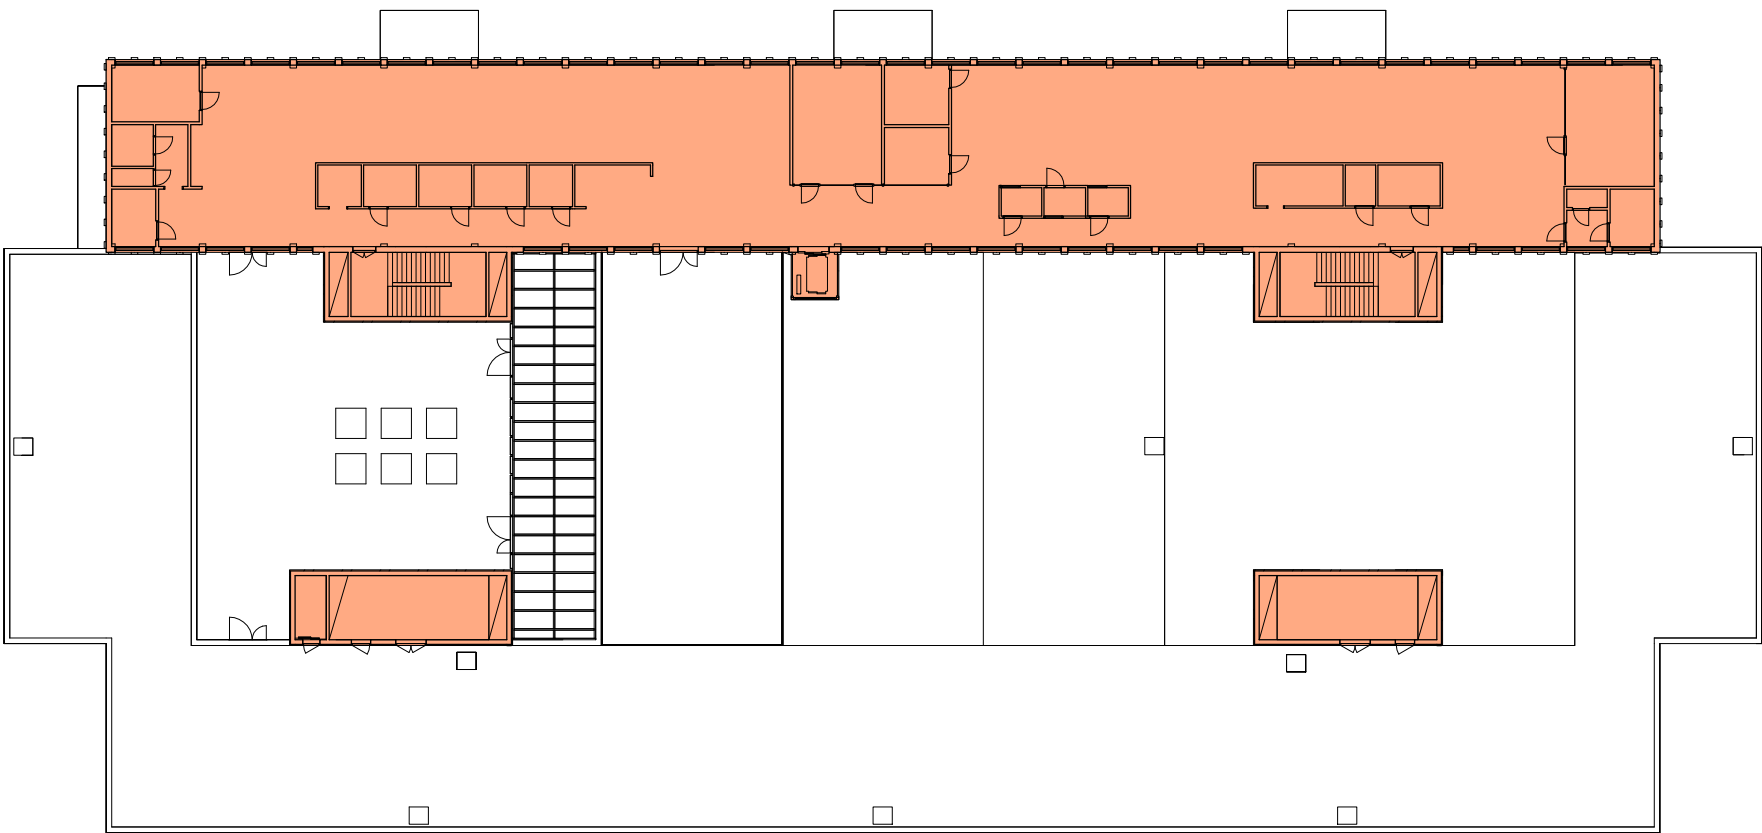


PLAN 12 BTA

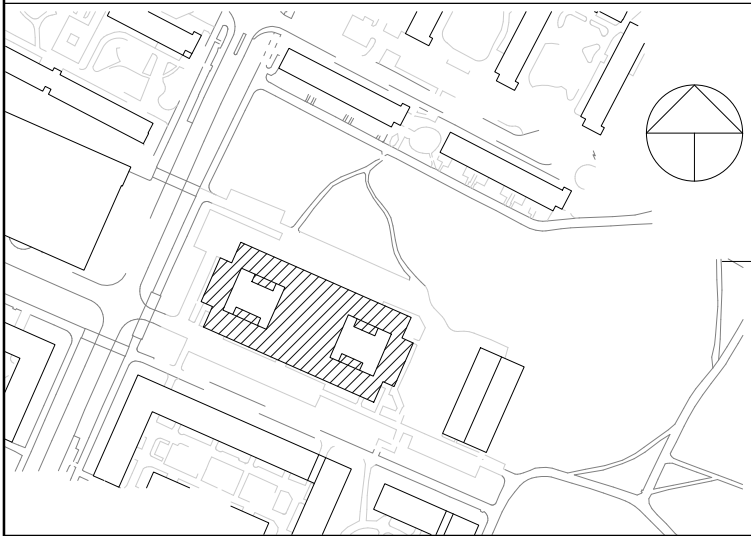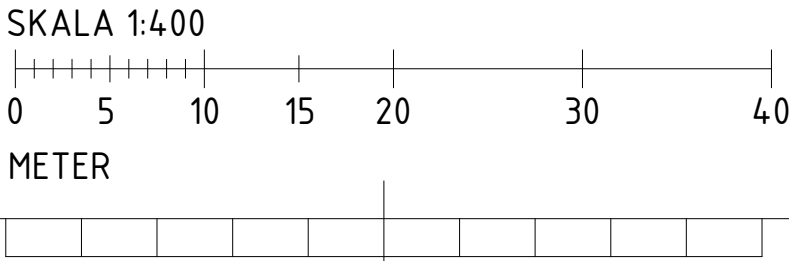


BET	ANT	ÄNDRINGEN AVSER	DATUM	SIGN
PROGRAMHANDLING				
FASTIGHET: KÄMPINGE 2:1				
BYGGNAD: A				
HUS.NR:				
PLAN:				
SEKRETESS:				
Henning Larsen				
Stockholms stad				
B FASTIGHETSKONTORET		Tel: 08-508 270 00		
P WSP		Tel: 070-275 08 96		
A HENNING LARSEN		Tel: 070-574 61 43		
K NORCONSULT		Tel: 079-142 89 57		
V SAMKONSULT		Tel: 070-278 06 29		
PROJEKT NR 74320		RITADYKONSTR. AV SE/JK/AS		ANLÄGGNINGSNUMMER 0260
DATUM 20250124		ANSVARIG M. WAHLGREN		DISCIPLIN A
JÄRVA SDF				
SAMMANSATT REDOVISNING				
AREASAMMANSTÄLLNING - BTA				
SKALA A1 1:400 A3 1:800		RITNINGSNAMN BILAGA 1		
BET				


PRELMINÄR AREASAMMANSTÄLLNING.
KAN KOMMA ATT JUSTERAS UNDER PROJEKTERING.

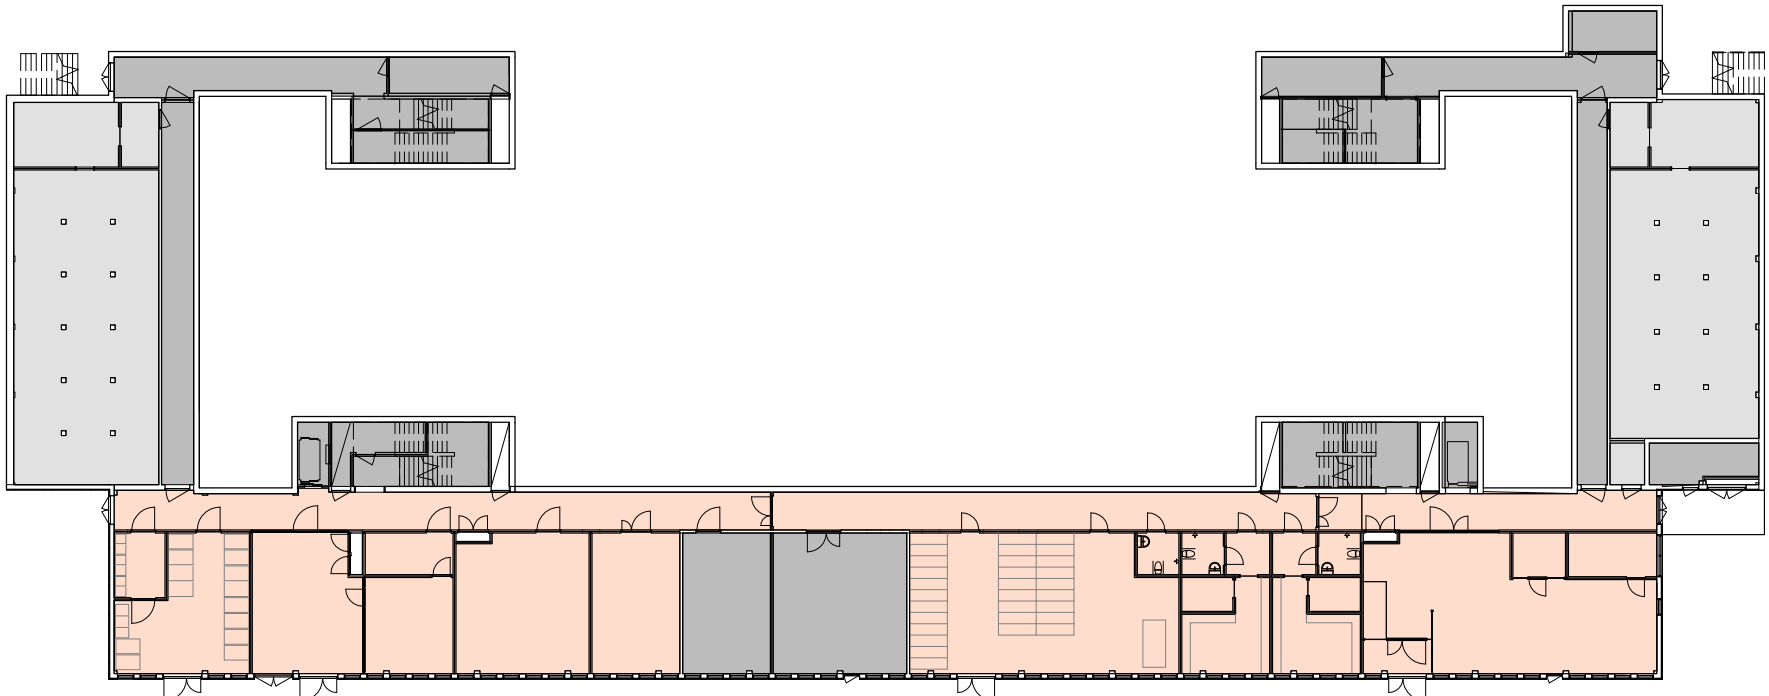


PLAN 09 BRA

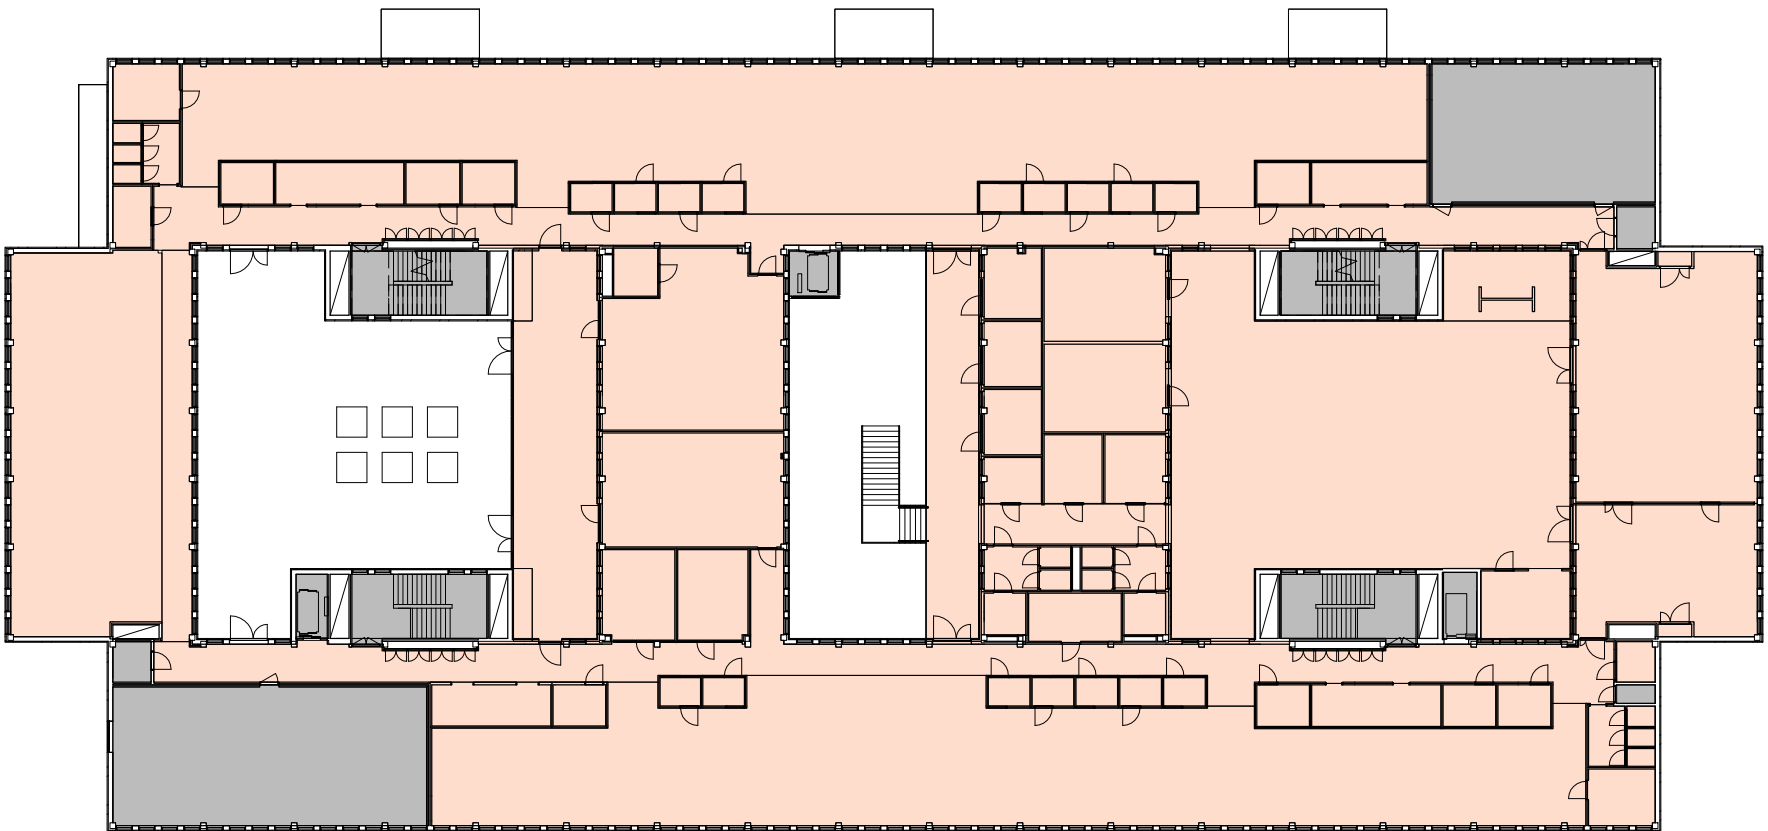

PLAN 11 BRA

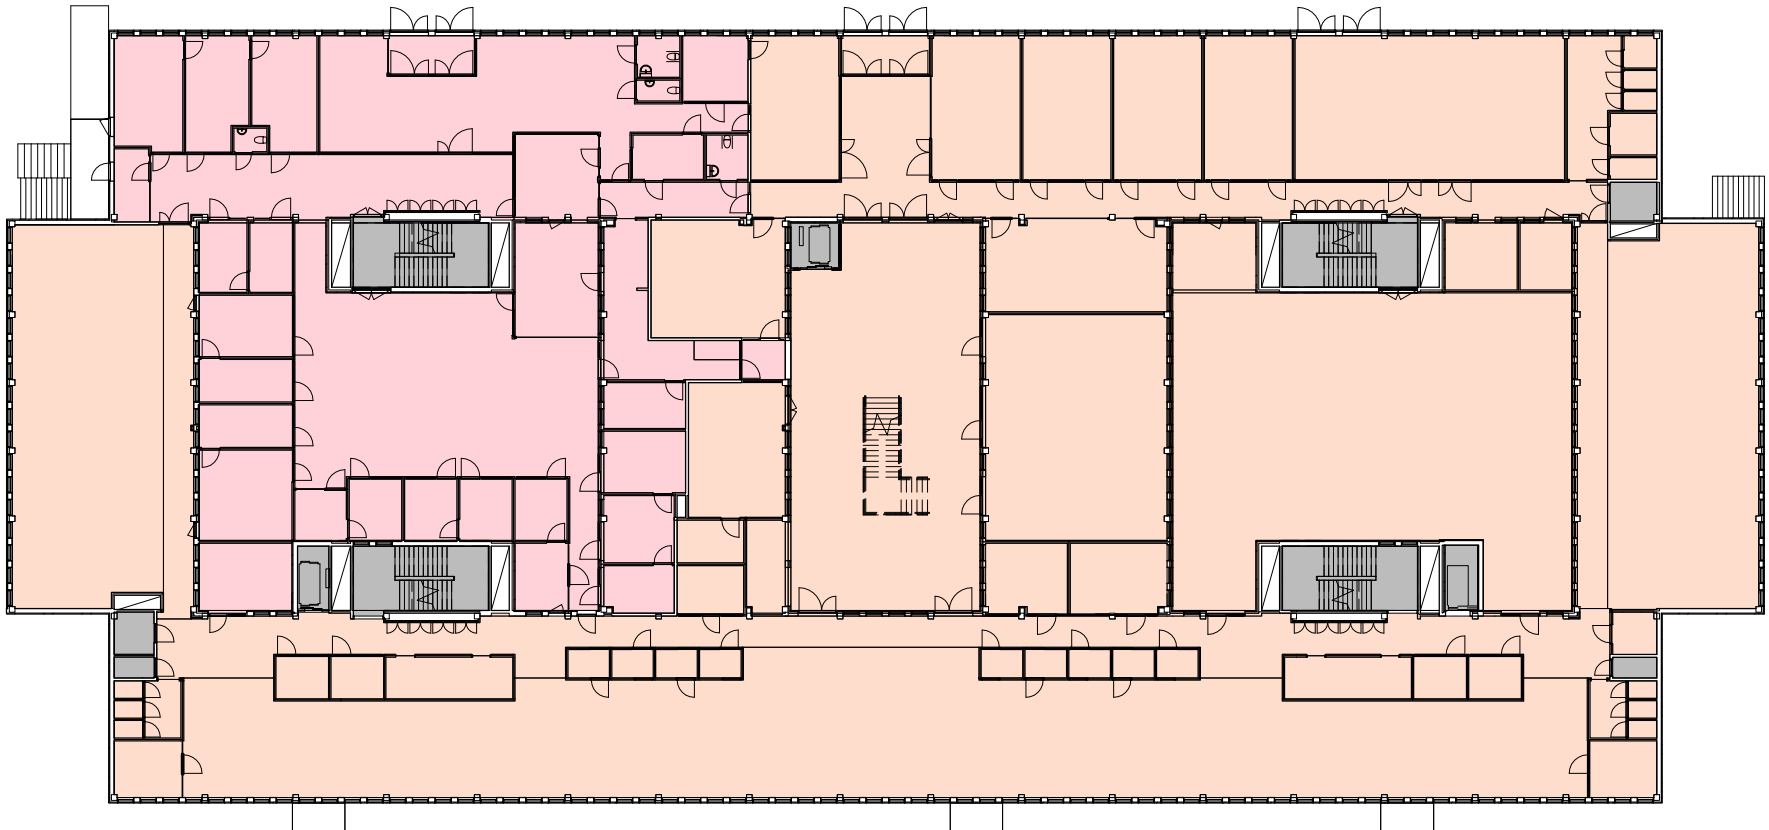

PLAN 10 BRA

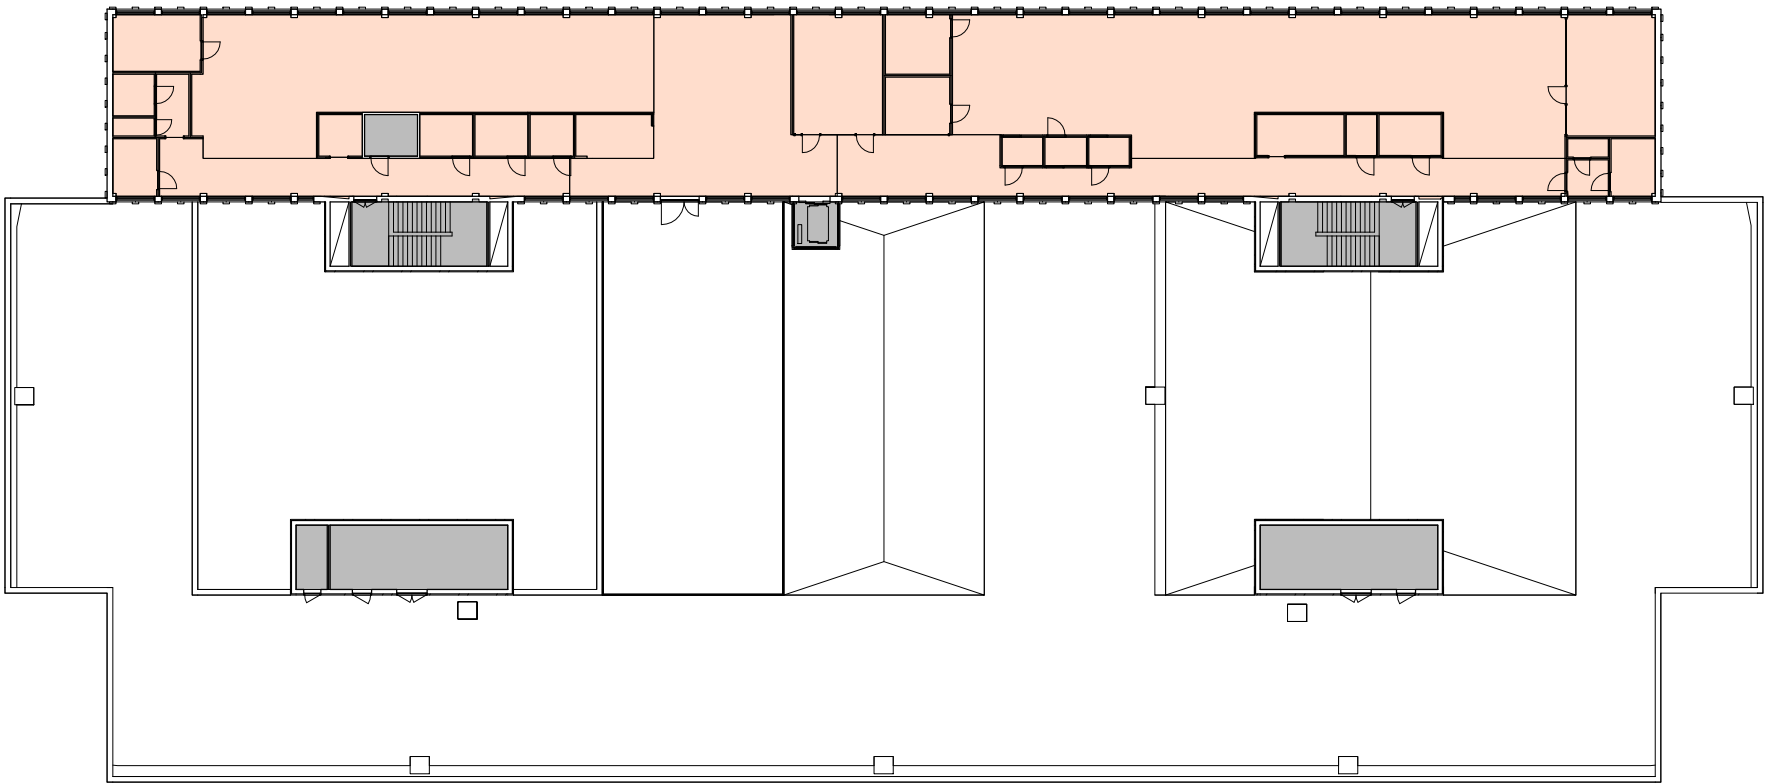


PLAN 12 BRA

AREASAMMANSTÄLLNING - BRA

PLAN 09	
LOA-SDF	686 m ²
SKYDDSRUM	299 m ²
ÖVA	379 m ²
PLAN 10	
LOA-MB	769 m ²
LOA-SDF	2506 m ²
ÖVA	136 m ²
PLAN 11	
LOA-SDF	2649 m ²
ÖVA	343 m ²
PLAN 12	
LOA-SDF	775 m ²
ÖVA	132 m ²
8675 m ²	

SDF - STADSDELSFÖRVALTNING
MB - MEDBORGARBESÖK

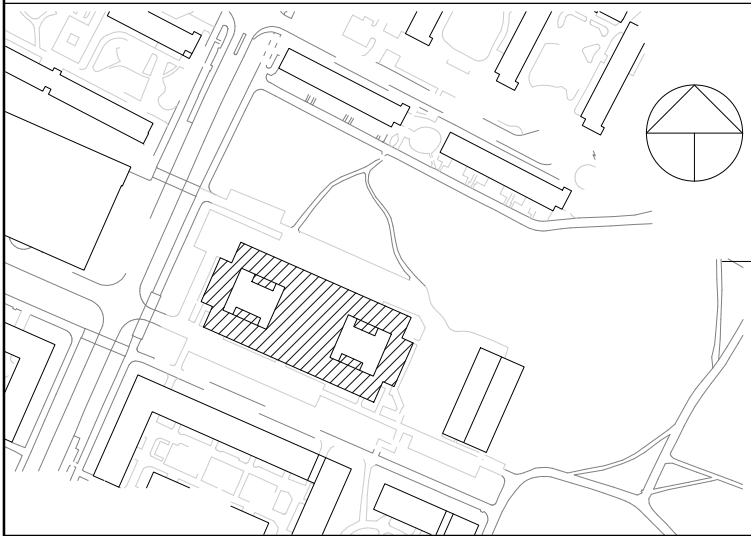

BET	ANT	ÄNDRINGEN AVSER	DATUM	SIGN
-----	-----	-----------------	-------	------

PROGRAMHANDLING

FASTIGHET: KÄMPINGE 2:1
BYGGNAD: A
HUS.NR:
PLAN: SEKRETESS:

Henning
Larsen



B	FASTIGHETSKONTORET	Tel: 08-508 270 00
P	WSP	Tel: 070-275 08 96
A	HENNING LARSEN	Tel: 070-574 61 43
K	NORCONSULT	Tel: 079-142 89 57
V	SAMKONSULT	Tel: 070-278 06 29


PROJEKT NR	RITADYKONSTR. AV	ANLÄGGNINGSNUMMER
74320	SE/JK/AS	0260
DATUM	ANSVARIG	DISCIPLIN
20250124	M. WAHLGREN	A

JÄRVA SDF
SAMMANSATT REDOVISNING
AREASAMMANSTÄLLNING - BRA


SKALA	RITNINGSNAMN	BET
A1 1:400 A3	BILAGA 2	

PRELMINÄR AREASAMMANSTÄLLNING.
KAN KOMMA ATT JUSTERAS UNDER PROJEKTERING.


AREASAMMANSTÄLLNING - NTA	
PLAN 09	1322 m ²
PLAN 10	3283 m ²
PLAN 11	2888 m ²
PLAN 12	886 m ²
8379 m ²	

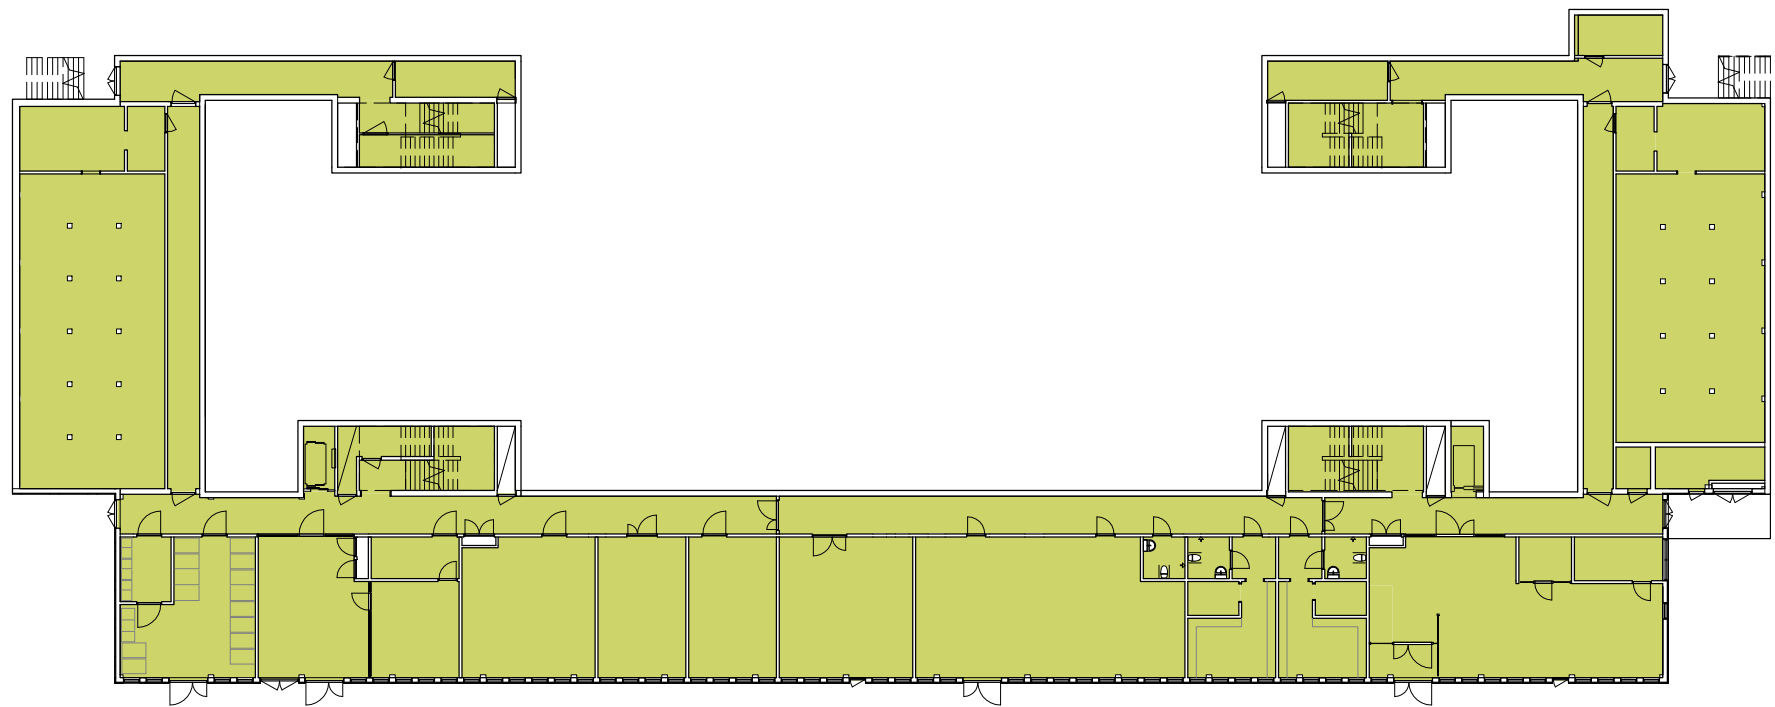


PLAN 09 NTA

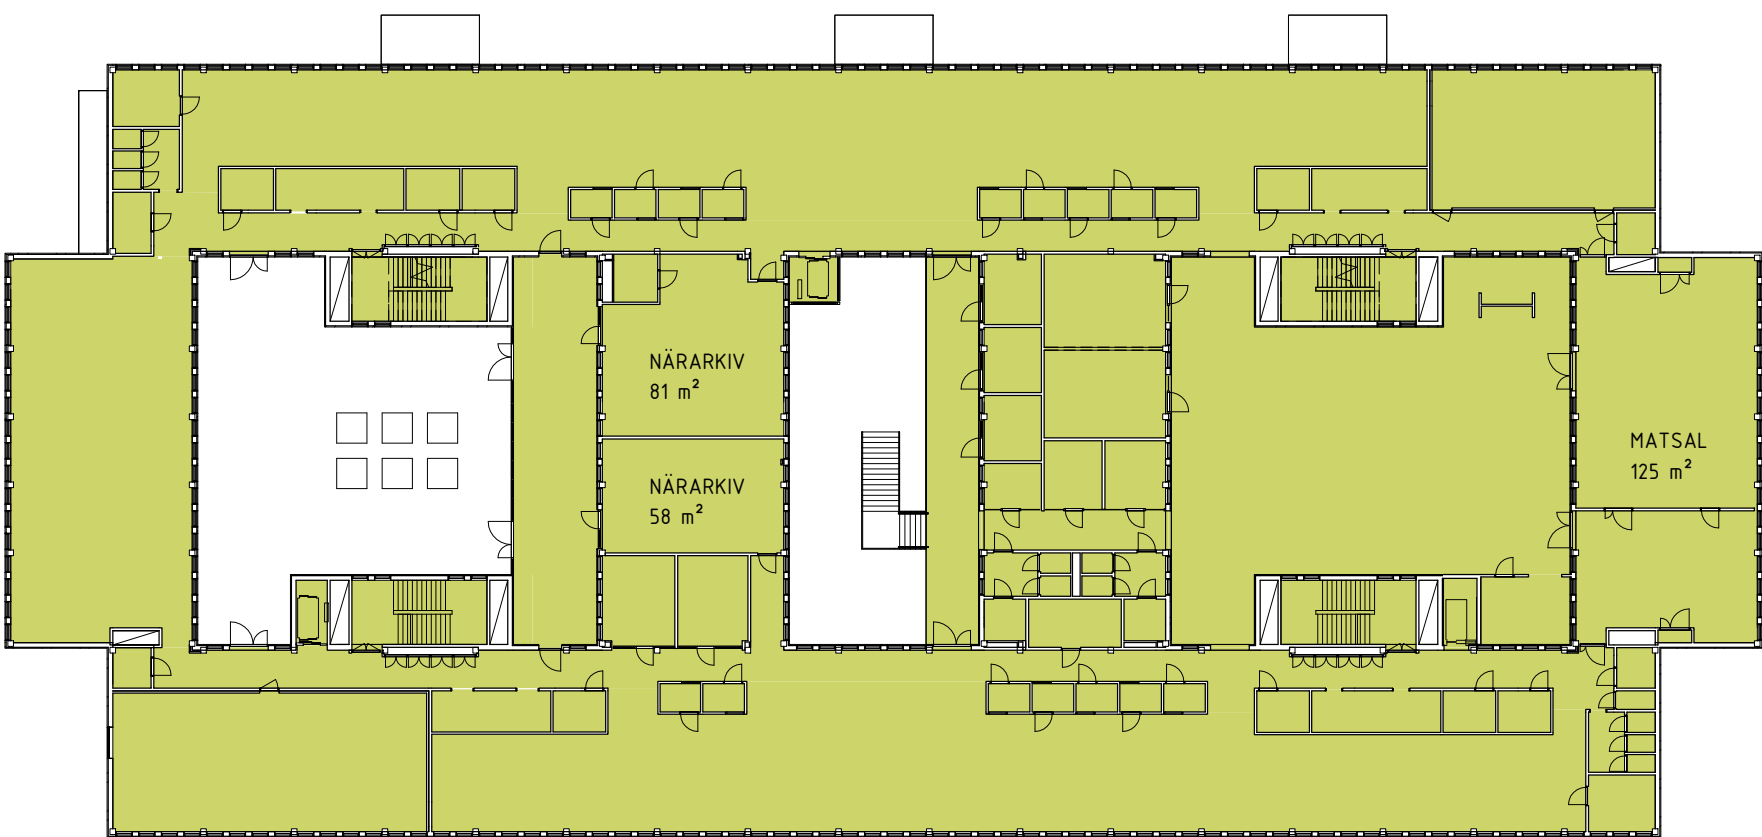


PLAN 11 NTA

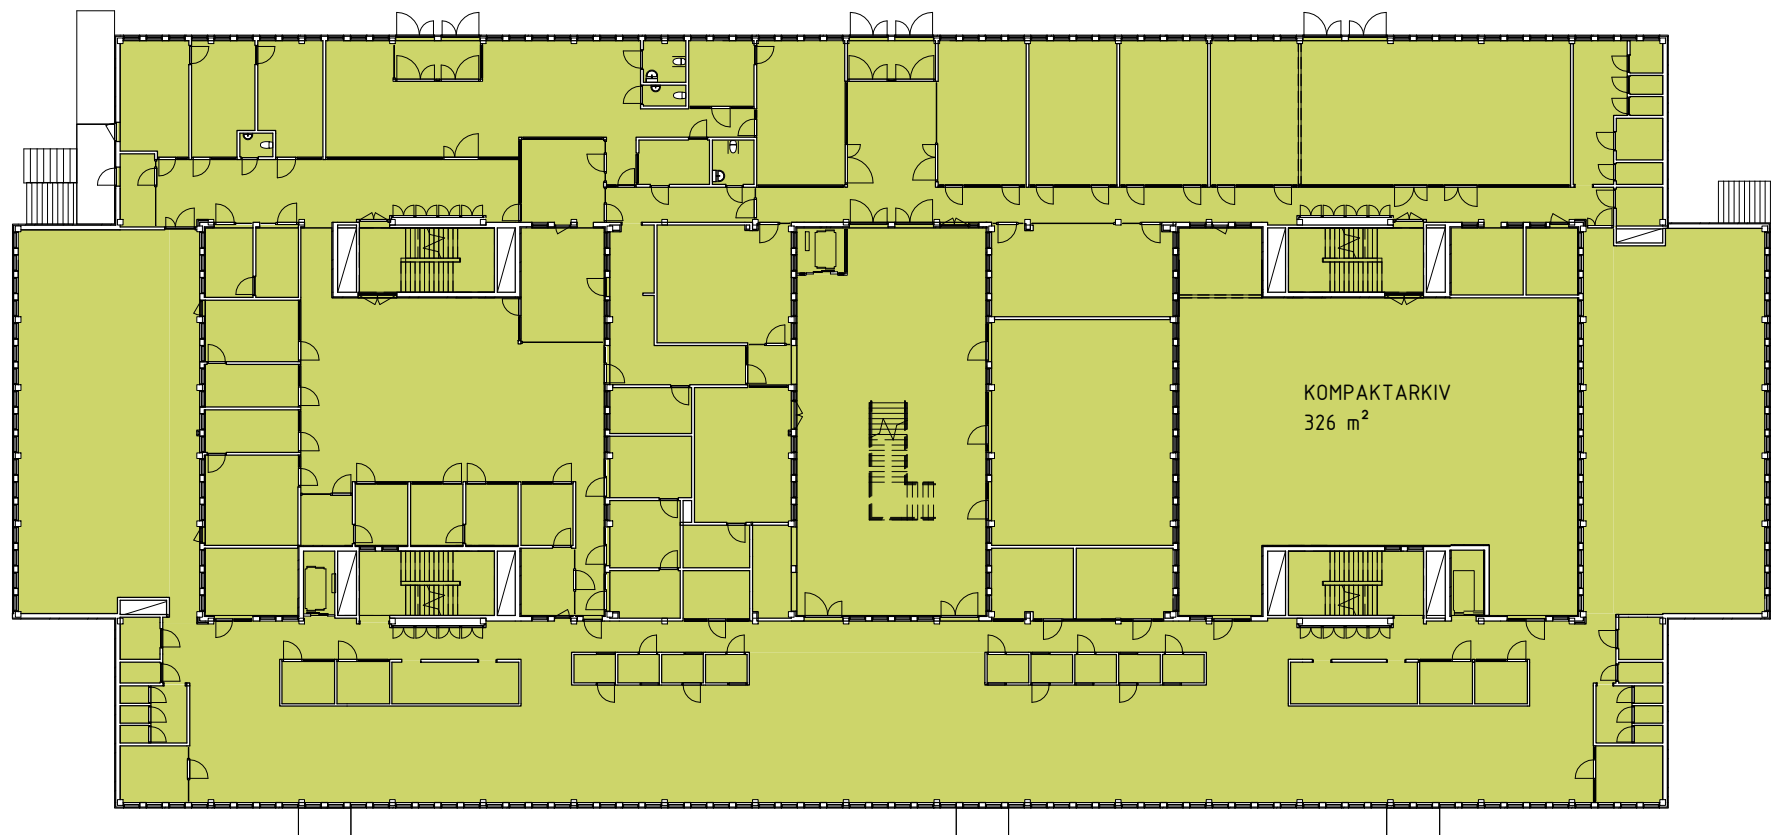

PLAN 10 NTA

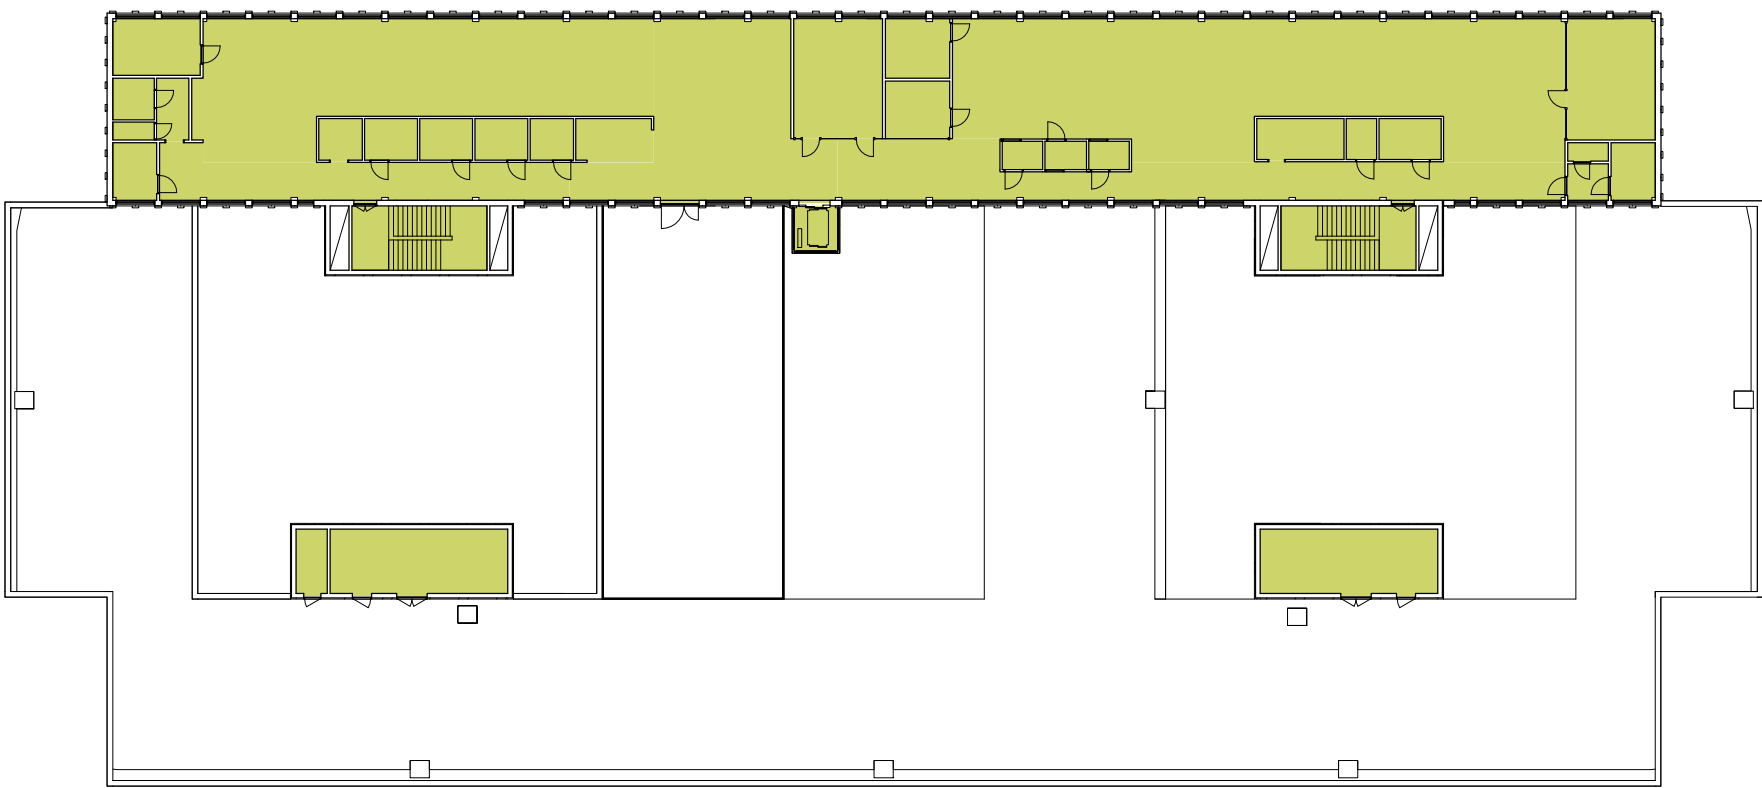

PLAN 12 NTA

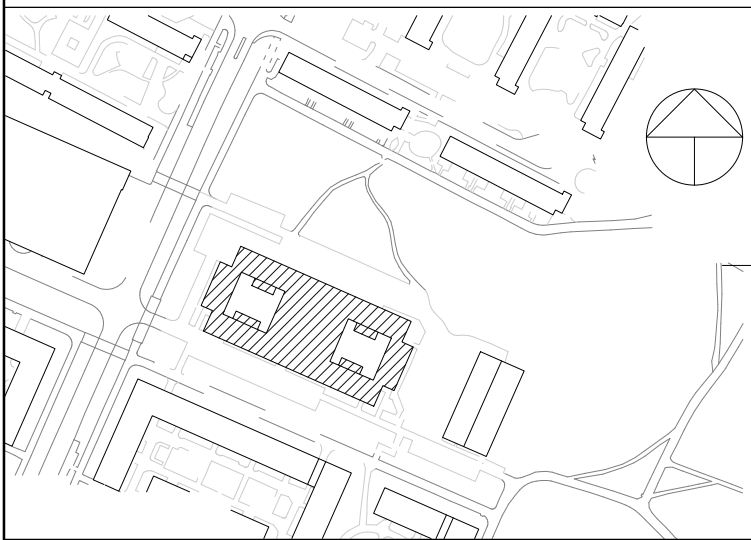

BET	ANT	ÄNDRINGEN AVSER	DATUM	SIGN
PROGRAMHANDLING				
FASTIGHET: KÄMPINGE 2:1				
BYGGNAD: A				
HUS.NR:				
PLAN:				SEKRETESS:
Henning Larsen				
 Stockholms stad				
B FASTIGHETSKONTORET		Tel: 08-508 270 00		
P WSP		Tel: 070-275 08 96		
A HENNING LARSEN		Tel: 070-574 61 43		
K NORCONSULT		Tel: 079-142 89 57		
V SAMKONSULT		Tel: 070-278 06 29		
PROJEKT NR 74320		RITADYKONSTR. AV SE/JK/AS		ANLÄGGNINGSNUMMER 0260
DATUM 20250124		ANSVARIG M. WAHLGREN		DISCIPLIN A
JÄRVA SDF				
SAMMANSATT REDOVISNING				
AREASAMMANSTÄLLNING - NTA				
SKALA A1 1:400 A3 1:800		RITNINGSNAMN BILAGA 3		BET