



Tillgänglig utrymning

- Placering av utrymningsplatser fastställs i kommande projektering

Slagriktning på dörrar ska ses över i nästa skede

TECKENFÖRKLARING

- Utrymningsväg
- Utrymningsstrategi
- Brandcellsgräns EI 60

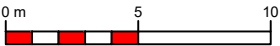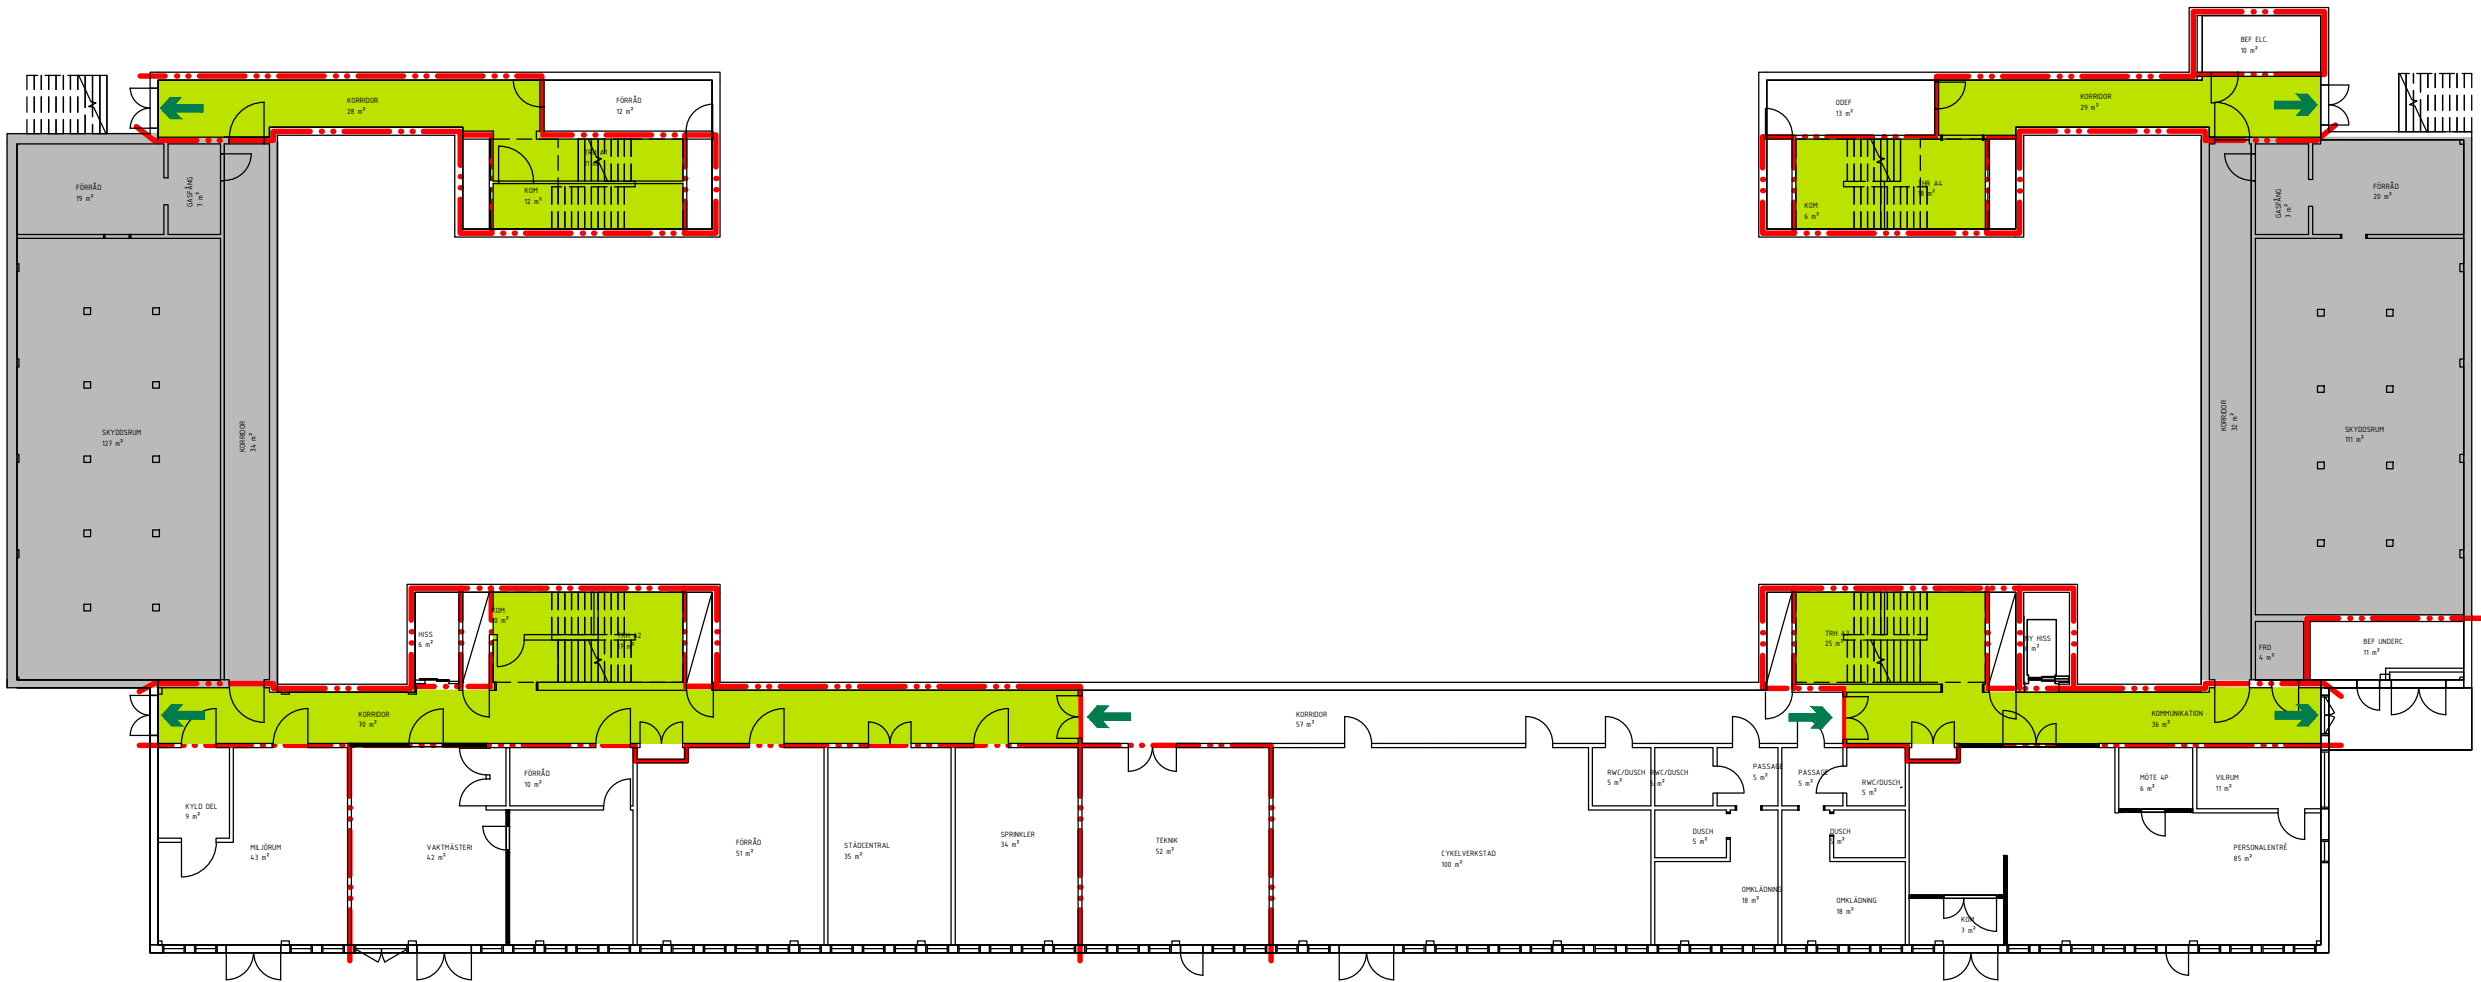


A	XXX	XXX	XXXX-XX-XX
BET	ÄNDRINGEN AVSER		SIGN DATUM
Programhandling			
Stockholm-Kämpingeskolan, Järva			
Stockholm stad			
			
SÄKERHETSPARTNER			
A	ARKITEKT	Arkitekt tel	
K	KONSTRUKTÖR	Konstruktör tel	
V	VVS	VVS tel	
E	EL	El tel	
M	MARK	Mark tel	
BR	SÄKERHETSPARTNER NORDEN AB		072-72 730 85 85
UPPDRAGSMUMMER	RTAD / KONSTR AV	HANDLÄGGARE	
-	Håkan Lindström	Gustav Näslund	
DATUM	UPPDRAGSANSVARIG		
2025-01-24	Ali Babayan		
Plan 09			
ÖVERSIKT BRAND			
SKALA	NUMMER	BET	
-	BR-40-1-0009-ÖB01		-

Tillgänglig utrymning

- Placering av utrymningsplatser fastställs i kommande projektering

Slagriktning på dörrar ska ses över i nästa skede

Fri bredd på dörrar ska vara 1,2 meter

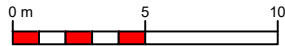

TECKENFÖRKLARING

- Utrymningsväg
- Utrymningsstrategi
- Brandcellsgräns EI 60
- Brandcellsgräns EI 120

A	XXX	XXX	XXXX-XX-XX
BET	ÄNDRINGEN AVSER		SIGN DATUM
Programhandling			
Stockholm-Kämpingeskolan, Järva			
Stockholm stad			
			
SÄKERHETSPARTNER			
A	ARKITEKT	Arkitekt tel	
K	KONSTRUKTÖR	Konstruktör tel	
V	VVS	VVS tel	
E	EL	El tel	
M	MARK	Mark tel	
BR	SÄKERHETSPARTNER NORDEN AB		072-72 730 85 85
UPPDRAGSMUMMER	RITAD / KONSTR AV	HANDLAGARE	
-	Håkan Lindström	Gustav Näslund	
DATUM	UPPDRAGSANSVARIG		
2025-01-24	Ali Babayan		
Plan 10			
ÖVERSIKT BRAND			
SKALA	NUMMER	BET	
-	BR-40-1-0010-ÖB01	-	



Tillgänglig utrymning

- Placering av utrymningsplatser fastställs i kommande projektering

Slagriktning på dörrar ska ses över i nästa skede

TECKENFÖRKLARING

- Utrymningsväg
- Utrymningsstrategi
- Brandcellsgräns EI 60
- Brandcellsgräns EI 120

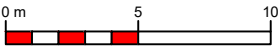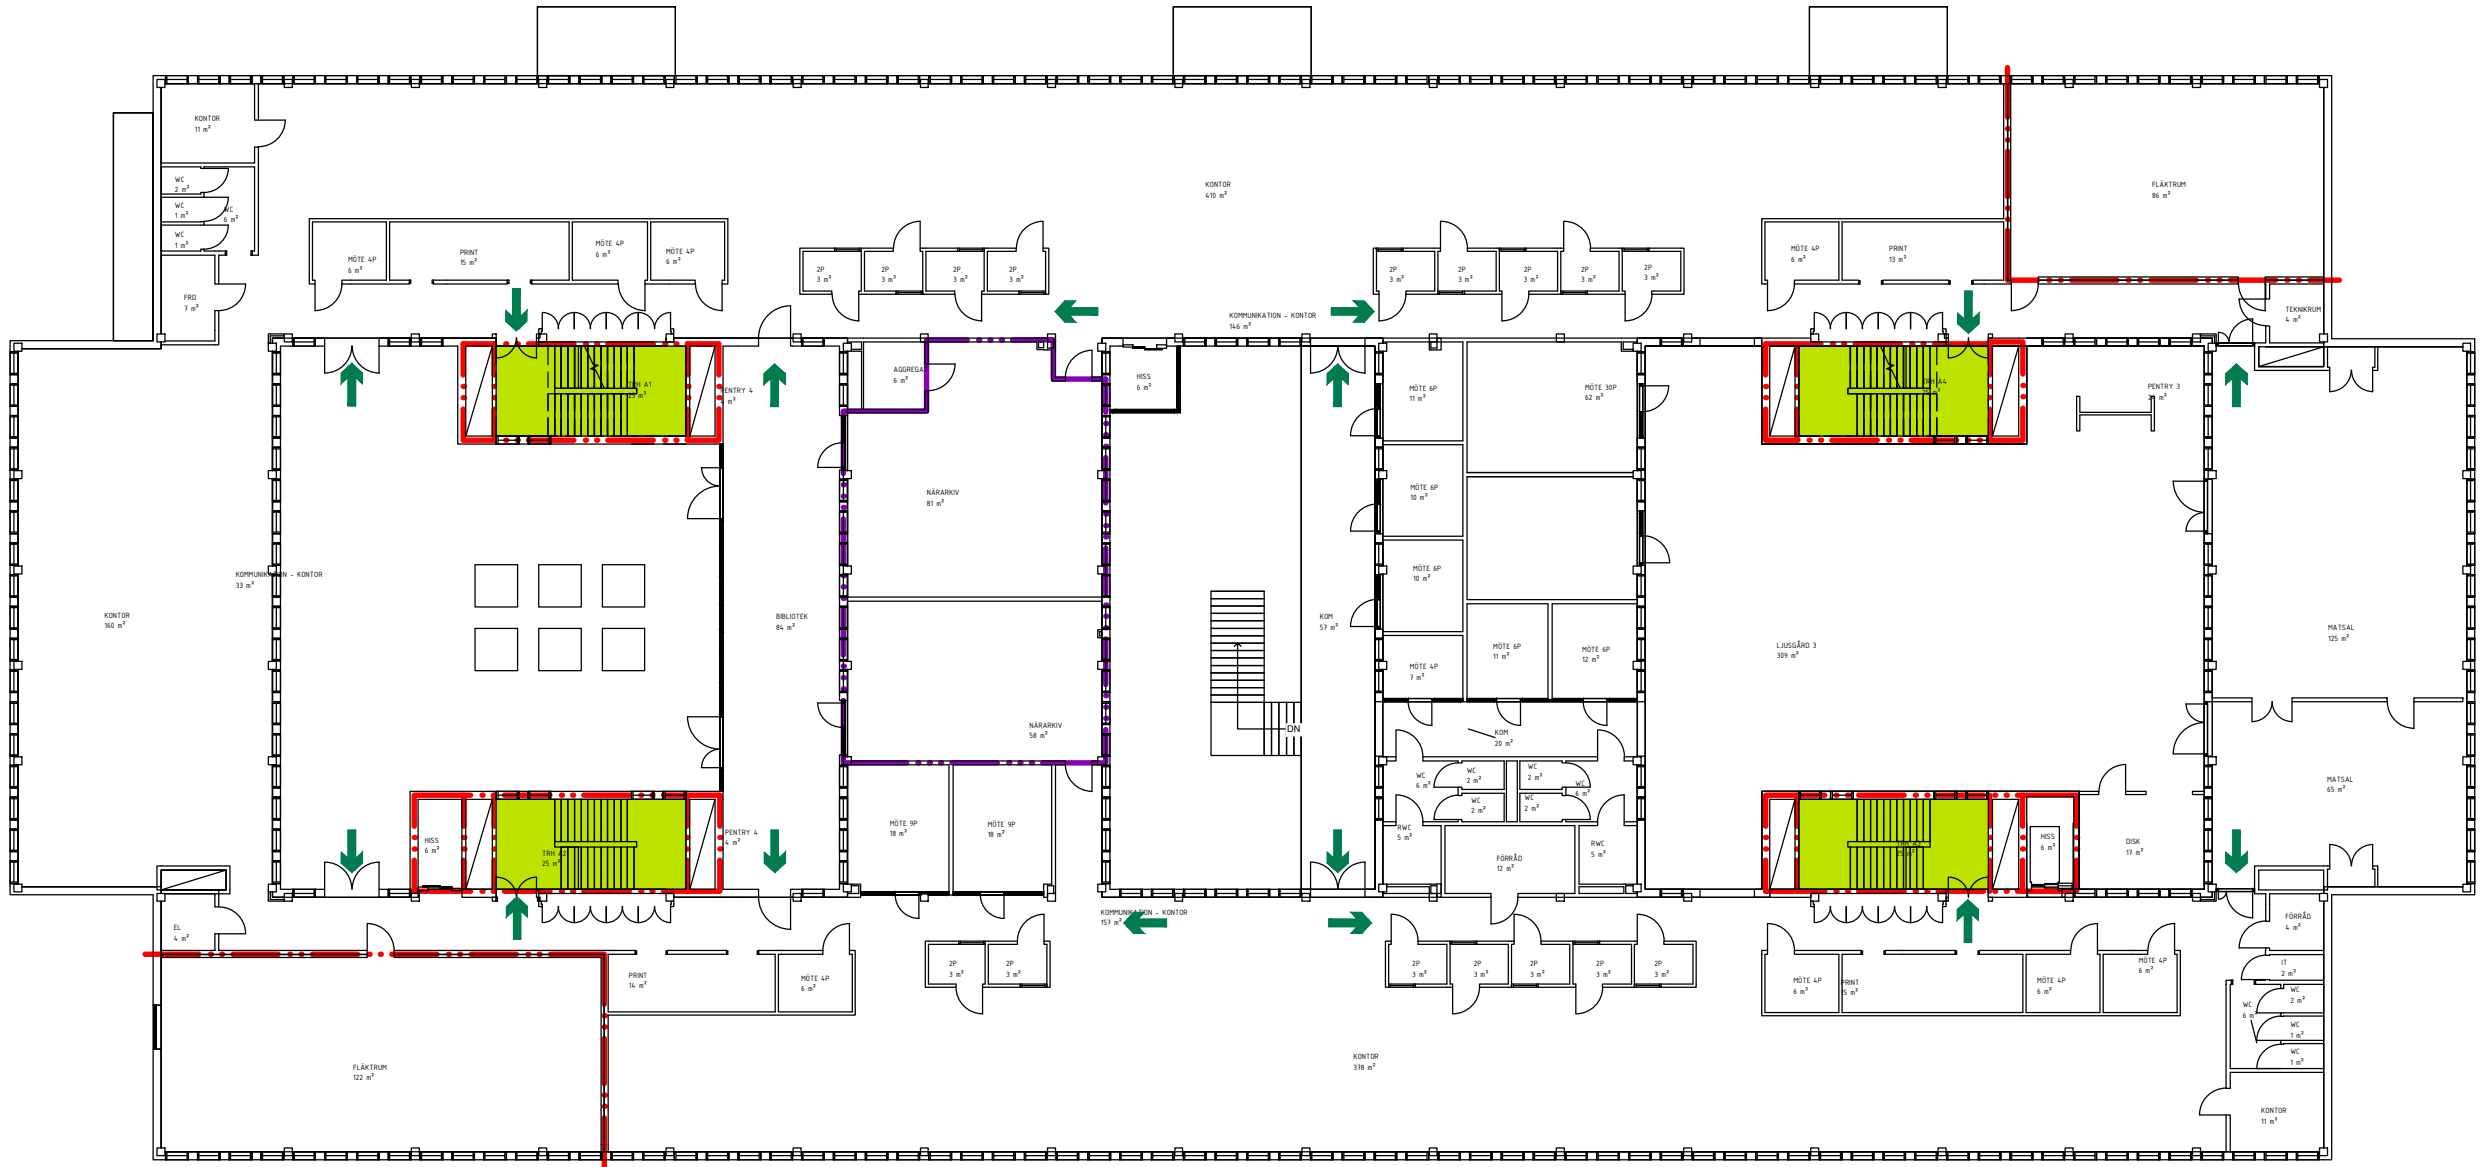

XXX		XXX	XXXX-XX-XX
BET	ÄNDRINGEN AVSER	SIGN	DATUM
Programhandling			
Stockholm-Kämpingeskolan, Järva			
Stockholm stad			
			
SÄKERHETSPARTNER			
A	ARKITEKT	Arkitekt tel	
K	KONSTRUKTÖR	Konstruktör tel	
V	VVS	VVS tel	
E	EL	El tel	
M	MARK	Mark tel	
BR	SÄKERHETSPARTNER NORDEN AB		072-72 730 85 85
UPPGÄVNUMMER	RITAD / KONSTR AV	HANDLAGARE	
-	Håkan Lindström	Gustav Näslund	
DATUM	UPPGÄVANSVARIG		
2025-01-24	Ali Babayan		
Plan 11			
ÖVERSIKT BRAND			
SKALA	NUMMER	BET	
-	BR-40-1-0011-ÖB01	-	



Tillgänglig utrymning

- Placering av utrymningsplatser fastställs i kommande projektering

Slagriktning på dörrar ska ses över i nästa skede

TECKENFÖRKLARING

- Utrymningsväg
- Utrymningsstrategi
- Brandcellsgräns EI 60

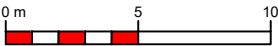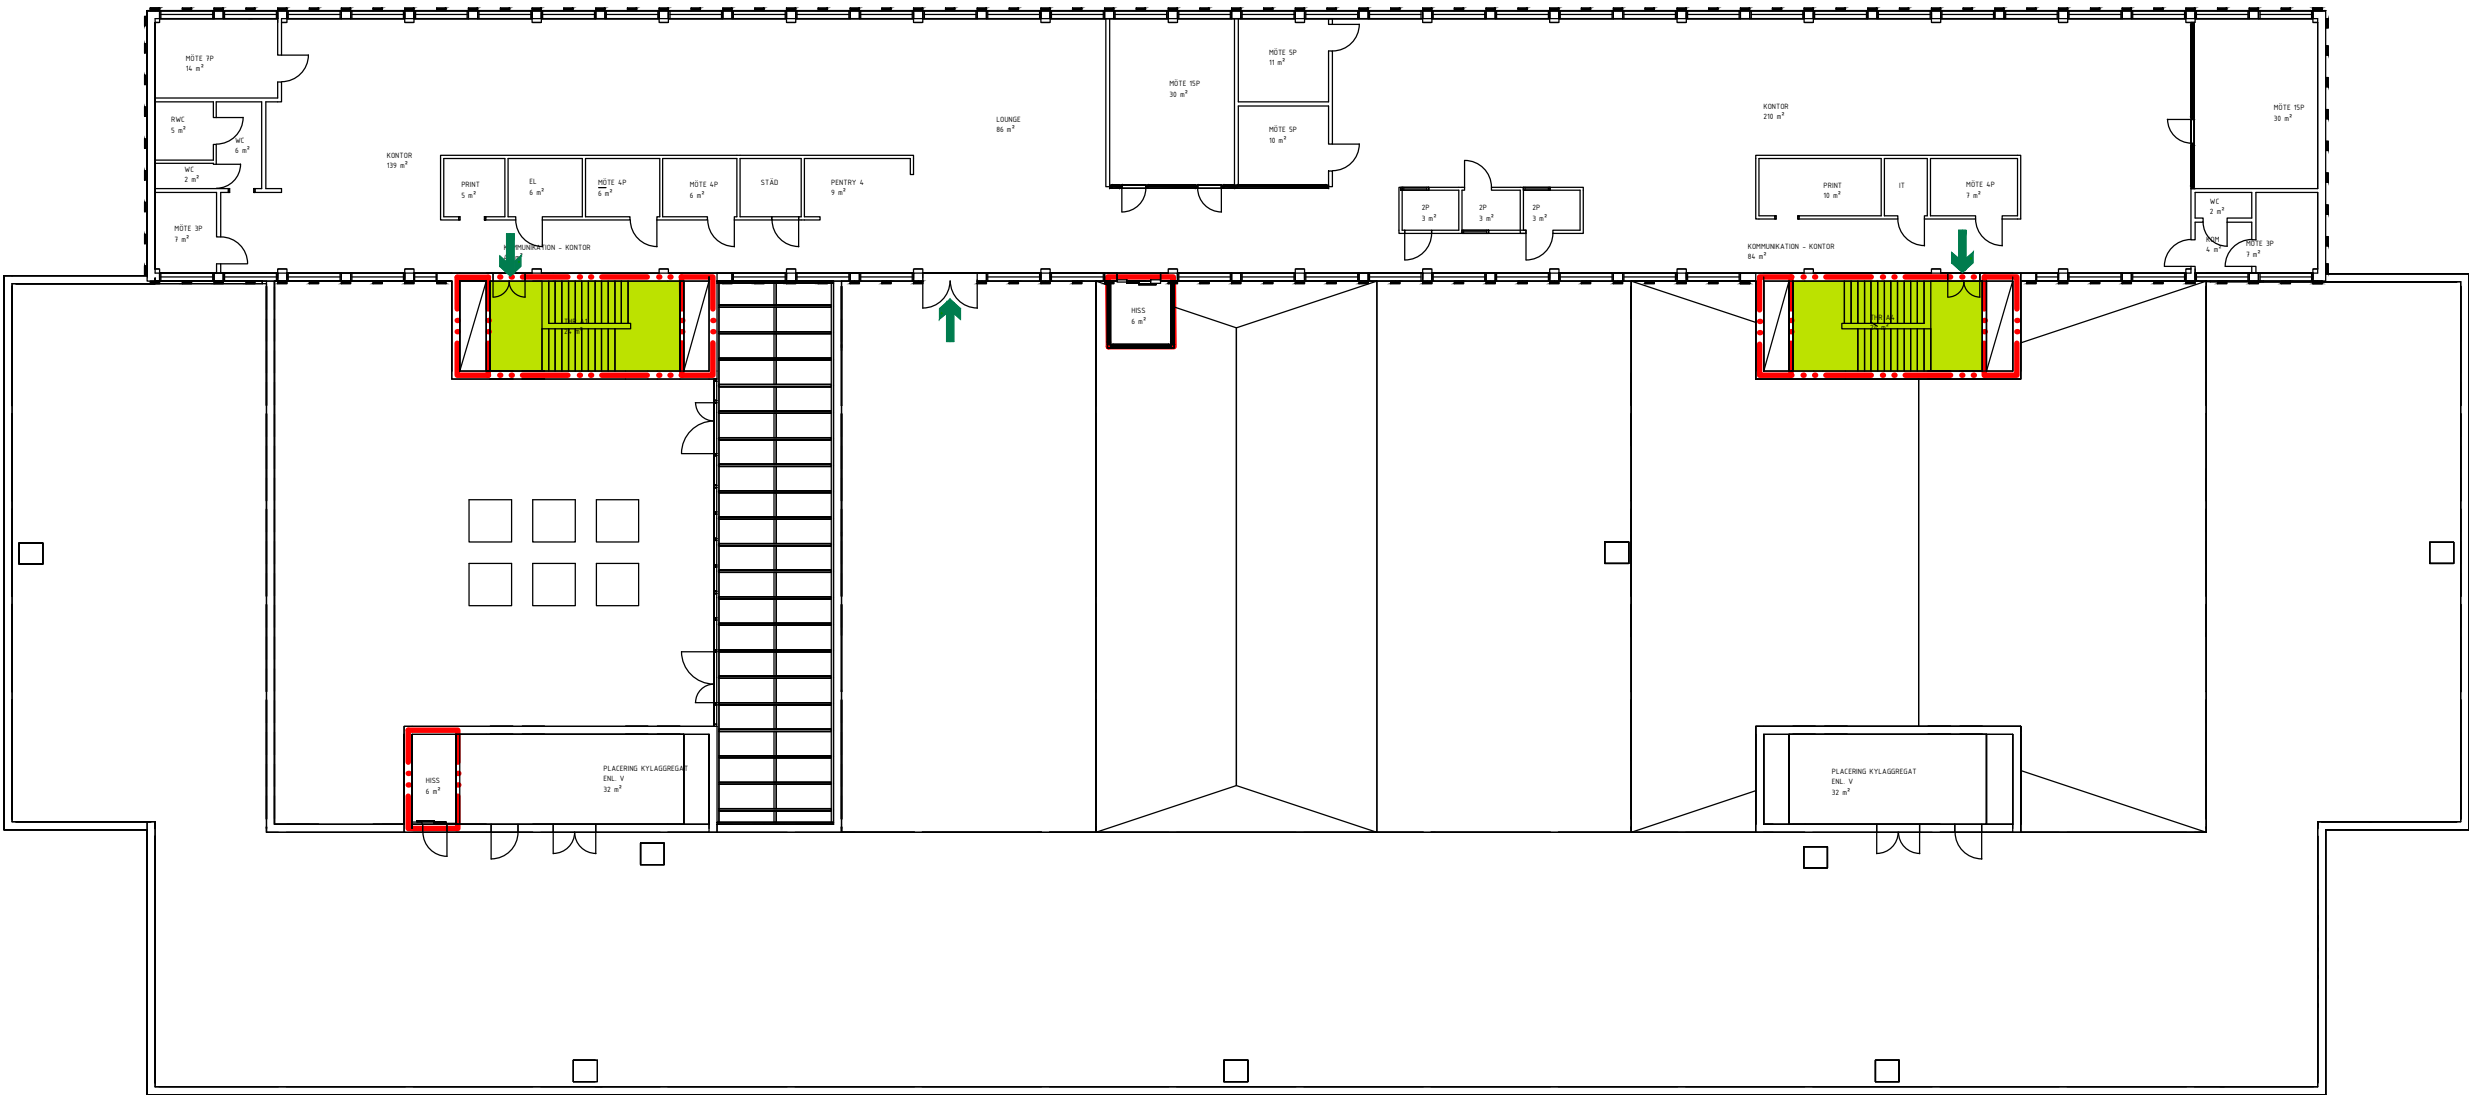

		XXXX	XXXX	XXXX-XX-XX
BET	ÄNDRINGEN AVSER		SIGN	DATUM
Programhandling				
Stockholm-Kämpingeskolan, Järva				
Stockholm stad				
				
SÄKERHETSPARTNER				
A	ARKITEKT			Arkitekt tel
K	KONSTRUKTÖR			Konstruktör tel
V	VVS			VVS tel
E	EL			El tel
M	MARK			Mark tel
BR	SÄKERHETSPARTNER NORDEN AB			072-72 730 85 85
UPPDRAGSNUMMER	RITAD / KONSTR AV		HANDLÄGGARE	
-	Håkan Lindström		Gustav Näslund	
DATUM	UPPDRAGSANSVARIG			
2025-01-24	Ali Babayan			
Plan 12				
ÖVERSIKT BRAND				
SKALA	NUMMER			BET
-	BR-40-1-0012-ÖB01			-

REF: ..\A\0260-A-40-1-0012.dwg

LAGER: SB11

PLO: 2025-01-24 14:11 C:\SÄKERHETSPARTNER NORDEN AB\2. KUNDER - FILER\STOCKHOLMS STAD\2. PROJEKT\STOCKHOLM-KÄMPINGESKOLAN. JÄRVA\4. RITNINGAR\BR-40-1-0012.DWG MAGNUS BOKVIST