

FÖRKLARINGAR

BRANDSKYDD

SE ÄVEN BRANDSKYDDSBESKRIVNING


BRANDCELLSGRÄNS E130
BRANDCELLSGRÄNS E160


UTRYMNINGSSKYLT
TYP ENLIGT BRANDSKYDDSBESKRIVNING

ÖVRIGT

- NY VÄGG
- NY ÖPPNING
- AK = ARMBÅGSKONTAKT
- STR = STUPRÖR (BEFINTLIGT)
- Dxx = DÖRRPOSITIONSNUMMER

STORKÖKSANLÄGGNING VISAS HÄR ENDAST FÖR ILLUSTRATION
SE STORKÖKSHANDLINGAR FÖR KOMPLETT REDOVISNING.

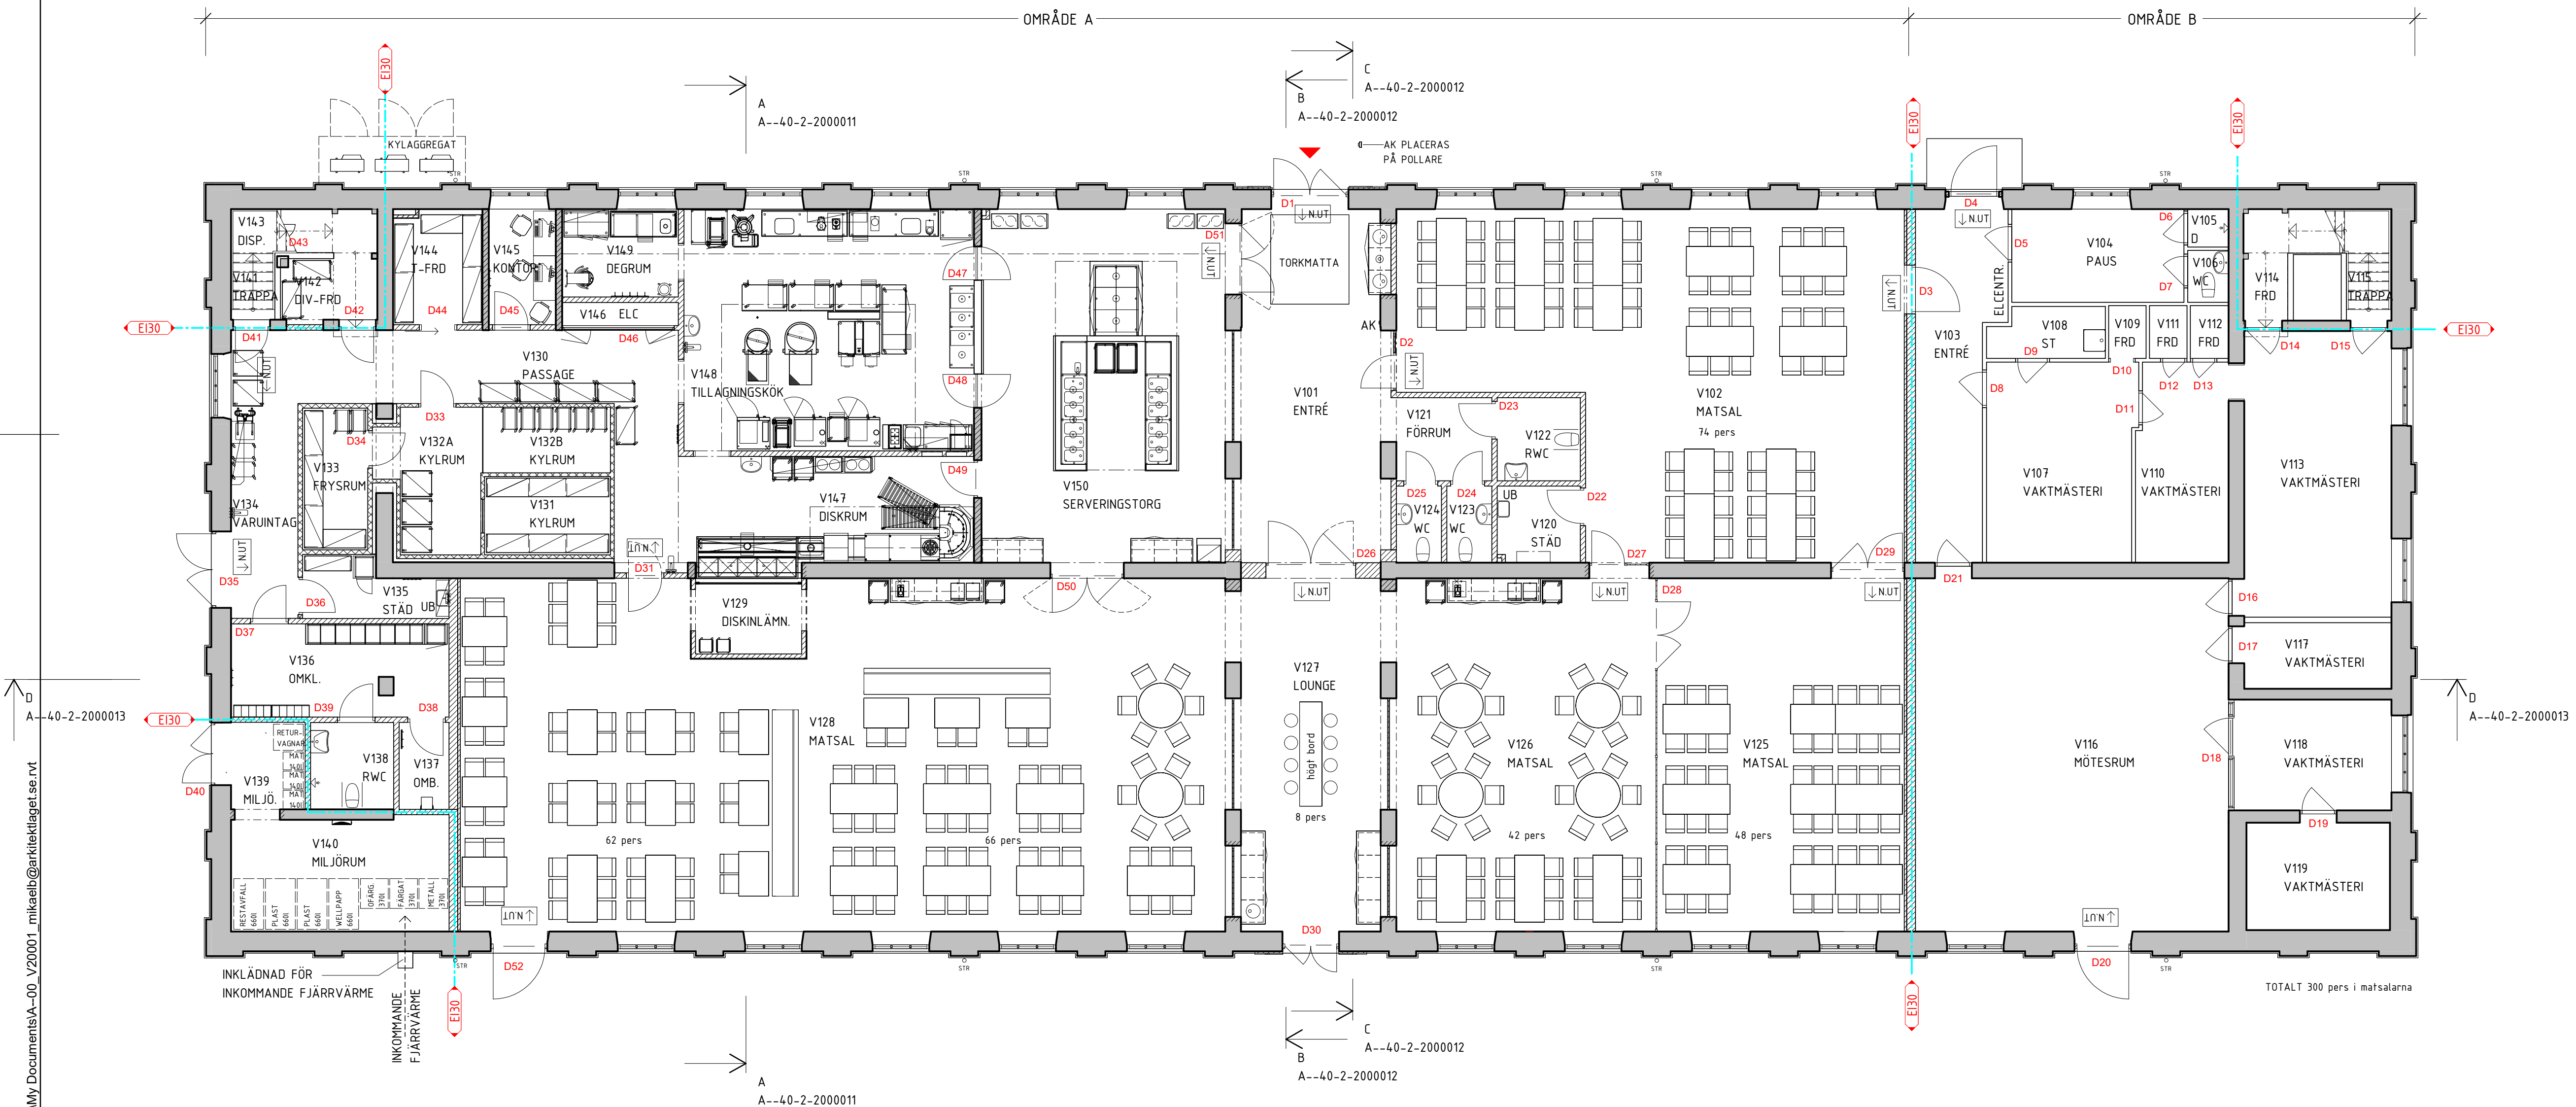

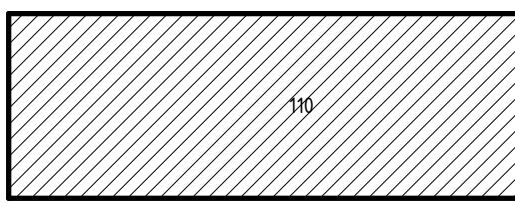ÄNDRING AVSER		DATUM	SIGN
FÖRFRÅGNINGSUNDERLAG			
 HELSINGBORG FASTIGHETSFÖRVALTNINGEN			
FASTIGHET			
ORIENTEN 6			
RÖNNOWSKA SKOLAN, NYTT KÖK OCH MATSAL			
OBJEKTSNR	BYGGNADS-ID	PROJEKTSNR	
1457	5-266088	60095	
BYGGNAD			
1457-20 - HUS V (BYGGNAD 449)			
ORIENTERINGSFIGUR			
PLAN		03	
DEL		01	
			
VÄSTRA SANDGATAN			
(A) ARKITEKTLAGET SKÅNE AB		T: 042-19 96 00	
BR FIRETECH ENGINEERING EMRON AB		T: 010-150 14 00	
E DEVELCON AB		T: 079-020 27 02	
K ÅKERMANS INGENJÖRSBYRÅ AB		T: 042-12 00 10	
M TYRÉNS AB		T: 010-452 20 00	
S SWECO SVERIGE AB		T: 08-695 60 00	
SK STORKÖKSVISION		T: 040-744 29	
V SWECO SVERIGE AB		T: 08-695 60 00	
W SWECO SVERIGE AB		T: 08-695 60 00	
UPPDRAGSNR		ANSVARIG	
22063_00		BRANISLAV KUZMANOVIC	
DATUM		RITAD/KONSTR AV	
2025-01-27		MB	
HANDLAGGARE		SYSTEMBETECKNING	
BK		40-1	
HUS 20			
BOTTENVÅNING, DEL 110			
-			
-			
SKALA		NUMMER	
1:100		A--40-1-2001110	
ORIGINALFORMAT: A1		REV	

