


2025-01-23 14:25:29 \\AL-AG-FS\RedirectedFolders\mkkaeb\My Documents\A-00_V20001_mkkaeb\arkitektlagst.se.rvt

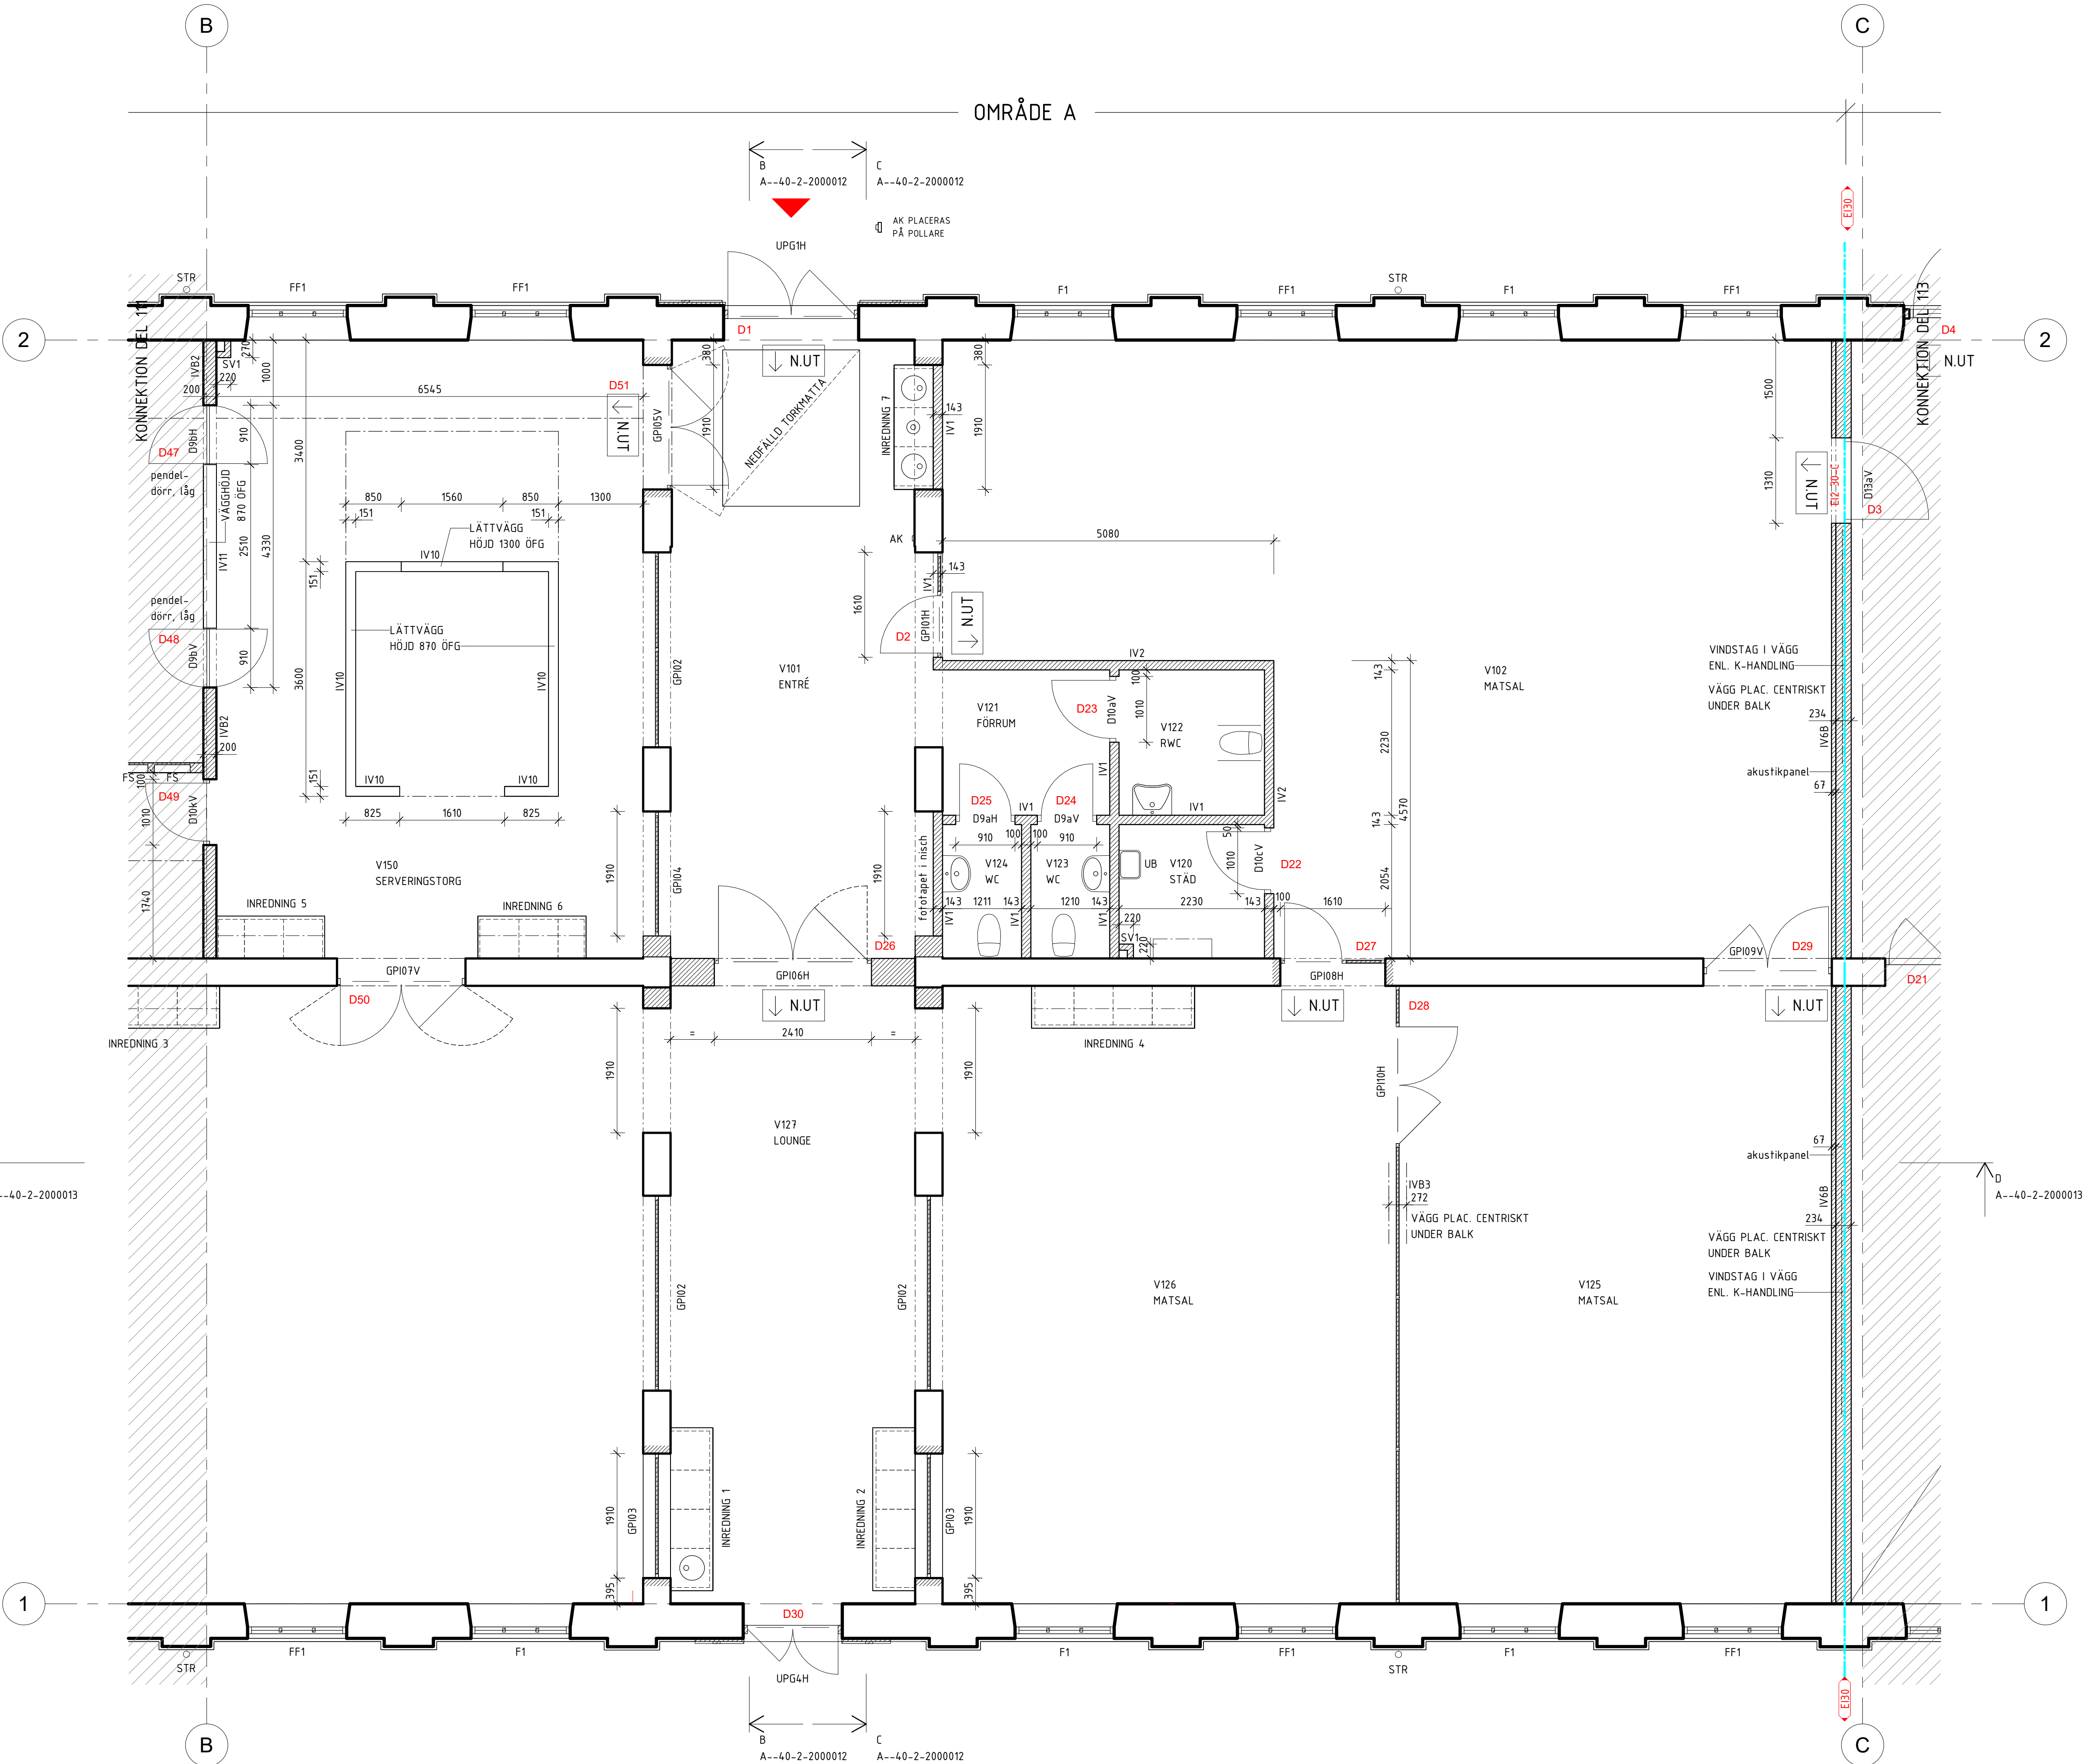


FÖRKLARINGAR

BRANDSKYDD

SE ÄVEN BRANDSKYDDSBESKRIVNING

BRANDCELLSGRÄNS EI30
BRANDCELLSGRÄNS EI60

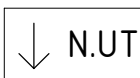

UTRYMNINGSSKYLT
TYP ENL. BRANDSKYDDSBESKRIVNING



ÖVRIGT

- NY VÄGG
- NY ÖPPNING
- VÄGG ENL. STORKÖKSINSULT
- AK = ARMBÅGSKONTAKT
- STR = STUPRÖR (BEFINTLIGT)
- FS = FÖRDELARSKÅP
- Dxx = DÖRRPOSITIONS-NUMMER

HÄNVISNINGAR

NYA VÄGGAR TYPER ENLIGT RITNING A--49-4-2001001
SAMT K-HANDLINGAR.

FÖR STORKÖKSANLÄGGNING, SE RITNING SK-46-1-2001110,
SK-46-1-2001111, SK-46-4-0000001 SAMT UTRUSTNINGSLISTA.

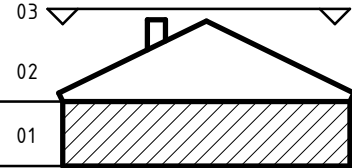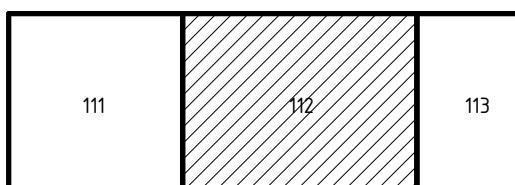ÄNDRING AVSER		DATUM	SIGN
FÖRFRÅGNINGSUNDERLAG			
 HELSINGBORG FASTIGHETSFÖRVALTNINGEN			
FASTIGHET			
ORIENTEN 6			
RÖNNOWSKA SKOLAN, NYTT KÖK OCH MATSAL			
OBJEKTSNR	BYGGNADS-ID	PROJEKTSNR	
1457	5-266088	60095	
BYGGNAD			
1457-20 - HUS V (BYGGNAD 449)			
ORIENTERINGSGRÄNS			
PLAN 03			
			
DEL			
			
VÄSTRA SANDGATAN			
(A) ARKITEKTLAGET SKÅNE AB		T: 042-19 96 00	
BR FIRETECH ENGINEERING EMRON AB		T: 010-150 14 00	
E DEVELCON AB		T: 079-020 27 02	
K ÅKERMANS INGENJÖRSBYRÅ AB		T: 042-12 00 10	
M TYRÉNS AB		T: 010-452 20 00	
S SWECO SVERIGE AB		T: 08-695 60 00	
SK STORKÖKSVISION		T: 040-744 29	
V SWECO SVERIGE AB		T: 08-695 60 00	
W SWECO SVERIGE AB		T: 08-695 60 00	
UPPDRAGSNR		ANSVARIG	
22063.00		BRANISLAV KUZMANOVIC	
DATUM	RITAD/KONSTR AV	HANDLAGGARE	SYSTEMBETECKNING
2025-01-27	MB	BK	40-1
HUS 20			
BOTTENVÅNING, DEL 112			
-			
-			
SKALA	NUMMER		
1 : 50	A--40-1-2001112		
			REV