


2025-01-23 14:25:49 \\ALAG-FS\redirected\Folders\mikaeb\My Documents\A-00_V20001_mikaeb\arkitektlaget.se.rvt

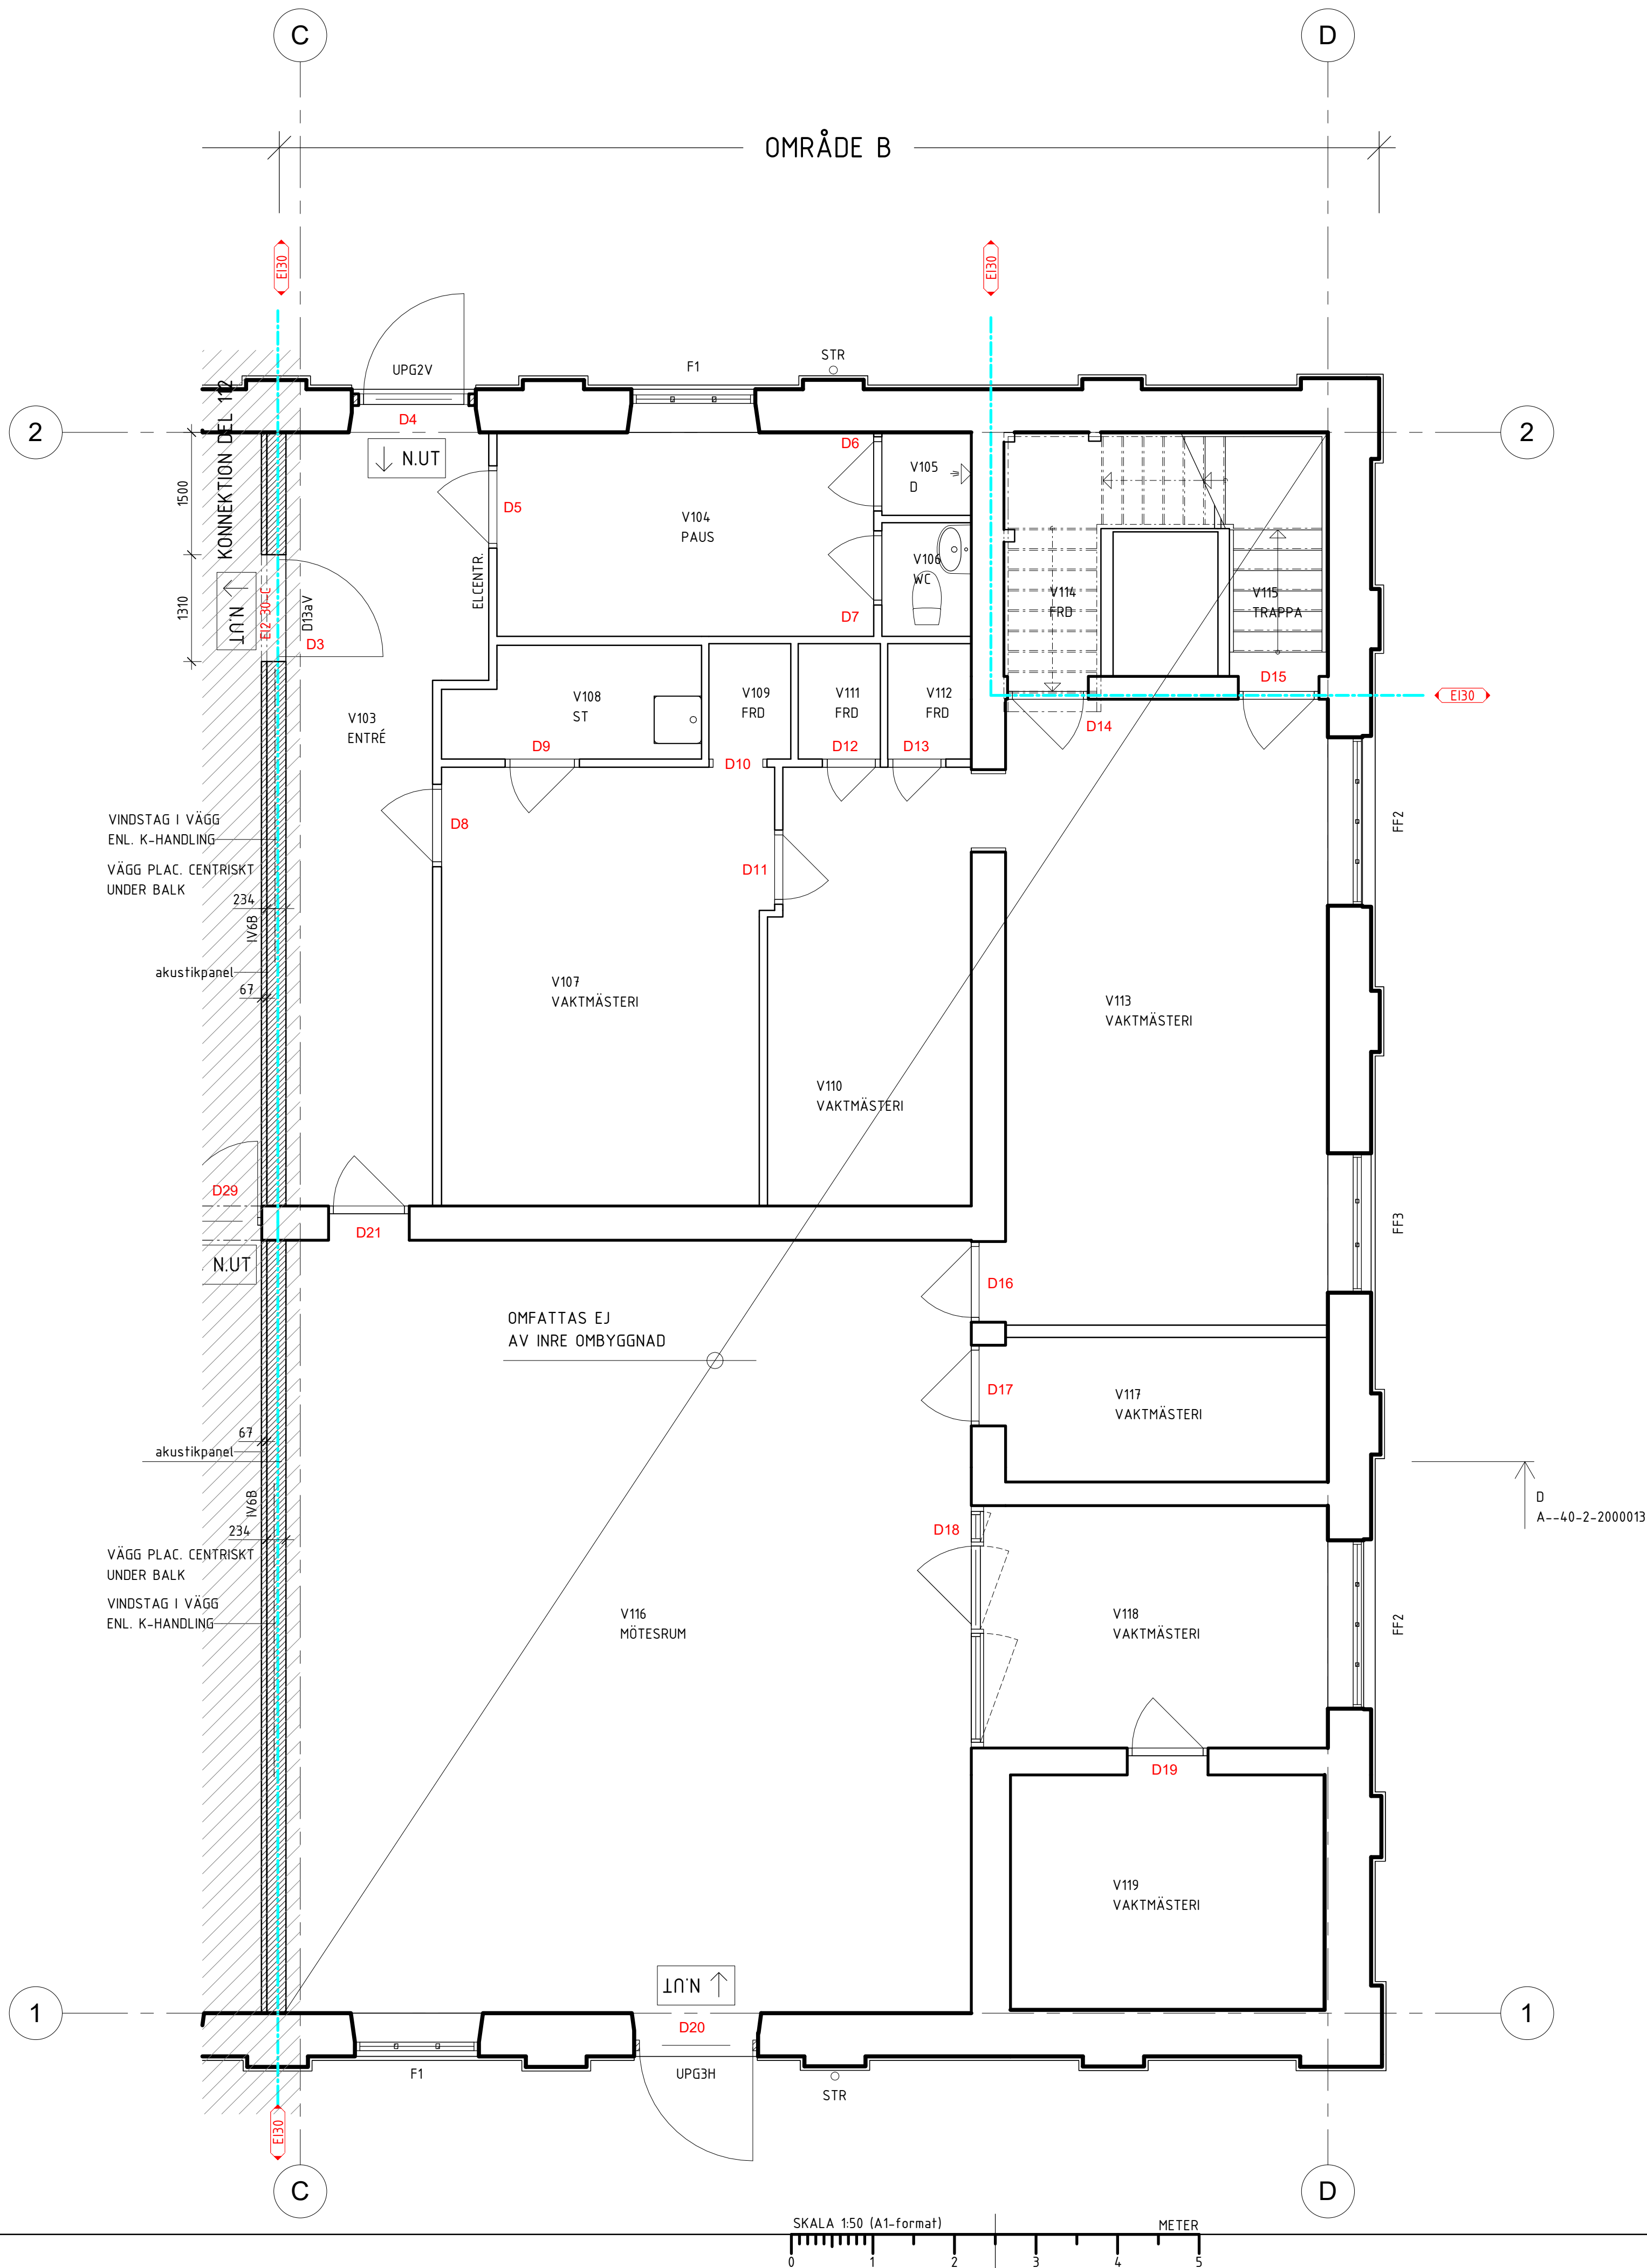


FÖRKLARINGAR

BRANDSKYDD

SE ÄVEN BRANDSKYDDSBESKRIVNING

BRANDCELLSGRÄNS EI30
BRANDCELLSGRÄNS EI60

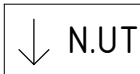

UTRYMNINGSSKYLT
TYP ENL. BRANDSKYDDSBESKRIVNING



ÖVRIGT

- NY VÄGG
- NY ÖPPNING
- VÄGG ENL. STORKÖKSCONSULT
- AK = ARMBÅGSKONTAKT
- STR = STUPRÖR (BEFINTLIGT)
- FS = FÖRDELARSKÅP
- Dxx = DÖRRPOSITIONS-NUMMER

HÄNVISNINGAR

NYA VÄGGAR TYPER ENLIGT RITNING A--49-4-2001001
SAMT K-HANDLINGAR.

FÖR STORKÖKSANLÄGGNING, SE RITNING SK-46-1-2001110,
SK-46-1-2001111, SK-46-4-0000001 SAMT UTRUSTNINGSLISTA.

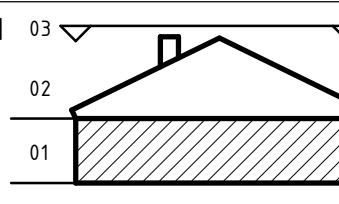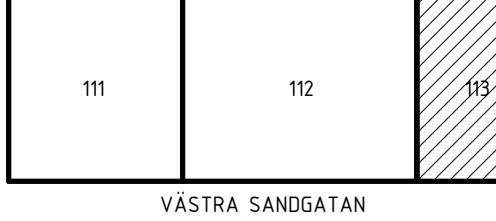BET		ÄNDRING AVSER		DATUM	SIGN
FÖRFRÅGNINGSUNDERLAG					
		HELSINGBORG FASTIGHETSFÖRVALTNINGEN			
FASTIGHET					
ORIENTEN 6					
RÖNNOWSKA SKOLAN, NYTT KÖK OCH MATSAL					
OBJEKTSNR	BYGGNADS-ID		PROJEKTNR		
1457	5-266088		60095		
BYGGNAD					
1457-20 - HUS V (BYGGNAD 449)					
ORIENTERINGSFIGUR					
PLAN		03			
DEL		02			
		01			
					
VÄSTRA SANDGATAN					
A	ARKITEKTLAGET SKÅNE AB			T: 042-19 96 00	
BR	FIRETECH ENGINEERING EMRON AB			T: 010-150 14 00	
E	DEVELCON AB			T: 079-020 27 02	
K	ÅKERMANS INGENJÖRSBYRÅ AB			T: 042-12 00 10	
M	TYRÉNS AB			T: 010-452 20 00	
S	SWECO SVERIGE AB			T: 08-695 60 00	
SK	STORKÖKSVISION			T: 040-744 29	
V	SWECO SVERIGE AB			T: 08-695 60 00	
W	SWECO SVERIGE AB			T: 08-695 60 00	
UPPDRAGSNR		ANSVARIG			
22063_00		BRANISLAV KUZMANOVIC			
DATUM		RITAD/KONSTR AV		HANDLAGGARE	
2025-01-27		MB		BK	
				SYSTEMBETEKNING	
				40-1	
HUS 20					
BOTTENVÅNING, DEL 113					
-					
-					
SKALA		NUMMER		REV	
1 : 50		A--40-1-2001113			

ORIGINALFORMAT: A1