


2025-01-23 14:26:37 \\AL-AG-FS\Redirekted\Folders\mikaeb\My Documents\A--00_V20001_mikaeb\arkitektlagst.se.rvt

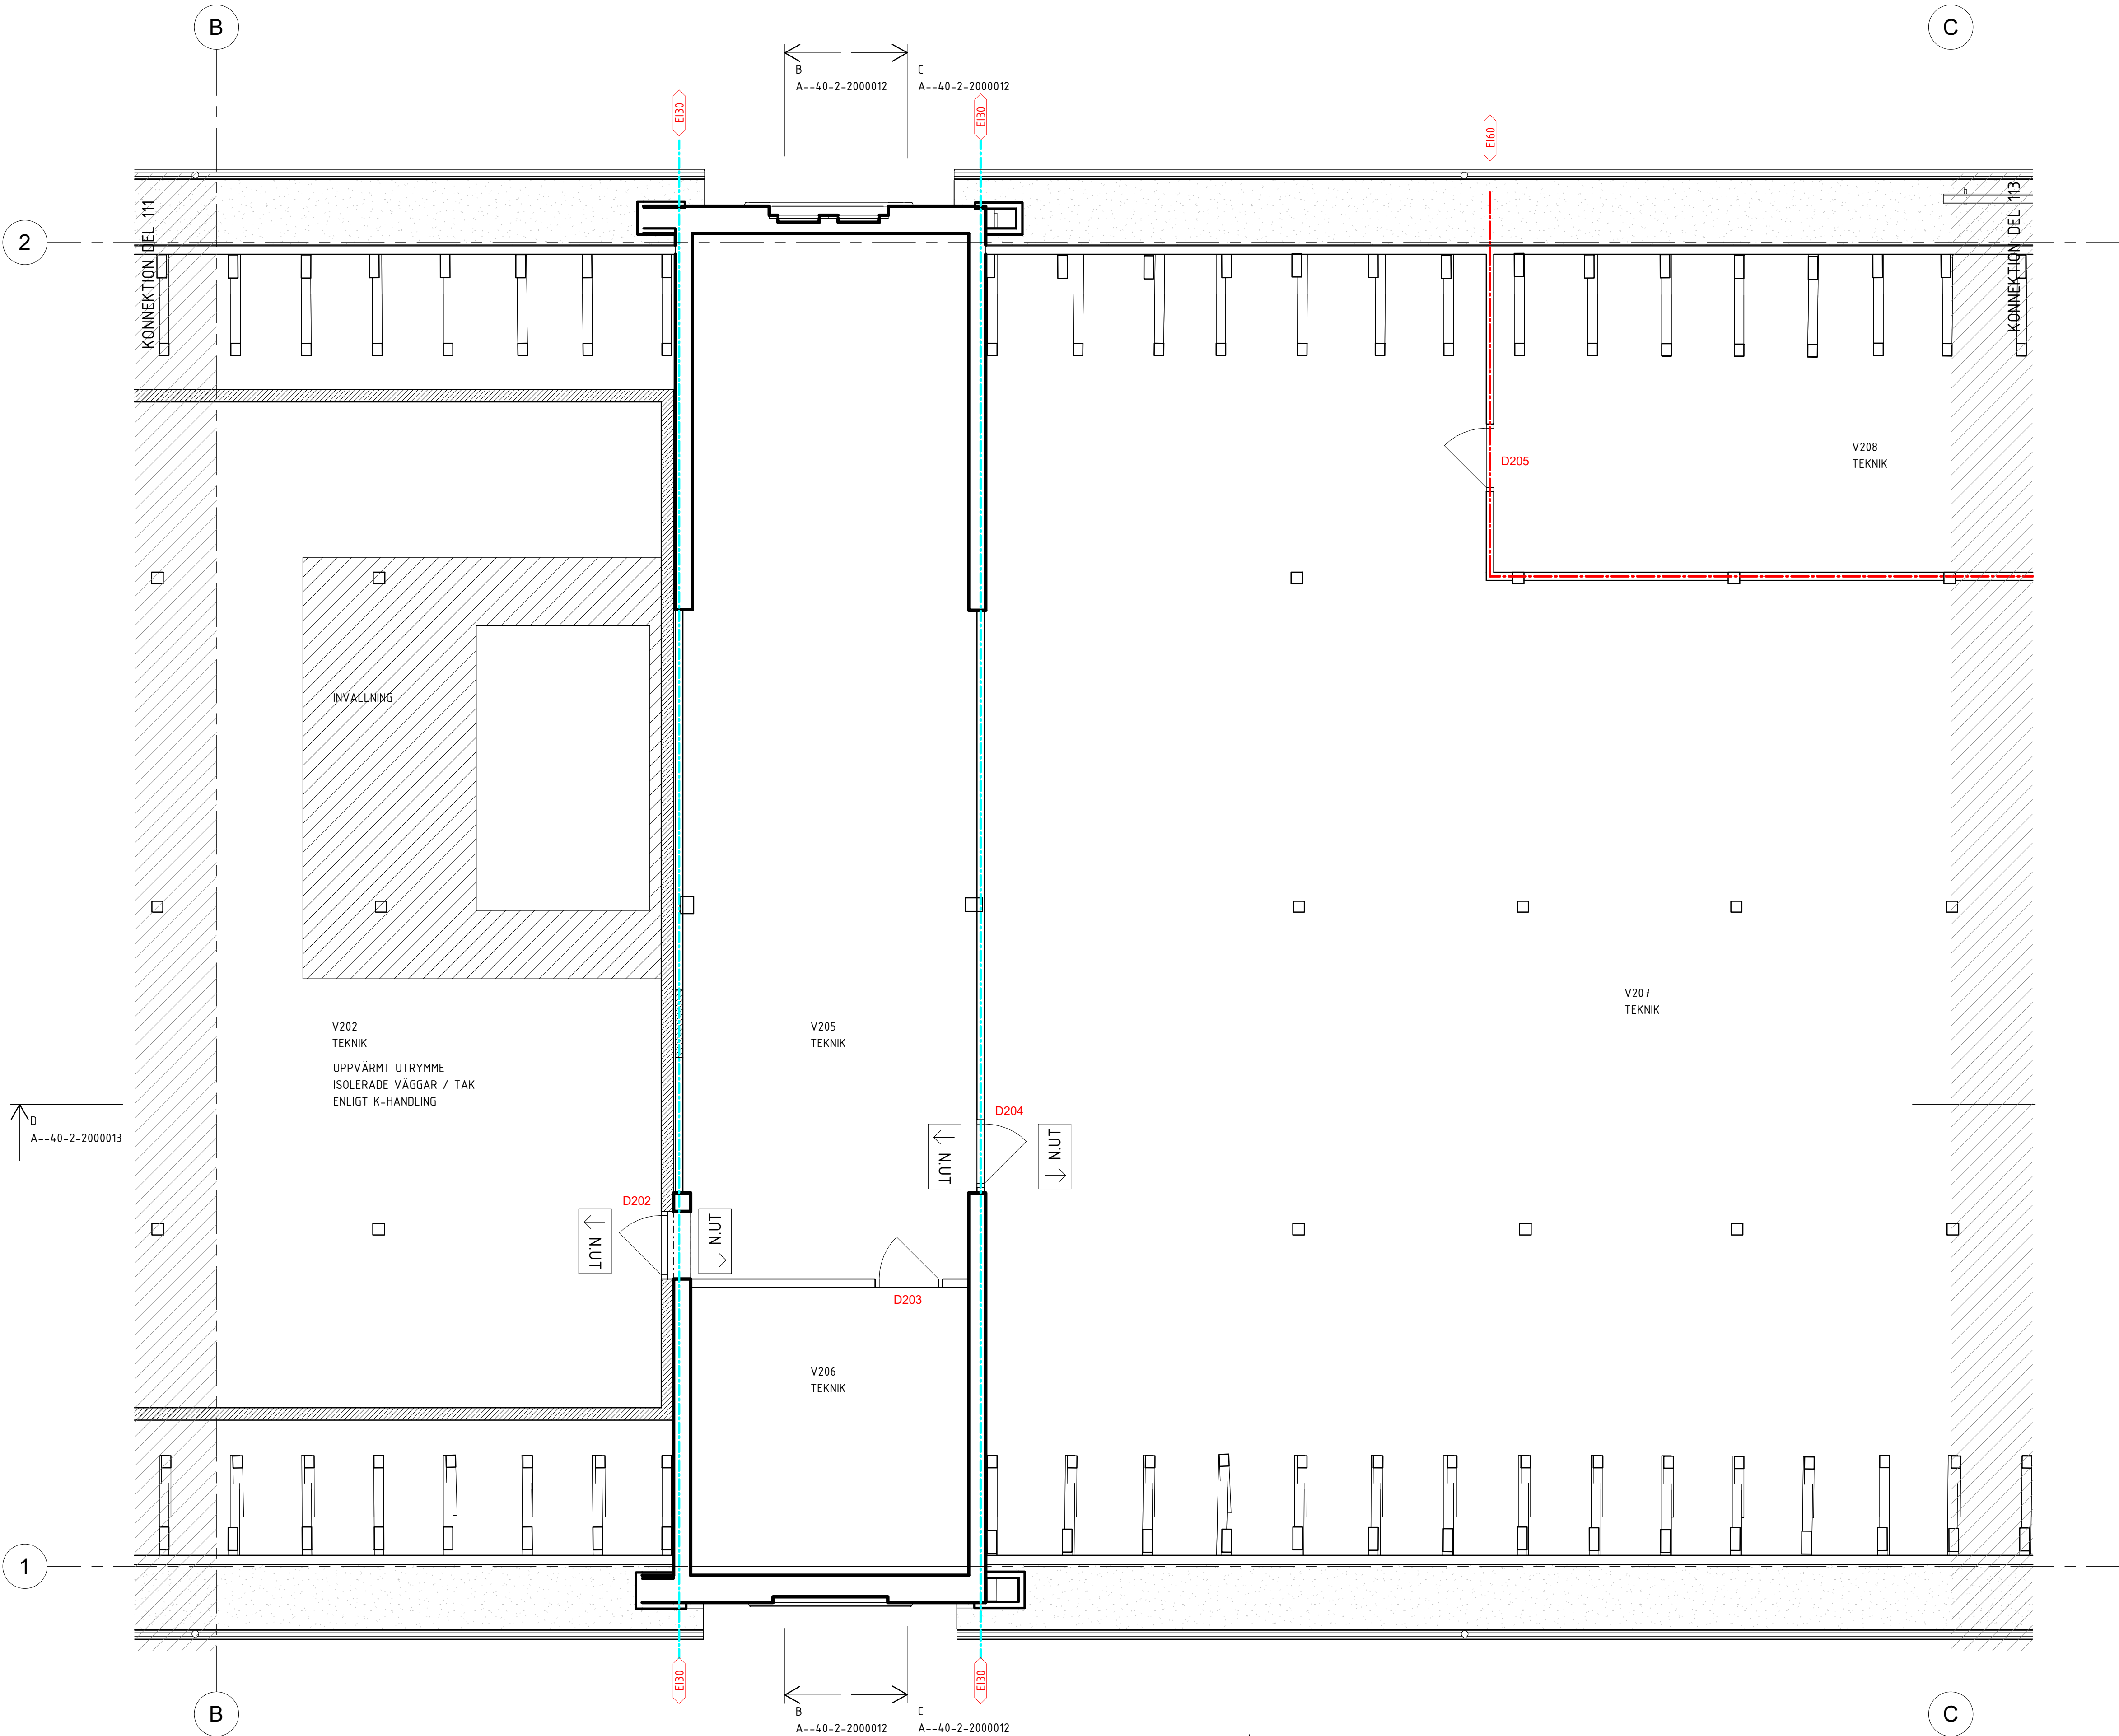


FÖRKLARINGAR

BRANDSKYDD

SE ÄVEN BRANDSKYDDSBESKRIVNING

BRANDCELLSGRÄNS EI30
BRANDCELLSGRÄNS EI60

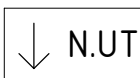

UTRYMNINGSSKYLT
TYP ENL. BRANDSKYDDSBESKRIVNING


ÖVRIGT

- NY VÄGG
- NY ÖPPNING
- VÄGG ENL. STORKÖKSCONSULT
- AK = ARMBÅGSKONTAKT
- STR = STUPRÖR (BEFINTLIGT)
- FS = FÖRDELARSKÅP
- Dxx = DÖRRPOSITIONS-NUMMER

HÄNVISNINGAR

NYA VÄGGAR TYPER ENLIGT RITNING A--49-4-2001001
SAMT K-HANDLINGAR.

FÖR STORKÖKSANLÄGGNING, SE RITNING SK-46-1-2001110,
SK-46-1-2001111, SK-46-4-0000001 SAMT UTRUSTNINGSLISTA.

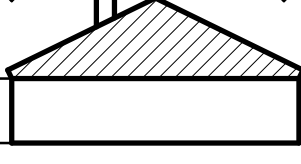BET		ÄNDRING AVSER		DATUM		SIGN	
FÖRFRÅGNINGSUNDERLAG							
		HELSINGBORG FASTIGHETSFÖRVALTNINGEN					
FASTIGHET							
ORIENTEN 6							
RÖNNOWSKA SKOLAN, NYTT KÖK OCH MATSAL							
OBJEKTSNR		BYGGNADS-ID		PROJEKTNR			
1457		5-266088		60095			
BYGGNAD							
1457-20 – HUS V (BYGGNAD 449)							
ORIENTERINGSFIGUR							
PLAN				03			
				02			
				01			
DEL							
							
VÄSTRA SANDGATAN							
(A)		ARKITEKTLAGET SKÅNE AB			T: 042-19 96 00		
BR		FIRETECH ENGINEERING EMRON AB			T: 010-150 14 00		
E		DEVELCON AB			T: 079-020 27 02		
K		ÅKERMANS INGENJÖRSBYRÅ AB			T: 042-12 00 10		
M		TYRÉNS AB			T: 010-452 20 00		
S		SWECO SVERIGE AB			T: 08-695 60 00		
SK		STORKÖKSVISION			T: 040-744 29		
V		SWECO SVERIGE AB			T: 08-695 60 00		
W		SWECO SVERIGE AB			T: 08-695 60 00		
UPPDRAGSNR		ANSVARIG					
22063.00		BRANISLAV KUZMANOVIC					
DATUM		RITAD/KONSTR AV		HANDLAGGARE		SYSTEMBETECKNING	
2025-01-27		MB		BK		40-1	
HUS 20							
VINDSPLAN, DEL 112							
-							
-							
SKALA		NUMMER				REV	
1 : 50		A--40-1-2002112					

ORIGINALFORMAT: A1