
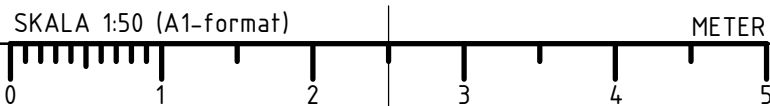


2025-01-23 14:26:52 \\ALAG-FS\RedirectedFolders\mikaeb\My Documents\A-00_V2001_mikaeb\arkitektlagat.se.rvt

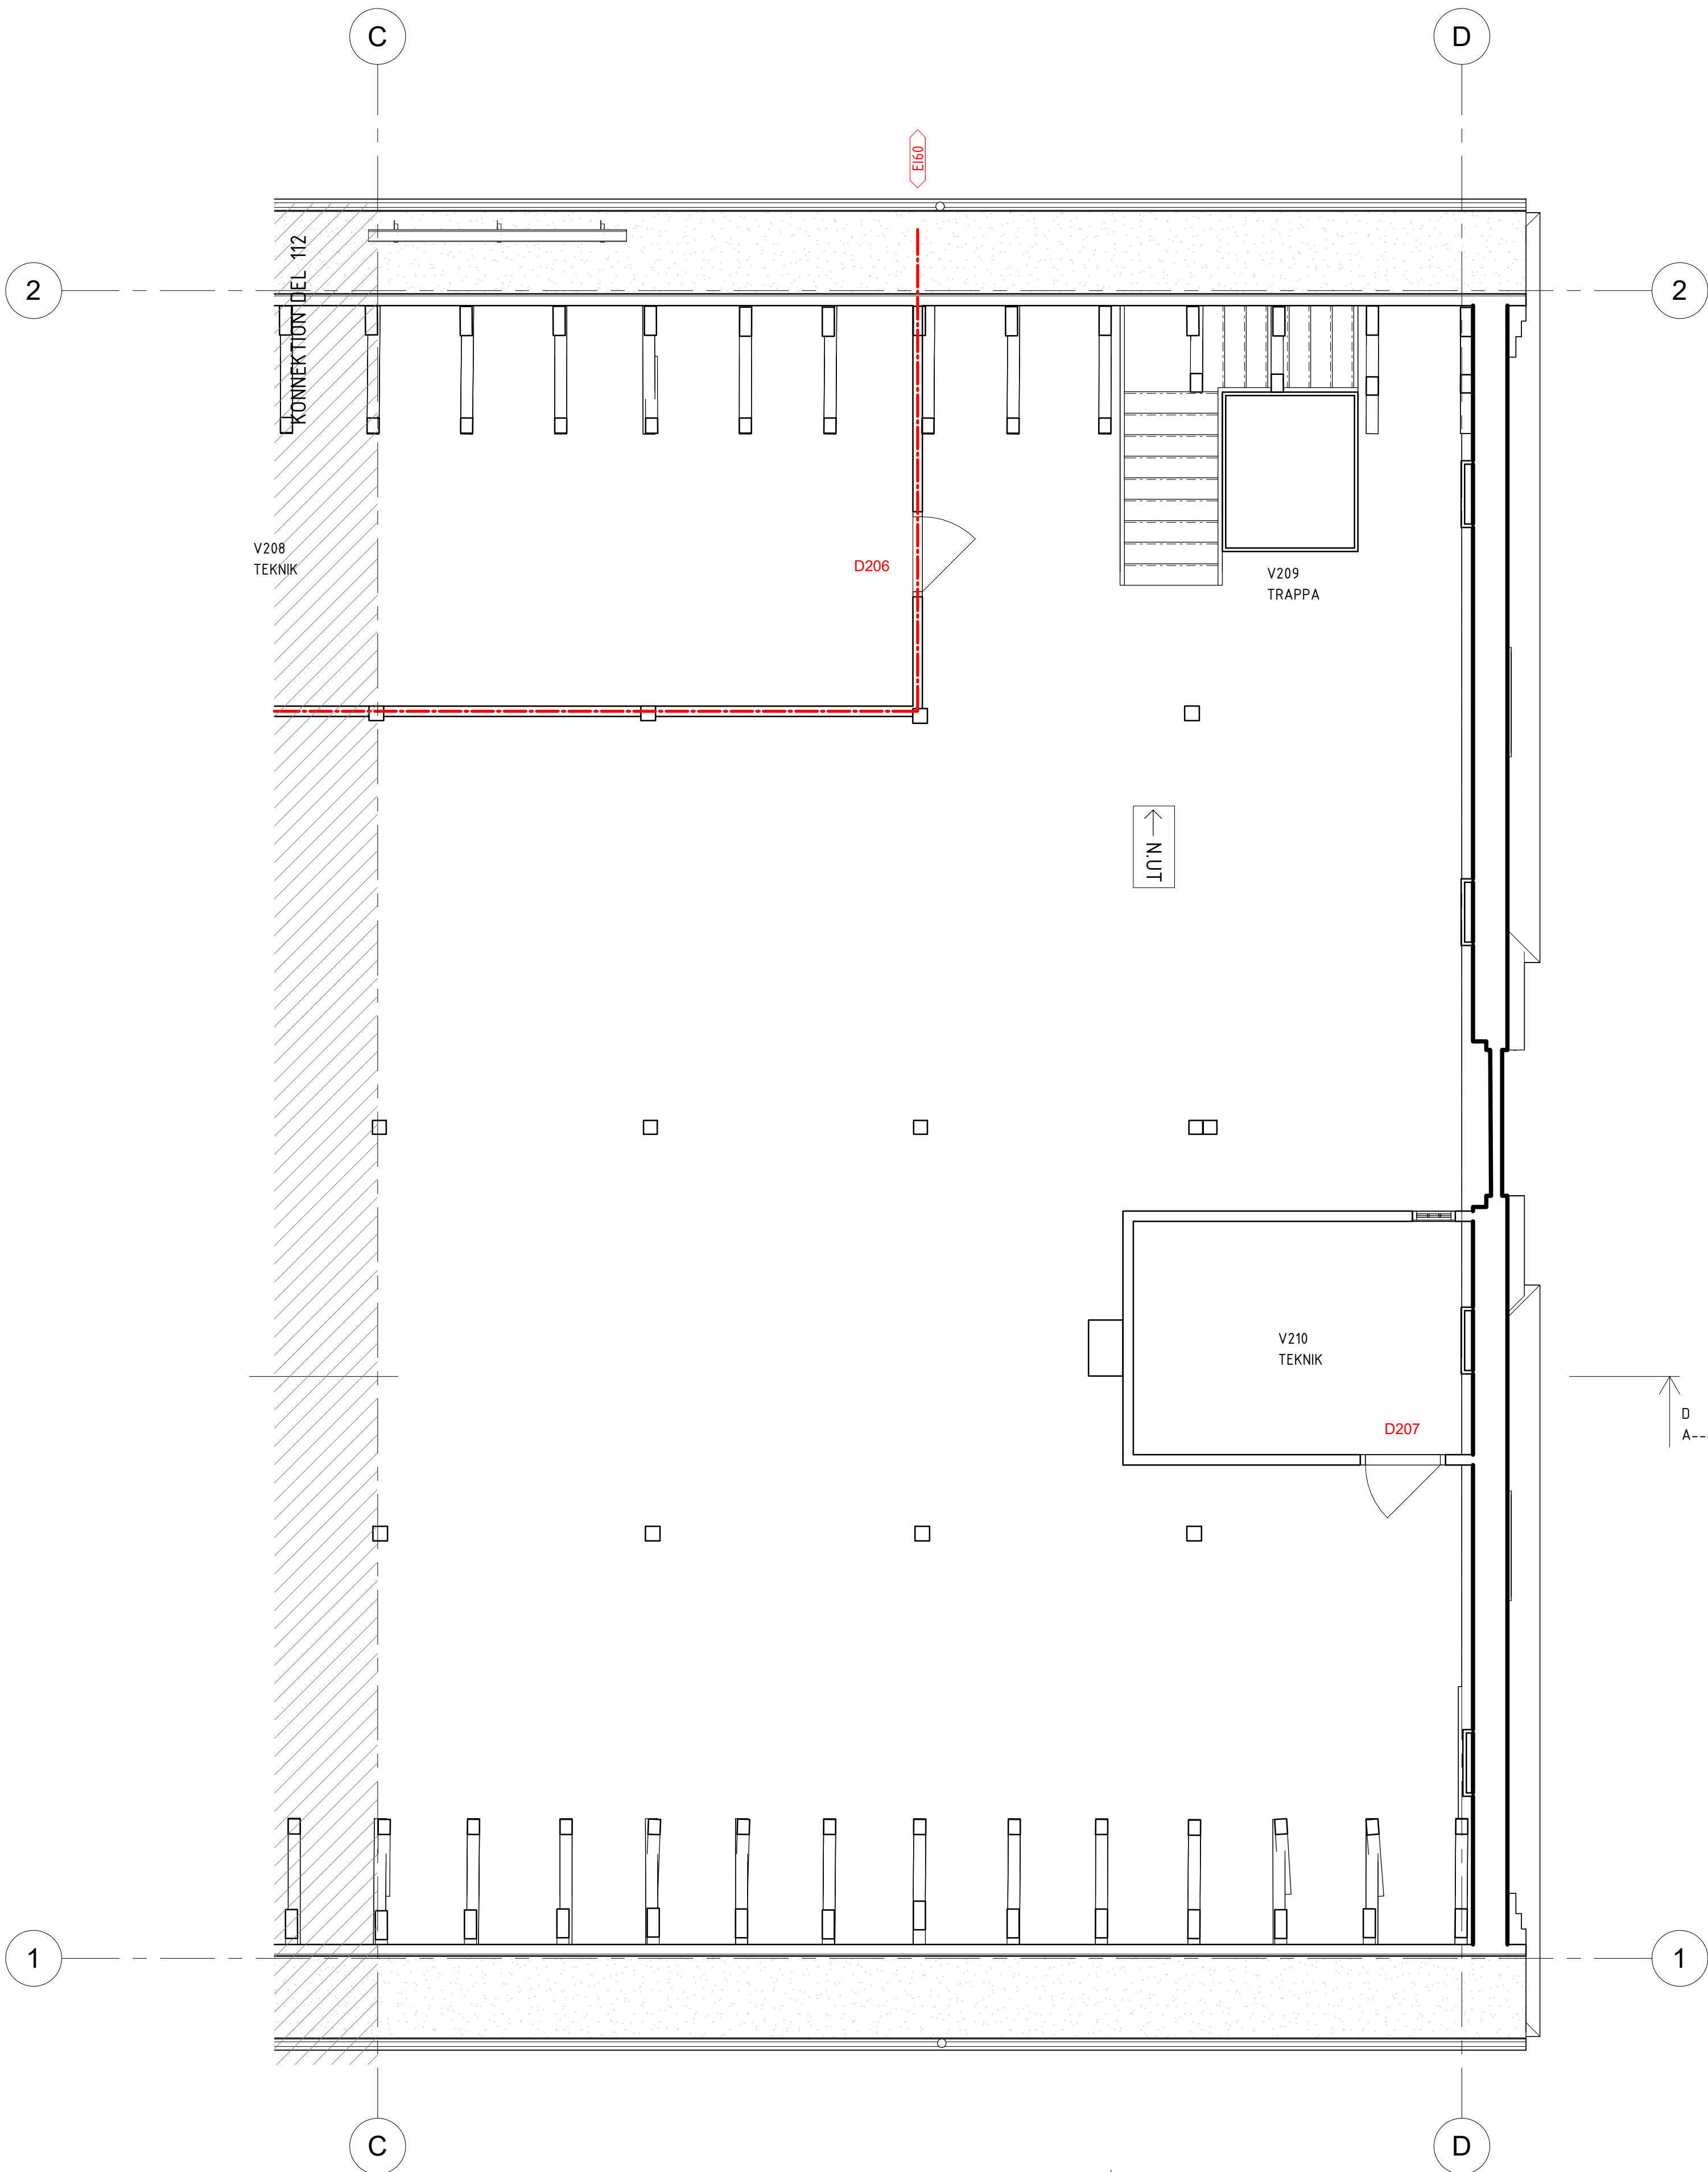


FÖRKLARINGAR

BRANDSKYDD

SE ÄVEN BRANDSKYDDSBESKRIVNING

BRANDCELLSGRÄNS EI30
BRANDCELLSGRÄNS EI60

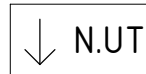

NUT

UTRYMNINGSSKYL T
TYP ENL. BRANDSKYDDSBESKRIVNING



ÖVRIGT

- = NY VÄGG
- = NY ÖPPNING
- = VÄGG ENL. STORKÖKSCONSULT
- AK = ARMBÅGSKONTAKT
- STR = STUPRÖR (BEFINTLIGT)
- FS = FÖRDELARSKÅP
- Dxx = DÖRRPOSITIONS-NUMMER

HÄNVISNINGAR

NYA VÄGGAR TYPER ENLIGT RITNING A--49-4-2001001
SAMT K-HANDLINGAR.

FÖR STORKÖKSANLÄGGNING, SE RITNING SK-46-1-2001110,
SK-46-1-2001111, SK-46-4-0000001 SAMT UTRUSTNINGSLISTA.

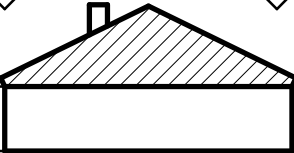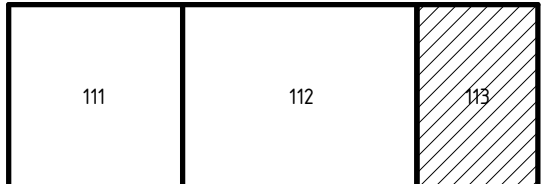BET	ÄNDRING AVSER		DATUM	SIGN
FÖRFRÅGNINGSUNDERLAG				
 HELSINGBORG FASTIGHETSFÖRVALTNINGEN				
FASTIGHET				
ORIENTEN 6				
RÖNNOWSKA SKOLAN, NYTT KÖK OCH MATSAL				
OBJEKTSNR	BYGGNADS-ID		PROJEKTSNR	
1457	5-266088		60095	
BYGGNAD				
1457-20 – HUS V (BYGGNAD 449)				
ORIENTERINGSFIGUR				
PLAN 03				
DEL				
VÄSTRA SANDGATAN				
A	ARKITEKTLAGET SKÅNE AB		T: 042-19 96 00	
BR	FIRETECH ENGINEERING EMRON AB		T: 010-150 14 00	
E	DEVELCON AB		T: 079-020 27 02	
K	ÅKERMANS INGENJÖRSBYRÅ AB		T: 042-12 00 10	
M	TYRÉNS AB		T: 010-452 20 00	
S	SWECO SVERIGE AB		T: 08-695 60 00	
SK	STORKÖKSVISION		T: 040-744 29	
V	SWECO SVERIGE AB		T: 08-695 60 00	
W	SWECO SVERIGE AB		T: 08-695 60 00	
UPPDRAGSNR		ANSVARIG		
22063_00		BRANISLAV KUZMANOVIC		
DATUM	RITAD/KONSTR AV	HANDLAGGARE	SYSTEMBETEKNING	
2025-01-27	MB	BK	40-1	
HUS 20				
VINDSPLAN, DEL 113				
-				
-				
-				
SKALA	NUMMER			REV
1 : 50	A--40-1-2002113			

ORIGINALFORMAT: A1