




2025-01-23 14:27:47 \\ALAG-FS\Redirekted\Folders\mikaeb\My Documents\A-00_V20001_mikaeb\arkitektlagd.se.rvt


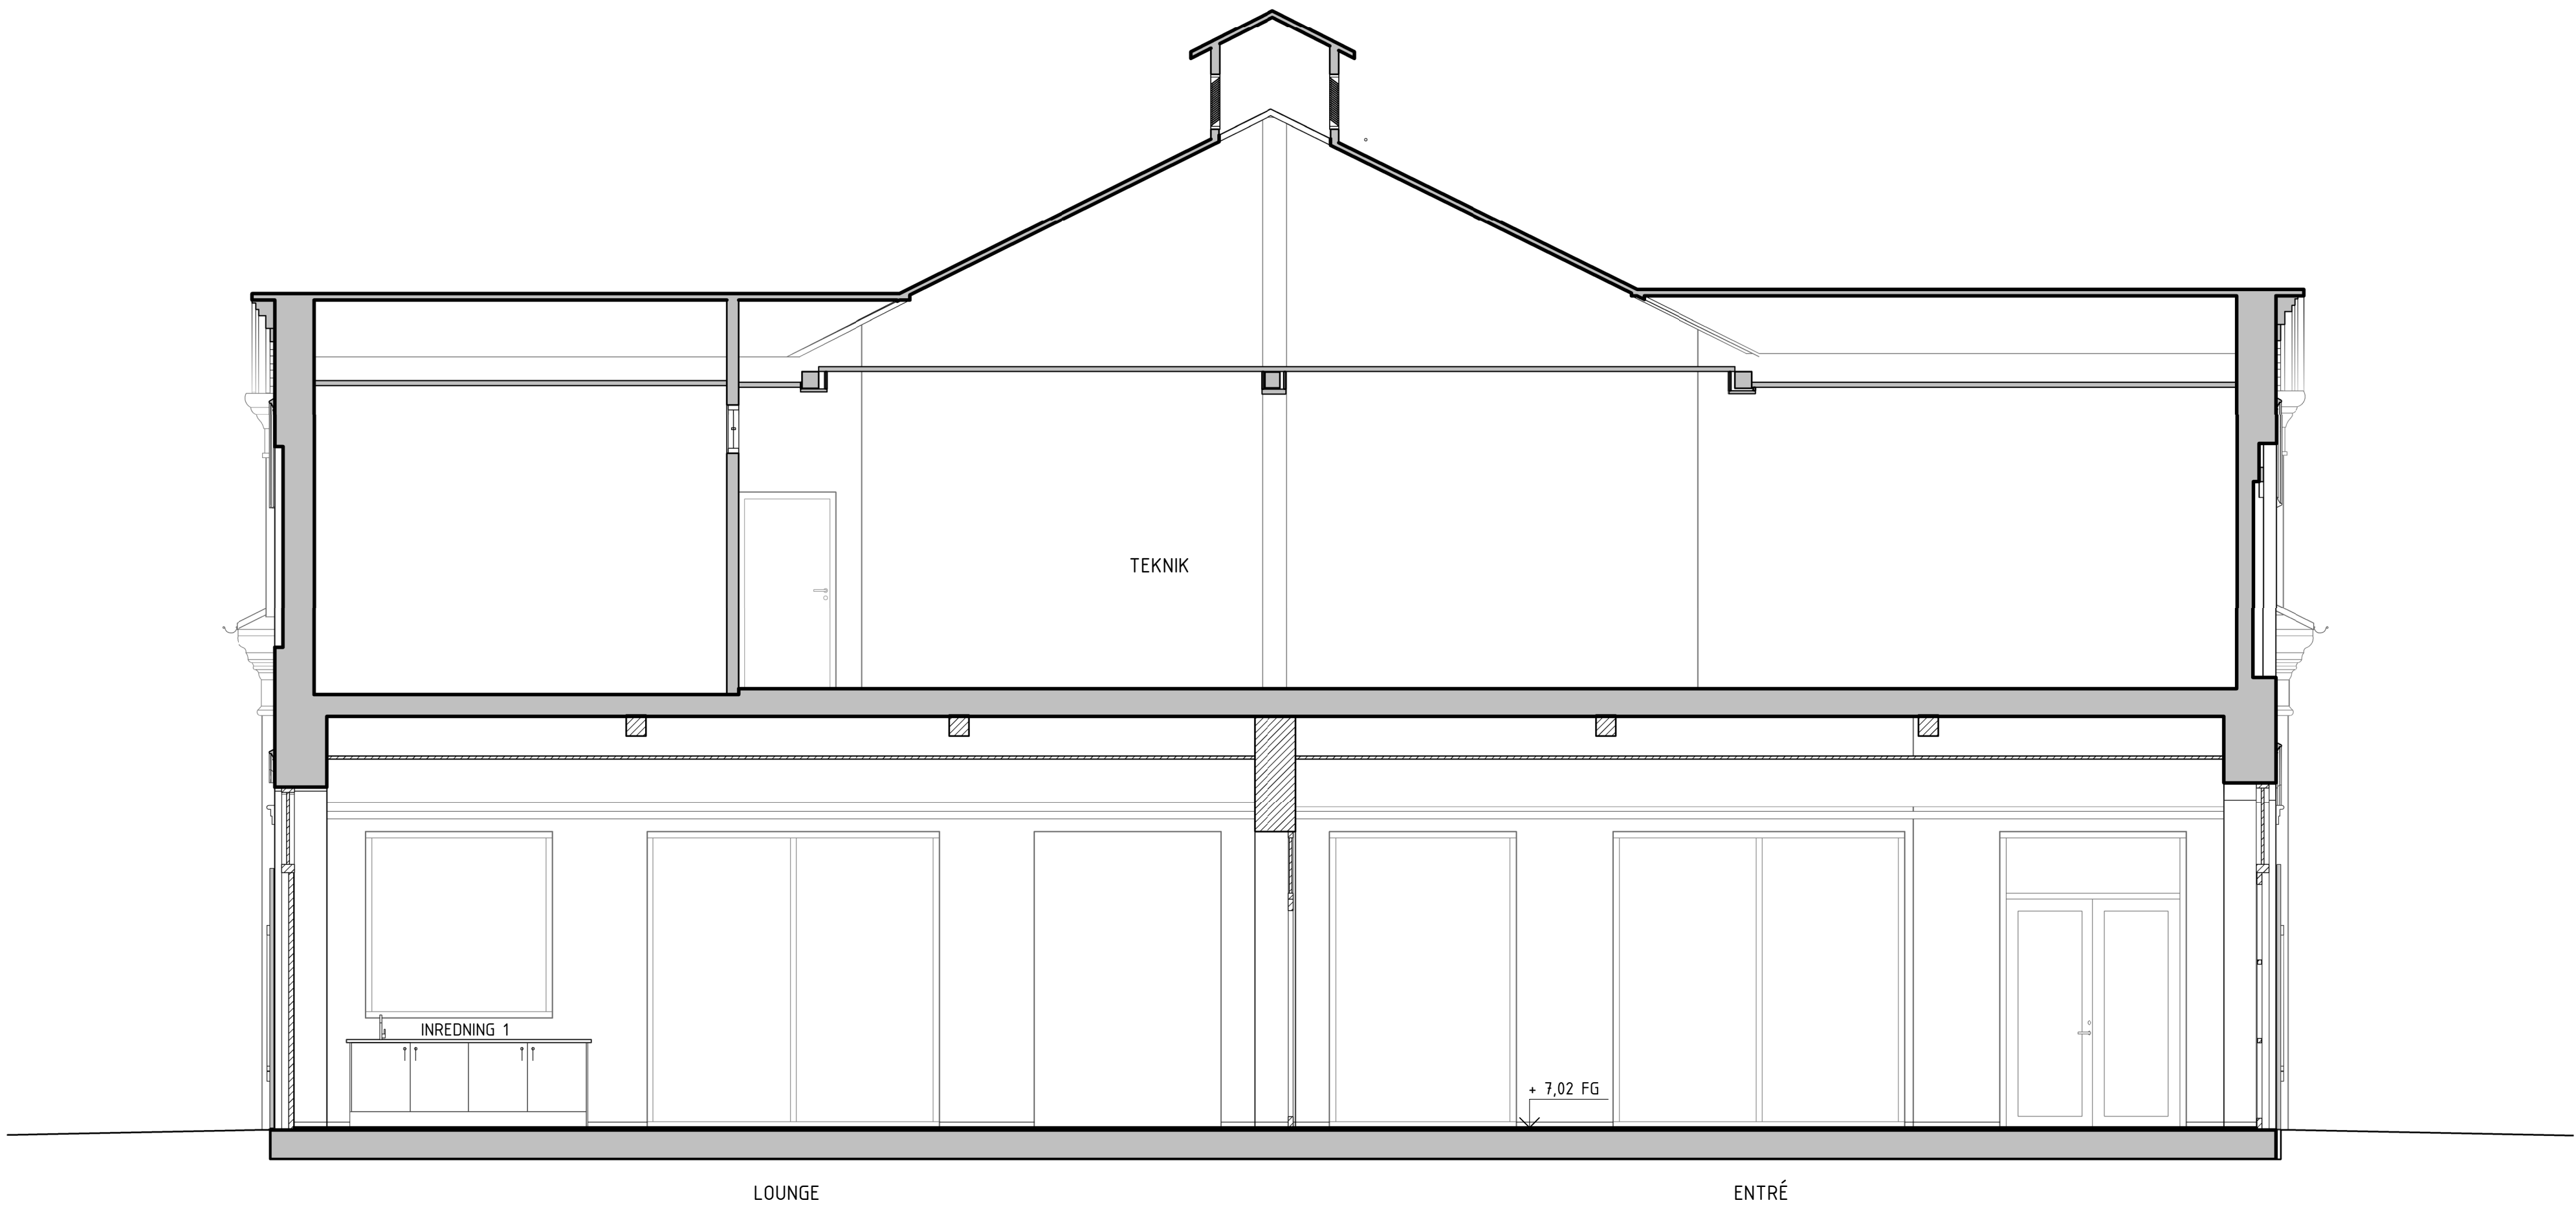


SEKTION B-B

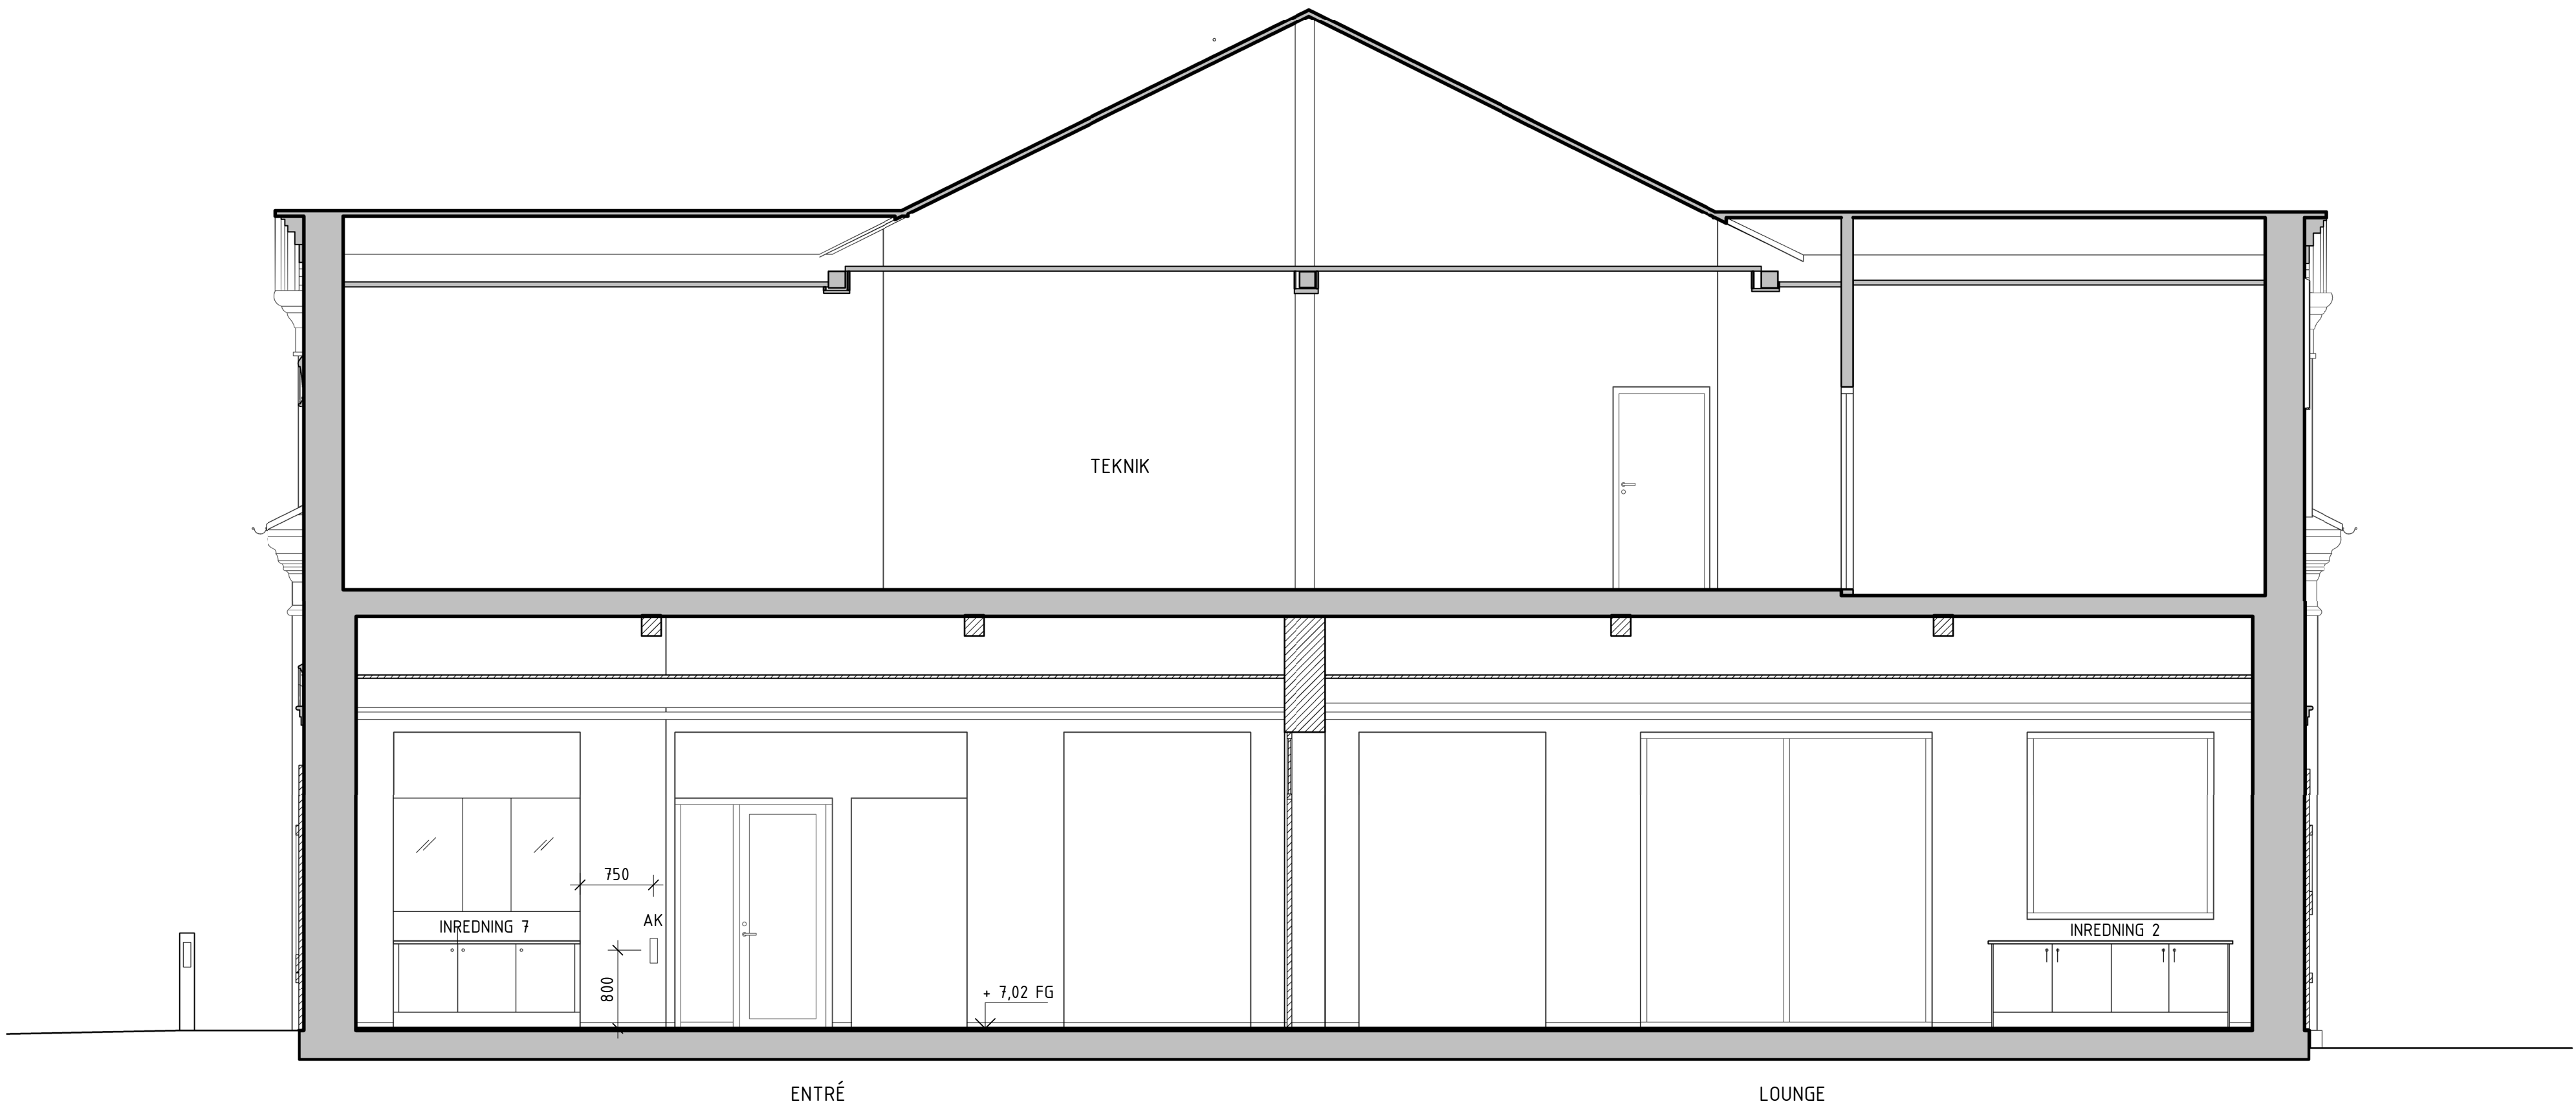

SEKTION C-C

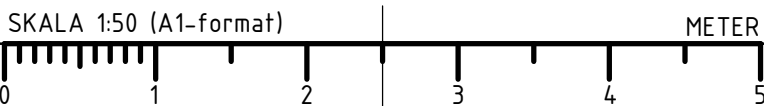

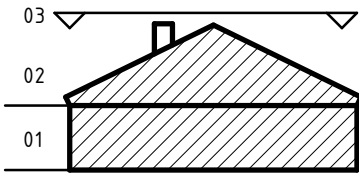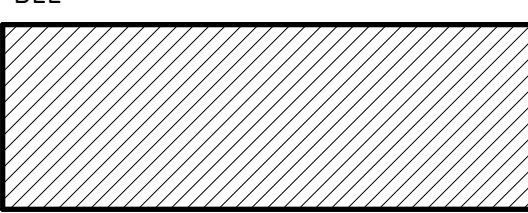BET	ÄNDRING AVSER	DATUM	SIGN																											
FÖRFRÅGNINGSUNDERLAG																														
 HELSINGBORG FASTIGHETSFÖRVALTNINGEN																														
FASTIGHET ORIENTEN 6 RÖNNOWSKA SKOLAN, NYTT KÖK OCH MATSAL																														
OBJEKTSNR 1457	BYGGNADS-ID 5-266088	PROJEKTNR 60095																												
BYGGNAD 1457-20 - HUS V (BYGGNAD 449)																														
ORIENTERINGSGRUPP PLAN 03 																														
DEL  VÄSTRA SANDGATAN																														
<table><tr><td>(A)</td><td>ARKITEKTLAGET SKÅNE AB</td><td>T: 042-19 96 00</td></tr><tr><td>BR</td><td>FIRETECH ENGINEERING EMRON AB</td><td>T: 010-150 14 00</td></tr><tr><td>E</td><td>DEVELCON AB</td><td>T: 079-020 27 02</td></tr><tr><td>K</td><td>ÅKERMANS INGENJÖRSBYRÅ AB</td><td>T: 042-12 00 10</td></tr><tr><td>M</td><td>TYRÉNS AB</td><td>T: 010-452 20 00</td></tr><tr><td>S</td><td>SWECO SVERIGE AB</td><td>T: 08-695 60 00</td></tr><tr><td>SK</td><td>STORKÖKSVISION</td><td>T: 040-744 29</td></tr><tr><td>V</td><td>SWECO SVERIGE AB</td><td>T: 08-695 60 00</td></tr><tr><td>W</td><td>SWECO SVERIGE AB</td><td>T: 08-695 60 00</td></tr></table>				(A)	ARKITEKTLAGET SKÅNE AB	T: 042-19 96 00	BR	FIRETECH ENGINEERING EMRON AB	T: 010-150 14 00	E	DEVELCON AB	T: 079-020 27 02	K	ÅKERMANS INGENJÖRSBYRÅ AB	T: 042-12 00 10	M	TYRÉNS AB	T: 010-452 20 00	S	SWECO SVERIGE AB	T: 08-695 60 00	SK	STORKÖKSVISION	T: 040-744 29	V	SWECO SVERIGE AB	T: 08-695 60 00	W	SWECO SVERIGE AB	T: 08-695 60 00
(A)	ARKITEKTLAGET SKÅNE AB	T: 042-19 96 00																												
BR	FIRETECH ENGINEERING EMRON AB	T: 010-150 14 00																												
E	DEVELCON AB	T: 079-020 27 02																												
K	ÅKERMANS INGENJÖRSBYRÅ AB	T: 042-12 00 10																												
M	TYRÉNS AB	T: 010-452 20 00																												
S	SWECO SVERIGE AB	T: 08-695 60 00																												
SK	STORKÖKSVISION	T: 040-744 29																												
V	SWECO SVERIGE AB	T: 08-695 60 00																												
W	SWECO SVERIGE AB	T: 08-695 60 00																												
<table><tr><td>UPPDRAGSNR 22063_00</td><td colspan="3">ANSVARIG BRANISLAV KUZMANOVIC</td></tr><tr><td>DATUM 2025-01-27</td><td>RITAD/KONSTR AV MB</td><td>HANDLAGGARE BK</td><td>SYSTEMBETEKNING 40-2</td></tr></table>				UPPDRAGSNR 22063_00	ANSVARIG BRANISLAV KUZMANOVIC			DATUM 2025-01-27	RITAD/KONSTR AV MB	HANDLAGGARE BK	SYSTEMBETEKNING 40-2																			
UPPDRAGSNR 22063_00	ANSVARIG BRANISLAV KUZMANOVIC																													
DATUM 2025-01-27	RITAD/KONSTR AV MB	HANDLAGGARE BK	SYSTEMBETEKNING 40-2																											
HUS 20 SEKTION B-B & C-C																														
-																														
-																														
-																														
SKALA 1 : 50	NUMMER A--40-2-2000012		REV																											

ORIGINALFORMAT: A1