



2025-01-23 14:29:28 \\AL-AG-FS\RedirectedFolders\mikaeb\My Documents\A-00_V20001_mikaeb\arkitekt\agt.se.rvt


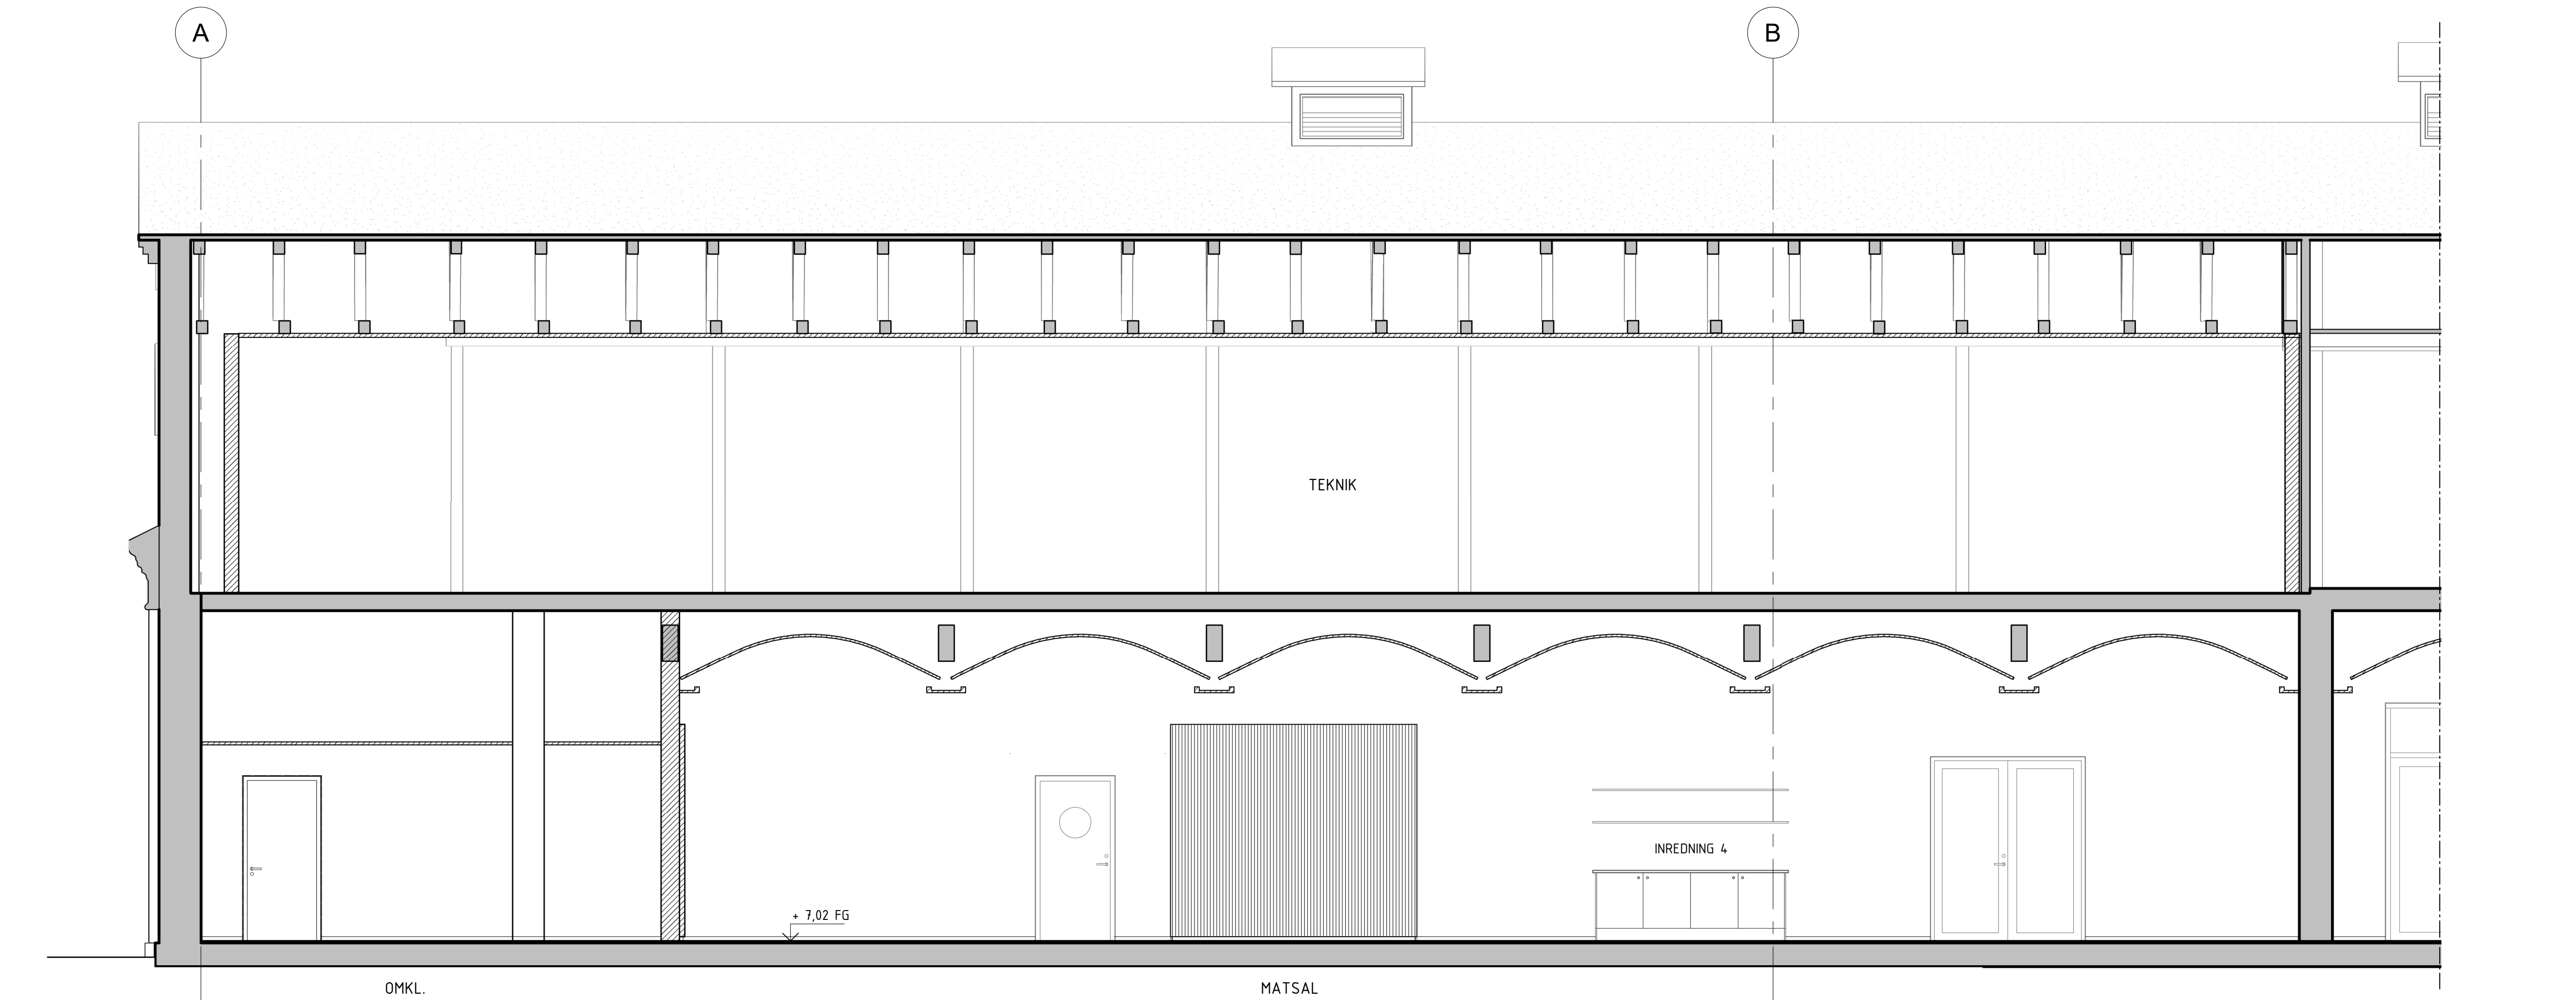


SEKTION D-D (DEL 1)

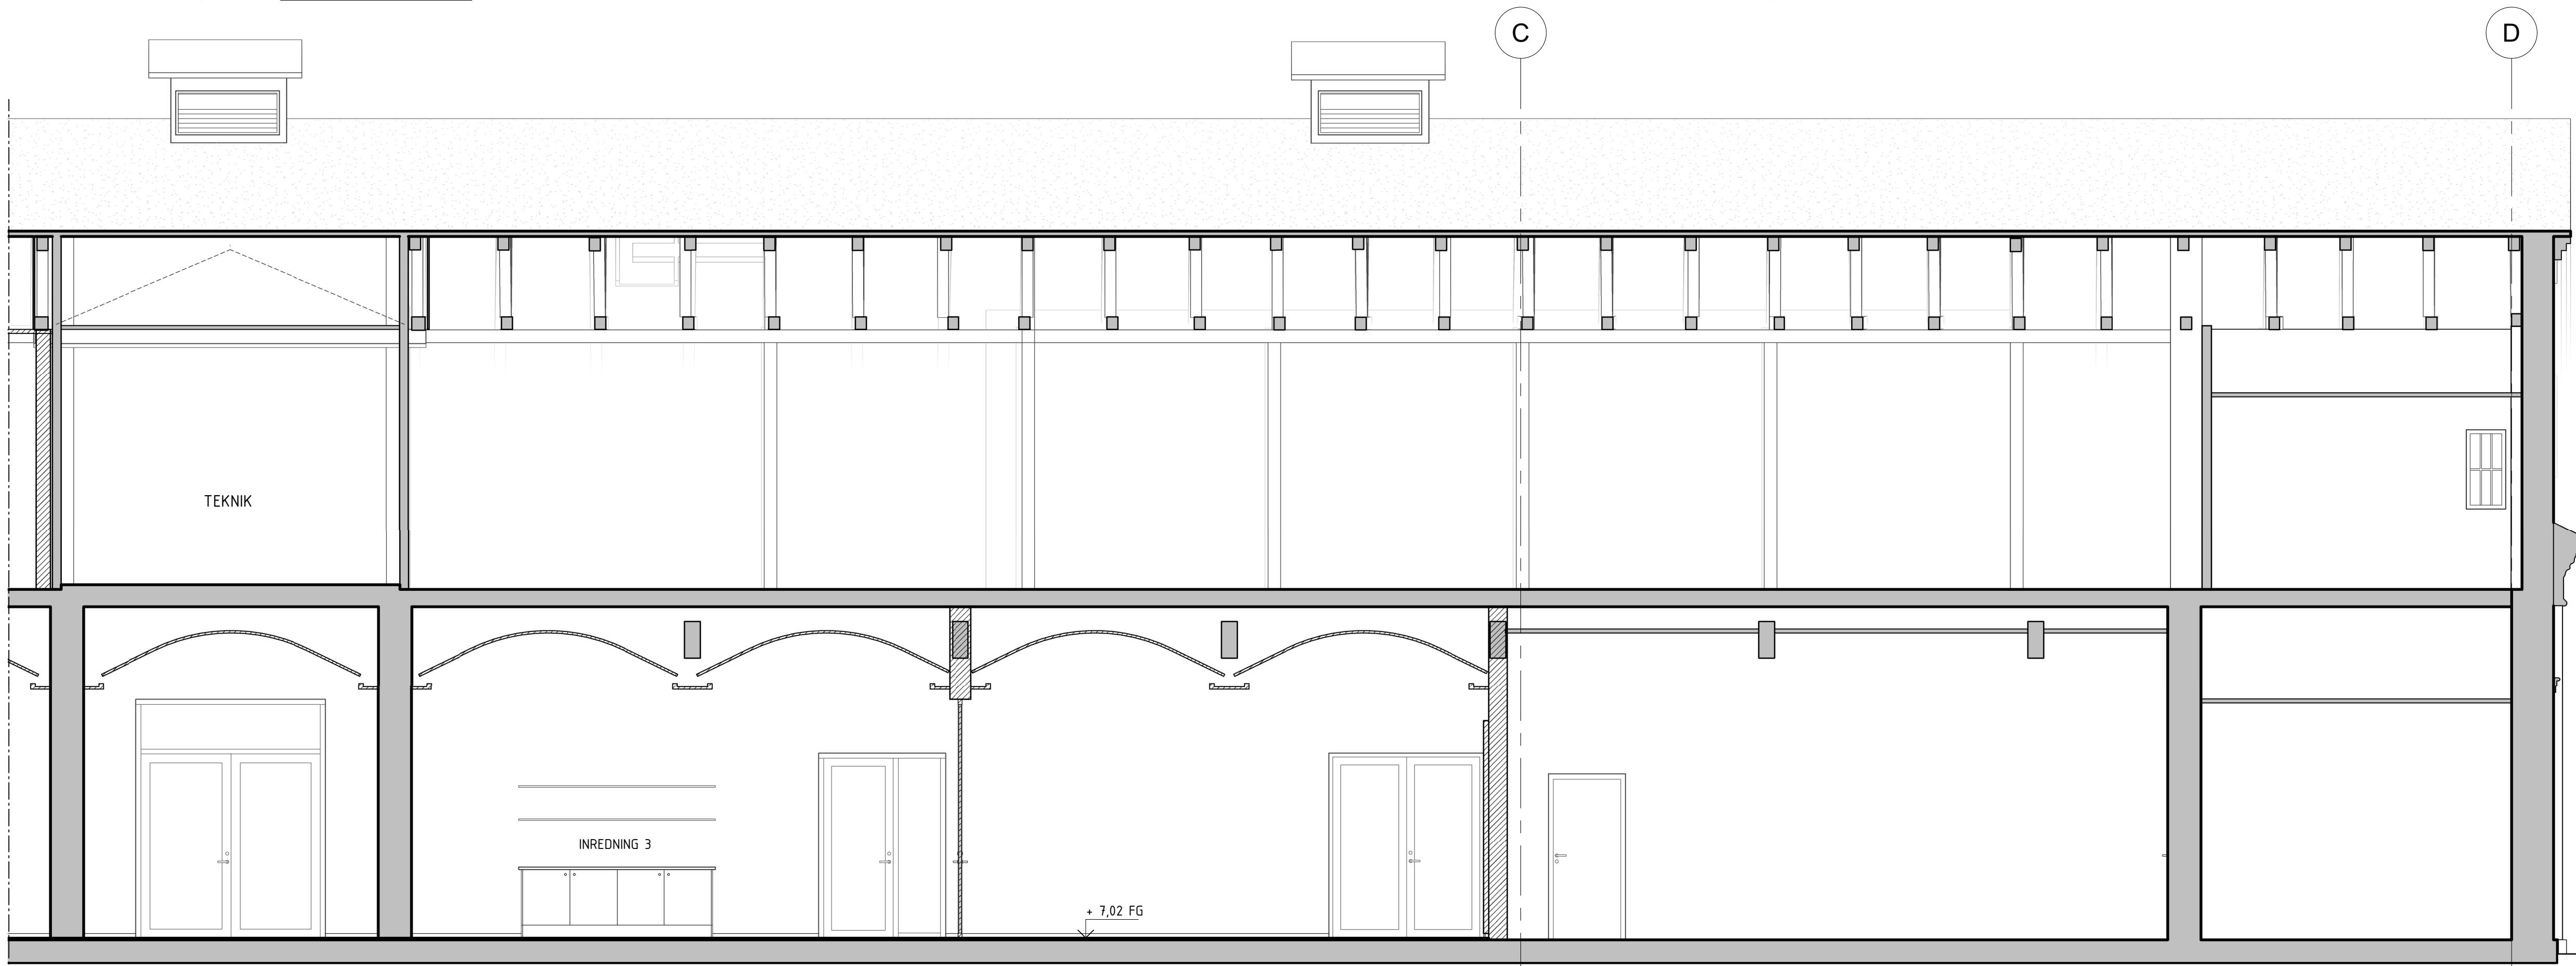

SEKTION D-D (DEL 2)

SKALA 1:50 (A1-format)
0 1 2 3 4 5
METER

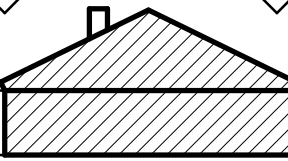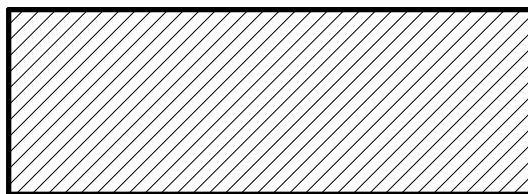BET		ÄNDRING AVSER		DATUM	SIGN
FÖRFRÅGNINGSUNDERLAG					
		HELSINGBORG FASTIGHETSFÖRVALTNINGEN			
FASTIGHET					
ORIENTEN 6					
RÖNNOWSKA SKOLAN, NYTT KÖK OCH MATSAL					
OBJEKTSNR 1457		BYGGNADS-ID 5-266088		PROJEKTNR 60095	
BYGGNAD 1457-20 – HUS V (BYGGNAD 449)					
ORIENTERINGSGRUPP					
PLAN		03			
		02			
		01			
DEL					
					
VÄSTRA SANDGATAN					
(A)		ARKITEKTLAGET SKÅNE AB		T: 042-19 96 00	
BR		FIRETECH ENGINEERING EMRON AB		T: 010-150 14 00	
E		DEVELCON AB		T: 079-020 27 02	
K		ÅKERMANS INGENJÖRSBYRÅ AB		T: 042-12 00 10	
M		TYRÉNS AB		T: 010-452 20 00	
S		SWECO SVERIGE AB		T: 08-695 60 00	
SK		STORKÖKSVISION		T: 040-744 29	
V		SWECO SVERIGE AB		T: 08-695 60 00	
W		SWECO SVERIGE AB		T: 08-695 60 00	
UPPDRAGSNR 22063_00		ANSVARIG BRANISLAV KUZMANOVIC			
DATUM 2025-01-27		RITAD/KONSTR AV MB		HANDLAGGARE BK	
				SYSTEMBETECKNING 40-2	
HUS 20					
SEKTION D-D					
-					
-					
SKALA 1 : 50		NUMMER A--40-2-2000013			REV