


2025-01-23 14:30:44 \\ALAG-FS\Redirekted\Folders\mkkaeb\My Documents\A--00_V20001_mkkaeb\@arkitektlagt.se.rvt

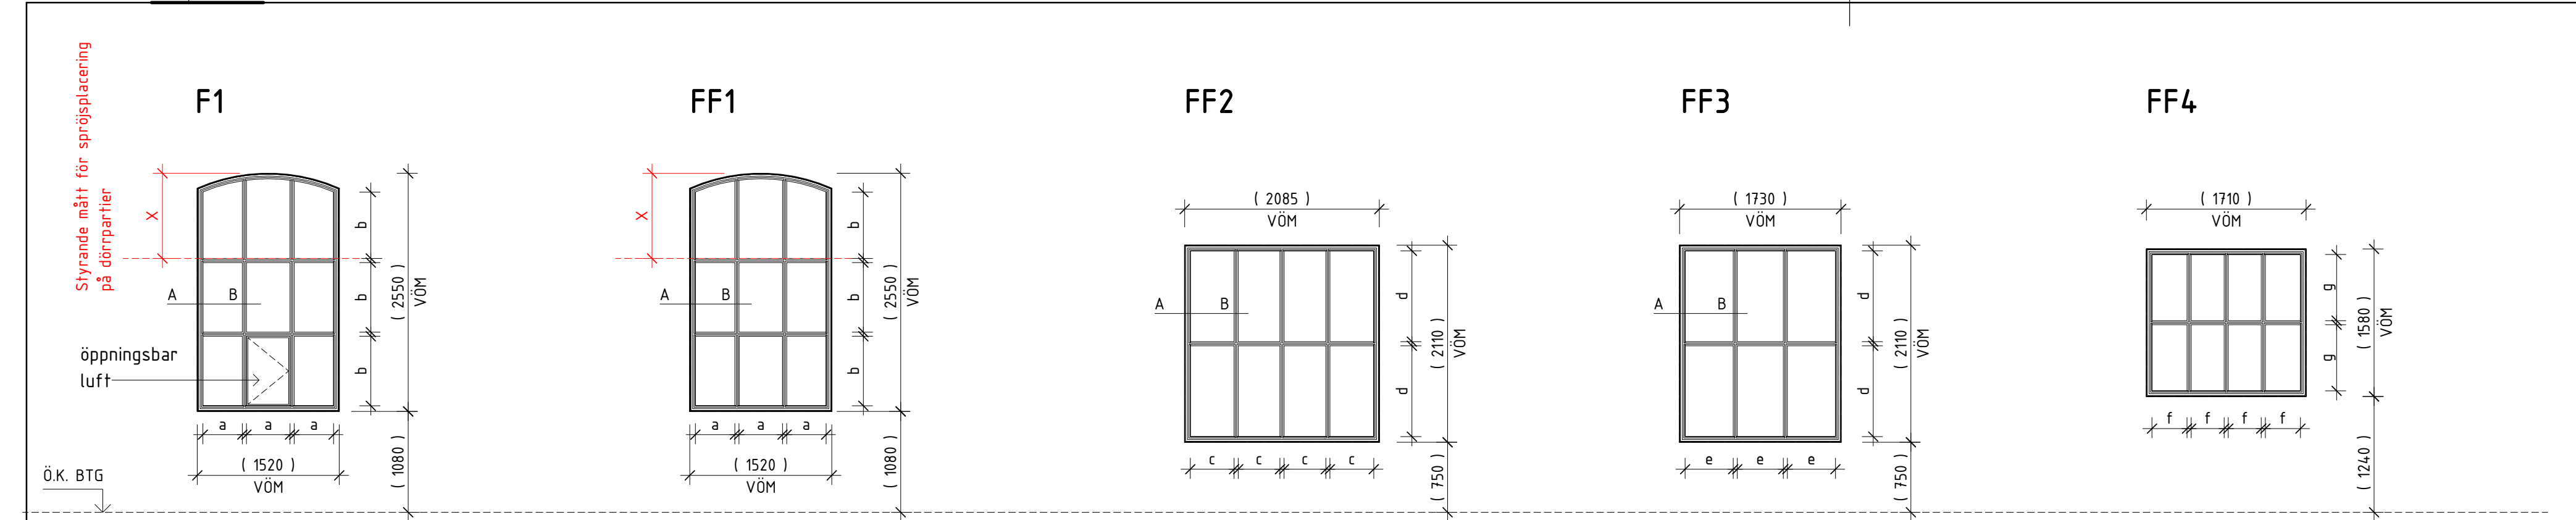

Typ	F1
Beskrivning	Fast fönster m öppningsbar del
Antal H / V	
Antal	12

4. Öppningsbar luft sidohängd inåtgående (vänsterhängd)






17.9 Färdigmonterad magnetkontakt med anslutningskabel i öppningsbar luft

Typ	FF1
Beskrivning	Fast fönster
Antal H / V	
Antal	9

Typ	FF2
Beskrivning	Fast fönster
Antal H / V	
Antal	2

Typ	FF3
Beskrivning	Fast fönster
Antal H / V	
Antal	1

Typ	FF4
Beskrivning	Fast fönster
Antal H / V	
Antal	1

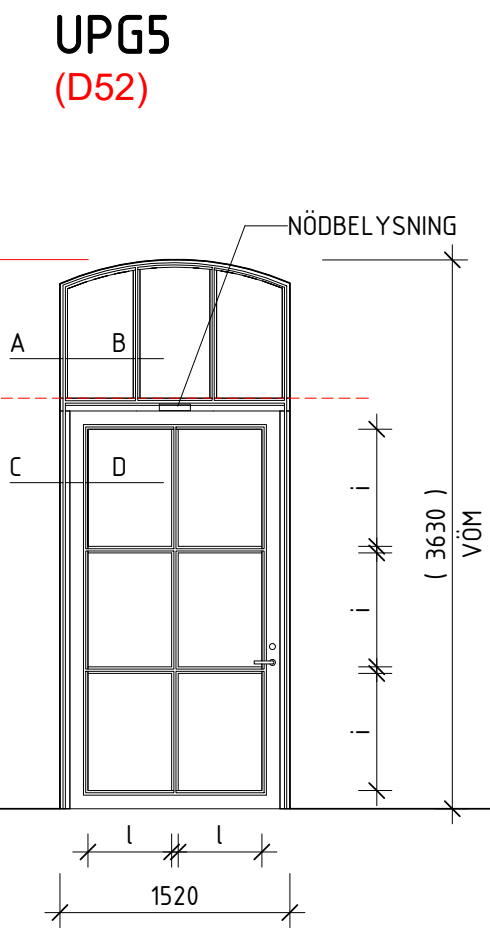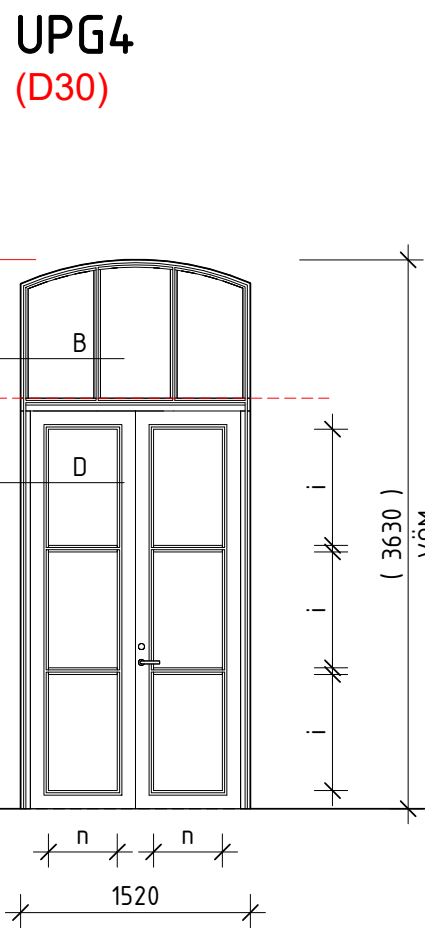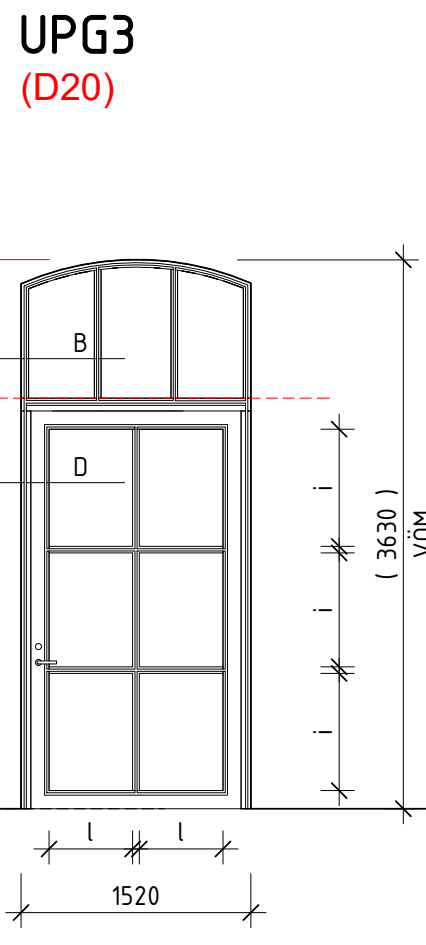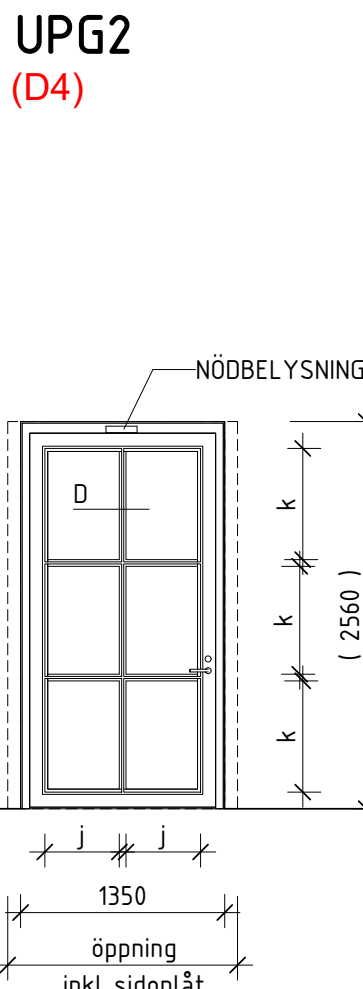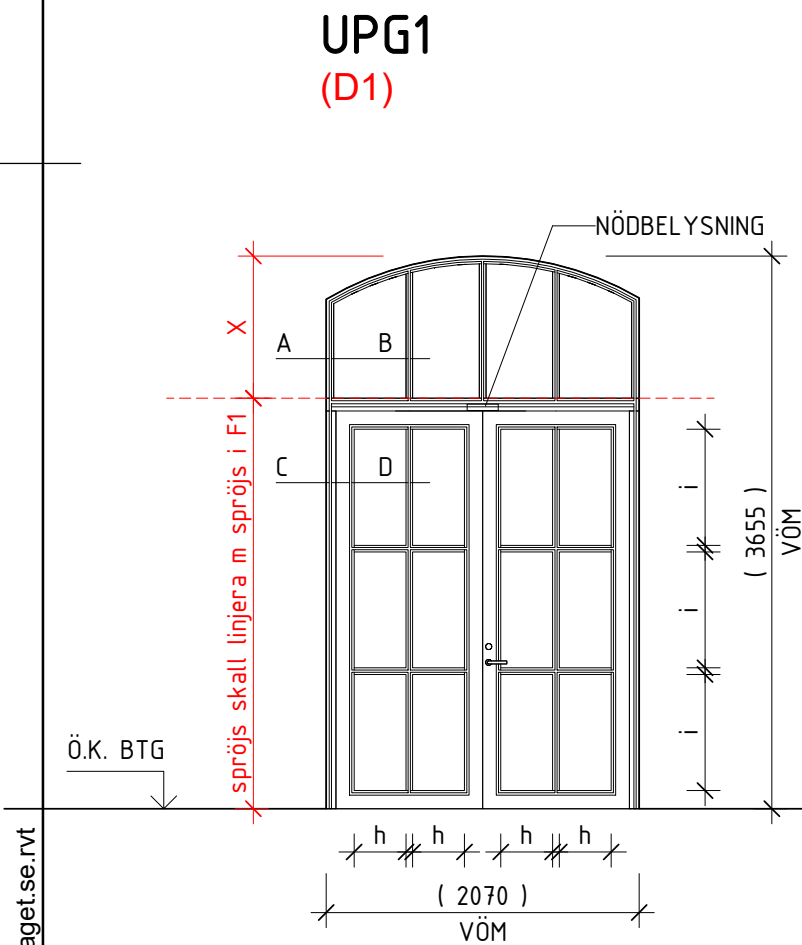

Typ	UPG1
Beskrivning	Entréparti m utåtgående pardörr
Antal H / V	1H/0V
Antal	1

4. Aluminiumparti i klimatgräns

Utåtgående pardörr med fast överljus

8.2 Nödutrymning

10. Säkerhetsglas (uk glas < 0,6 m ö golv)

17. Beslagning enl Bestagskort D01

17.9 Nödbelysning

Typ	UPG2
Beskrivning	Entrédörr utåtgående
Antal H / V	0H/1V
Antal	1

4. Aluminiumparti i klimatgräns

Utåtgående enkeldörr

8.2 Nödutrymning

10. Säkerhetsglas (uk glas < 0,6 m ö golv)

15. OBS! Befintlig muröppning är större än dörrrens karmyttermått. Muröppning skall kompletteras med plåtbeklädnad (sidoplåt) i kulör lika parti och enl. senare detaljritning

17. Beslagning enl Bestagskort D04

17.9 Nödbelysning

Typ	UPG3
Beskrivning	Glasparti m utåtgående enkeldörr
Antal H / V	1H/0V
Antal	1

4. Aluminiumparti i klimatgräns

Utåtgående enkeldörr med fast överljus

8.2 Nödutrymning

10. Säkerhetsglas (uk glas < 0,6 m ö golv)

17. Beslagning enl Bestagskort D20

17.9 Uppställningsbeslag

Typ	UPG4
Beskrivning	Glasparti m utåtgående pardörr
Antal H / V	1H/0V
Antal	1

4. Aluminiumparti i klimatgräns

Utåtgående pardörr med fast överljus

10. Nödutrymning

17. Beslagning enl Bestagskort D30

Typ	UPG5
Beskrivning	Glasparti m utåtgående enkeldörr
Antal H / V	0H/1V
Antal	1

4. Aluminiumparti i klimatgräns

Utåtgående enkeldörr med fast överljus

8.2 Nödutrymning

10. Säkerhetsglas (uk glas < 0,6 m ö golv)

17. Beslagning enl Bestagskort D52

17.9 Nödbelysning

FÖRESKRIFTER

Arbets- och detaljritningar skall upprättas av leverantören och godkännas av byggnadsentreprenör och arkitekt före tillverkning. Kontrollmätning av samtliga öppningar skall utföras före tillverkning, angivna mått inom parentes är cirkamått.

Utförande enligt fabrikantens grundutförande om ej annat anges. Partier dimensioneras av tillverkaren/leverantören. Enheter skall märkas enligt ritningens litterering, i förekommande fall med tillagt v eller h för hängning. Partierna skall kvalitetssäkras med P-märkning.

GEMENSAMMA EGENSKAPER

4. TYP

Profilsystem av aluminium.

Fönster: Typ Preconal Hansen millenium eller likvärdigt.

Synlig bredd på karm 29 mm, genomgående spröjs bredd 44 mm med invändig rektangulär glaslist, dold dränering. Öppningsbara fönster skall vara med dold ytterbåge och dolda gångjärn.

Dörrar: SAPA dörr 2086 eller likvärdigt med spröjs lika fönstersystem. 3-bladiga gångjärn enligt partifillverkaren.

5. MÅTT

Mått enl uppställning, profilmått enligt detalj.

OBS! Alla mått skall kontrolleras på plats

Erforderlig ställplats runt om skall tillgodoses av tillverkaren.

8. FUNKTIONSKRAV

8.1 Värmeisolering

U-värde för hela konstruktionen.

Vid 3-glas (fönster): Uw = 1,2 W/m²K

Vid 2-glas (dörrar): Ud max 1,9 W/m²K

Tätningsslister utförs av EPDM-gummi.

8.2 Brandkrav, se resp parti

8.3 Ljudkrav, min R'w = 30 dB

8.4 Inbrottskydd: Skyddsklass 1 enligt SSF 200

9.2 YTBEHANDLING

Glaspartier inklusive dörrar levereras pulverlackerade ut- och invändigt.

Pulverlackering ca 60 MY. Förbehandling enl. tillverkarens standard.

Gångjärn ytbehandlas lika karm.

Kulör utsida: grön, NCS S 7020-B90G / RAL 6005

Kulör insida: mörkgrå, Gris 2900 Sablé YW355F, Interpon Collection Futura

10. GLAS

3-glas förseglade isolerrutor fönster och över- och sidoljus.

2-glas förseglade isolerrutor i glasade dörrar.

Yttre glaset skall vara härdat, innersta glaset skall vara laminerat.

Glas skall vara klarglas, då ej annat anges.

Förseglade rutor skall uppfylla kraven för P-märkning enl.

tillverkarens standard. Montering enligt MTK:S föreskrifter. Glas

dimensioneras av tillverkaren. Glas skall uppfylla kraven enl. BBR 8:35

beträffande säkerhet vid användning.

Säkerhetsglas krävs där u.k. glas är <0,6 m över färdigt golv.

13 KARM

Stomprofiler synlig bredd max 29 mm, profildjup dimensioneras av

tillverkaren. Profildjup dörrar 86 mm = Typ SAPA 2086 eller likvärdigt.

Mått på karmöverstycke skall medge montage av dörrautomatik resp

dörrstängare.

14 TRÖSKEL

Handikappanpassad anslagströskel enl. tillverkarens standard.

Tröskel av rostfritt stål.

17. BESLAG

(Beslagning och funktion skall utföras enligt av RA Låshuset AB upprättade Bestagskort. Beslagskort är numrerade lika Dörrpositionsnummer.)

Beslagning och funktion enligt handling nr 6.2.5 "RAMBESKRIVNING OMBYGGNAD, EL- OCH TELESYSTEM".

17.7 STÄNGNINGSBESLAG

Dörröppningsautomatik och dörrstängare monteras på karm på anslagssidan.

Kåpa målas lika glasparti.

17.9. ANMÄRKNING

All dragning av el skall utföras dold.

Nödbelysning:

Armatur, typ enligt elhandling monteras utvändigt på karm

(OBS frigång dörrblad). Dim. BxHxD = 205x43x15 mm.

Armatur lackeras i grön kulör lika utsida partier.

FÖRKLARINGAR

Dörrpositionsnummer (Dxx) anger nya och befintliga dörrars unika placering, se planritningar.

Figurer ses från utsidan.

Hängning anges med utgångspunkt från gångjärnsidan.

Vid pardörr avses gångdörrens hängning.

Bokstaven V resp. H efter angivet antal anger Vänster- resp. Högerhängning.

Mått är angivna i mm. Mått anger väggöppningsmått, VÖM,



samt väggöppningens placering i höjdd över betongbjälklag

(Ö.K. betong). Färdigt golv är 20 mm ovan Ö.K. betongbjälklag.

Egenskaper anges dels som GEMENSAMMA EGENSKAPER, dels som specifika för resp. littera. Egenskaper angivna för resp. littera gäller tillsammans med gemensamma egenskaper och ersätter i förekommande fall egenskaper angivna som gemensamma.

KODSYSTEM ENL SIS 81 73 40.

- Littera
- Hängning/Antal
- Dörrtyp
- Mått
- Klassindelning
- Virkesklass
- Funktionskrav
- Värmeisolering
- Brandkrav
- Ljud
- Inbrottskydd
- Ventilation
- Dörrbladsyta
- Material
- Ytbehandling
- Glas
- Dörrbladskant
- Skyddsbeklädnad
- Karm
- Väggfjocklek
- Karmdjup
- Typ & material
- Påskörningskydd
- Material
- Ytbehandling
- Tröskel
- Karmfällagg
- Foder
- Beslag
- Ändring
- Beteckning
- Låstyp
- Tryck/Draghandtag
- Nyckelhållare/Toalettbehör/Täckbricka
- Ringklocka/Kiköga
- Dörrstängare/Dörrautomatik/Spanjolett
- El-slutbleck/Magnetållare
- Anmärkning/Kortläsare/Armbågskontakt

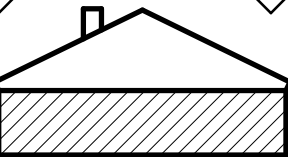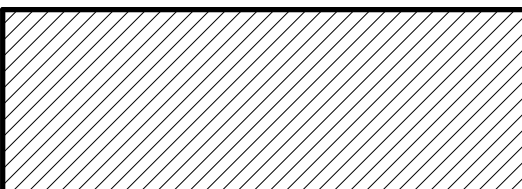BET		ÄNDRING AVSER		DATUM		SIGN	
FÖRFRÅGNINGSUNDERLAG							
		HELSINGBORG FASTIGHETSFÖRVALTNINGEN					
FASTIGHET							
ORIENTEN 6							
RÖNNOWSKA SKOLAN, NYTT KÖK OCH MATSAL							
OBJEKTSNR		BYGGNADS-ID			PROJEKTNR		
1457		5-266088			60095		
BYGGNAD							
1457-20 - HUS V (BYGGNAD 449)							
ORIENTERINGSGRUPP							
PLAN		03					
DEL							
							
VÄSTRA SANDGATAN							
(A)		ARKITEKTLAGET SKÅNE AB				T: 042-19 96 00	
BR		FIRETECH ENGINEERING EMRON AB				T: 010-150 14 00	
E		DEVELCON AB				T: 079-020 27 02	
K		ÅKERMANS INGENJÖRSBYRÅ AB				T: 042-12 00 10	
M		TYRÉNS AB				T: 010-452 20 00	
S		SWECO SVERIGE AB				T: 08-695 60 00	
SK		STORKÖKSVISION				T: 040-744 29	
V		SWECO SVERIGE AB				T: 08-695 60 00	
W		SWECO SVERIGE AB				T: 08-695 60 00	
UPPDRAGSNR		ANSVARIG					
22063_00		BRANISLAV KUZMANOVIC					
DATUM		RITAD/KONSTR AV			HANDLAGGARE		
2025-01-27		MVJ			BK		
					SYSTEMBETECKNING		
					42-4		
HUS 20							
UTV. FÖNSTER & GLASPARTIER							
UPPSTÄLLNING							
SKALA		NUMMER					
1 : 50		A--42-4-2000001					
						REV	

ORIGINALFORMAT: A1

