



2025-01-23 14:30:59 \\AL-AG-FS\RedirectedFolders\mikaels\mikaels\00_V20001_mikaels\arkitekt\arkitekt.se.rvt

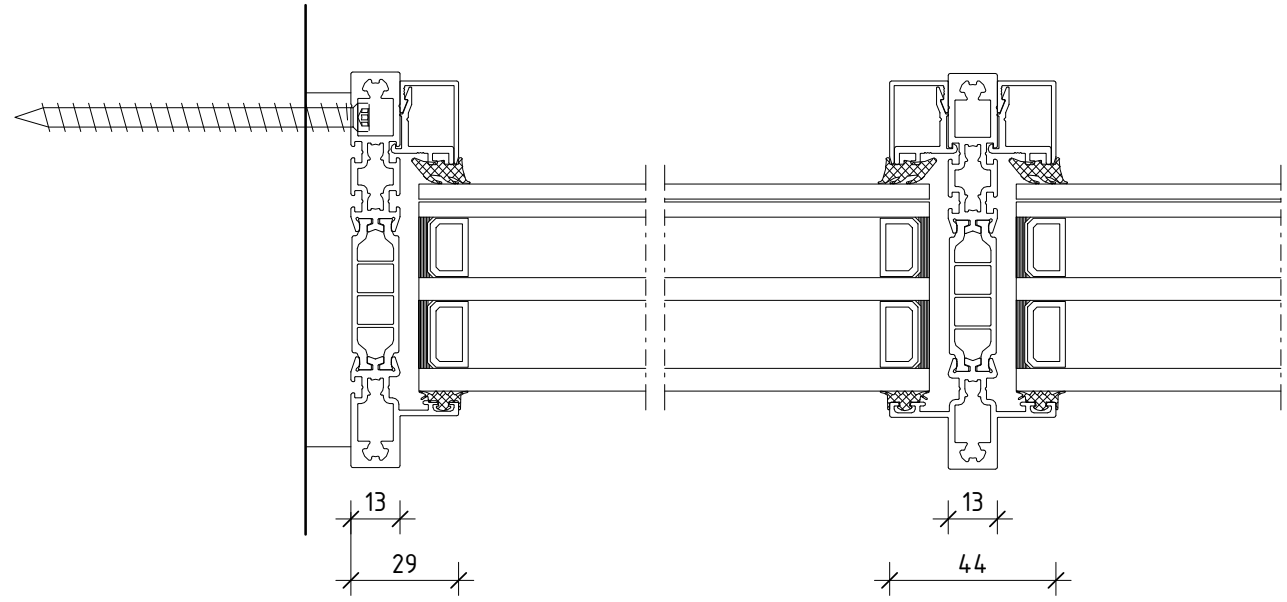

A

B


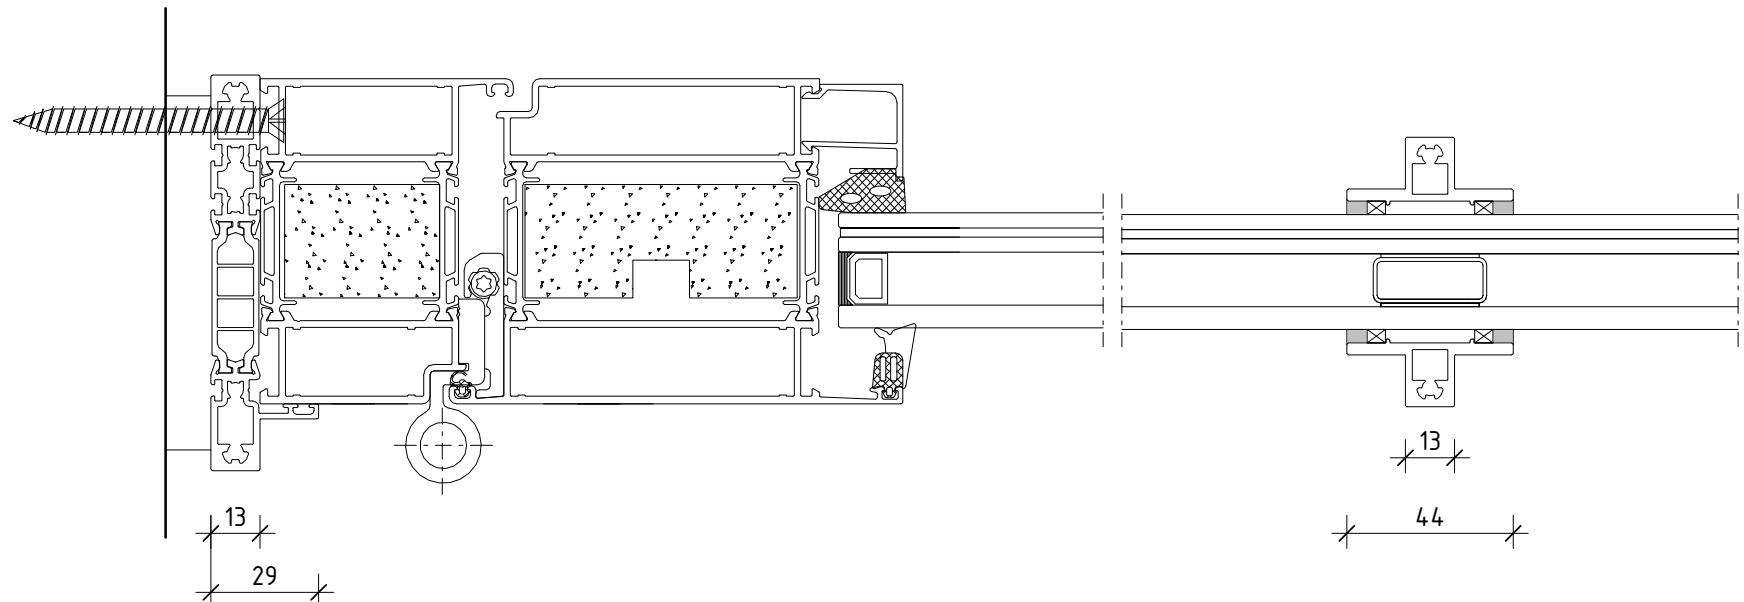


C

D

HÄNVISNINGAR

FÖRKLARINGAR OCH FÖRESKRIFTER,
SE RITNING A--42-4-2000001

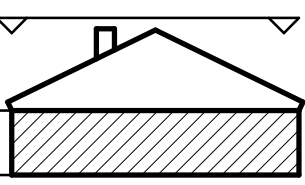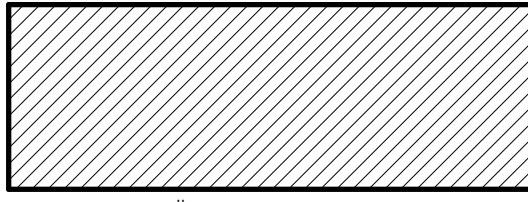ÄNDRING AVSER		DATUM	SIGN
FÖRFRÅGNINGSUNDERLAG			
 HELSINGBORG FASTIGHETSFÖRVALTNINGEN			
FASTIGHET			
ORIENTEN 6			
RÖNNOWSKA SKOLAN, NYTT KÖK OCH MATSAL			
OBJEKTSNR 1457	BYGGNADS-ID 5-266088	PROJEKTNR 60095	
BYGGNAD			
1457-20 - HUS V (BYGGNAD 449)			
ORIENTERINGSGRUPP			
PLAN 03			
03 02 01 			
DEL			
			
VÄSTRA SANDGATAN			
(A)	ARKITEKTLAGET SKÅNE AB		T: 042-19 96 00
BR	FIRETECH ENGINEERING EMRON AB		T: 010-150 14 00
E	DEVELCON AB		T: 079-020 27 02
K	ÅKERMANS INGENJÖRSBYRÅ AB		T: 042-12 00 10
M	TYRÉNS AB		T: 010-452 20 00
S	SWECO SVERIGE AB		T: 08-695 60 00
SK	STORKÖKSVISION		T: 040-744 29
V	SWECO SVERIGE AB		T: 08-695 60 00
W	SWECO SVERIGE AB		T: 08-695 60 00
UPPDRAGSNR			
22063_00			
ANSVARIG			
BRANISLAV KUZMANOVIC			
DATUM	RITAD/KONSTR AV	HANDLAGGARE	SYSTEMBETECKNING
2025-01-27	MVJ	BK	42-4
HUS 20			
UTV. FÖNSTER & GLASPARTIER			
PRINCIPDETALJER			
SKALA	NUMMER		REV
1:2	A--42-4-2000002		

ORIGINALFORMAT: A1