
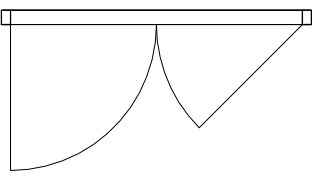
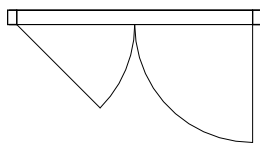


2025-01-23 14:31:19 \\ALAG-FS\RedirectedFolders\mikaeb\My Documents\A-00_V20001_mikaeb\arkitektlagat.se.rtf

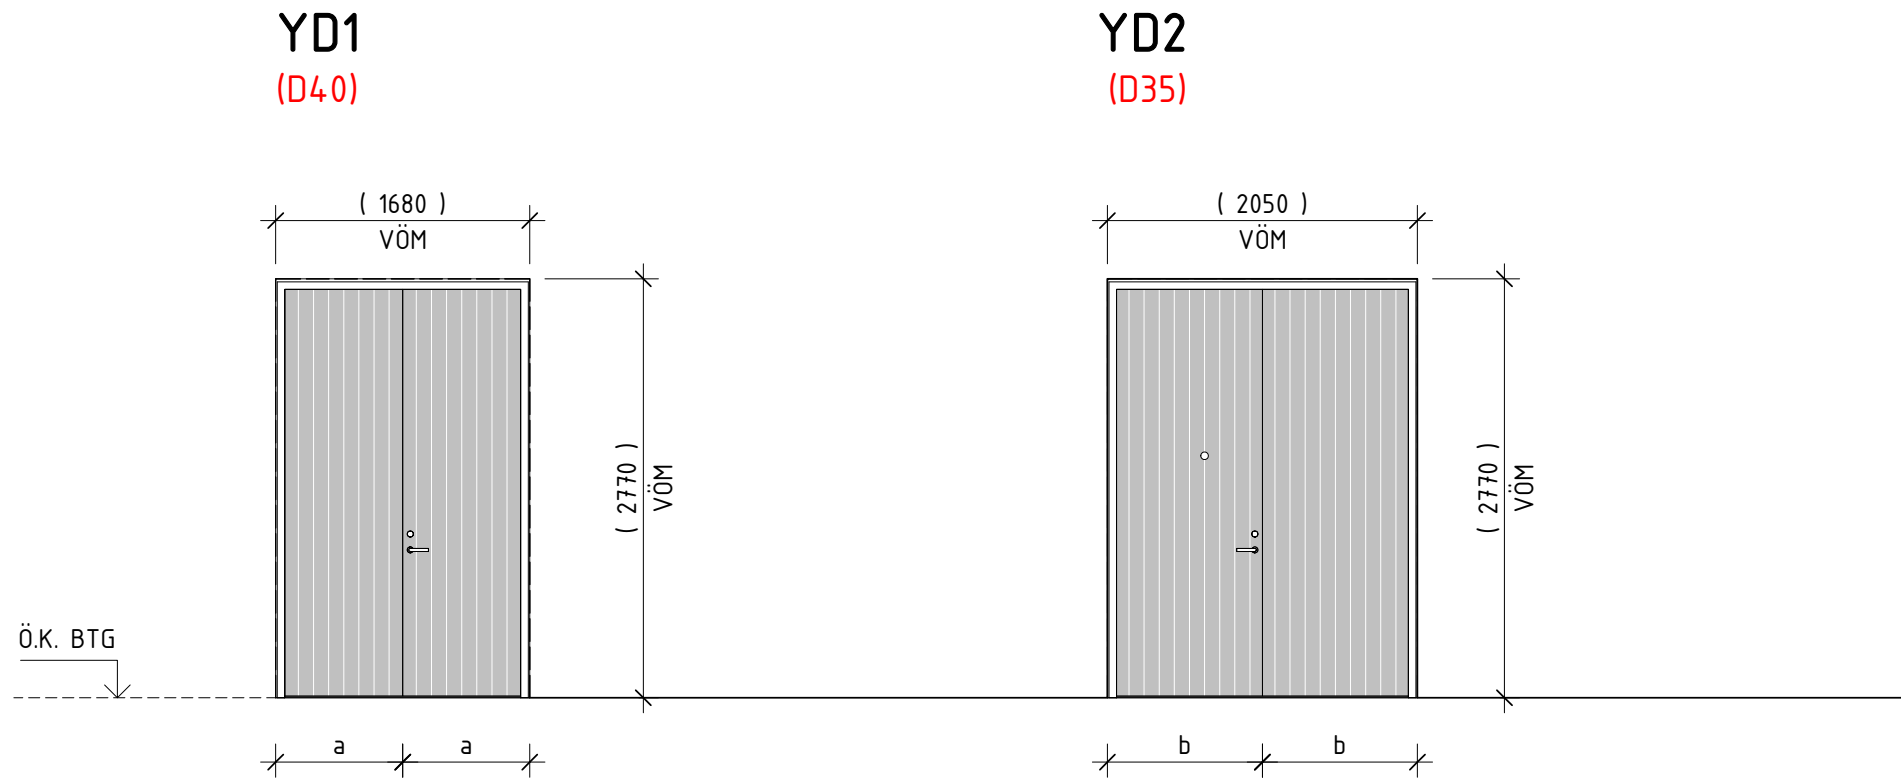

Typ	YD1
Beskrivning	Pardörr utåtgående till miljörum
Antal H / V	1H/0V
Antal	1

4. Dörr av trä i klimatgräns
- Utåtgående symmetrisk pardörr
17. Beslagning enligt Beslagskort D40
- 17.9 Uppställningsbeslag på båda dörrbladen

Typ	YD2
Beskrivning	Pardörr utåtgående till varuintag
Antal H / V	0H/1V
Antal	1

4. Dörr av trä i klimatgräns
- Utåtgående symmetrisk pardörr
- 8.2 Nödutrymning
17. Beslagning enligt Beslagskort D35
- 17.6 Dörrkik på aktivt dörrblad
- 17.9 Uppställningsbeslag på båda dörrbladen

FÖRESKRIFTER

Arbets- och detaljritningar skall upprättas av leverantören och godkännas av byggnadsentreprenör och arkitekt före tillverkning. Kontrollmätning av samtliga öppningar skall utföras före tillverkning, angivna mått inom parentes är cirka mått.

Utförande enligt fabrikantens grundutförande om ej annat anges. Partier dimensioneras av tillverkaren/leverantören. Enheter skall märkas enligt ritningens litterering, i förekommande fall med tillagt v eller h för hängning. Partierna skall kvalitetssäkras med P-märkning. Fabriksmålad.

GEMENSAMMA EGENSKAPER

4. TYP
Ytterdörr av trä, typ Tylösand av Fabrikat Ekstrands eller likvärdigt. Vertikalt spårad träpanel utvändigt, slät yta invändigt. Fabriksmålad.

5. MÅTT
OBS! Alla mått skall kontrolleras på plats
Erforderlig ställplats runt om skall tillgodoses av tillverkaren.

8. FUNKTIONSKRAV
8.1 Värmeisolering
U-värde 1,20 W/m²K
Tätningstister utförs av EPDM-gummi.
8.2 Brandkrav, se resp parti
8.3 Ljudkrav, min R'w = 30 dB
8.4 Inbrottskydd: Skyddsklass 1 enligt SSF 200

9.2 YTBEHANDLING
Kulör in- och utsida: grön, NCS S 7020-B90G / RAL 6005

12. SKYDDSEKÄLNAD
Innsida dörrblad och karm förses med beklädnad av rostfri stålplåt upp till höjd 1200 mm.

13. KARM
Träkarm 55x105 mm
Ytbehandling /kulör lika dörrblad.

14. TRÖSKEL
Tillgänglighetsanpassad anslagströskel enl. tillverkarens standard. Tröskel av aluminium.

17. BESLAG
(Beslagning och funktion skall utföras enligt av RA Låshuset AB upprättade Beslagskort. Beslagskort är numrerade likia Dörrpositionsnummer.)

Beslagning och funktion enligt handling nr 6.2.5 "RAMBESKRIVNING OMBYGGNAD, EL- OCH TELESYSTEM".


17.9. ANMÄRKNING
All dragning av el skall utföras dold.

FÖRKLARINGAR

Dörrpositionsnummer (Dxx) anger nya och befintliga dörrars unika placering, se planritningar. Figurer ses från utsidan. Hängning anges med utgångspunkt från gångjärnsidan. Vid pardörr avses gångdörrrens hängning. Bokstaven V resp. H efter angivet antal anger Vänster- resp. Högerhängning. Mått är angivna i mm. Mått anger väggöppningsmått, VÖM, samt väggöppningens placering i höjdd över betongbjälklag (Ö.K. betong). Färdigt golv är 20 mm ovan Ö.K. betongbjälklag.

Egenskaper anges dels som GEMENSAMMA EGENSKAPER, dels som specifika för resp. liffra. Egenskaper angivna för resp. liffra gäller tillsammans med gemensamma egenskaper och ersätter i förekommande fall egenskaper angivna som gemensamma.

- KODSYSTEM ENL. SIS 81 73 40.
2. Littera
3. Hängning/Anfal
4. Dörrtyp
5. Mått
6. Klassindelning
7. Virkesklass
8. Funktionskrav
- 8.1 Värmeisolering
- 8.2 Brandkrav
- 8.3 Ljud
- 8.4 Inbrottskydd
- 8.5 Ventilation
9. Dörrbladsyta
- 9.1 Material
- 9.2 Ytbehandling
10. Glas
11. Dörrbladskant
12. Skyddsbeklädnad
13. Karm
- 13.1 Väggjocklek
- 13.2 Karmdjup
- 13.3 Typ & material
- 13.4 Påkörningsskydd
- 13.5 Material
- 13.6 Ytbehandling
14. Tröskel
15. Karmtillägg
16. Foder
17. Beslag
- 17.1 Ändring
- 17.2 Beteckning
- 17.3 Låstyp
- 17.4 Trycke/Draghandtag
- 17.5 Nyckelhållsskytt/Toalettbehör/Täckbricka
- 17.6 Ringklocka/Kiköga
- 17.7 Dörrstängare/Dörrautomatik/Spanjolett
- 17.8 El-slutbleck/Magnethållare
- 17.9 Anmärkning/Kortläsare/Armbågskontakt

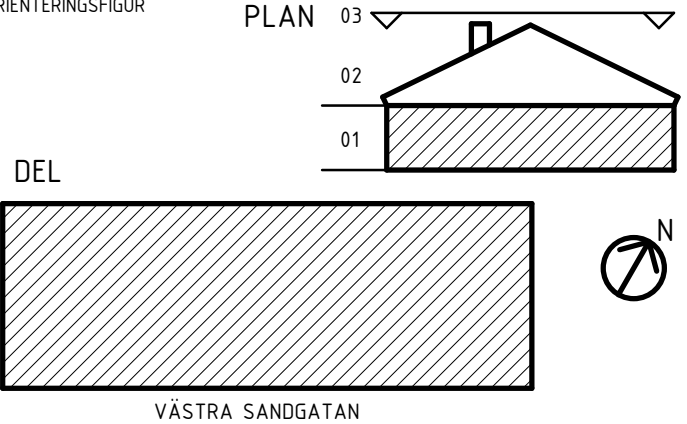BET	ÄNDRING AVSER	DATUM	SIGN
FÖRFRÅGNINGSUNDERLAG			
 HELSINGBORG FASTIGHETSFÖRVALTNINGEN			
FASTIGHET			
ORIENTEN 6			
RÖNNOWSKA SKOLAN, NYTT KÖK OCH MATSAL			
OBJEKTSNR	BYGGNADS-ID	PROJEKTNR	
1457	5-266088	60095	
BYGGNAD			
1457-20 - HUS V (BYGGNAD 449)			
ORIENTERINGSGR			
PLAN 03			
			
DEL			
VÄSTRA SANDGATAN			
A	ARKITEKTLAGET SKÅNE AB	T: 042-19 96 00	
BR	FIRETECH ENGINEERING EMRON AB	T: 010-150 14 00	
E	DEVELCON AB	T: 079-020 27 02	
K	ÅKERMANS INGENJÖRSBYRÅ AB	T: 042-12 00 10	
M	TYRÉNS AB	T: 010-452 20 00	
S	SWECO SVERIGE AB	T: 08-695 60 00	
SK	STORKÖKSVISION	T: 040-744 29	
V	SWECO SVERIGE AB	T: 08-695 60 00	
W	SWECO SVERIGE AB	T: 08-695 60 00	
UPPDRAGSNR			
22063_00			
ANSVARIG			
BRANISLAV KUZMANOVIC			
DATUM	RITAD/KONSTR AV	HANDLAGGARE	SYSTEMBETEKNING
2025-01-27	MB	BK	42-4
HUS 20			
UTVÄNDIGA DÖRRAR AV TRÄ			
UPPSTÄLLNING			
SKALA	NUMMER		REV
1 : 50	A-42-4-2000011		

ORIGINALFORMAT: A1

