



2025-01-23 14:31:55 \\ALAG-FS\RedirectedFolders\mklaeb\My Documents\A-00_V20001_mklaeb\arkitektlaget.se.rvt

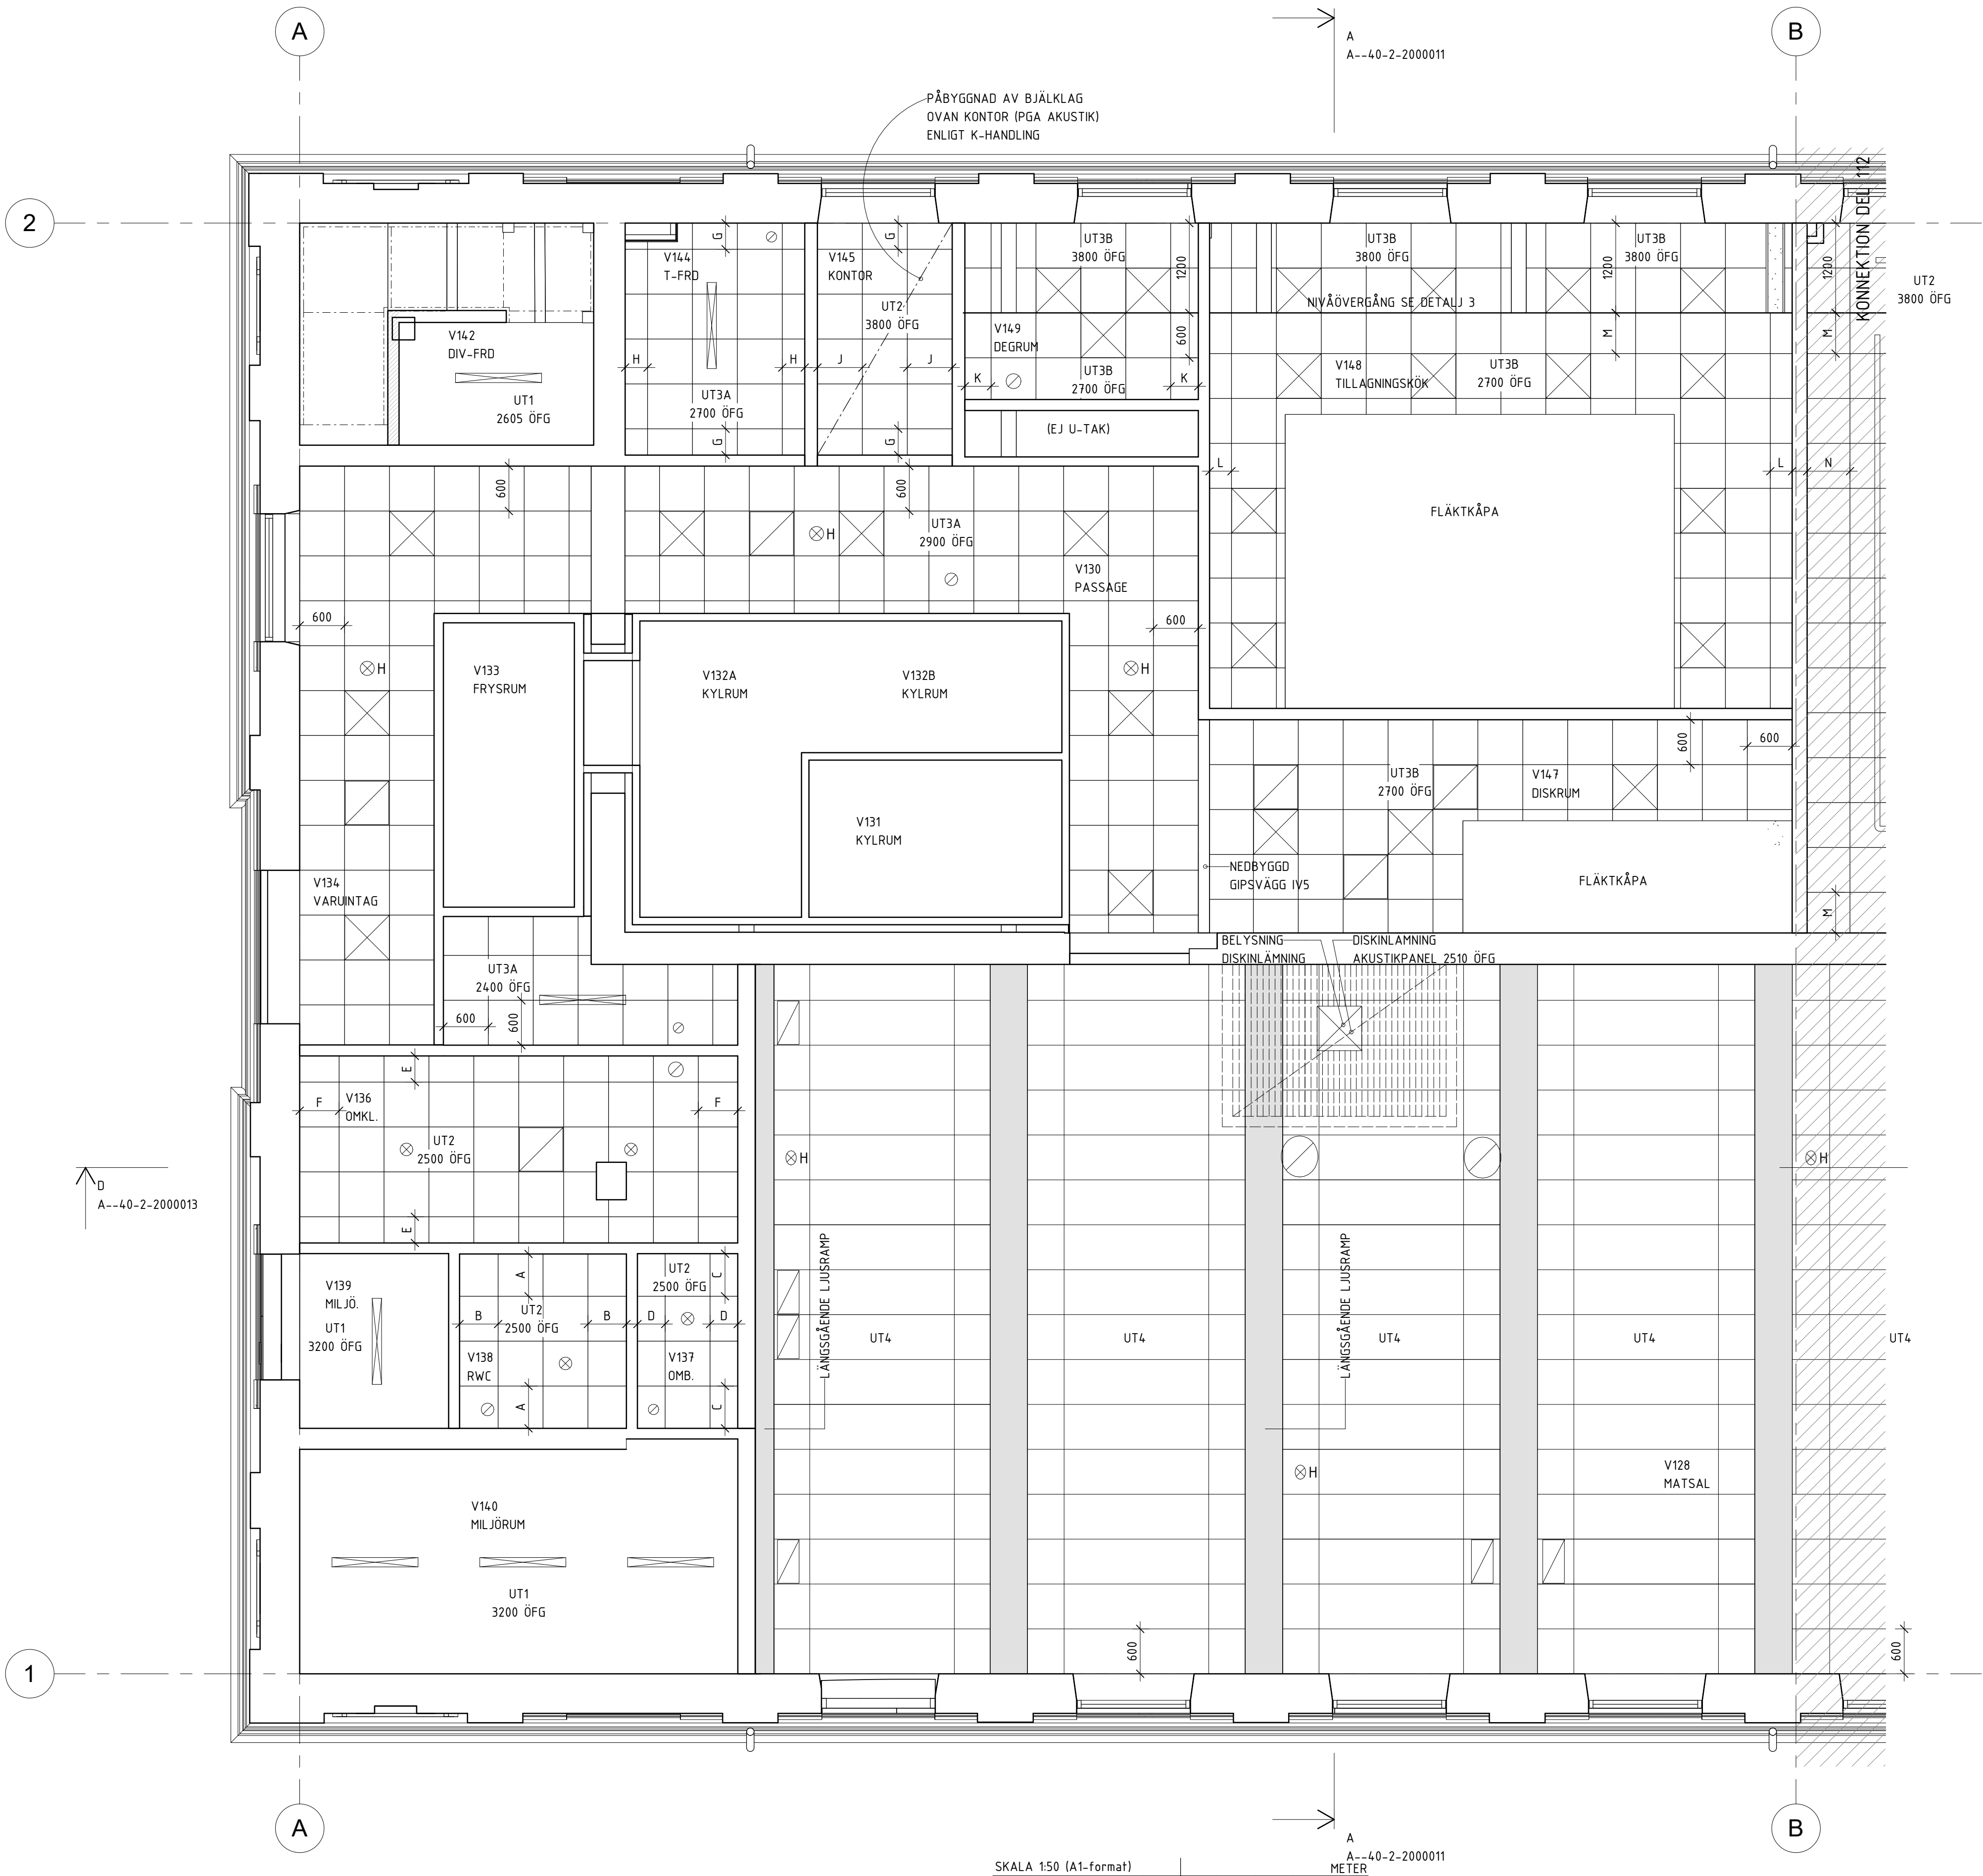

FÖRKLARINGAR

SAMTLIGA MÅTT ANGES I MM.
ÖFG AVSER UNDERTAKSHÖJD ÖVER FÄRDIGT GOLV.

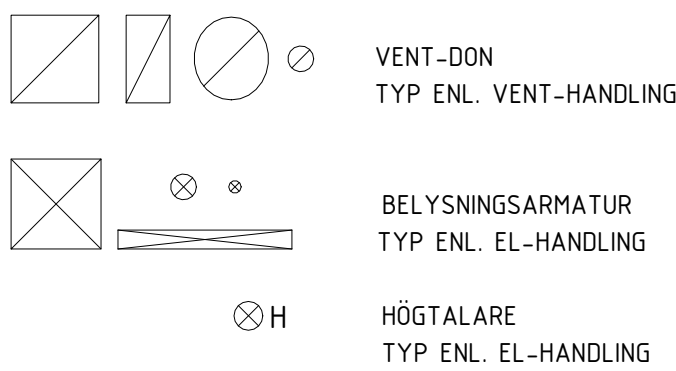

FÖRESKRIFTER

UNDERTAK

DÄR KAPADE PLATTOR FÖREKOMMER MÅLAS KANTEN I KULÖR LIKA PLATTA.
SYNLIGA DELAR AV BETONG OCH FAST GIPSTAK MÅLAS ENL. ANVISNINGAR I RUMSBESKRIVNING.

UT1

FAST MONTERAT GIPSUNDERTAK

UT2

LJUDABSORBENTER TYP ECOPHON MASTER E, 600x600x40. KULÖR VIT, NCS S 0500-N
LJUDABSORPTIONSKLASS A, BÄRVERK T24 VIT 01

UT3A

LJUDABSORBENTER TYP ECOPHON HYGIENE PERFORMANCE A, 600x600x40. KULÖR VIT, NCS S 0500-N
LJUDABSORPTIONSKLASS A, BÄRVERK T24 VIT 01

UT3B

LJUDABSORBENTER TYP ECOPHON HYGIENE PERFORMANCE A, 600x600x40. KULÖR VIT, NCS S 0500-N
LJUDABSORPTIONSKLASS A, BÄRVERK T24 C3, VIT 01


UT4

VÄLVD A UNDERTAK
LJUDABSORBENTER TYP ECOPHON FOCUS FLEXIFORM A.
LÄNGSGÅENDE LJUSRAMP.
SE PRINCIPDETALJ, RITNING NR A--43-4-200115

HÄNVISNINGAR

PENDLAD BELYSNING ENLIGT EL-HANDLINGAR.

- 6.3.1 A-HANDLINGSFÖRTECKNING
- 6.2.1 RAMBESKRIVNING BYGG
- 6.2.2 RUMSBESKRIVNING

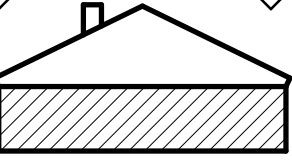BET	ÄNDRING AVSER		DATUM	SIGN
FÖRFRÅGNINGSUNDERLAG				
 HELSINGBORG FASTIGHETSFÖRVALTNINGEN				
FASTIGHET				
ORIENTEN 6				
RÖNNOWSKA SKOLAN, NYTT KÖK OCH MATSAL				
OBJEKTSNR	BYGGNADS-ID		PROJEKTSNR	
1457	5-266088		60095	
BYGGNAD				
1457-20 – HUS V (BYGGNAD 449)				
ORIENTERINGSFIGUR				
PLAN 03 02 01 				
DEL				
111 112 113 				
VÄSTRA SANDGATAN				
A ARKITEKTLAGET SKÅNE AB T: 042-19 96 00				
BR FIRETECH ENGINEERING EMRON AB T: 010-150 14 00				
E DEVELCON AB T: 079-020 27 02				
K ÅKERMANS INGENJÖRSBYRÅ AB T: 042-12 00 10				
M TYRÉNS AB T: 010-452 20 00				
S SWECO SVERIGE AB T: 08-695 60 00				
SK STORKÖKSVISION T: 040-744 29				
V SWECO SVERIGE AB T: 08-695 60 00				
W SWECO SVERIGE AB T: 08-695 60 00				
UPPDRAGSNR		ANSVARIG		
22063_00		BRANISLAV KUZMANOVIC		
DATUM	RITAD/KONSTR AV	HANDLAGGARE	SYSTEMBETECKNING	
2025-01-27	MB	BK	43-1	
HUS 20				
UNDERTAKSPLAN, DEL 111				
-				
-				
-				
SKALA	NUMMER			REV
1 : 50	A--43-1-2001111			
ORIGINALFORMAT: A1				