


2025-01-23 14:33:18 \\ALAG-FS\RedirectedFolders\mikaeb\My Documents\A-00_V20001_mikaeb\arkitektlagst.se.rtf

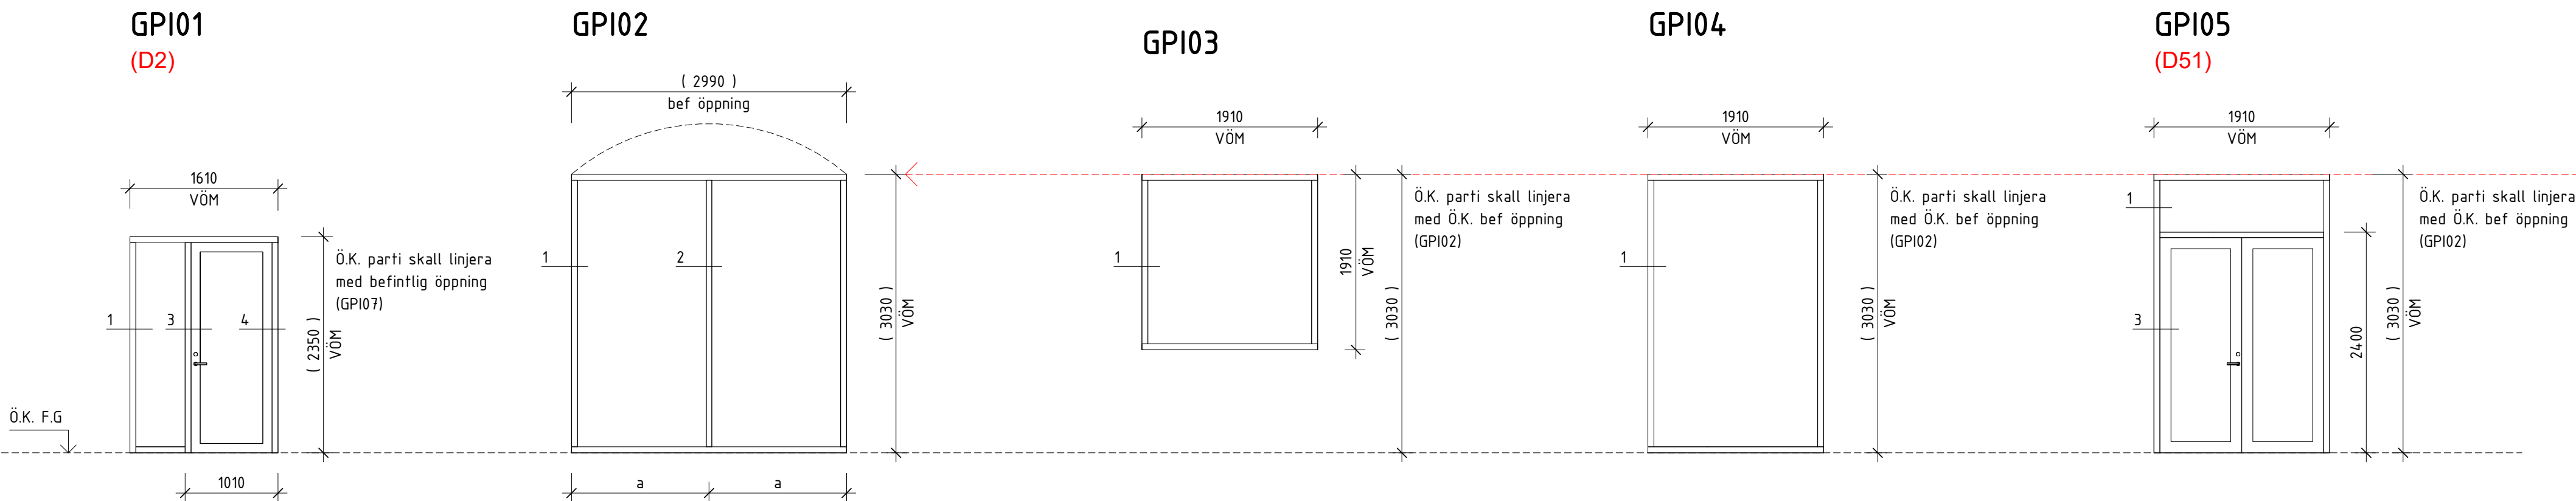

Typ	GPI01
Beskrivning	Glasad dörr med sidoljus
Antal H / V	1H/0V
Antal	1

4. SP 300 - Stålparti i ny öppning
8.2 Nödutrymning
8.3 Ljudkrav R_w 25 dB
10. Säkerhetsglas (uk glas < 0,6 m ö golv)
14. Rostfritt plattstål + släplst, ljudkrav beaktas
17. Beslagning enligt Beslagskort D02

Typ	GPI02
Beskrivning	Fast glasparti
Antal H / V	
Antal	3

4. SP 300 - Stålparti i befintlig öppning
10. Säkerhetsglas (uk glas < 0,6 m ö golv)

Typ	GPI03
Beskrivning	Fast glasparti
Antal H / V	
Antal	2

4. SP 300 - Stålparti i ny öppning


Typ	GPI04
Beskrivning	Fast glasparti
Antal H / V	
Antal	1

4. SP 300 - Stålparti i ny öppning
10. Säkerhetsglas (uk glas < 0,6 m ö golv)

Typ	GPI05
Beskrivning	Glasad pardörr med överljus
Antal H / V	0H / 1V
Antal	1

4. SP 300 - Stålparti i ny öppning
8.2 Nödutrymning
10. Säkerhetsglas (uk glas < 0,6 m ö golv)
14. Utan tröskel
17. Beslagning enligt Beslagskort D51

17.9 Dörrhållare i golv för uppställning av dörrar

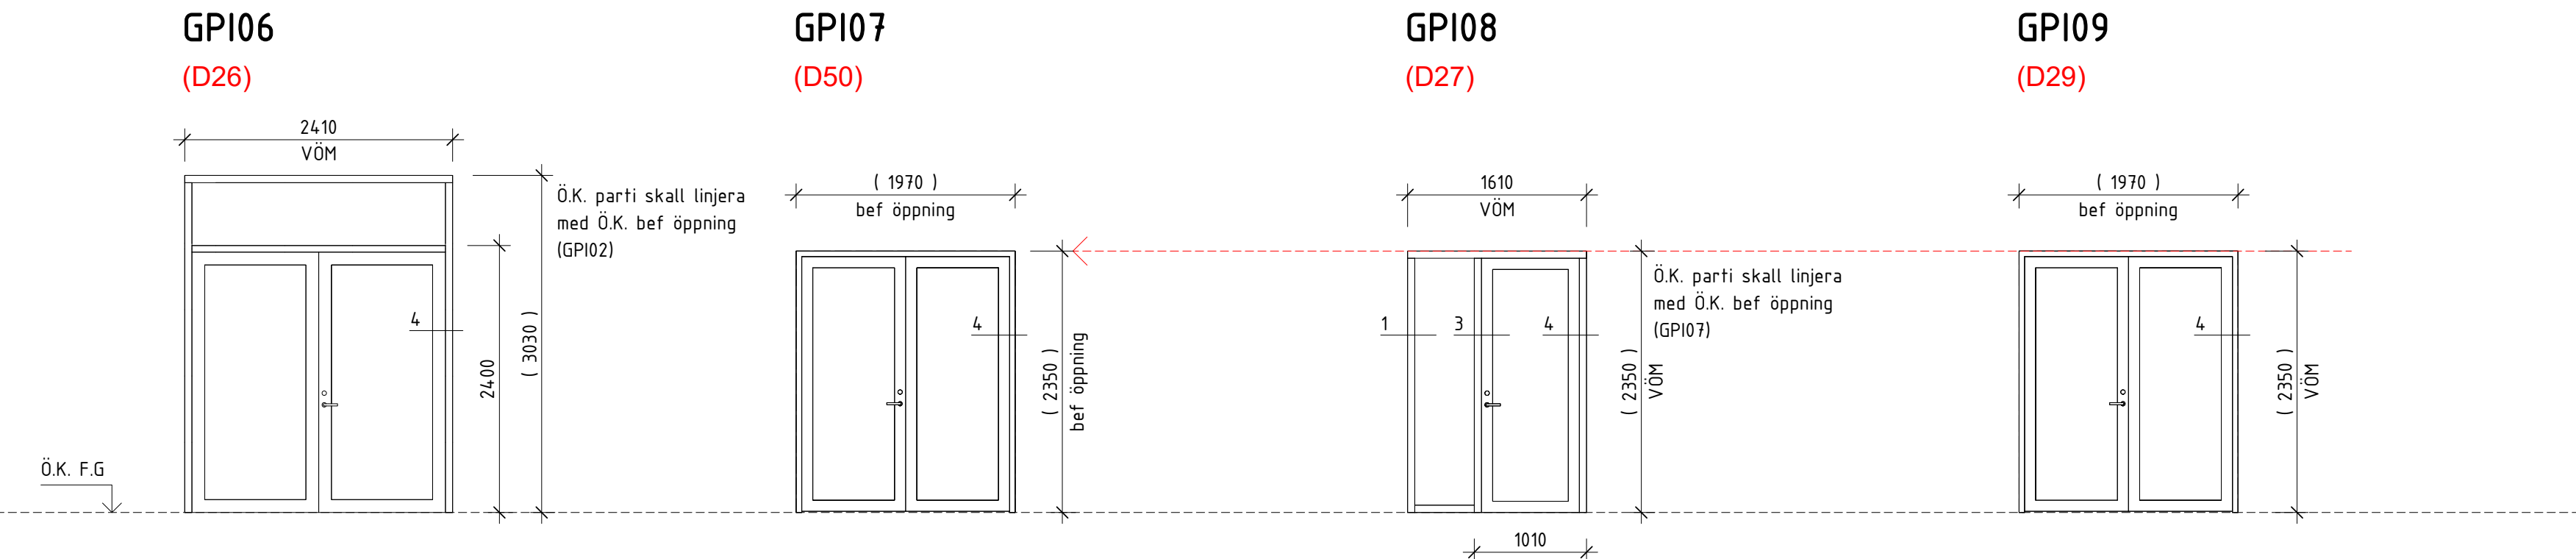

Typ	GPI06
Beskrivning	Glasad pardörr med överljus
Antal H / V	1H/0V
Antal	1

4. SP 300 - Stålparti i ny öppning
8.2 Nödutrymning
10. Säkerhetsglas (uk glas < 0,6 m ö golv)
14. Utan tröskel
17. Beslagning enligt Beslagskort D26

17.9 Dörrhållare i golv för uppställning av dörrar

Typ	GPI07
Beskrivning	Glasad pardörr
Antal H / V	0H/1V
Antal	1

4. SP 300 - Stålparti i befintlig öppning
8.2 Nödutrymning
10. Säkerhetsglas (uk glas < 0,6 m ö golv)
14. Rostfritt plattstål
17. Beslagning enligt Beslagskort D50

17.9 Dörrhållare i golv för uppställning av dörrar

Typ	GPI08
Beskrivning	Glasad pardörr med sidoljus
Antal H / V	1H/0V
Antal	1

4. SP 300 - Stålparti i ny öppning
8.2 Nödutrymning
8.3 Ljudkrav R_w 35 dB
10. Säkerhetsglas (uk glas < 0,6 m ö golv)
14. Rostfritt plattstål + släplst, ljudkrav beaktas
17. Beslagning enligt Beslagskort D27

Typ	GPI09
Beskrivning	Glasad pardörr
Antal H / V	0H/1V
Antal	1

4. SP 700 - Stålparti i befintlig öppning
8.2 Nödutrymning
8.3 Ljudkrav R_w 35 dB
10. Säkerhetsglas (uk glas < 0,6 m ö golv)
14. Rostfritt plattstål + släplst, ljudkrav beaktas
17. Beslagning enligt Beslagskort D29

FÖRESKRIFTER

Arbets- och detaljritningar skall upprättas av leverantören och godkännas av byggnadsentreprenör och arkitekt före tillverkning. Kontrollmätning av samtliga öppningar skall utföras före tillverkning, mått inom parentes är cirkamått.

Utförande enligt fabrikantens grundutförande om ej annat anges. Partier dimensioneras av tillverkaren/leverantören. Enheter skall märkas enligt ritningens litterering, i förekommande fall med tillagt v eller h för hängning. Partierna skall kvalitetssäkras med P-märkning.

GEMENSAMMA EGENSKAPER

4. TYP

Partier av fabrikat Stålprofil AB, typ SP 300 respektive SP 700 eller likvärdigt. Profiltyp, se resp parti. Samtliga partier utförs med centrerad glasning med vinkelst. Gångjärn enligt tillverkarens standard.

5. MÅTT

Mått enligt uppställning, profilmått enligt detalj. OBS! Alla mått skall kontrolleras på plats. Erforderlig stålplåt runt om skall tillgodoses av tillverkaren.

9.2. YTBEHANDLING

Glaspartier inklusive dörrar levereras pulverlackerade. Pulverlackering ca 60 MY. Förbehandling enl. tillverkarens standard. Gångjärn ytbehandlas lika karm. Kulör: Gris 2900 Sablé YW355F - Interpon Collection Futura

10. GLAS

Glas skall vara klarglas, då ej annat anges. Montering enligt MTK:S föreskrifter. Glas dimensioneras av tillverkaren. Glas skall uppfylla kraven enl. BBR 8:35 beträffande säkerhet vid användning.

Kontrastmarkering av opalfilm kontrast min. 0,4 enl. NCS. Placering enl. senare ritning.

14. TRÖSKEL

Se respektive parti.

17. BESLAG

(Beslagning och funktion skall utföras enligt av RA Låshuset AB upprättade Beslagskort. Beslagskort är numrerade lika Dörrpositionsnummer.)

Beslagning och funktion enligt handling nr 6.2.5 "RAMBESKRIVNING OMBYGGNAD, EL- OCH TELESYSTEM".

17.9. ANMÄRKNING

All dragning av el skall utföras dold

HÄNVISNINGAR

PRINCIPDETALJER, SE RITNING A--43-4-2000003



FÖRKLARINGAR

Dörrpositionsnummer (Dxx) anger nya och befintliga dörrars unika placering, se planritningar. Figurer med dörr ses från gångjärnsidan. Hängning anges med utgångspunkt från gångjärnsidan. Vid pardörr avses gångdörrens hängning.

Bokstaven V resp. H efter angivet antal anger Väster- resp. Högerhängning. Mått är angivna i mm. Mått anger väggöppningsmått, VÖM, samt väggöppnings placering i höjddel över färdigt golv. OBS! Färdigt golv ligger 20 mm över befintligt golv. Ö.K. glaspartier skall linjera enligt uppställning. Egenskaper anges dels som GEMENSAMMA EGENSKAPER, dels som specifika för resp. littera. Egenskaper angivna för resp. littera gäller tillsammans med gemensamma egenskaper och ersätter i förekommande fall egenskaper angivna som gemensamma.

KODSYSTEM ENL. SIS 81 73 40.

- Littera
- Hängning/Antal
- Dörrtyp
- Mått
- Klassindelning
- Virkesklass
- Funktionskrav
- Värmeisolering
- Brandkrav
- Ljud
- Inbrottskydd
- Ventilation
- Dörrbladsyta
- Material
- Ytbehandling
- Glas
- Dörrbladskant
- Skyddsbeklädnad
- Karm
- Väggfjocklek
- Karmdjup
- Typ & material
- Påkörningsskydd
- Material
- Ytbehandling
- Tröskel
- Karmfyllägg
- Foder
- Beslag
- Ändring
- Beteckning
- Låstyp
- Trycke/Draghandtag
- Nyckelhållsskylt/Toaletthöör/Täckbricka
- Ringklocka/Kiköga
- Dörrstängare/Dörrautomatik/Spanjolett
- El-slutbleck/Magnetållare
- Anmärkning/Kortläsare/Armbågskontakt

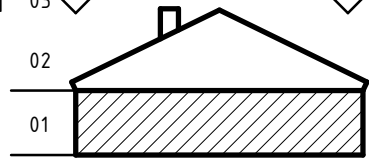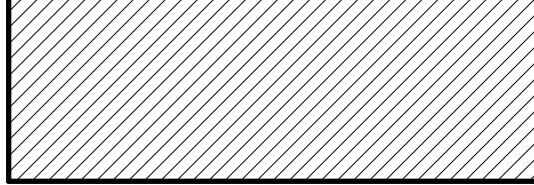BET	ÄNDRING AVSER		DATUM	SIGN
FÖRFRÅGNINGSUNDERLAG				
 HELSINGBORG FASTIGHETSFÖRVALTNINGEN				
FASTIGHET				
ORIENTEN 6				
RÖNNOWSKA SKOLAN, NYTT KÖK OCH MATSAL				
OBJEKTSNR	BYGGNADS-ID	PROJEKTNR		
1457	5-266088	60095		
BYGGNAD				
1457-20 – HUS V (BYGGNAD 449)				
ORIENTERINGSFIGUR				
PLAN 03				
				
DEL				
				
VÄSTRA SANDGATAN				
A	ARKITEKTLAGET SKÅNE AB		T: 042-19 96 00	
BR	FIRETECH ENGINEERING EMRON AB		T: 010-150 14 00	
E	DEVELCON AB		T: 079-020 27 02	
K	ÅKERMANS INGENJÖRSBYRÅ AB		T: 042-12 00 10	
M	TYRÉNS AB		T: 010-452 20 00	
S	SWECO SVERIGE AB		T: 08-695 60 00	
SK	STORKÖKSVISION		T: 040-744 29	
V	SWECO SVERIGE AB		T: 08-695 60 00	
W	SWECO SVERIGE AB		T: 08-695 60 00	
UPPDRAGSNR		ANSVARIG		
22063_00		BRANISLAV KUZMANOVIC		
DATUM	RITAD/KONSTR AV	HANDLAGGARE	SYSTEMBETECKNING	
2025-01-27	MVJ	BK	43-4	
HUS 20				
INVÄNDIGA GLASPARTIER				
UPPSTÄLLNING				
—				
SKALA	NUMMER			REV
1 : 50	A--43-4-2000001			

ORIGINALFORMAT: A1

