


2025-01-23 14:34:12 \\ALAG-FS\RedirectedFolders\mkaelb\My Documents\A--00_V20001_mkaelb@arkitektlaget.se.rvt

D9a
(D24, D25)

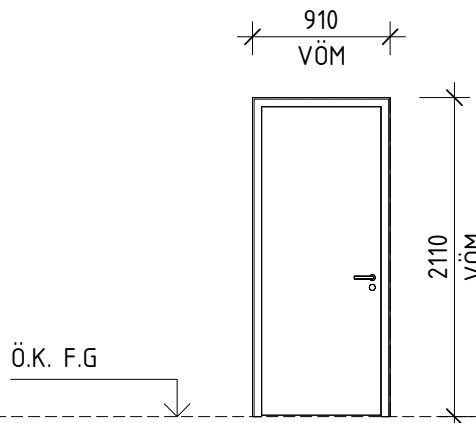


Typ	D9a
Beskrivning	Slagdörr
Antal H / V	1H/1V
Antal	2

4. Enkel slagdörr till WC.
8.3 Ljudkrav R_w 25 dB
13.2 Karmdjup 118 mm
14. Anslagsströskel av trä
17. Beslagning enligt Beslagskort D24, D25

- 17.5 WC-behör, öppningsbar med fyrkantsnyckel

D10a
(D23, D39)

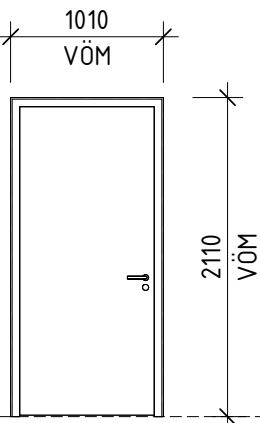


Typ	D10a
Beskrivning	Slagdörr
Antal H / V	0H/2V
Antal	2

4. Enkel slagdörr till RWC
8.3 Ljudkrav R_w 25 dB
13.2 Karmdjup 118 mm
14. Massiv gummitröskel med släpläst
17. Beslagning enligt Beslagskort D23, D39

- 17.4 Draghandtag monterat på insida dörrblad
17.5 RWC-behör, öppningsbar med fyrkantsnyckel

D10b
(D38)

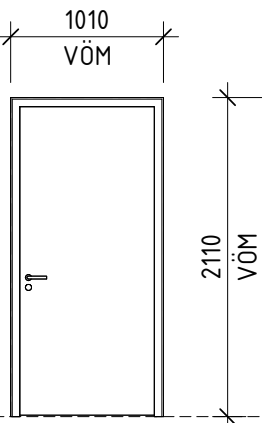


Typ	D10b
Beskrivning	Slagdörr
Antal H / V	1H/0V
Antal	1

4. Enkel slagdörr till OMB
8.3 Ljudkrav R_w 25 dB
13.2 Karmdjup 118 mm
14. Anslagsströskel av trä
17. Beslagning enligt Beslagskort D38

- 17.5 WC-behör, öppningsbar med fyrkantsnyckel

D10c
(D22)

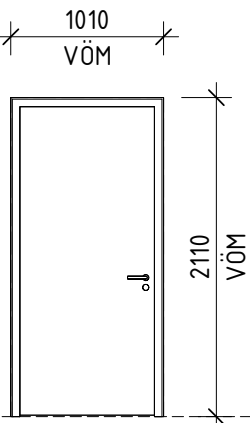

Typ	D10c
Beskrivning	Slagdörr
Antal H / V	0H/1V
Antal	1

4. Enkel slagdörr till STÄD
13.2 Larmdjup 118 mm
14. Låg tröskelplatta av trä
17. Beslagning enligt Beslagskort D22

- 17.5 WC-behör, öppningsbar med fyrkantsnyckel

FÖRESKRIFTER

Arbets- och detaljritningar skall upprättas av leverantören och godkännas av byggnadsentreprenör och arkitekt före tillverkning. Kontrollmätning av samtliga öppningar skall utföras före tillverkning, angivna mått inom parentes är cirkamått.

Utförande enligt fabrikantens grundutförande om ej annat anges. Enheter skall märkas enligt ritningens litterering, i förekommande fall med tillagt v eller h för hängning.

GEMENSAMMA EGENSKAPER

4. TYP
Massivdörrar fabrikat Swedoor eller likvärdigt.

5. MÅTT
Erforderlig ställplats runt om skall fyllgodoses av tillverkaren.

9. DÖRRBLADSYTA
Slåta dörrblad.

9.1 MATERIAL
Dörrblad belagda med laminat.
Kulör: Formica F9266 MAT Citadel, NCS S 6502-Y

11 DÖRRBLADSKANT
Plastkantlist runtom.
Kulör: NCS S 6502-Y

13 KARM
Karm av furu.

13.6 YTBEHANDLING
Fabriksmålad karm.
Kulör: NCS S 6502-Y

14. TRÖSKEL
Se respektive dörr.

17. BESLAG
(Beslagning och funktion skall utföras enligt av RA Låshuset AB upprättade Beslagskort. Beslagskort är numererade lika Dörrpositionsnummer.)

Beslagning och funktion enligt handling nr 6.25 "RAMBESKRIVNING OMBYGGNAD, EL- OCH TELESYSTEM".

17.9. ANMÄRKNING
All dragning av el skall utföras dold.

FÖRKLARINGAR



Dörrpositionsnummer (Dxx) anger nya och befintliga dörrars unika placering, se planritningar. Figurer ses från utsidan. Hängning anges med utgångspunkt från gångjärnsidan. Vid pardörr avses gångdörrrens hängning. Bokstaven V resp. H efter angivet antal anger Väster- resp. Högerhängning. Mått är angivna i mm. Mått anger väggöppningsmått, VÖM, samt väggöppningens placering i höjdded över Färdigt Golv.

Egenskaper anges dels som GEMENSAMMA EGENSKAPER, dels som specifika för resp. littera. Egenskaper angivna för resp. littera gäller tillsammans med gemensamma egenskaper och ersätter i förekommande fall egenskaper angivna som gemensamma.

- KODSYSTEM ENL SIS 81 73 40.
2. Littera
3. Hängning/Antal
4. Dörrtyp
5. Mått
6. Klassindelning
7. Virkesklass
8. Funktionskrav
8.1 Värmeisolering
8.2 Brandkrav
8.3 Ljud
8.4 Inbrottskydd
8.5 Ventilation
9. Dörrbladsyta
9.1 Material
9.2 Ytbehandling
10. Glas
11. Dörrbladskant
12. Skyddsbeklädnad
13. Karm
13.1 Väggtjocklek
13.2 Karmdjup
13.3 Typ & material
13.4 Påkörningsskydd
13.5 Material
13.6 Ytbehandling
14. Tröskel
15. Karmtillägg
16. Foder
17. Beslag
17.1 Ändring
17.2 Beteckning
17.3 Låstyp
17.4 Trycke/Draghandtag
17.5 Nyckelhåsskylt/Toalettbehör/Täckbricka
17.6 Ringklocka/Kiköga
17.7 Dörrstängare/Dörrautomatik/Spanjolett
17.8 EL-slutbleck/Magnethållare
17.9 Anmärkning/Kortläsare/Armbågskontakt

HÄNVISNINGAR

6.3.1 A-HANDLINGSFÖRTECKNING
PLANRITNINGAR A--40--1-2001111, A--40--1-2001112

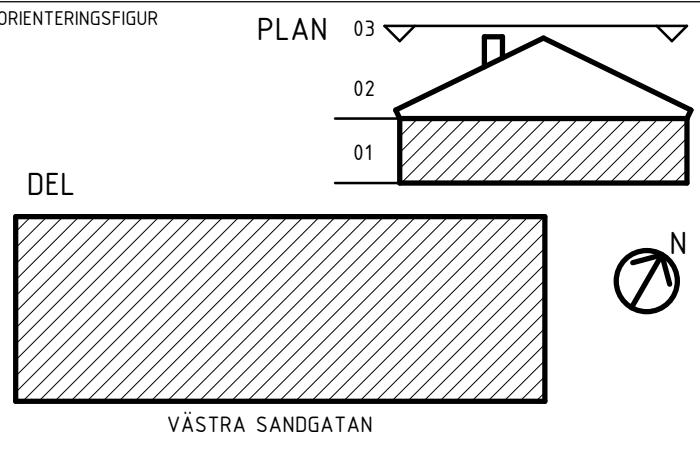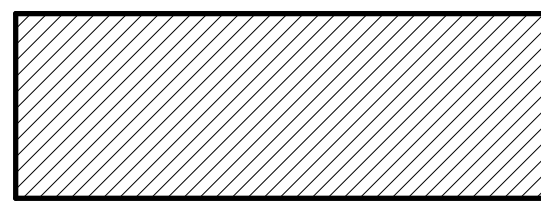BET	ÄNDRING AVSER	DATUM	SIGN																											
FÖRFRÅGNINGSUNDERLAG																														
 HELSINGBORG FASTIGHETSFÖRVALTNINGEN																														
FASTIGHET ORIENTEN 6 RÖNNOWSKA SKOLAN, NYTT KÖK OCH MATSAL																														
OBJEKTSNR 1457	BYGGNADS-ID 5-266088	PROJEKTNR 60095																												
BYGGNAD 1457-20 - HUS V (BYGGNAD 449)																														
ORIENTERINGFIGUR PLAN 03  DEL  VÄSTRA SANDGATAN																														
<table><tr><td>(A)</td><td>ARKITEKTLAGET SKÅNE AB</td><td>T: 042-19 96 00</td></tr><tr><td>BR</td><td>FIRETECH ENGINEERING EMRON AB</td><td>T: 010-150 14 00</td></tr><tr><td>E</td><td>DEVELCON AB</td><td>T: 079-020 27 02</td></tr><tr><td>K</td><td>ÅKERMANS INGENJÖRSBYRÅ AB</td><td>T: 042-12 00 10</td></tr><tr><td>M</td><td>TYRÉNS AB</td><td>T: 010-452 20 00</td></tr><tr><td>S</td><td>SWECO SVERIGE AB</td><td>T: 08-695 60 00</td></tr><tr><td>SK</td><td>STORKÖKSVISION</td><td>T: 040-744 29</td></tr><tr><td>V</td><td>SWECO SVERIGE AB</td><td>T: 08-695 60 00</td></tr><tr><td>W</td><td>SWECO SVERIGE AB</td><td>T: 08-695 60 00</td></tr></table>				(A)	ARKITEKTLAGET SKÅNE AB	T: 042-19 96 00	BR	FIRETECH ENGINEERING EMRON AB	T: 010-150 14 00	E	DEVELCON AB	T: 079-020 27 02	K	ÅKERMANS INGENJÖRSBYRÅ AB	T: 042-12 00 10	M	TYRÉNS AB	T: 010-452 20 00	S	SWECO SVERIGE AB	T: 08-695 60 00	SK	STORKÖKSVISION	T: 040-744 29	V	SWECO SVERIGE AB	T: 08-695 60 00	W	SWECO SVERIGE AB	T: 08-695 60 00
(A)	ARKITEKTLAGET SKÅNE AB	T: 042-19 96 00																												
BR	FIRETECH ENGINEERING EMRON AB	T: 010-150 14 00																												
E	DEVELCON AB	T: 079-020 27 02																												
K	ÅKERMANS INGENJÖRSBYRÅ AB	T: 042-12 00 10																												
M	TYRÉNS AB	T: 010-452 20 00																												
S	SWECO SVERIGE AB	T: 08-695 60 00																												
SK	STORKÖKSVISION	T: 040-744 29																												
V	SWECO SVERIGE AB	T: 08-695 60 00																												
W	SWECO SVERIGE AB	T: 08-695 60 00																												
<table><tr><td>UPPDRAGSNR 22063_00</td><td colspan="3">ANSVARIG BRANISLAV KUZMANOVIC</td></tr><tr><td>DATUM 2025-01-27</td><td>RITAD/KONSTR AV MB</td><td>HANDLAGGARE BK</td><td>SYSTEMBETECKNING 43-4</td></tr></table>				UPPDRAGSNR 22063_00	ANSVARIG BRANISLAV KUZMANOVIC			DATUM 2025-01-27	RITAD/KONSTR AV MB	HANDLAGGARE BK	SYSTEMBETECKNING 43-4																			
UPPDRAGSNR 22063_00	ANSVARIG BRANISLAV KUZMANOVIC																													
DATUM 2025-01-27	RITAD/KONSTR AV MB	HANDLAGGARE BK	SYSTEMBETECKNING 43-4																											
HUS 20 INVÄNDIGA DÖRRAR UPPSTÄLLNING																														
-																														
SKALA 1 : 50	NUMMER A--43-4-2000011		REV																											

ORIGINALFORMAT: A1

