




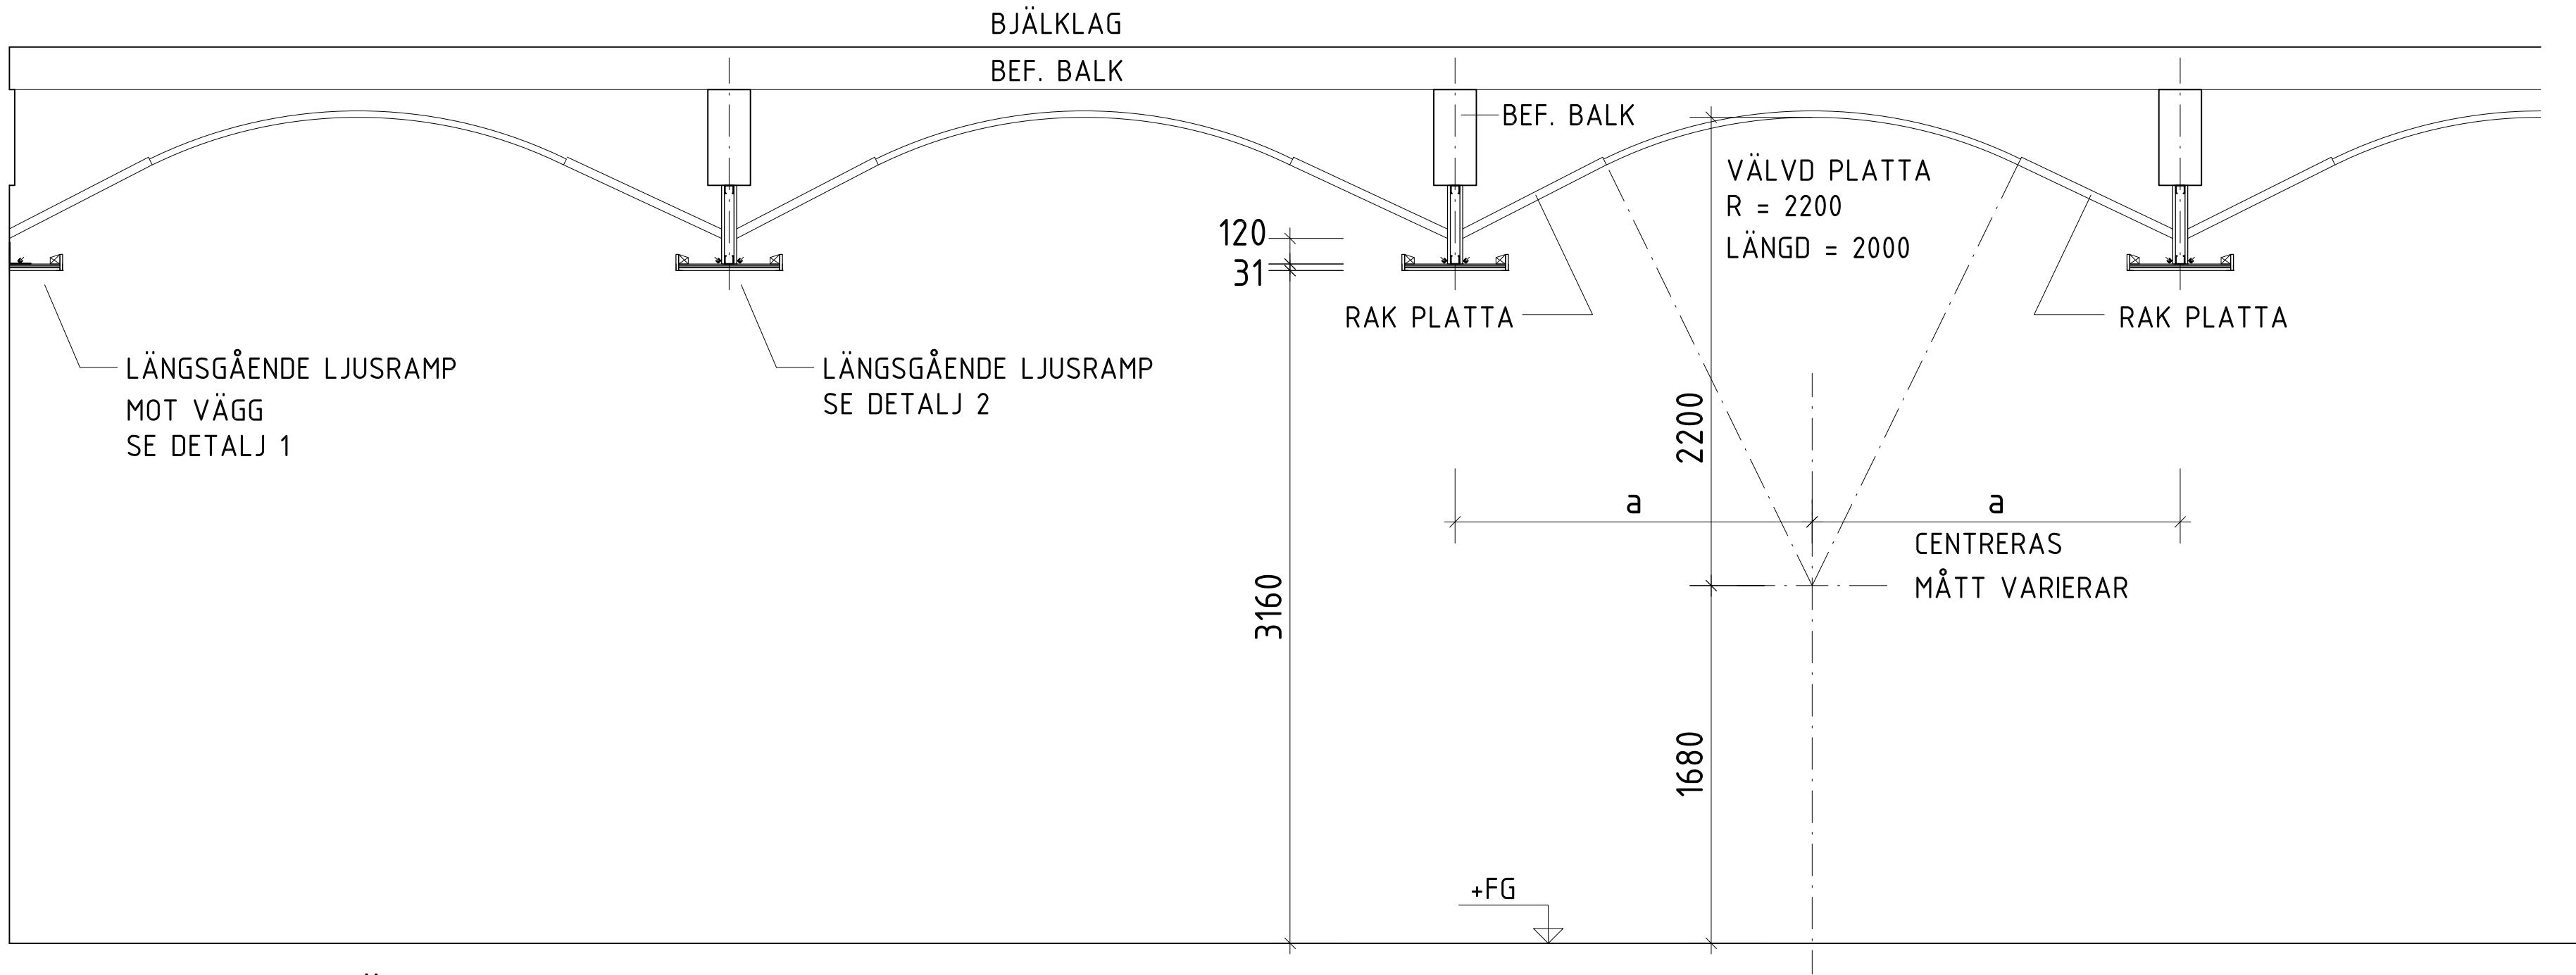

PRINCIPSEKTION VÄLVD UNDERTAK
SKALA 1:25

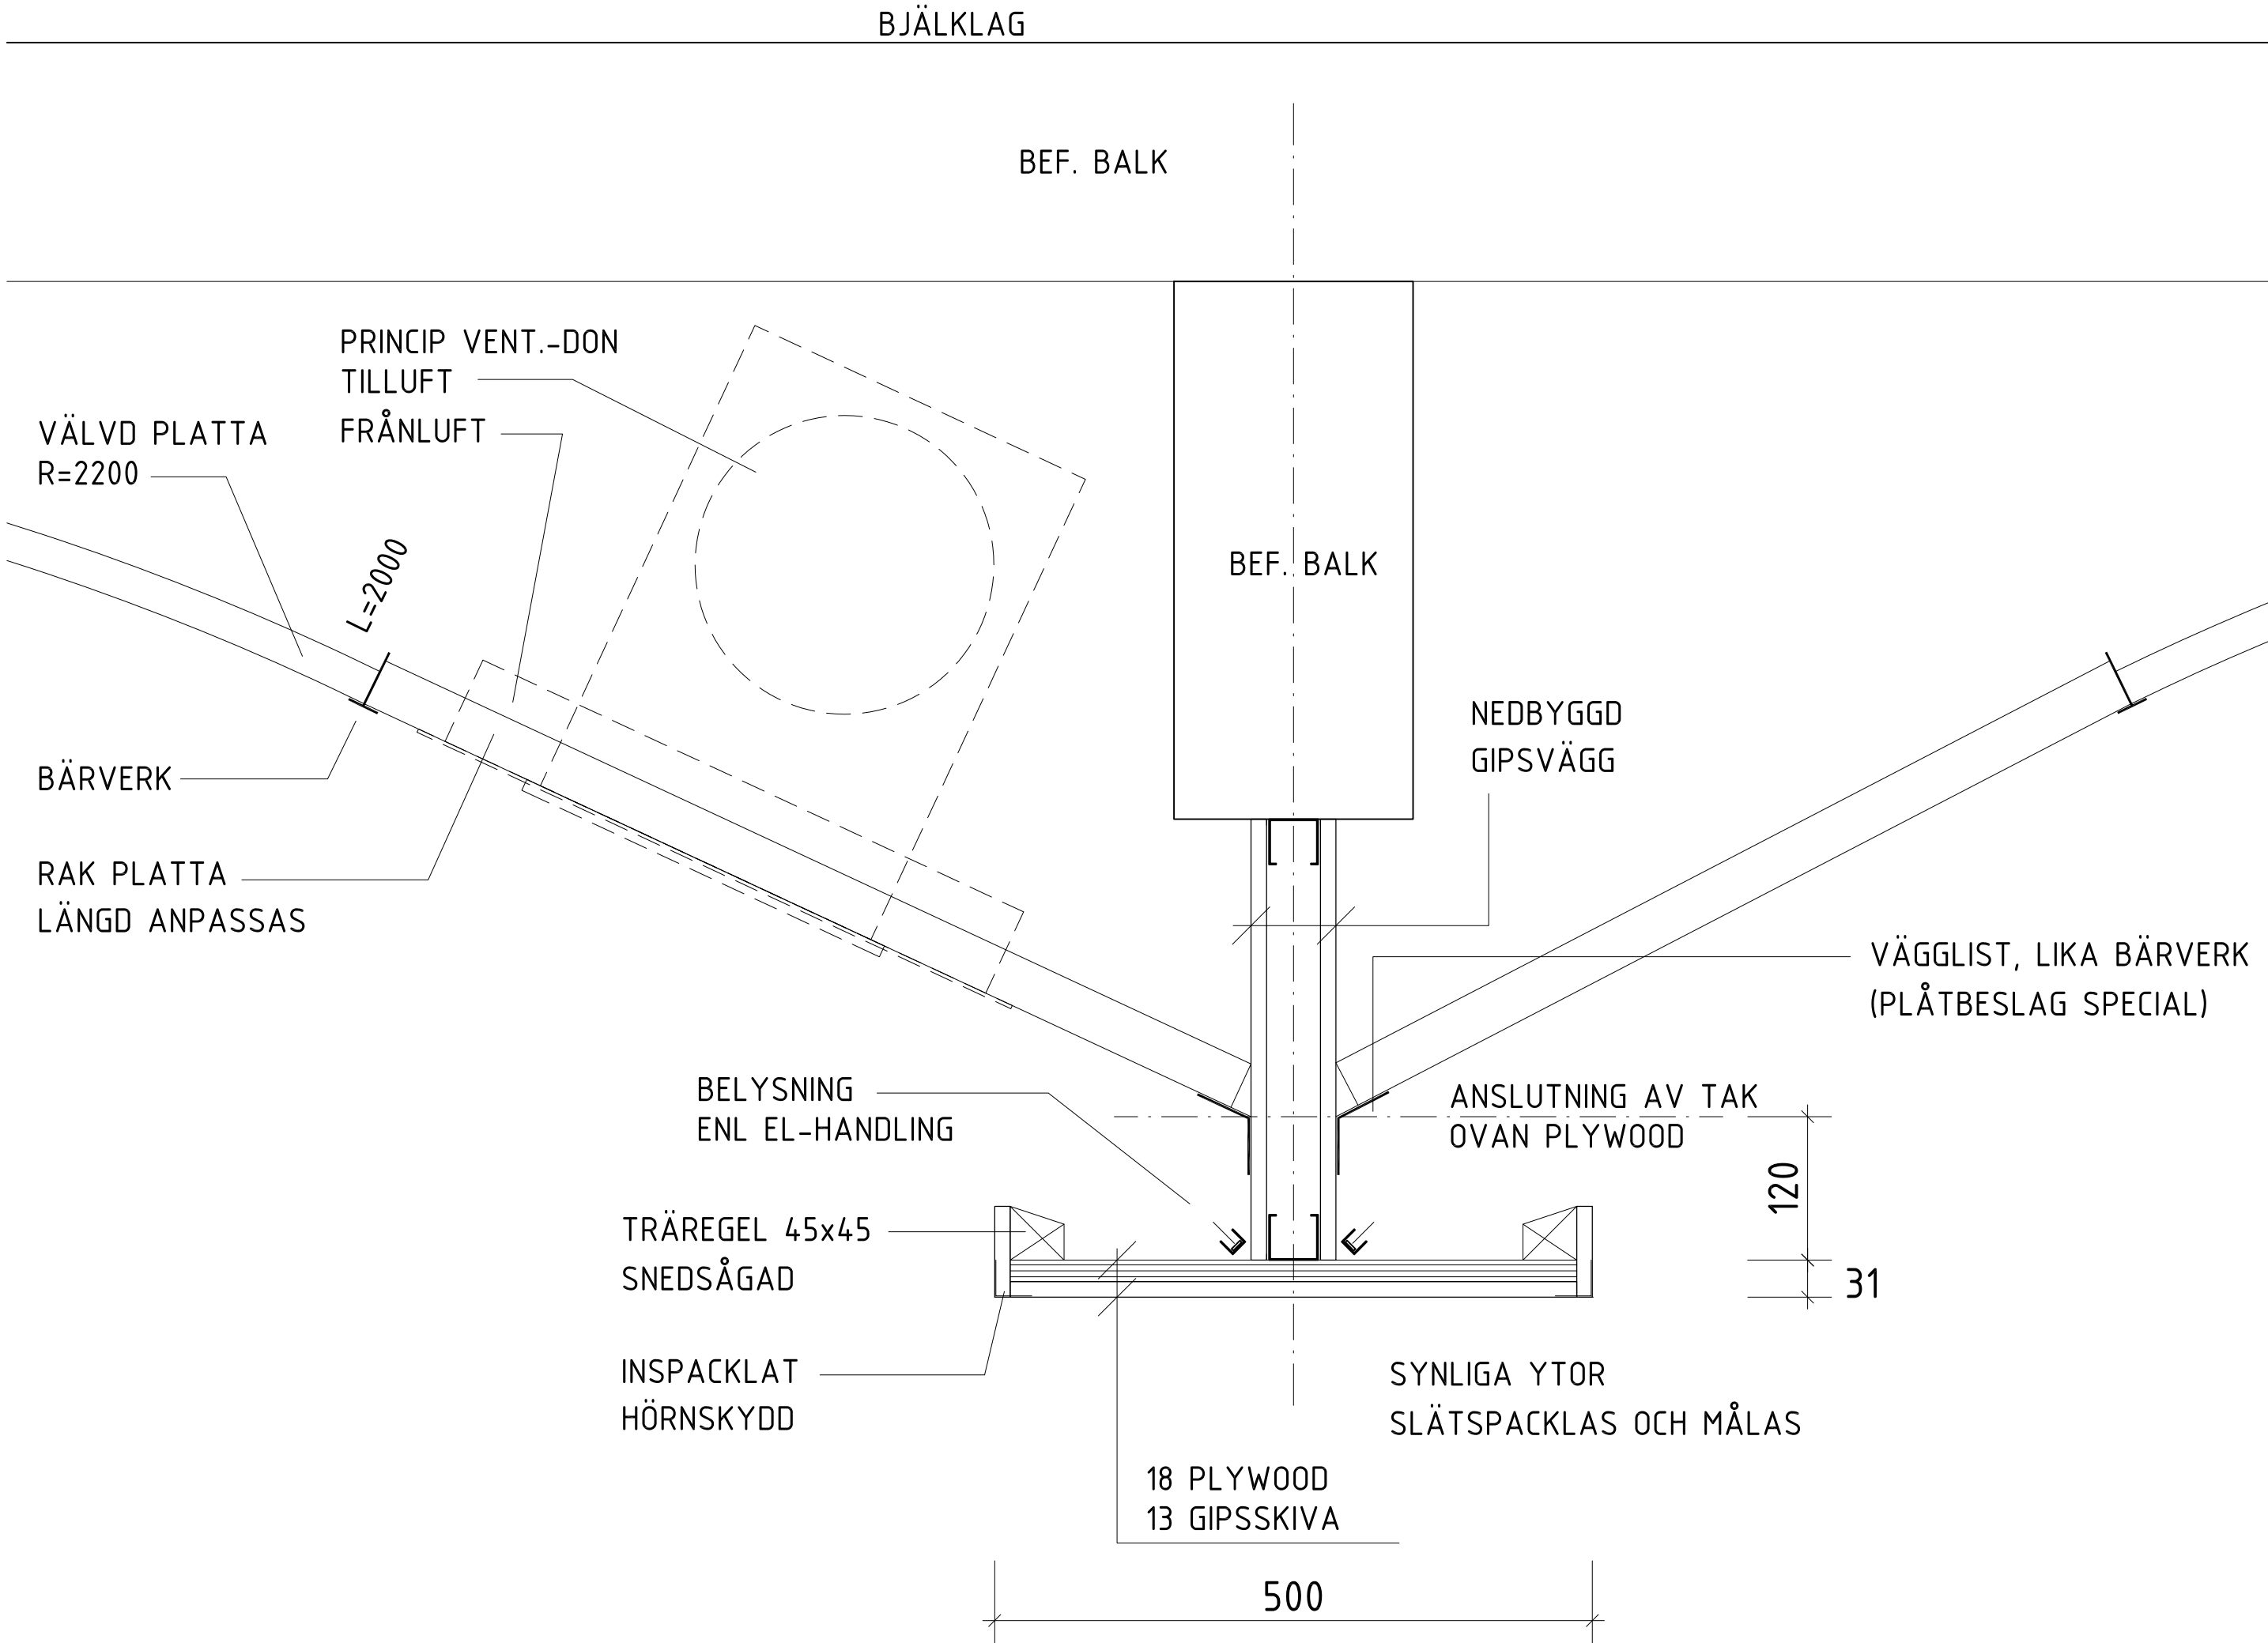

DET. 2
LÄNGSGÅENDE LJUSRAMP
SKALA 1:5

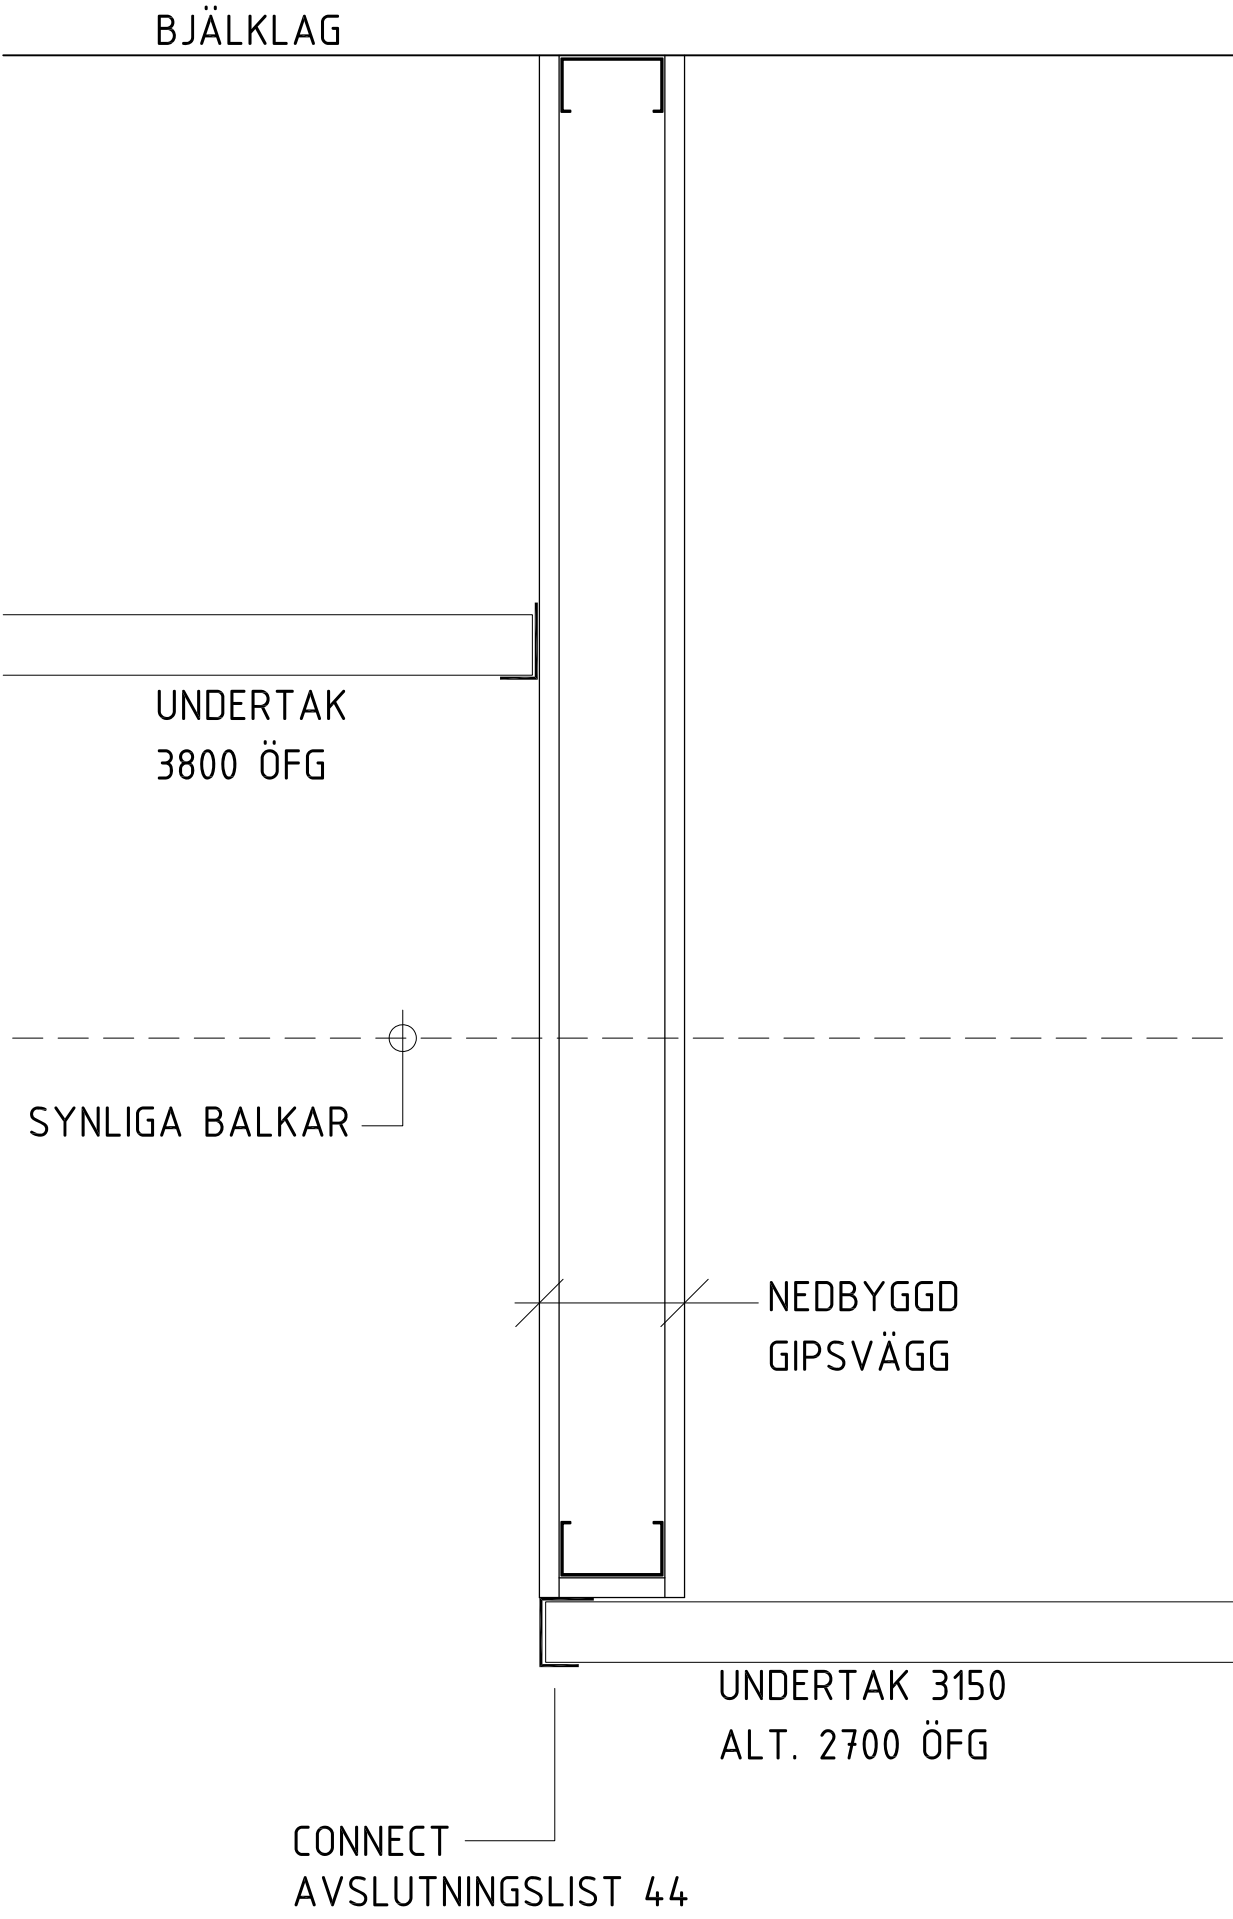

DET. 3
NIVÅÖVERGÅNG UNDERTAK
SKALA 1:5

FÖRKLARINGAR

SE UNDERTAKSPÄNEN, RITN. NR A--43-1-2001111
OCH A--43-1-2001112

FÖRESKRIFTER

UT4 VÄLVD UNDERTAK

VÄLVD PLATTA:
LJUDABSORBENTER TYP ECOPHON FOCUS FLEXIFORM A
2000 x 600 x 30 KULÖR VIT, NCS S 0500-N
LJUDABSORPTIONSKLASS A

RAK PLATTA:
LJUDABSORBENT TYP ECOPHON MASTER A
1200 x 600 x 40 KULÖR VIT, NCS S 0500-N
LJUDABSORPTIONSKLASS A

BÄRVERK T24 VIT 01

PROVMONTAGE SKALL UTFÖRAS MED VÄLVT TAK OCH
LÄNGSGÅENDE LJUSRAMP FÖR ATT FASTSTÄLLA
PLACERING, MÅTT OCH DIMENSIONER MED HÄNSYN TILL
BELYSNING (EJ SYNliga INSTALLATIONER, ACCEPTABEL
LJUSBILD) OCH PLACERING AV VENT-DON OCH ÖVRIGA
INSTALLATIONER.
PROVMONTAGE UTFÖRS I ETT FACK PÅ EN LÄNGD AV
3 m, FÖR GODKÄNNANDE FÖRE BESTÄLLNING AV
RESTERANDE MATERIAL / BELYSNINGSARMATURER ETC.

HÄNVISNINGAR

6.3.1 A-HANDLINGSFÖRTECKNING
6.2.1 RAMBESKRIVNING BYGG
6.2.2 RUMSBESKRIVNING

BET	ÄNDRING AVSER	DATUM	SIGN
FÖRFRÅGNINGSUNDERLAG			
HELSINGBORG FASTIGHETSFÖRVALTNINGEN			
FASTIGHET ORIENTEN 6			
RÖNNOWSKA SKOLAN, NYTT KÖK OCH MATSAL			
OBJEKTSNR 1457	BYGGNADS-ID 5-266088	PROJEKTNR 60095	
BYGGNAD 1457-20 - HUS V (BYGGNAD 449)			
ORIENTERINGSGRUPP PLAN 03 02 01			
DEL 111 112 113 VÄSTRA SANDGATAN			
A ARKITEKTLAGET SKÅNE AB T: 042-19 96 00			
BR FIRETECH ENGINEERING EMRON AB T: 010-150 14 00			
E DEVELCON AB T: 079-020 27 02			
K ÅKERMANS INGENJÖRSBYRÅ AB T: 042-12 00 10			
M TYRÉNS AB T: 010-452 20 00			
S SWECO SVERIGE AB T: 08-695 60 00			
SK STORKÖKSVISION T: 040-744 29			
V SWECO SVERIGE AB T: 08-695 60 00			
W SWECO SVERIGE AB T: 08-695 60 00			
UPPDRAGSNR 22063,00	ANSVARIG BRANISLAV KUZMANOVIC		
DATUM 2025-01-27	RITAD/KONSTR AV MB	HANDLAGGARE BK	SYSTEMBETECKNING -
HUS 20 UNDERTAK PRINCIPDETALJER			
SKALA (A1) 1:25, 1:5	NUMMER A--43-4-2001115		REV

ORIGINALFORMAT: A1