


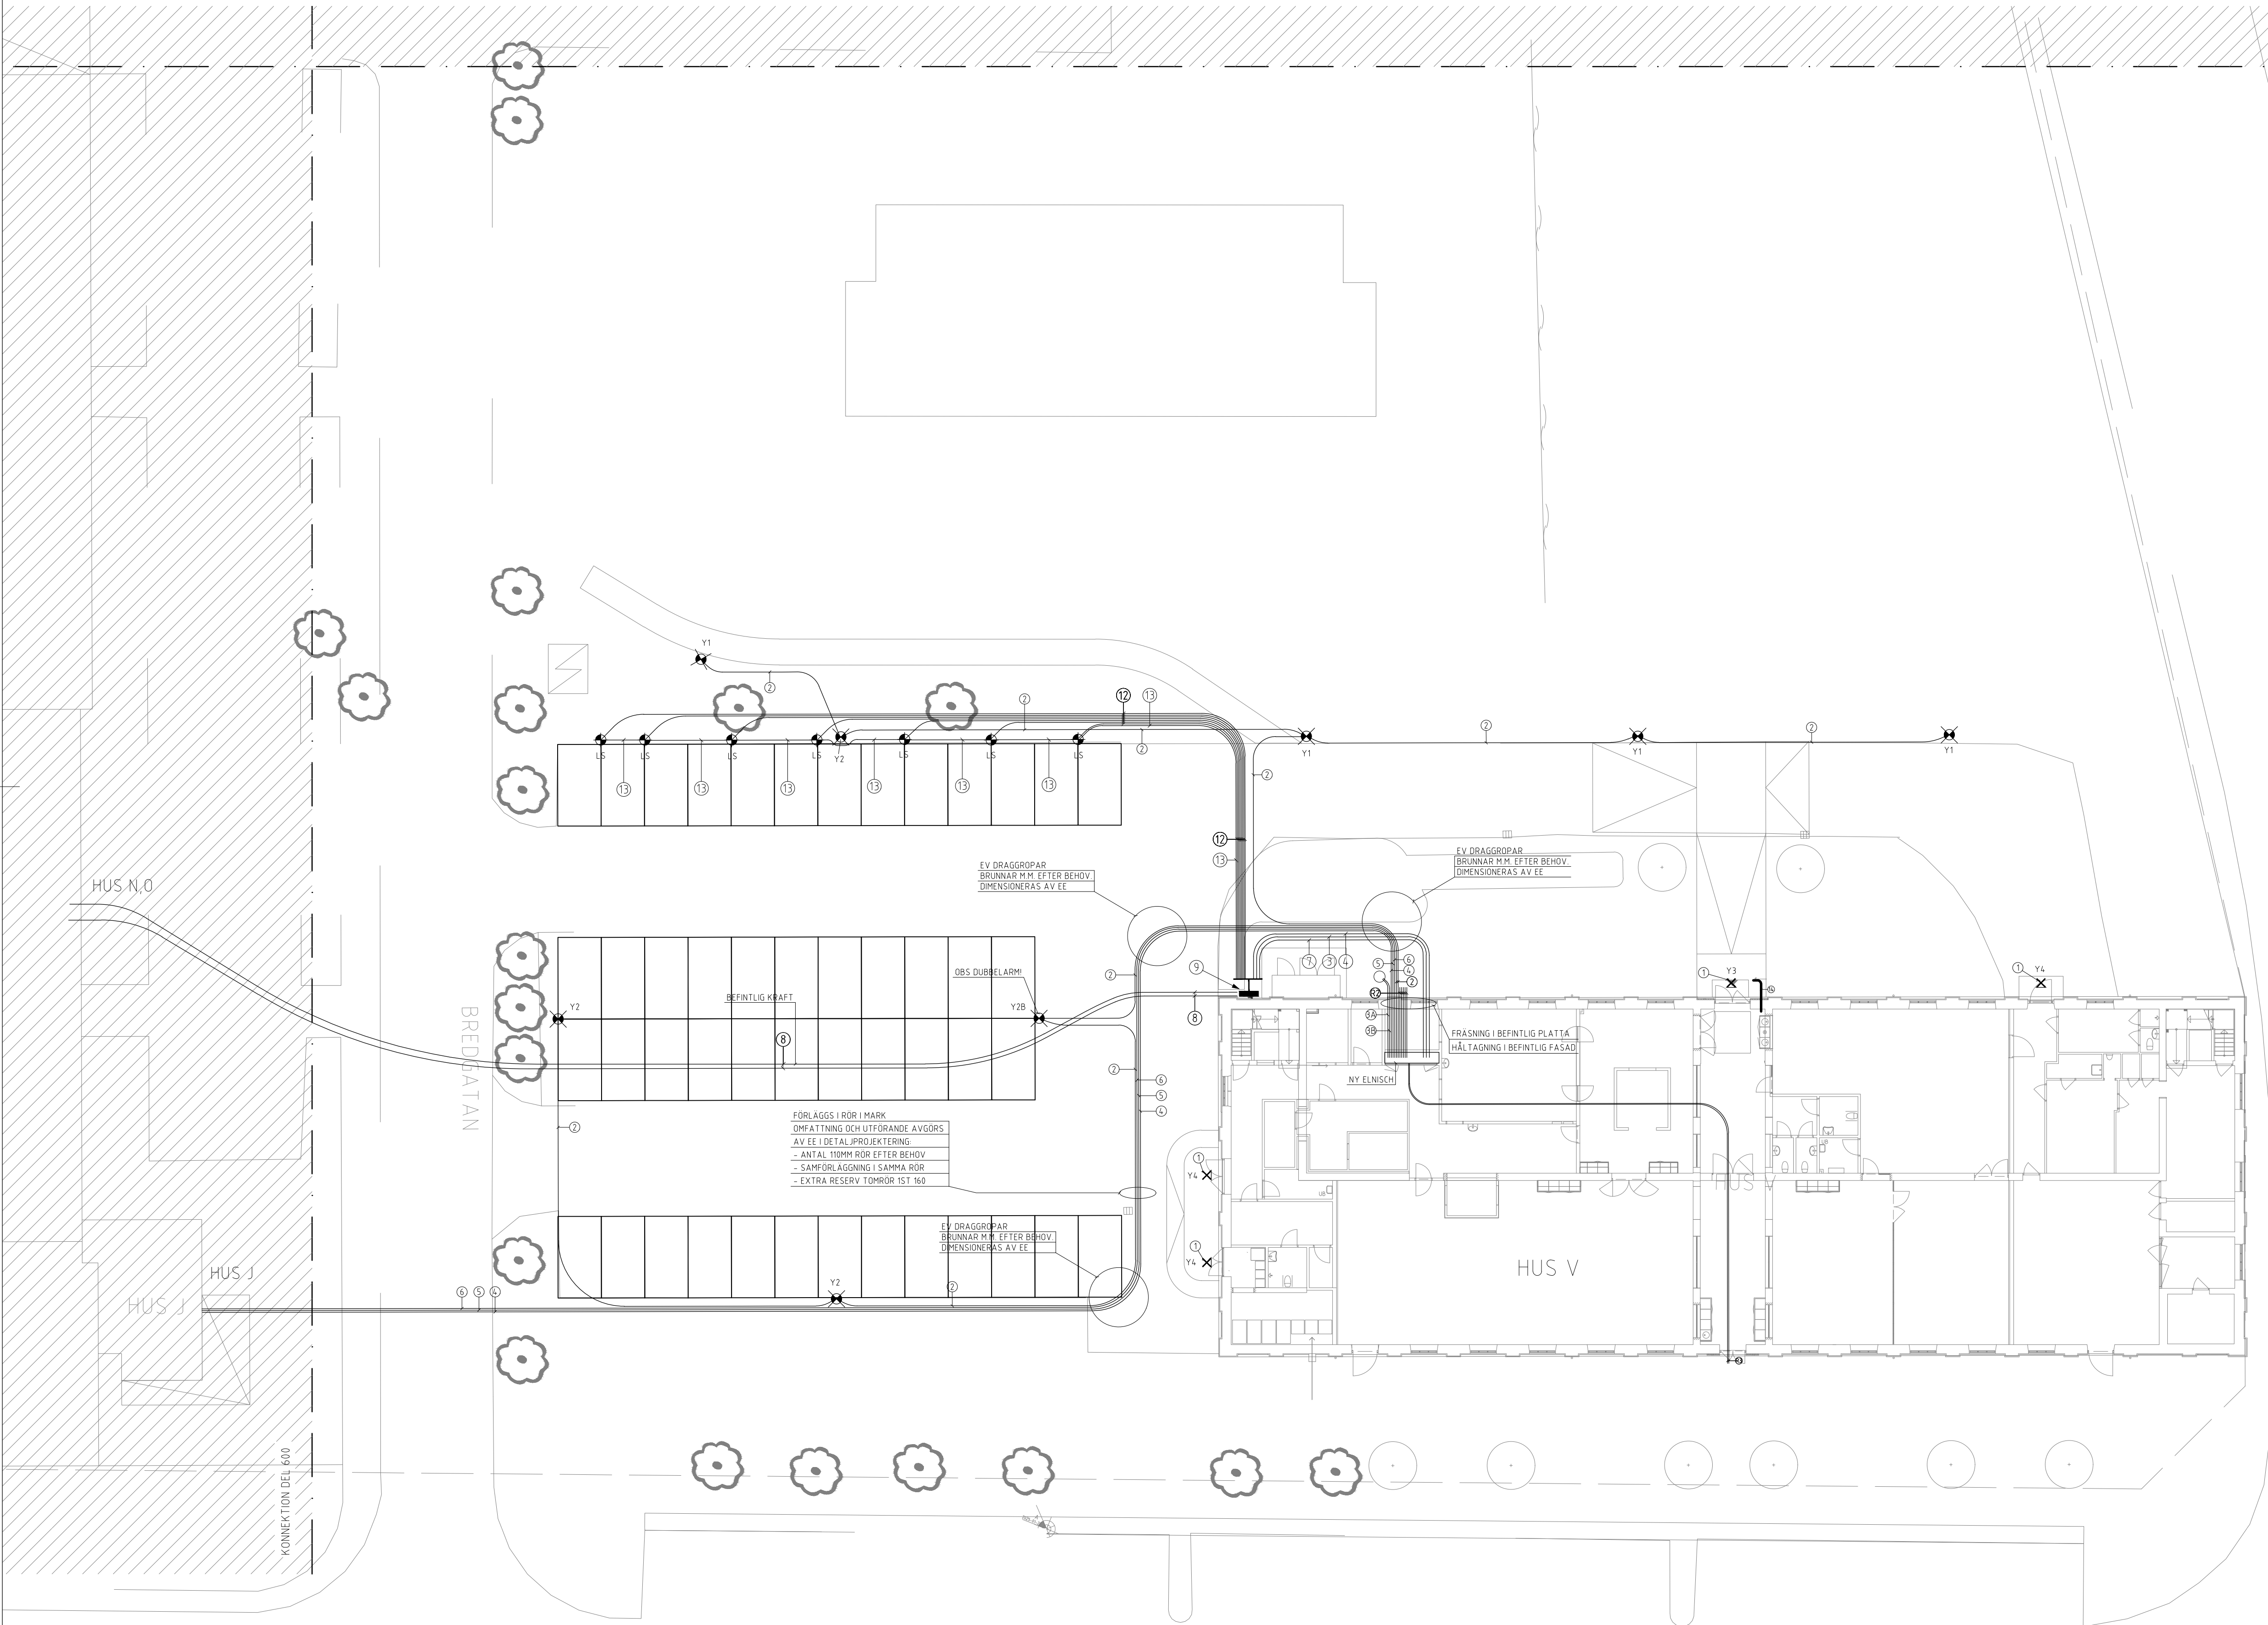

FÖRKLARINGAR

PRICKAD TYPRITNING FÖR YTTERBELYSNING TILL MATSAL.
BILAGA TILL RAMBESKRIVNING OCH RUMSFUNKTIONSPROGRAM.
SE ÄVEN:
- BESKRIVANDE TEXT I RAMBESKRIVNING
- ÖMFATTNING I RUMSFUNKTIONSPROGRAM
- ARMATYRFÖRTECKNING I RUMSFUNKTIONSPROGRAM
- ARKITEKT- OCH MARK-/RITNINGAR
- BILAGA MED LJUSKONCEPT LJUSBERÄKNING

SYMBOLER

- Yx BELYSNINGSARMATUR PÅ STOLPE
- Yx VÄGGMONTERAD ARMATUR
- LS FRAMTIDA LADDSTOLPE
- LS RÖR AVSLUTAS I MARK MED SONDBOLL

HÄNVISNINGAR

- ① YTTERBELYSNING PÅ FASAD. SE ÄVEN A-RITNING
- ② 50-RÖR FÖR STOLPBELYSNING. MATNING: 5G10.
- ③A 50-RÖR. FETTAVSKILJARE, KRAFT.
- ③B 50-RÖR. FETTAVSKILJARE, LARM.
- ④ 50-RÖR, GRÖNT. INKOMMANDE PASSAGE, OMNIS.
- ⑤ 50-RÖR, GRÖNT. INKOMMANDE FIBER.
- ⑥ 50-RÖR. INKOMMANDE BRANDLARM.
- ⑦ 320-RÖR. INKOMMANDE KRAFT
- ⑧ BEF. KANALISATION BEF. INKOMMANDE MATNING. BEF. MATNING: 27//AKKJ 3x240+95
- ⑨ MARKSKÅP MED FÖRDELNING. ATK.
- ⑩ VAKANT
- ⑪ VAKANT
- ⑫ 50-RÖR FÖR FRAMTIDA LADDPLATSER. KRAFT.
- ⑬ 50-RÖR FÖR FRAMTIDA LADDPLATSER. KOMMUNIKATION.
- ⑭ 20-RÖR TILL STOLPE FÖR ARMBÅGSKONTAKT.
- R1 160-RÖR. RESERV.
- R2 50-RÖR. RESERV. NORRSIDA. TOTALT 5st.
- R3 50-RÖR. RESERV. SYDSIDA. TOTALT 2st.

BET	ÄNDRING AVSER	DATUM	SIGN.
-----	---------------	-------	-------

FÖRFRÅGNINGSUNDERLAG

 **HELSINGBORG**
FASTIGHETSFÖRVALTNINGEN

FASTIGHET


ORIENTEN 6

RÖNNOWSKA SKOLAN, NYTT KÖK OCH MATSAL

OBJEKTSNR	BYGGNADS-ID	PROJEKTR
1457	-	60095

BYGGNAD

1457-0 - Gemensam

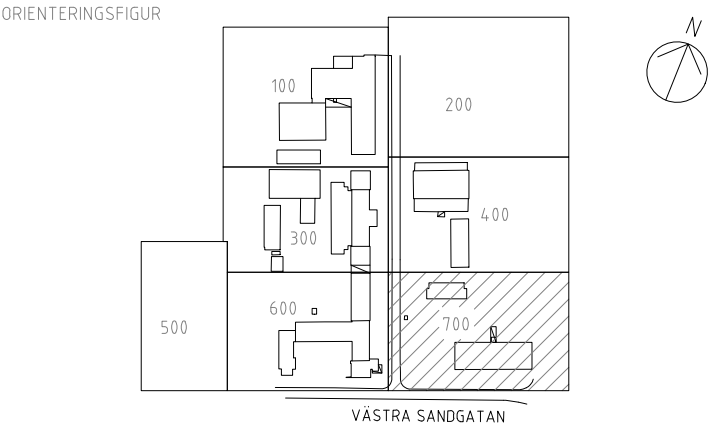

A	ARKITEKTLAGET SKÅNE AB	T: 042-19 96 00
BR	FIRETECH ENGINEERING EMRON AB	T: 010-150 14 00
E	DEVELCON AB	T: 079-020 27 02
K	ÅKERMANS INGENJÖRSBYRÅ AB	T: 042-12 00 10
M	TYRÉNS AB	T: 010-452 20 00
S	SWECO SVERIGE AB	T: 08-695 60 00
SK	STORKÖKSVISION AB	T: 040-744 29
V	SWECO SVERIGE AB	T: 08-695 60 00
W	SWECO SVERIGE AB	T: 08-695 60 00
C	ZYNKA BIM AB	T: 0734-45 98 99

UPPDRAGSNR	ANSVARIG
23053,001	NICKLAS HULT
DATUM	RITAD/KONSTR AV
2025-01-27	NH
	HANDLAGGARE
	NH
	SYSTEMBETECKNING
	-

GEMENSAM
MARKOMRÅDE, DEL 700
ELINSTALLATIONER
PRICKAD TYPRITNING

SKALA (A1)	NUMMER	REV
1:200	E-631-1-0000700	

ORIGINALFORMAT: A1