


PRICKAD TYPRITNING FÖR BELYSNING I MATSALAR.
BILAGA TILL RAMBESKRIVNING OCH RUMSFUNKTIONSPROGRAM

BELYSNING FÖR ÖVRIGA BYGGNADSELDAR DÄR BELYSNING EJ
ÄR RITAT SKA FÄRDIGPROJEKTERAS AV EE ENLIGT
RAMBESKRIVNING OCH RUMSFUNKTIONSPROGRAM.

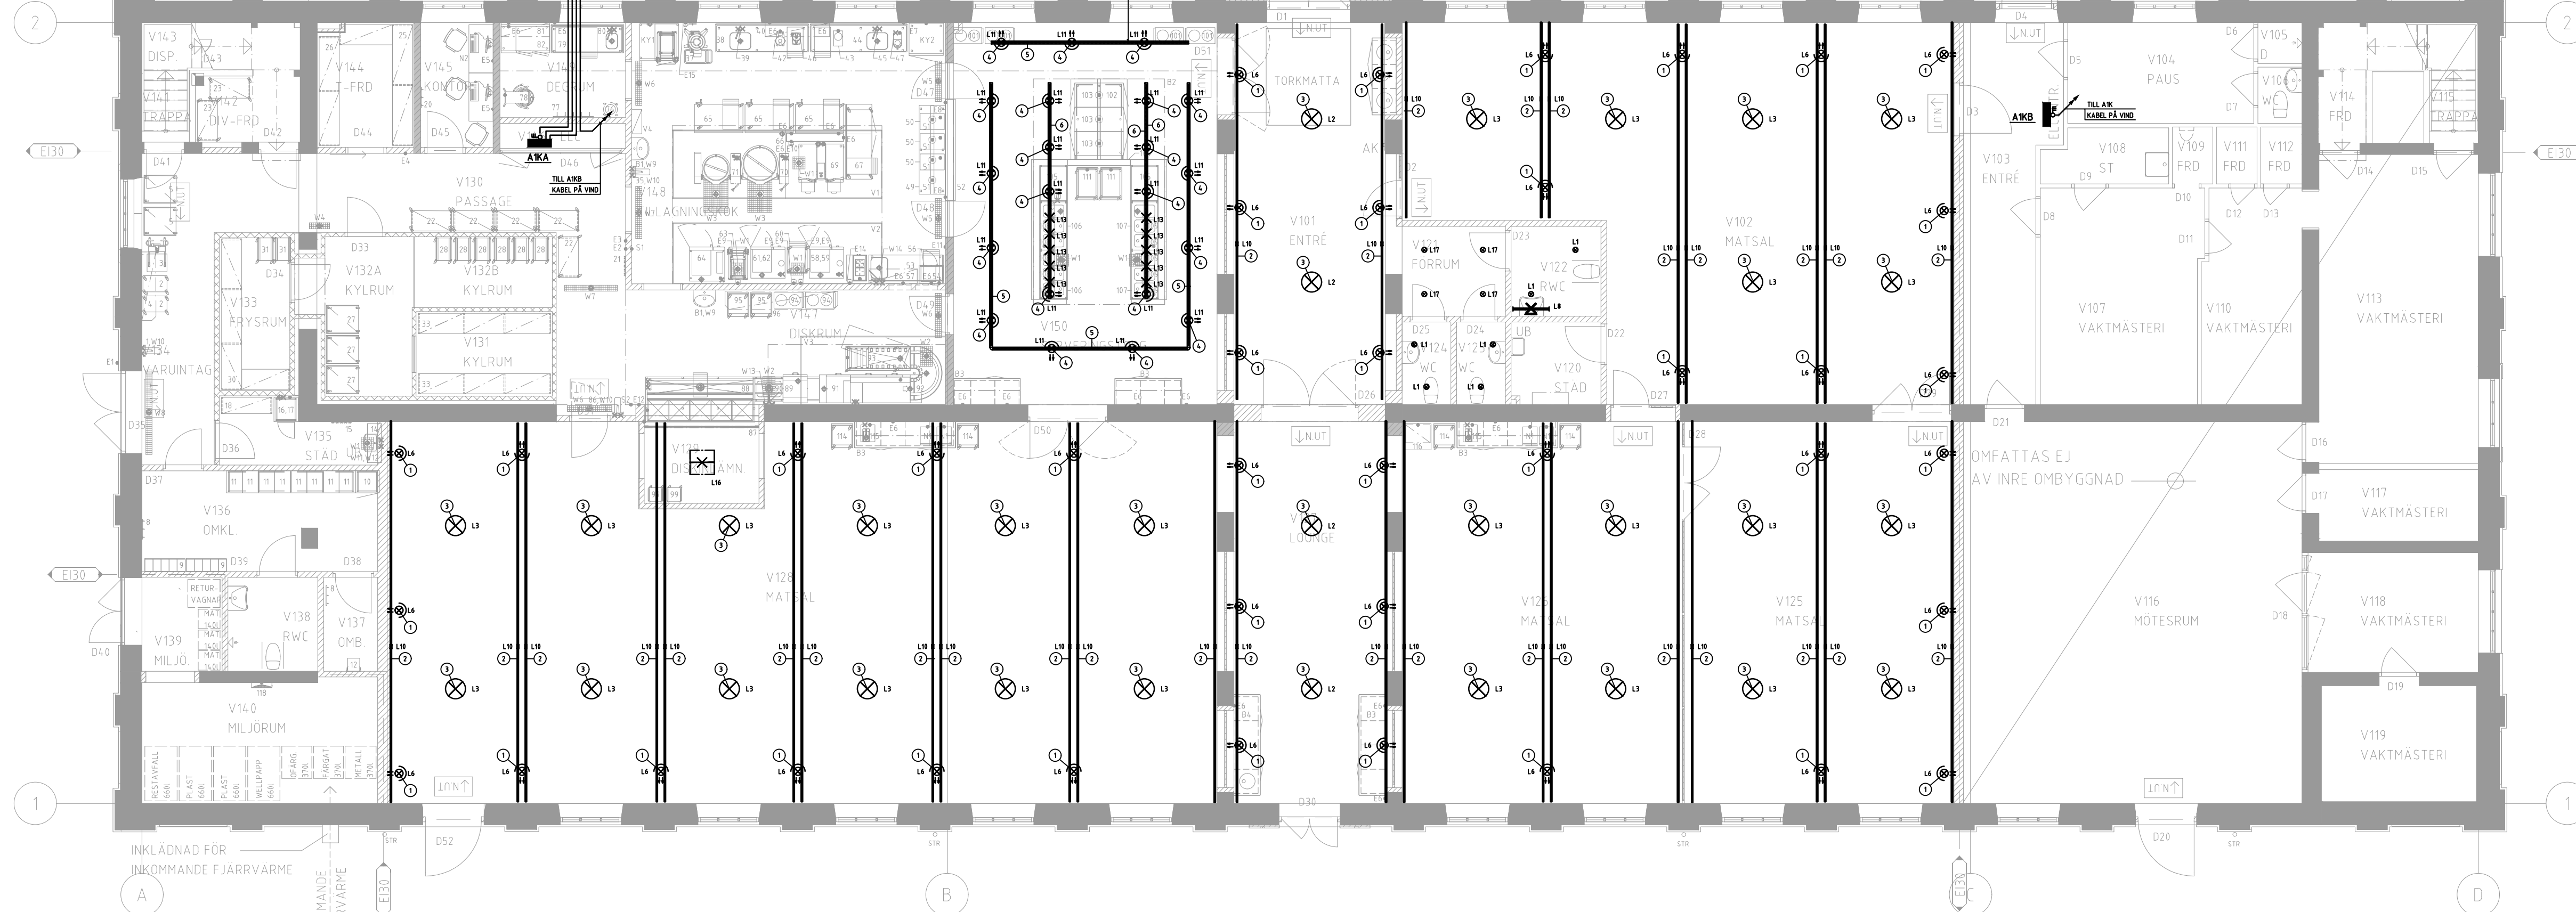

BET	ÄNDRING AVSER	DATUM	SIGN
-----	---------------	-------	------


HELSINGBORG
FASTIGHETSFÖRVALTNINGEN

FASTIGHET	
-----------	--

OBJEKTSNR	BYGGNADS-ID	PROJEKTSNR
1457	5-266088	60095

BYGGNAD	1457-20 - HUS V (BYGGNAD 449)
---------	-------------------------------

ORIENTERINGSFIGUR PLAN 03

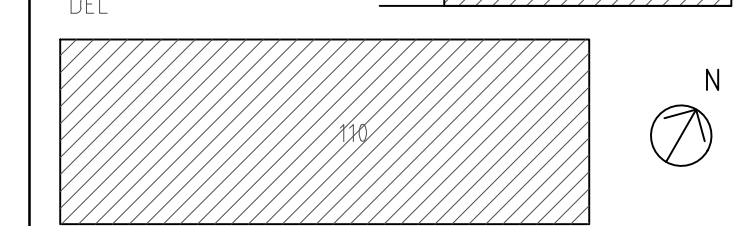

VÄSTRA SANDGATAN

UPPDRAGSNR 23053,001	ANSVARIG NICKLAS HULT		
DATUM 2025-01-27	RITAD/KONSTR AV NH	HANDLAGGARE NH	SYSTEMBETEKNING 00001

SKALA (A1)	NUMBER	REV
1:100	F-631-1-2001110	

ORIGINAL FORMAT: A1

```
list of Xrefs:
P=00R000=..A1[...VP_KompI/VP=00R000=..A1.dwg]
P=00MXCP000[...VP_KompI/VP=00MXCP000.dwg]
P=00MXCP000[...VP_KompI/VP=00MXCP000.dwg]
A=40..P20010[...VA_ModellVA=40..P20010.dwg]
E=631-T_001[...KompI/E=631-T_001.dwg]
E=631..P20010[...Modell/E=631..P20010.dwg]
SK=46..P20010[...SK_Modell/SK=46..P20010.dwg]
```