




E-Bilaga 3 Informationsritningar (äldre)
ÖNNOWSKA SKOLAN
ELSINGBORG
/GGNAD V

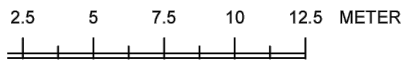

LA 1:250

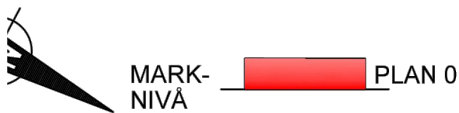

ERVICERITNING

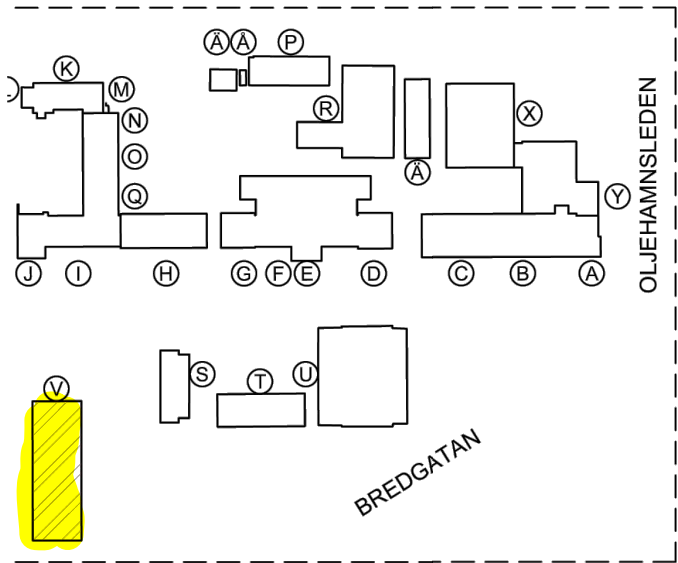


Brandlarmet ligger som stubbe
så är ingen retur på slingan.

VÄSTRA SANDGATAN

PRENAD

04216H1067
A PRENAD AB / FIRE SAFETY RESOURCE FSR AB
2017-01-04 av FSRAB / SS, REV. DATUM: 2021-10-04 av PRENAD AB / MR

2025-01-27

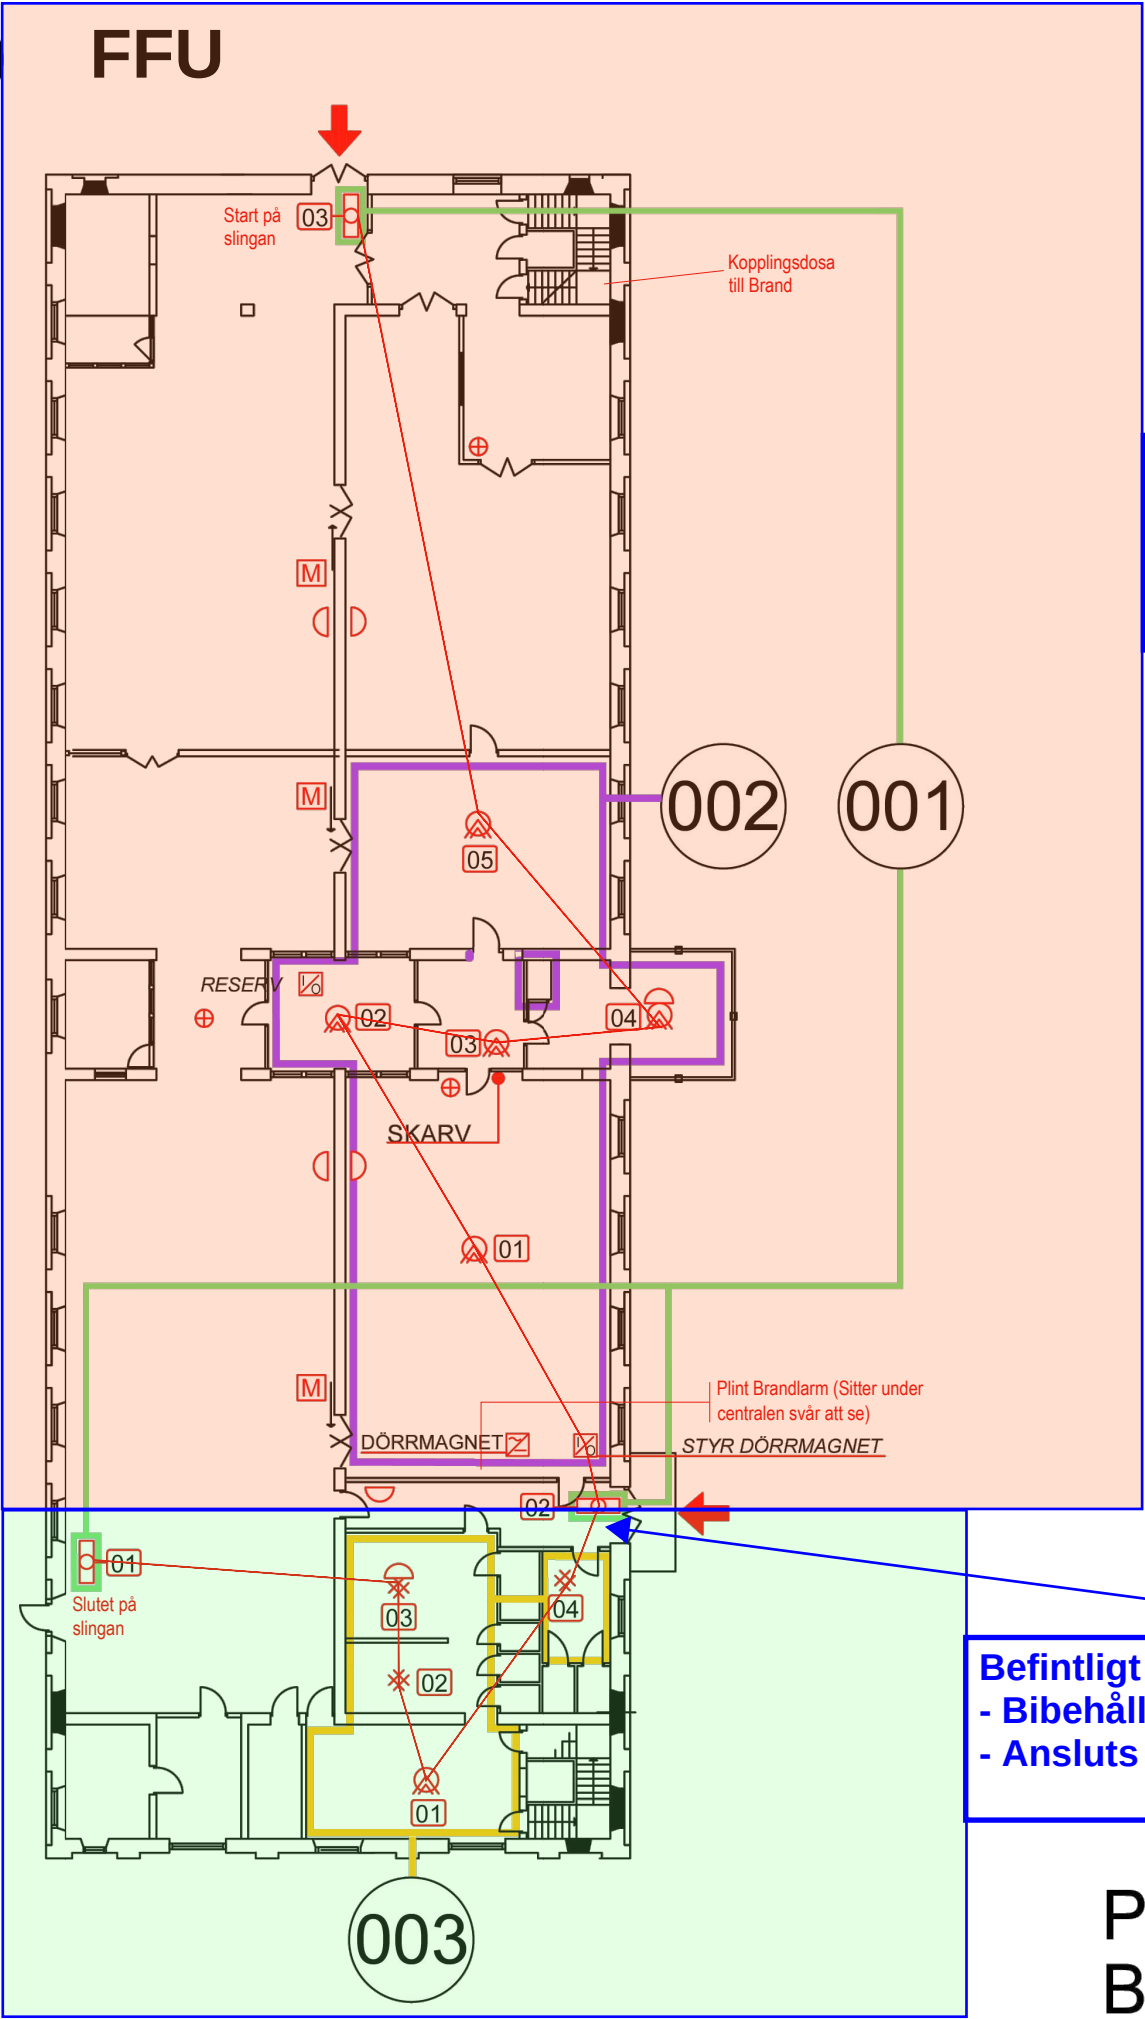

Befintligt brandlarm
inom Område A
- Rivs
- Ersätts med nytt


Befintlig slinga från
Område B ansluts till nya
installationer i Område A

Befintligt brandlarm inom Område B
- Bibehålls
- Ansluts till nytt brandlarm i Område A

PLAN 0
BLAD 1

Äldre informationsritning
OBS endast för information ej gällande underlag.

Se rumsfunktionsprogram och rambeskrivning för
omfattning samt gällande typritningar:
E-631-1-0000700

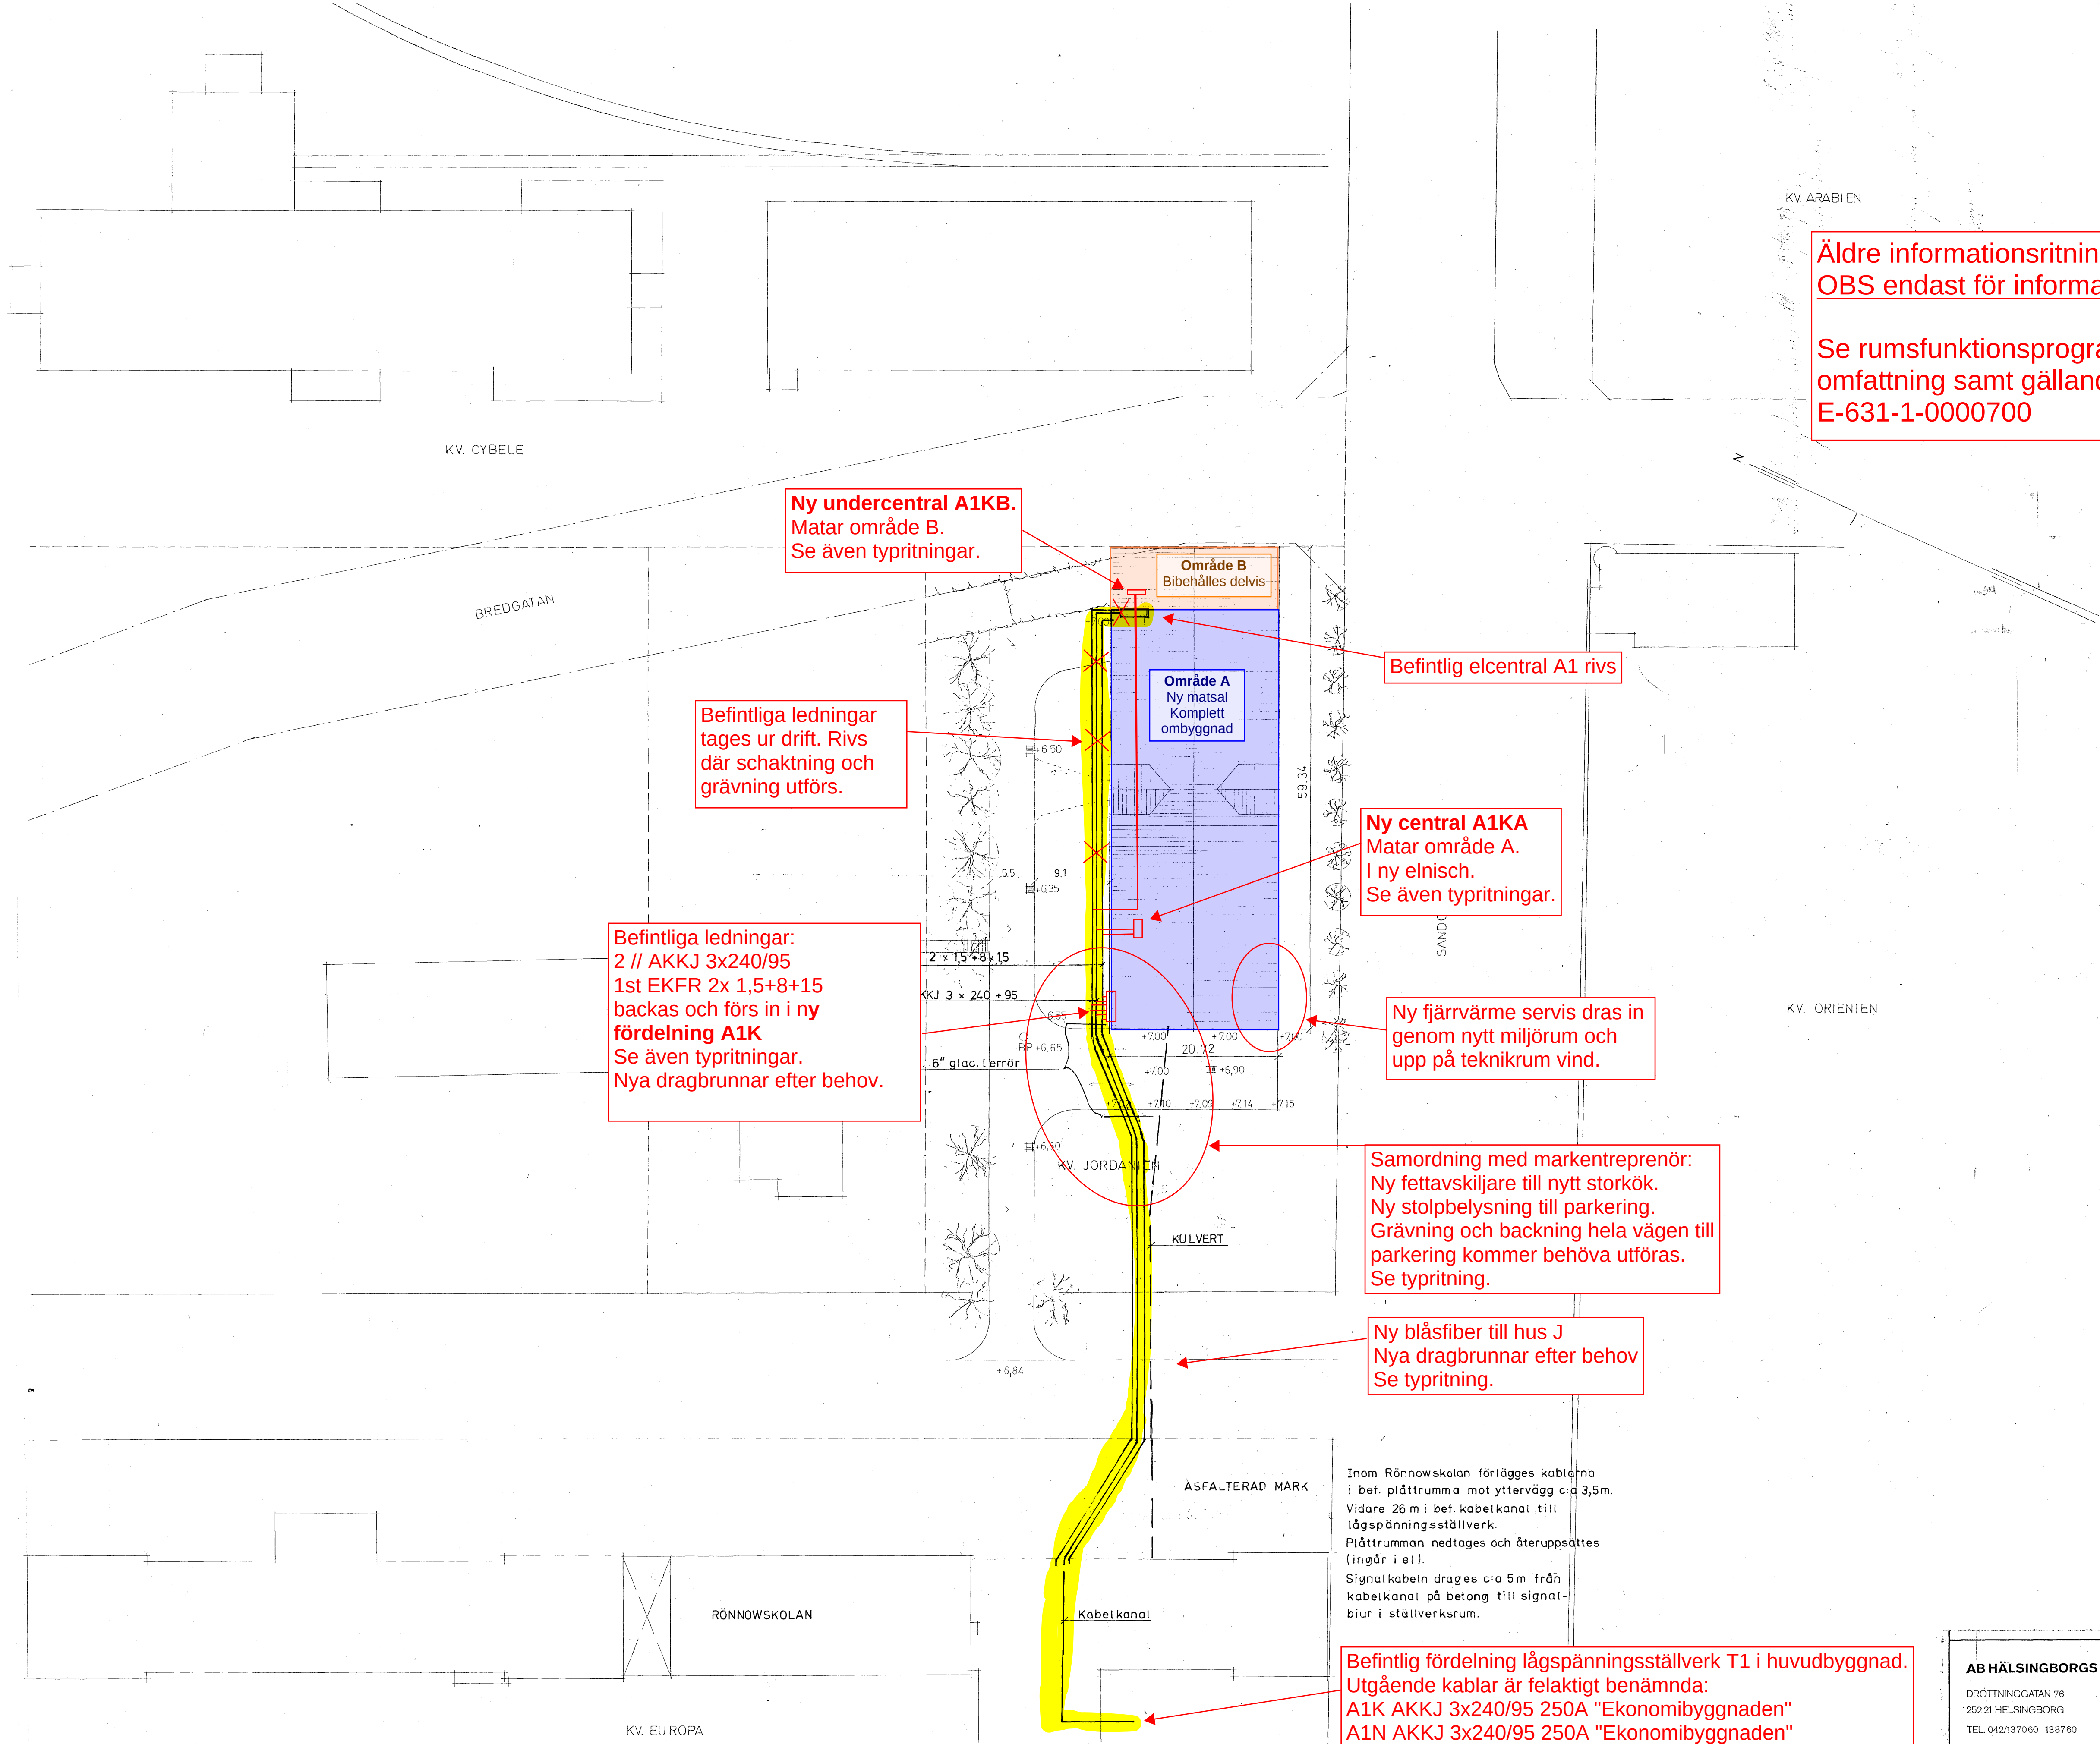

Ny undercentral A1KB.
Matar område B.
Se även typritningar.

Område B
Bibehålles delvis

Befintlig elcentral A1 rivs

Område A
Ny matsal
Komplett
ombyggnad

Befintliga ledningar
tages ur drift. Rivs
där schaktning och
grävning utförs.

Ny central A1KA
Matar område A.
I ny elnisch.
Se även typritningar.

Befintliga ledningar:
2 // AKKJ 3x240/95
1st EKFR 2x 1,5+8+15
backas och förs in i ny
fördelning A1K
Se även typritningar.
Nya dragbrunnar efter behov.

Ny fjärrvärme servis dras in
genom nytt miljörum och
upp på teknikrum vind.

Samordning med markentreprenör:
Ny fettavskiljare till nytt storkök.
Ny stolpbelysning till parkering.
Grävning och backning hela vägen till
parkering kommer behöva utföras.
Se typritning.

Ny blåsfiber till hus J
Nya dragbrunnar efter behov
Se typritning.

Inom Rönnowskolan förlägges kablarna
i bef. plåttrumma mot yttervägg c:a 3,5m.
Vidare 26 m i bef. kabelkanal till
lågspänningsställverk.
Plåttrumman nedtages och återuppsättes
(ingår i el).
Signalkabeln drages c:a 5m från
kabelkanal på betong till signal-
biur i ställverksrum.


Befintlig fördelning lågspänningsställverk T1 i huvudbyggnad.
Utgående kablar är felaktigt benämnda:
A1K AKKJ 3x240/95 250A "Ekonomibyggnaden"
A1N AKKJ 3x240/95 250A "Ekonomibyggnaden"
A1N märks om enligt rambeskrivning.

			REV.	ANT.	REVIDERINGEN AVSER	SIGN.	DATUM
AB HÅLSINGBORGS ELKONSULT			KV. JORDANIEN, HELSINGBORG				
DROTTNINGGATAN 78			OMBYGGNAD AV EKONOMIBYGGNAD				
252 21 HELSINGBORG			SITUATIONSPLAN				
TEL. 042/137060 138760			ELINSTALLATION: HUVUD LEDN., SIGNALLEDN.				
RITAD AV	KONSTR. AV	GRANSKAD AV	SKALA 1:400				
A. R.	LÖWGREN		ARBETSNR.		RITNINGSNR.	REV.	
HELSINGBORG DEN			711		01		
1974. 04. 30							

Äldre informationsritning
OBS endast för information ej gällande underlag.

Se 360 foto inventering: <https://develcon.se/maps/ronnowska-matsal/>

Och gällande typritning
E-631-1-2001110

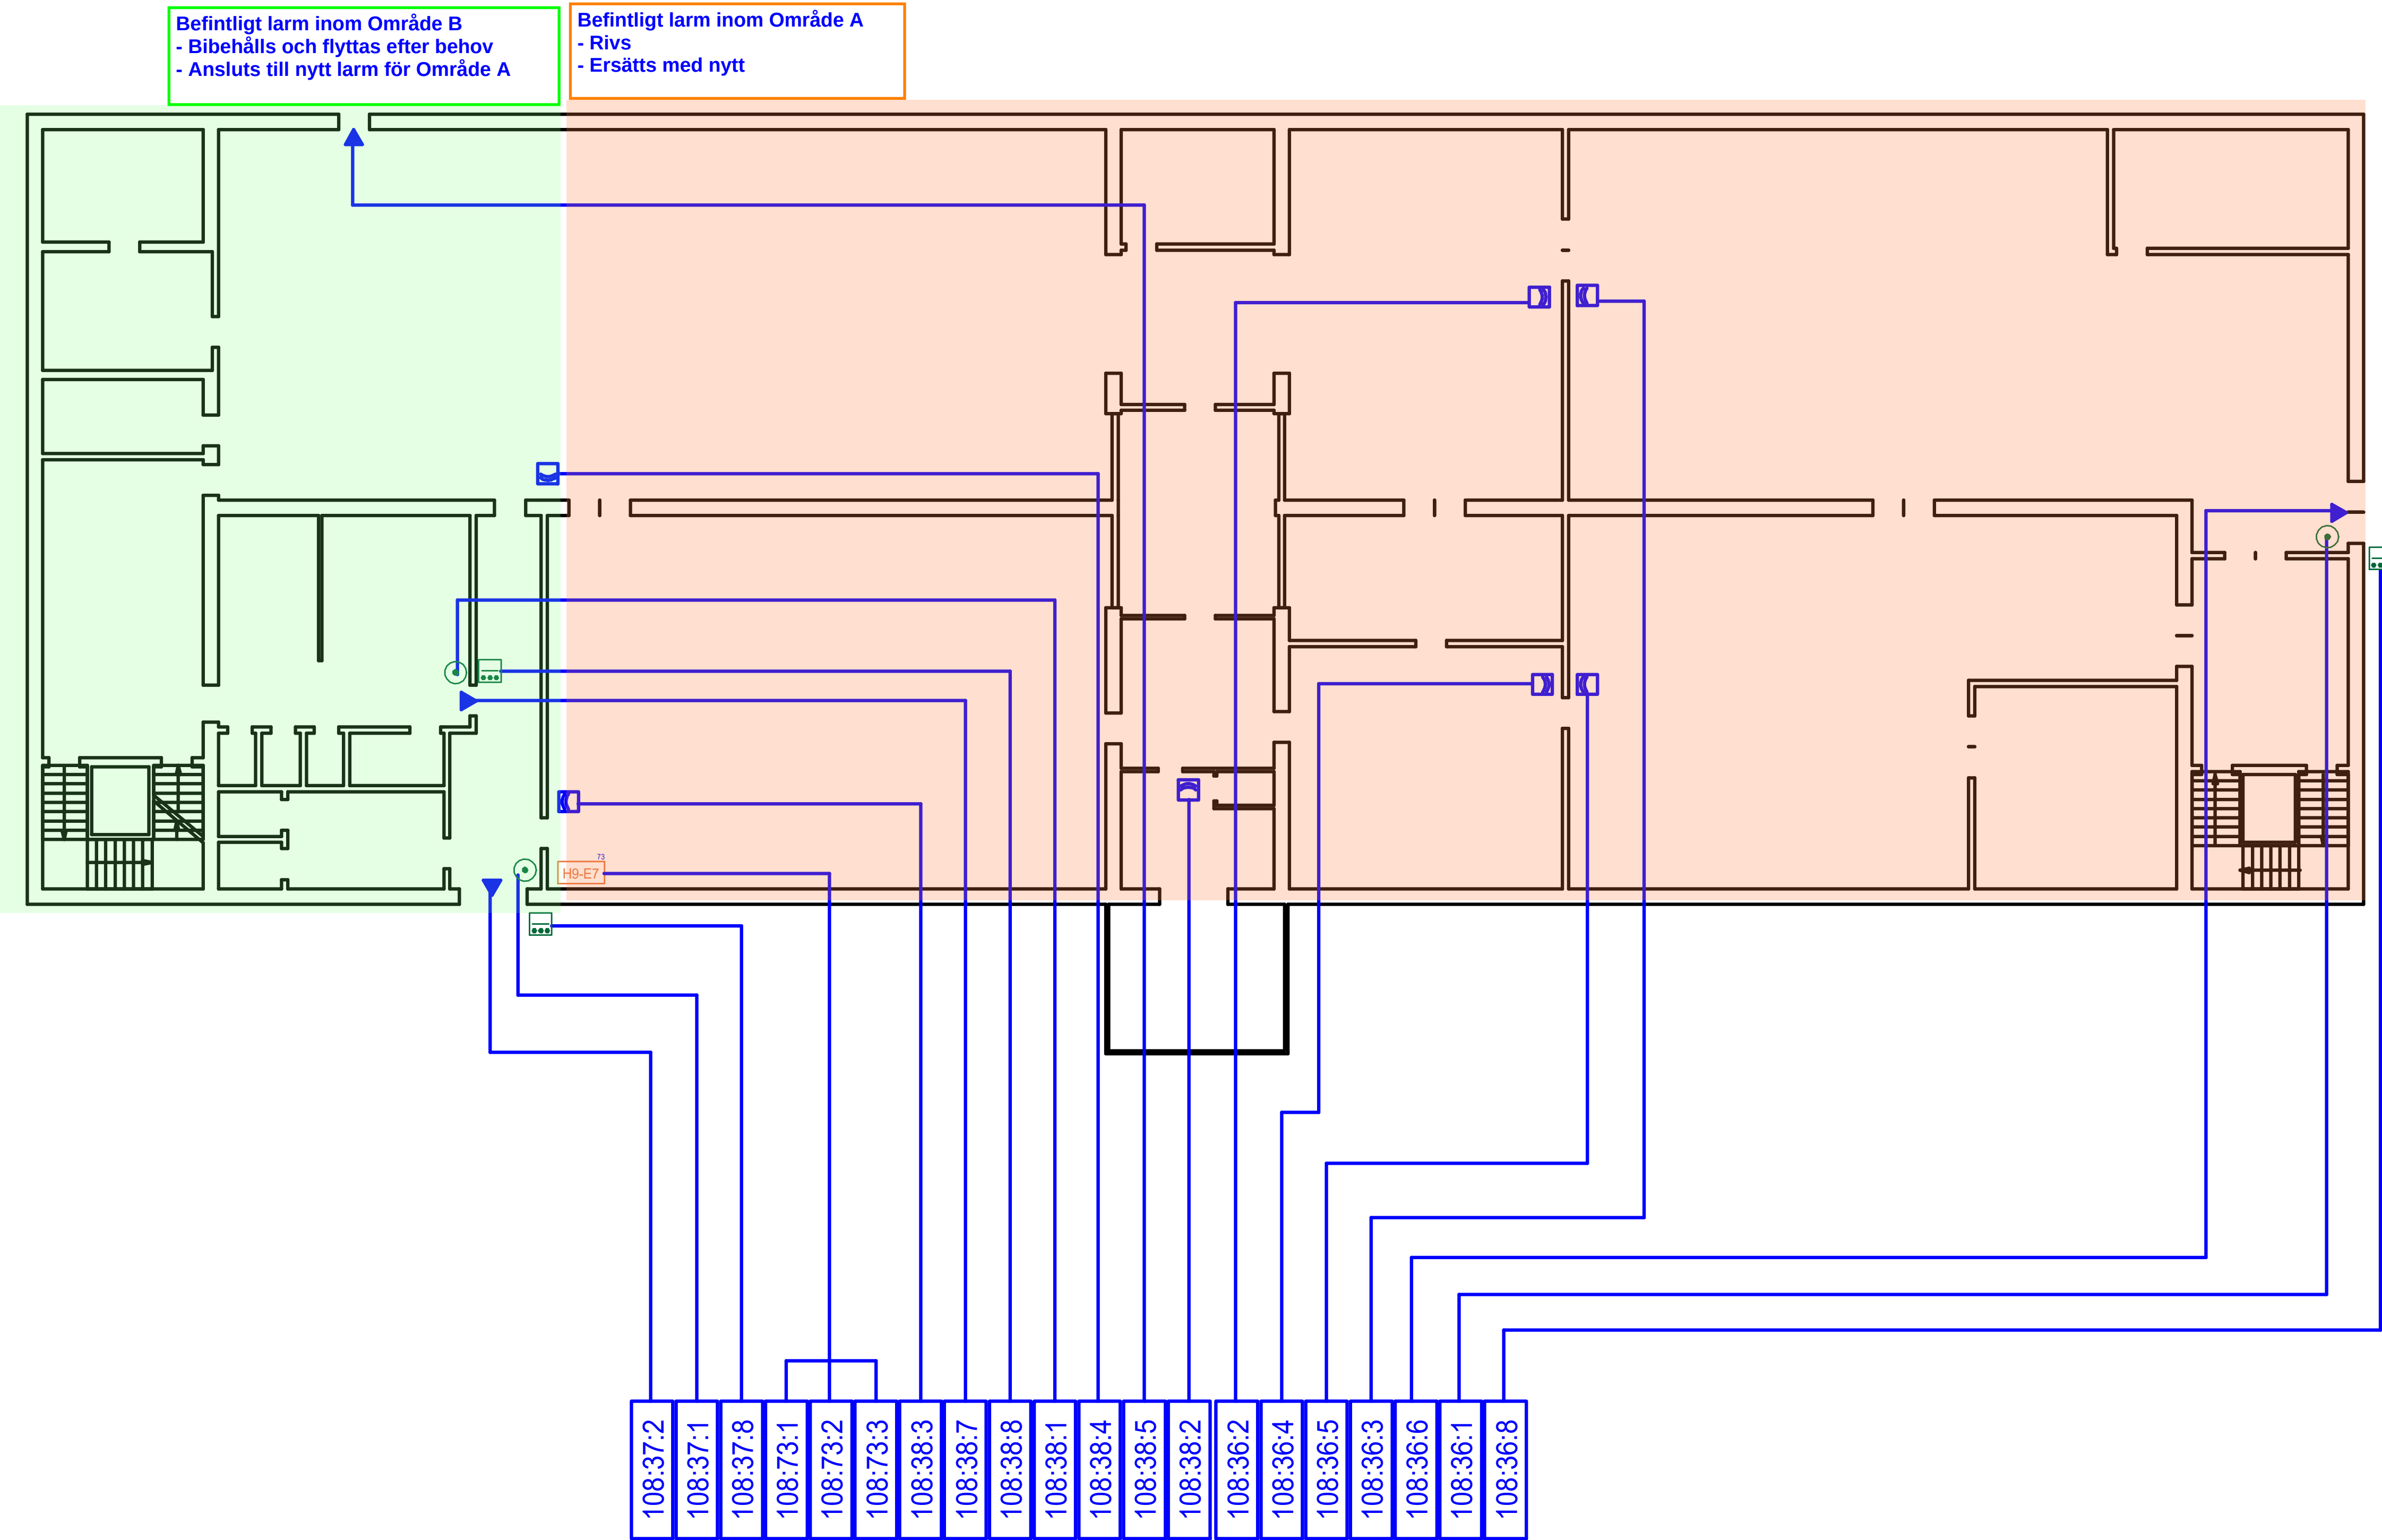

	Magnetkontakt		Värmetektor
	IR-detektor		Värmedetektor, dold
	IR-detektor 360		Rökdetektor
	Glaskrossdetektor		Rökdetektor, dold
	Akustisk Glaskrossdetektor		Bilbrandskåp
	Kolskontakt		Dörrhållarmagnet
	Siren		Rökdetektor, sirensöcket
	Inbrottslarmcentral		Rökdetektor, siren och blick
	Undercentral/ Sektionskort		Värmedetektor, sirensöcket
	Larmsändare		Värmedetektor, siren och blick
	Analysator		Larmdon
	Manöverpanel		Blixtljus
	Nyckelförbikopplare		Adressenhet, brandlarm
	Sektionsnummer		Centralaparat, brandlarm/utrymningsl
	Centralaparat, E1		I/O enhet, brandlarm
	Dörrcentral E200		Nyckelskåp
	Dörrcentral E2V		Larmsändare, brandlarm
	Undercentral, E2VL		Larmlagringstablå
	Manöverpanel, E4		Ändelement
	IP-modul, EDW-100		Kameraserver
	Likriktare, E700		Domekamera
	Repeater, E55		Domekamera, PTZ
	Kortläsare, HD500		Kamera
	Kortläsare, RB500		Kamera, PTZ
	Elektriskt lås		
	Eislutbleck		
	Tryckknapp		
	Karmöverföring, infallid		
	Karmöverföring		
	Salto On-Line		
	Salto Off-Line		
	Överfallslarm, Central		
	Trådlös mottagare		
	Text-display		
	Grafisk-display		
	Larmknapp		
	Trådlös larmknapp		
	Larmknapp med anslutning		

Anläggningstyp:
=H9

Ritningstyp:
ORIENTERINGSRITNING



www.elbolagetsyd.se

Ritad Av: TONO	AnläggningsID:
Datum: 2020-12-23	Larmsändarnr:
Byggnad/Område: Rönnowska - V Plan 1	
Adress: Bredgatan 22, Helsingborg	
Larmmottagare:	Dok.nr: 3106-051

Äldre informationsritning
OBS endast för information ej gällande underlag.

Se 360 foto inventering: <https://develcon.se/maps/ronnowska-matsal/>

Och gällande typritning
E-631-1-2001110

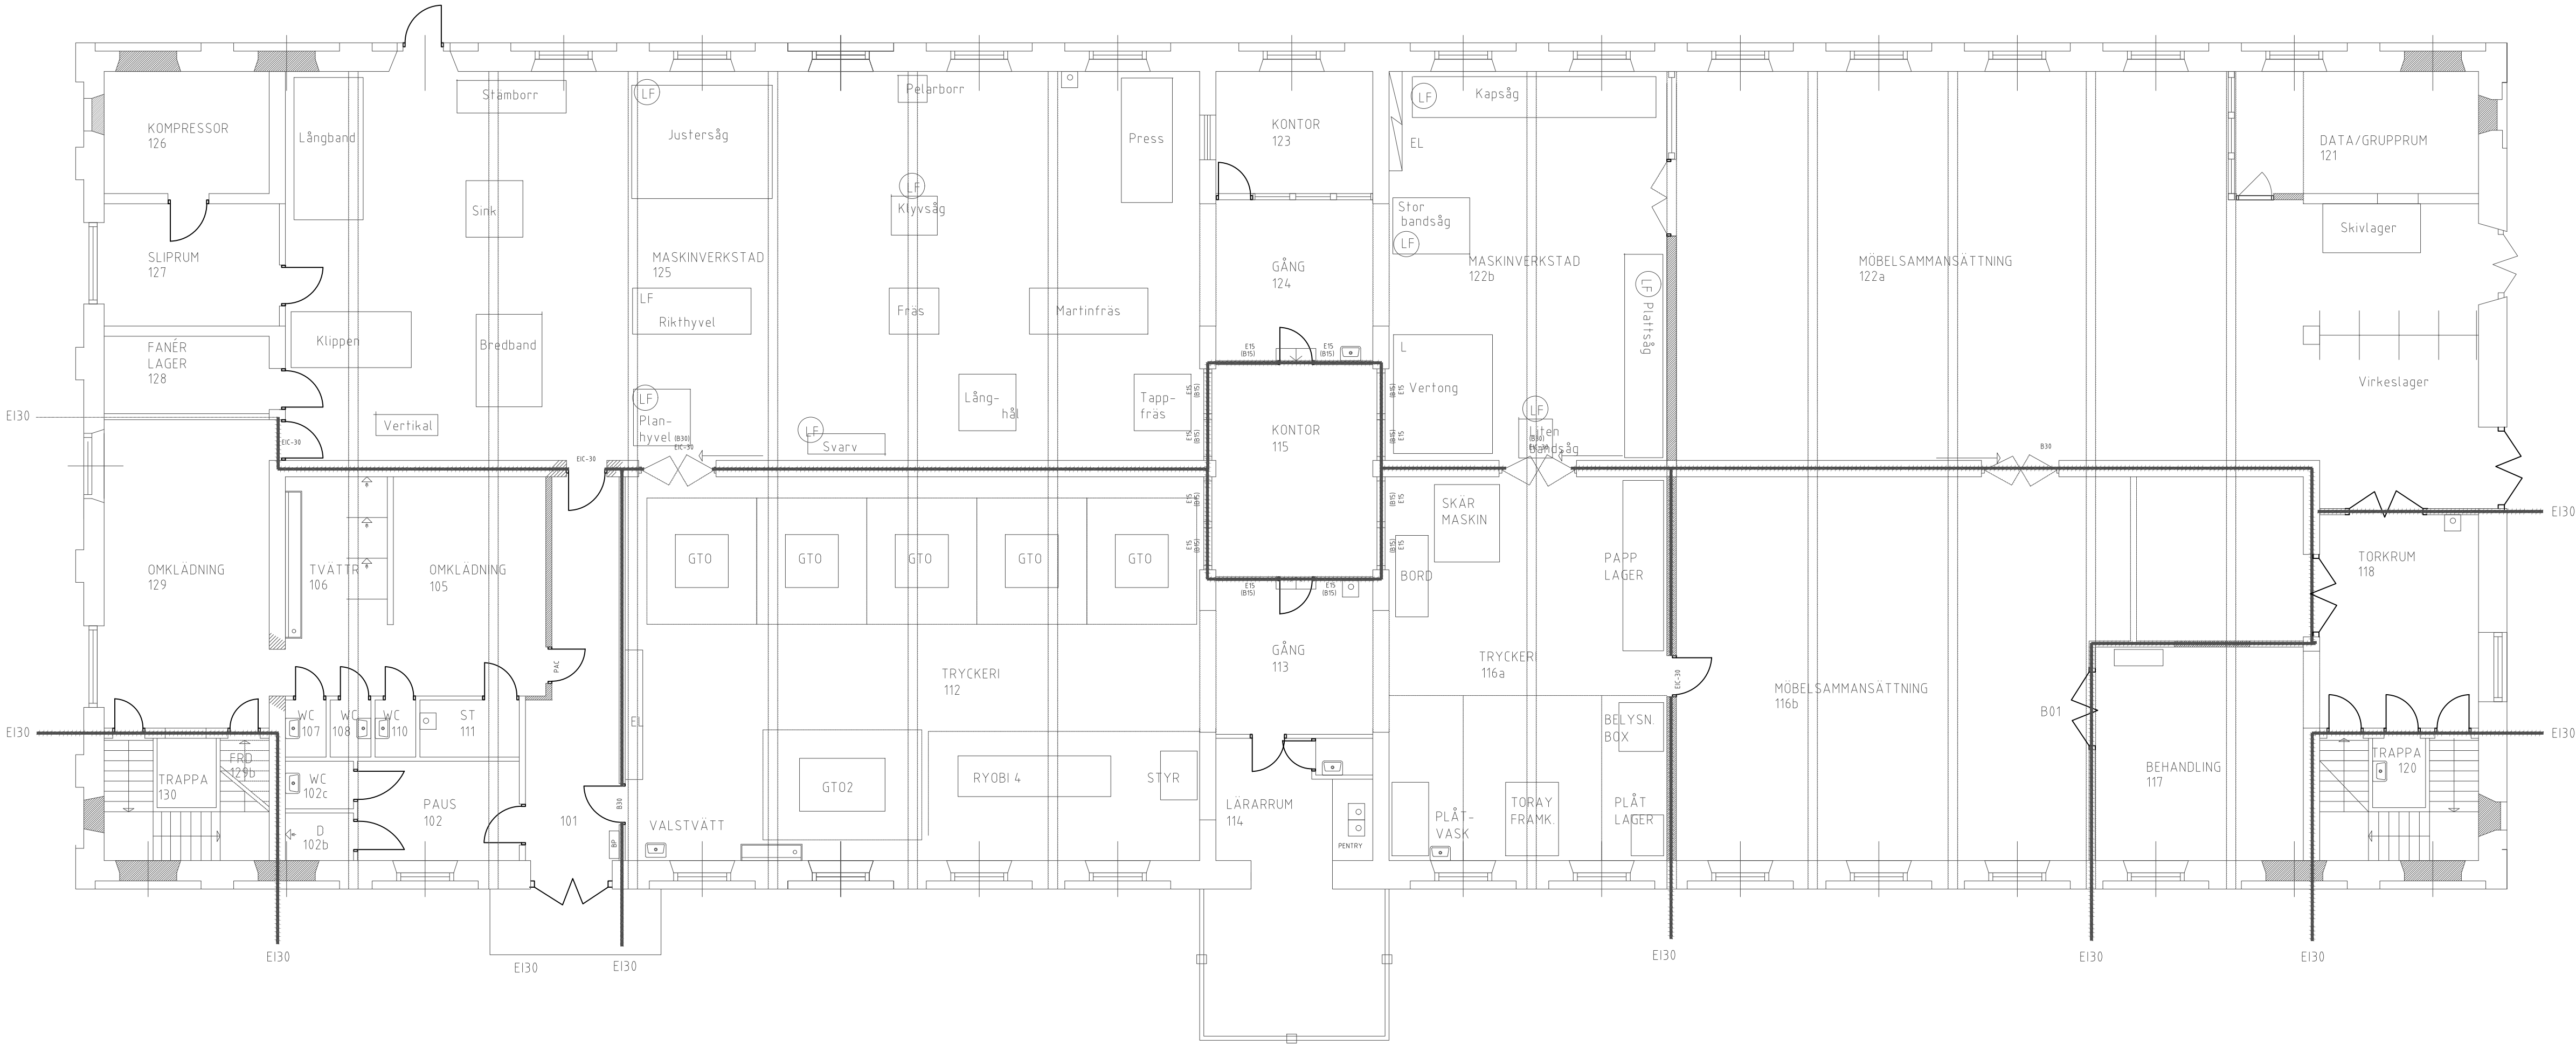

BYGGNAD 449
TRÄTEKNIK / TRYCKERI
BOTTENVÅNING
SKALA 1:150

Äldre informationsritning
OBS endast för information ej gällande underlag.

Se 360 foto inventering: <https://develcon.se/maps/ronnowska-matsal/>

Och gällande typritning
E-631-1-2001110

