


List of Xrefs:

M--01_P00001 [Model\M--01_P00001.dwg]
M--01_P00002 [Model\M--01_P00002.dwg]
R--10_P00002 [Model\R--10_P00002.dwg]
R--10_P00003 [Model\R--10_P00003.dwg]
R--10_P00004 [Model\R--10_P00004.dwg]
P--000000001 [VP\Kontroll\VP--000000001.dwg]
M--10_P00002 [Model\M--10_P00002.dwg]

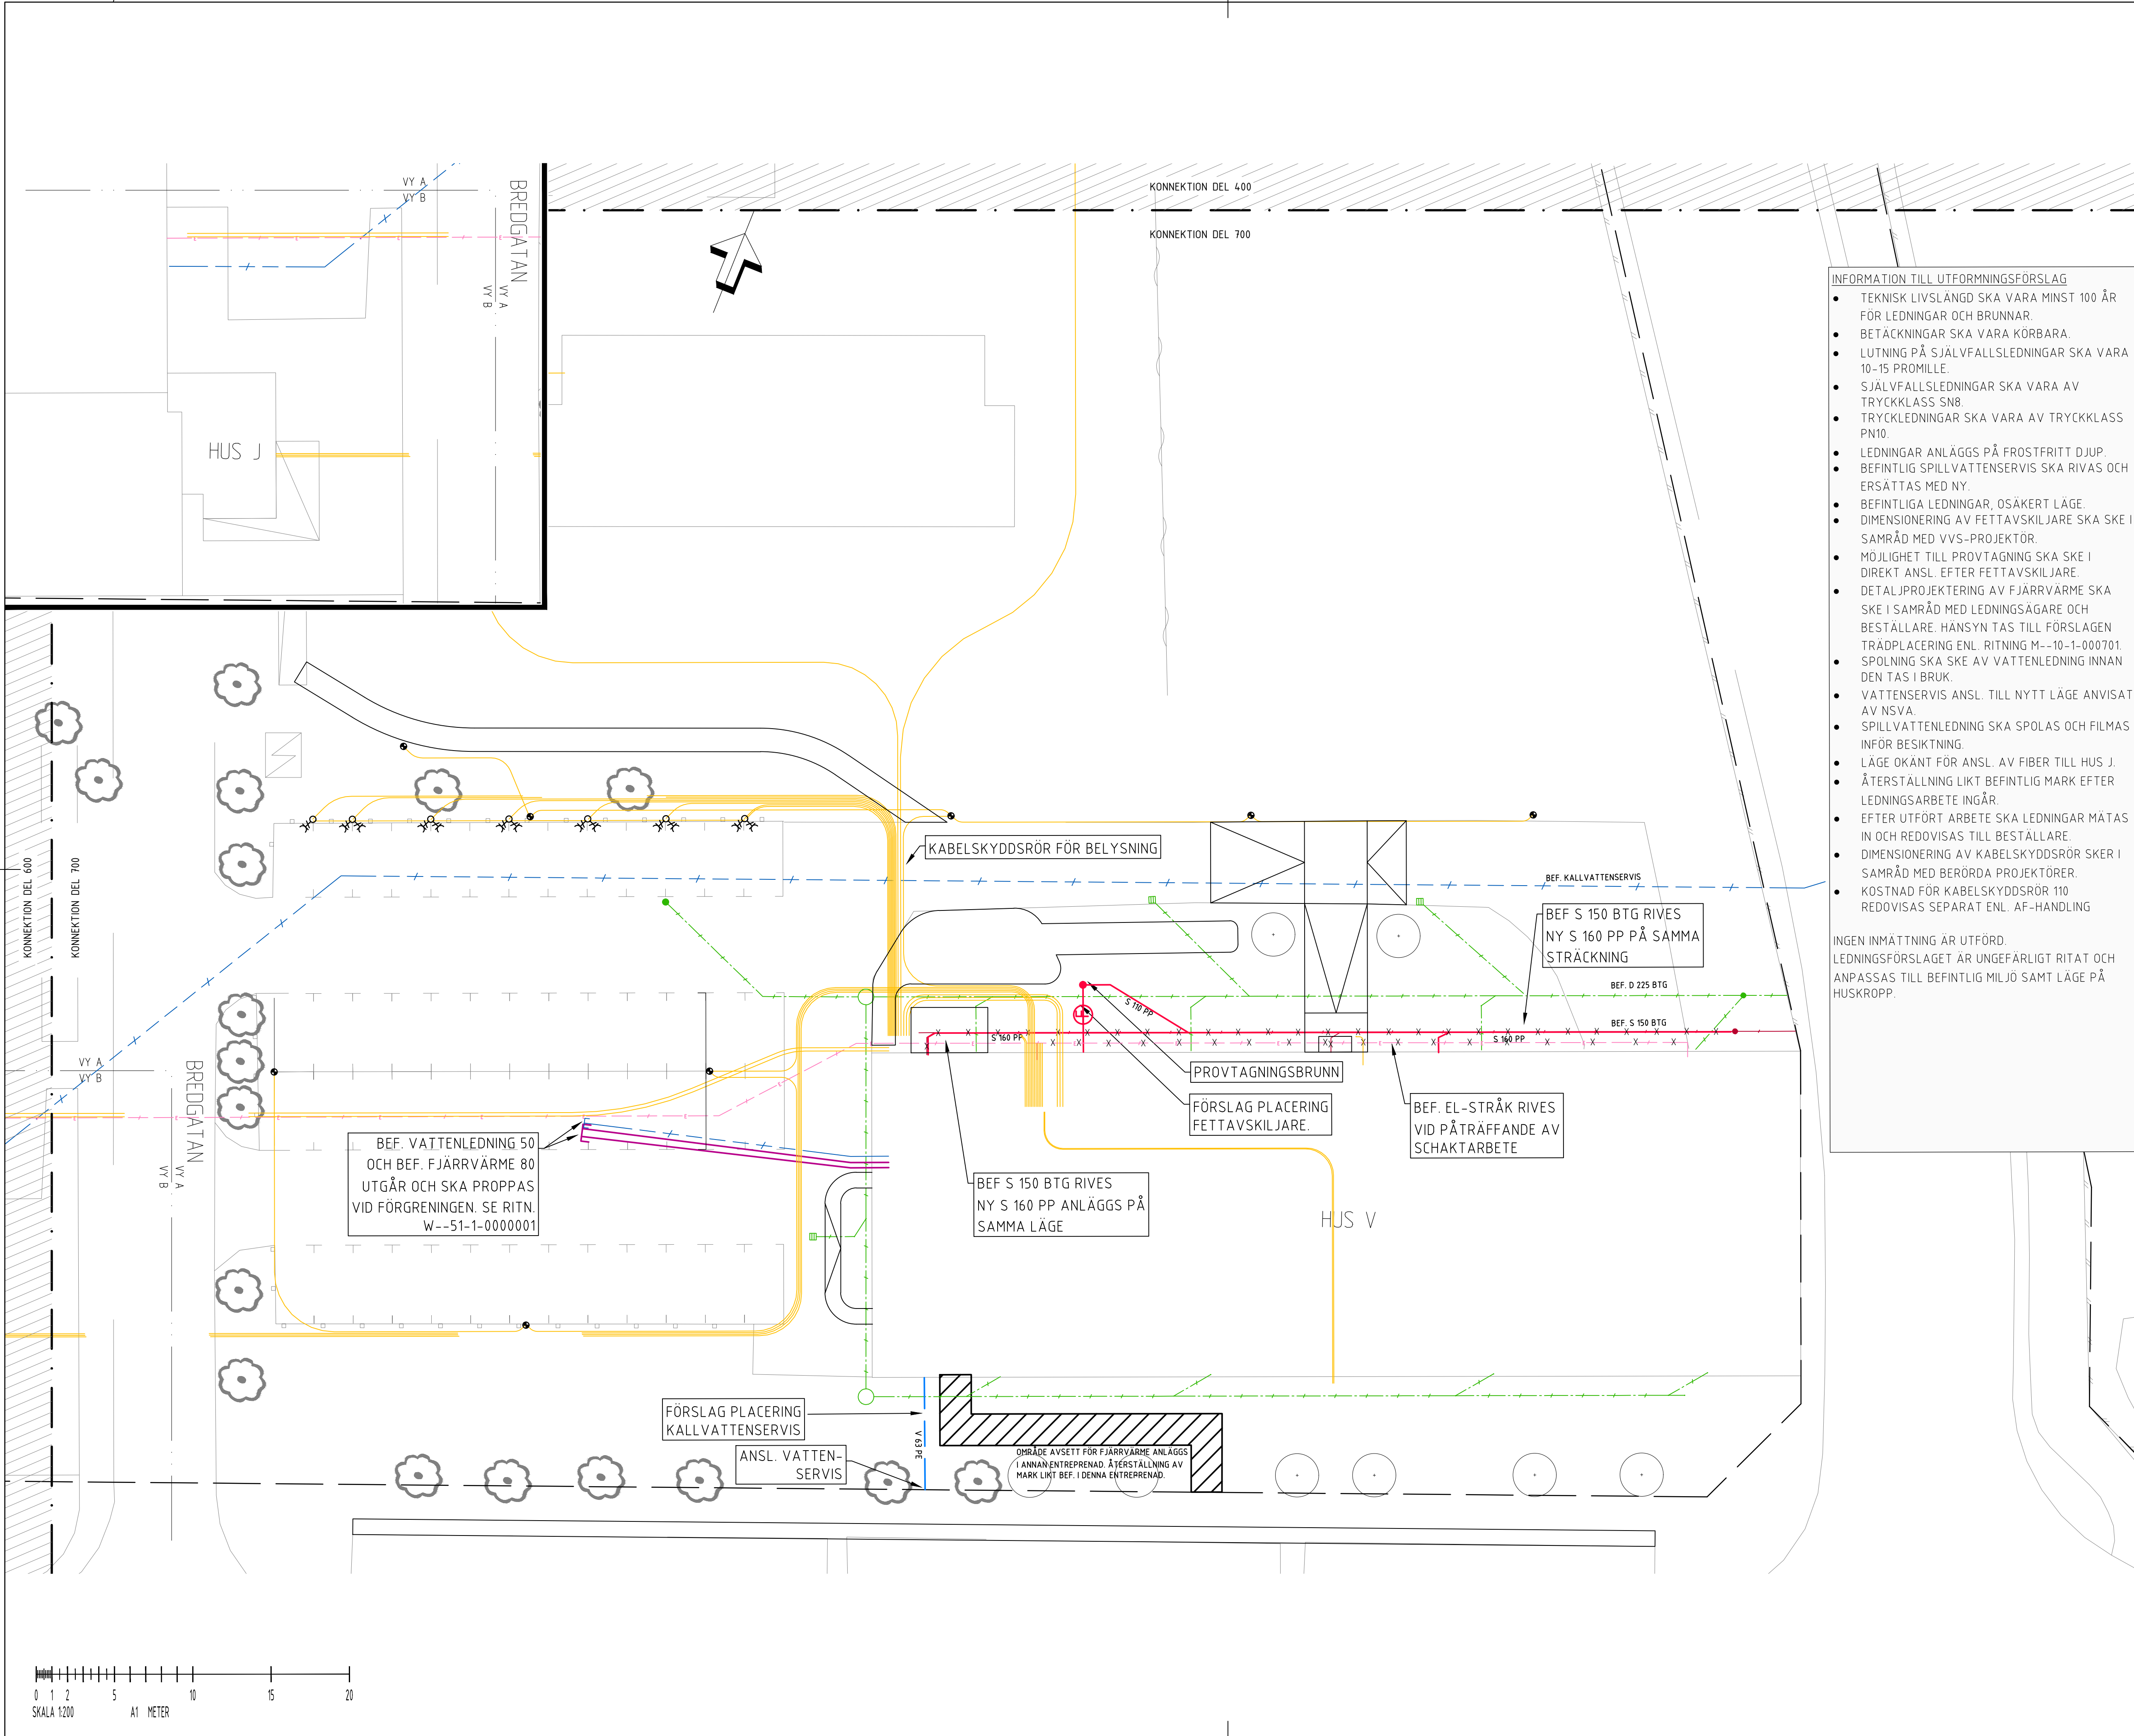

FÖRKLARINGAR


—	FASTIGHETSGRÄNS
—	VATTENLEDNING
—	SPILLVATTENLEDNING
—	BEF VATTENLEDNING
—	BEF DAGVATTENLEDNING
—	BEF SPILLVATTENLEDNING
—	BEF EL-STRÅK
—	BEF FJÄRRVÄRME
—	KABELSKYDDSRÖR ENLIGT E-HANDLINGAR
●	BELYSNINGSSTÖLPAR ENLIGT E-HANDLINGAR
○	NEDSTIGNINGSBRUNN
●	TILLSYNSBRUNN
■	DAGVATTENBRUNN Ø400 MED GALLERBETÄCKNING, SANDFÄNG OCH VATTENLÅS
●	PROVTAGNINGSBRUNN
⊕	FETTAVSKILJARE

INFORMATION TILL UTFORMNINGSFÖRSLAG

- TEKNISK LIVSLÄNGD SKA VARA MINST 100 ÅR FÖR LEDNINGAR OCH BRUNNAR.
- BETÄCKNINGAR SKA VARA KÖRBARA.
- LUTNING PÅ SJÄLVFALLSLEDNINGAR SKA VARA 10-15 PROMILLE.
- SJÄLVFALLSLEDNINGAR SKA VARA AV TRYCKKLASS SN8.
- TRYCKLEDNINGAR SKA VARA AV TRYCKKLASS PN10.
- LEDNINGAR ANLÄGGS PÅ FROSTFRITT DJUP.
- BEFINTLIG SPILLVATTENSERVIS SKA RIVAS OCH ERSÄTTAS MED NY.
- BEFINTLIGA LEDNINGAR, OSÄKERT LÄGE.
- DIMENSIONERING AV FETTAVSKILJARE SKA SKE I SAMRÅD MED VVS-PROJEKTÖR.
- MÖJLIGHET TILL PROVTAGNING SKA SKE I DIREKT ANSL. EFTER FETTAVSKILJARE.
- DETALJPROJEKTERING AV FJÄRRVÄRME SKA SKE I SAMRÅD MED LEDNINGSÄGARE OCH BESTÄLLARE. HÄNSYN TAS TILL FÖRSLAGEN TRÄDPLACERING ENL. RITNING M--10-1-000701.
- SPOLNING SKA SKE AV VATTENLEDNING INNAN DEN TAS I BRUK.
- VATTENSERVIS ANSL. TILL NYTT LÄGE ANVISAT AV NSVA.
- SPILLVATTENLEDNING SKA SPOLAS OCH FILMAS INFÖR BESIKTNING.
- LÄGE OKÄNT FÖR ANSL. AV FIBER TILL HUS J.
- ÅTERSTÄLLNING LIKT BEFINTLIG MARK EFTER LEDNINGSARBETE INGÅR.
- EFTER UTFÖRT ARBETE SKA LEDNINGAR MÄTAS IN OCH REDOVISAS TILL BESTÄLLARE.
- DIMENSIONERING AV KABELSKYDDSRÖR SKER I SAMRÅD MED BERÖRDA PROJEKTÖRER.
- KOSTNAD FÖR KABELSKYDDSRÖR 110 REDOVISAS SEPARAT ENL. AF-HANDLING

INGEN INMÄTTNING ÄR UTFÖRD.
LEDNINGSFÖRSLAGET ÄR UNGEFÄRLIGT RITAT OCH ANPASSAS TILL BEFINTLIG MILJÖ SAMT LÄGE PÅ HUSKROPP.

KOORDINATSYSTEM SWEREF 99 13 30		HÖJDSYSTEM RH 2000	
------------------------------------	--	-----------------------	--

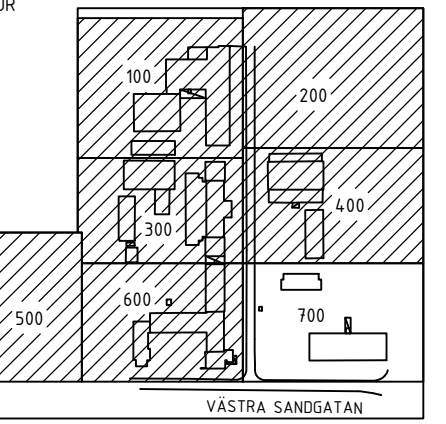BET	ÄNDRING AVSER	DATUM	SIGN
FÖRFRÅGNINGSUNDERLAG			
 HELSINGBORG FASTIGHETSFÖRVALTNINGEN			
FASTIGHET ORIENTEN 6			
RÖNNOWSKA SKOLAN, NYTT KÖK OCH MATSAL			
OBJEKTSNR 1457	BYGGNADS-ID -	PROJEKTNR 60095	
BYGGNAD 1457-0 - Gemensam			
ORIENTERINGSFIGUR			
			
A	ARKITEKTLAGET SKÅNE AB	T: 042-19 96 00	
BR	FIRETECH ENGINEERING EMRON AB	T: 010-150 14 00	
E	DEVELCON AB	T: 079-020 27 02	
K	ÅKERMAN'S INGENJÖRSBYRÅ AB	T: 042-12 00 10	
M	TYRÉN'S AB	T: 010-452 20 00	
S	SWECO SVERIGE AB	T: 08-695 60 00	
SK	STÖRKÖKSVISION	T: 040-744 29	
V	SWECO SVERIGE AB	T: 08-695 60 00	
W	SWECO SVERIGE AB	T: 08-695 60 00	
UPPDRAGSNR 338161		ANSVARIG EMMIE RYNEGARDH	
DATUM 2025-01-27	RITAD/KONSTR. AV EZ	HANDLÄGGARE EZ	SYSTEMBETECKNING -
GEMENSAM MARKOMRÅDE, DEL 700 VA-PÅN MED BEF LEDNINGAR & PLANERADE LEDNINGAR			
SKALA (A1) 1:200	NUMMER R--10-1-0000700	REV	

ORIGINALFORMAT: A1