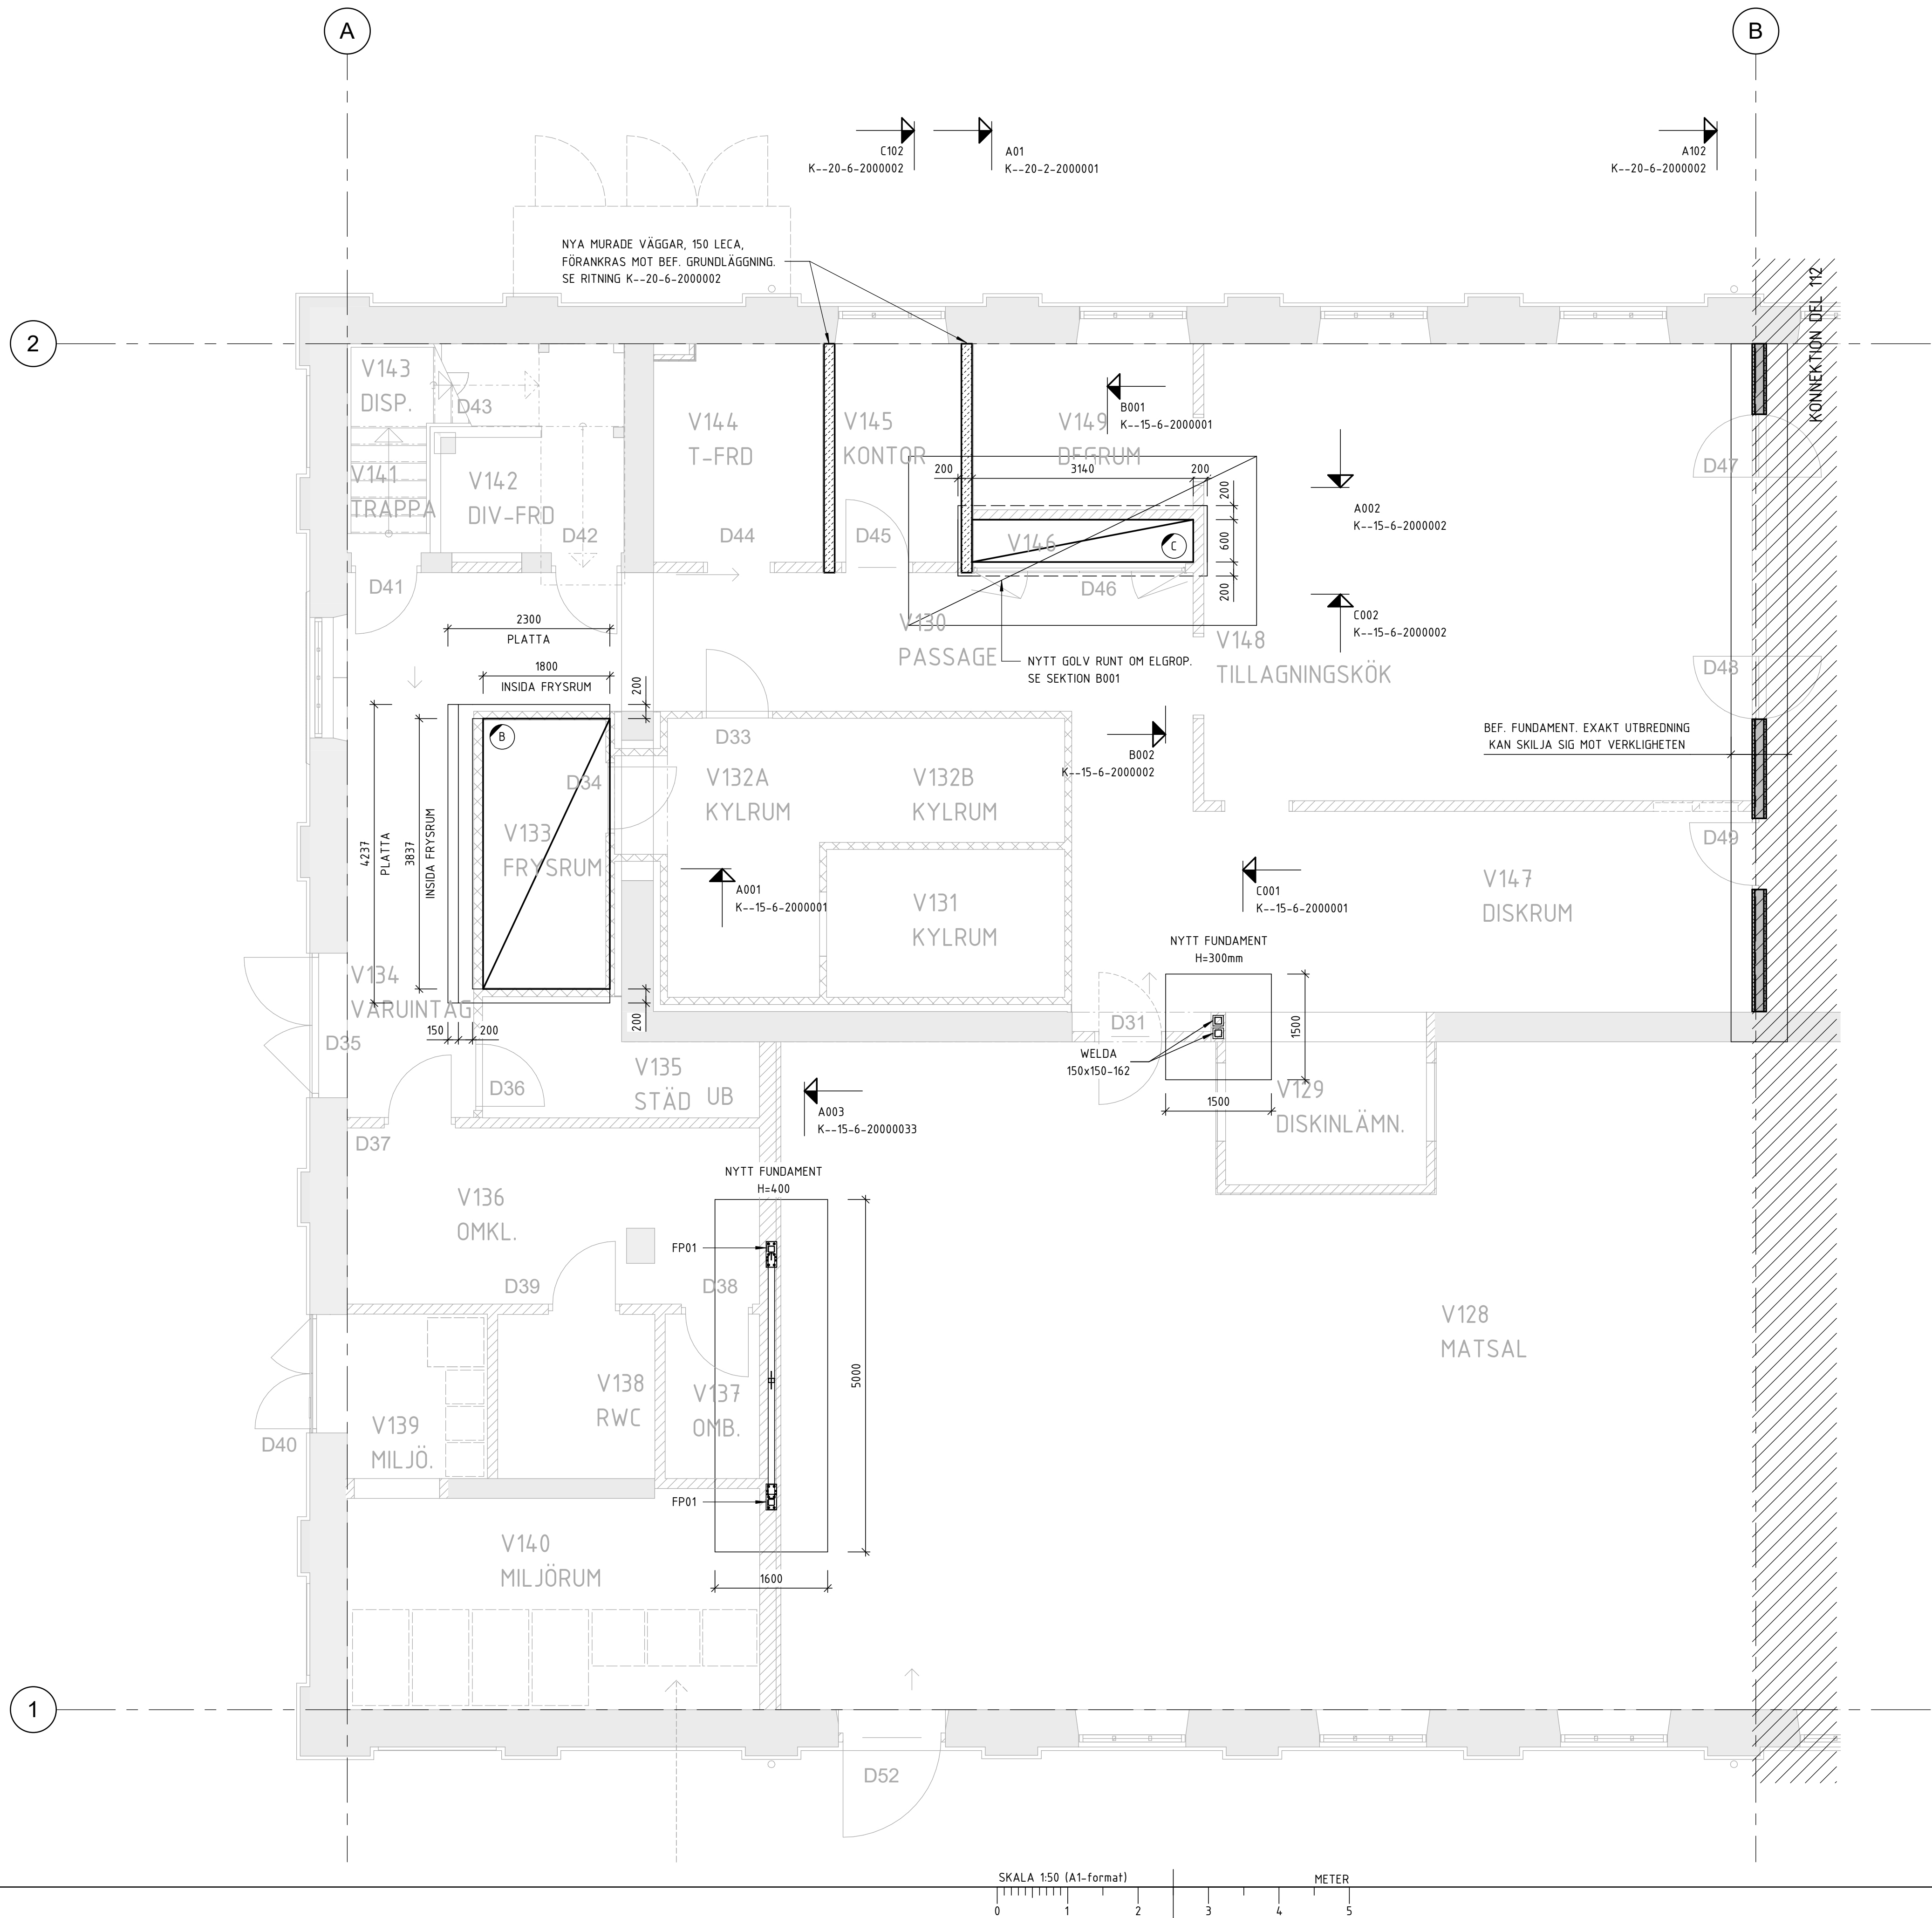


2025-01-24 08:51:32 F:\PROJEKT\2022\22000546 Rönnevaska skolan hus V. Helsingborg\KUP\1001337 Ombyggnad till matsal storkök\Modell\Revit\2023P\1001337_FFU.rvt



FÖRKLARINGAR

- A URSPARING FÖR TÖRKMATTA ARBETAS IN I FLYTSPACKEL. STORLEK ENL. A.
- B URSPARING FRYSRUM
- C URSPARING ELGROP

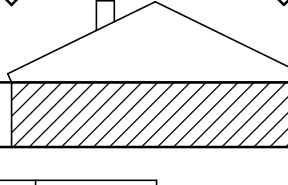
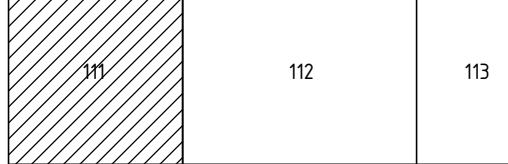
ÖVRIGT SE K--01-5-2000001

FÖRESKRIFTER

SE K--01-5-2000001

HÄNVISNINGAR

ALLMÄNNA ANVISNINGAR K--01-5-2000001

ÄNDRING AVSER		DATUM	SIGN
FÖRFRÅGNINGSUNDERLAG			
 HELSINGBORG FASTIGHETSFÖRVALTNINGEN			
FASTIGHET			
ORIENTEN 6			
RÖNNOWSKA SKOLAN, NYTT KÖK OCH MATSAL			
OBJEKTSNR	BYGGNADS-ID	PROJEKTNR	
1457	5-266088	60095	
BYGGNAD			
1457-20 - HUS V (BYGGNAD 449)			
ORIENTERINGSFIGUR			
PLAN 03 			
DEL			
 			
VÄSTRA SANDGATAN			
A	ARKITEKTLAGET SKÅNE AB		T: 042-19 96 00
BR	FIRETECH ENGINEERING EMRON AB		T: 042-400 02 20
E	DEVELCON AB		T: 079-020 27 02
K	ÅKERMANS INGENJÖRSBYRÅ AB		T: 042-12 00 10
M	TYRÉNS SVERIGE AB		T: 010-452 20 00
S	SWECO SVERIGE AB		T: 08-695 60 00
SK	STÖRKÖKSVISION AB		T: 040-744 29
V	SWECO SVERIGE AB		T: 08-695 60 00
W	SWECO SVERIGE AB		T: 08-695 60 00
C	ZYNKA BIM AB		T: 0734-45 98 99
UPPDRAGSNR	ANSVARIG		
P1001337	HUGO JACOBSSON		
DATUM	RITAD/KONSTR AV	HANDLÄGGARE	SYSTEMBETECKNING
2025-01-27	HJ	HJ	15-1
HUS 20			
GRUNDPLAN DEL 111			
SKALA	NUMMER	REV	
1 : 50	K--15-1-2001111		

ORIGINALFORMAT: A1