




F:\PROJEKT\2022\20200546 Rönnowska skolan hus V - Helsingborg\KUP\1001337 Ombyggnad till matsal storkök\Modell\Revit\2023P\1001337_FFU.rvt 2025-01-24 08:51:40

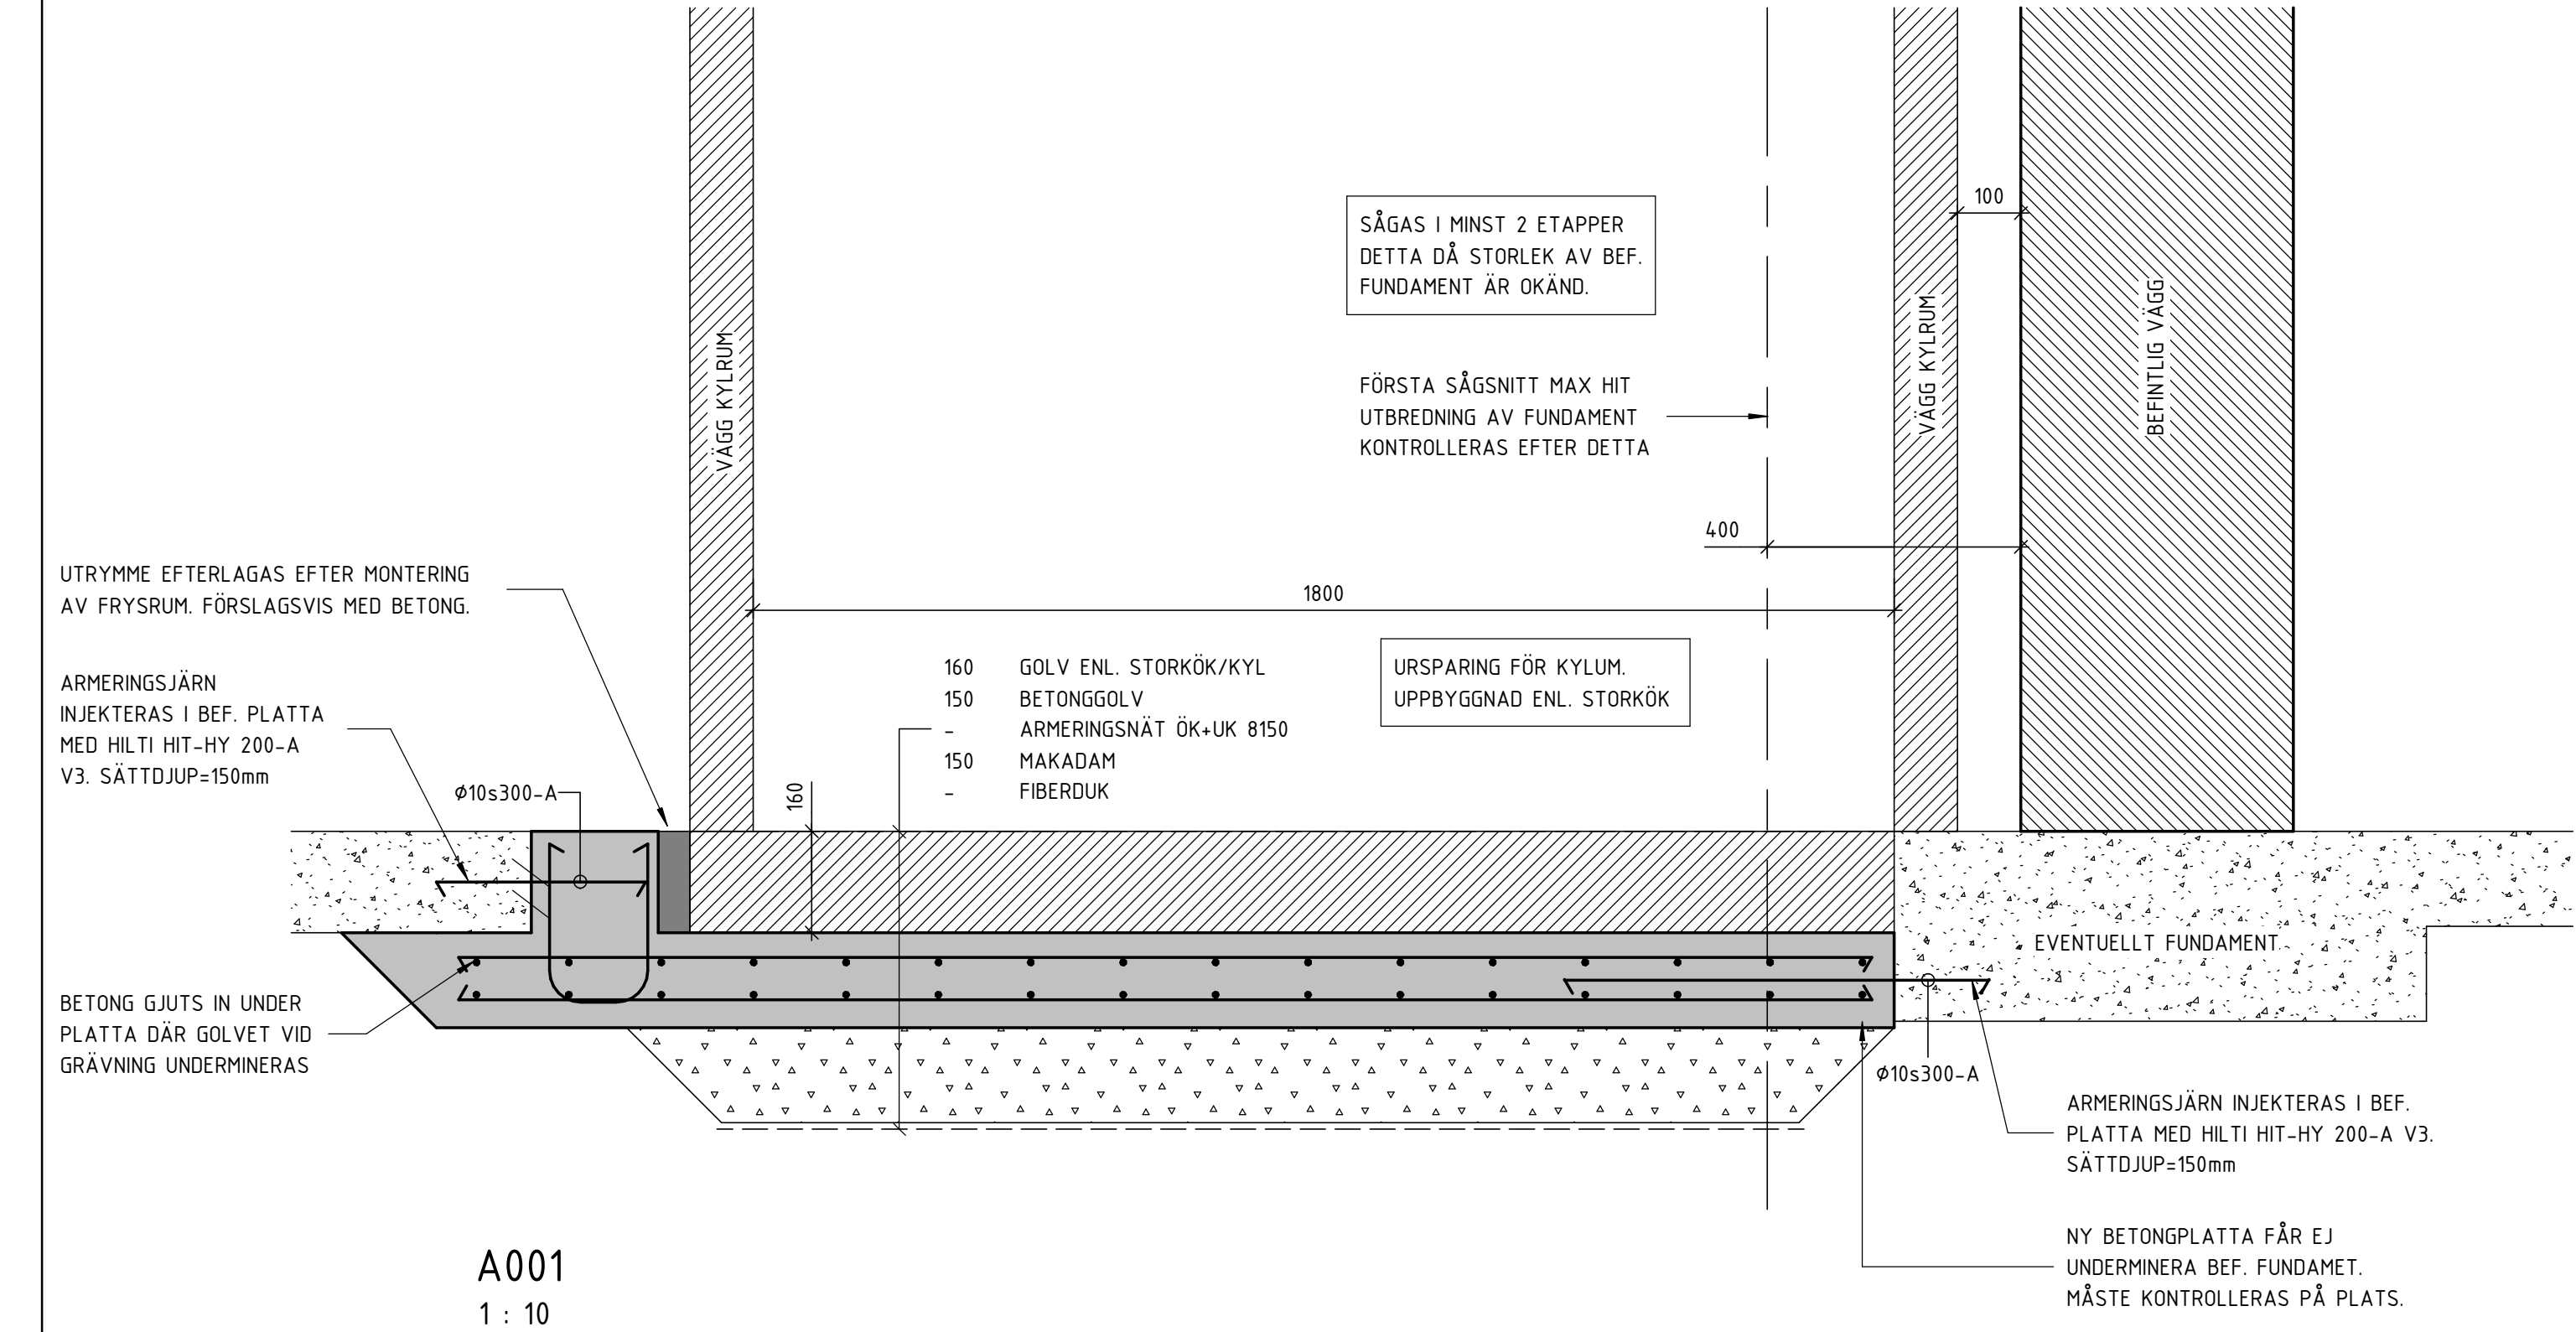


A001
1 : 10

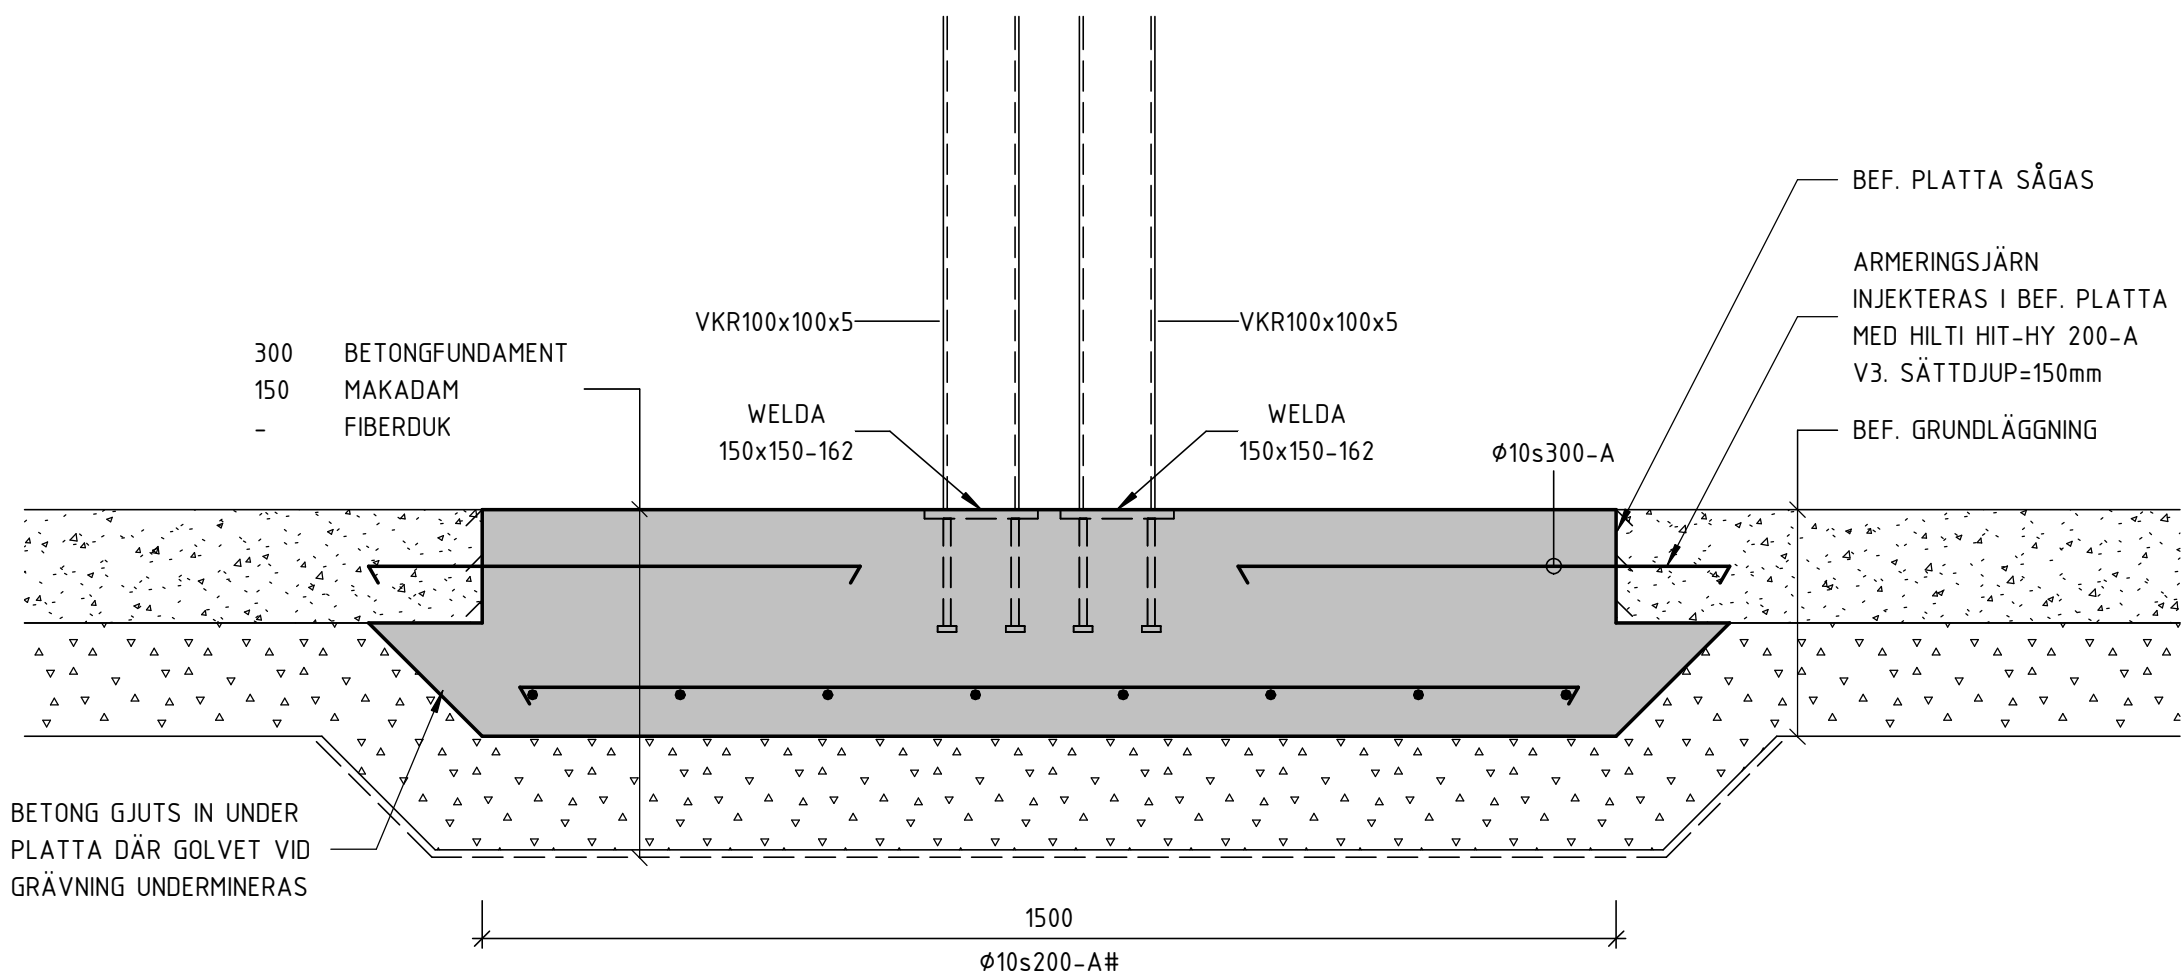

C001
1 : 10

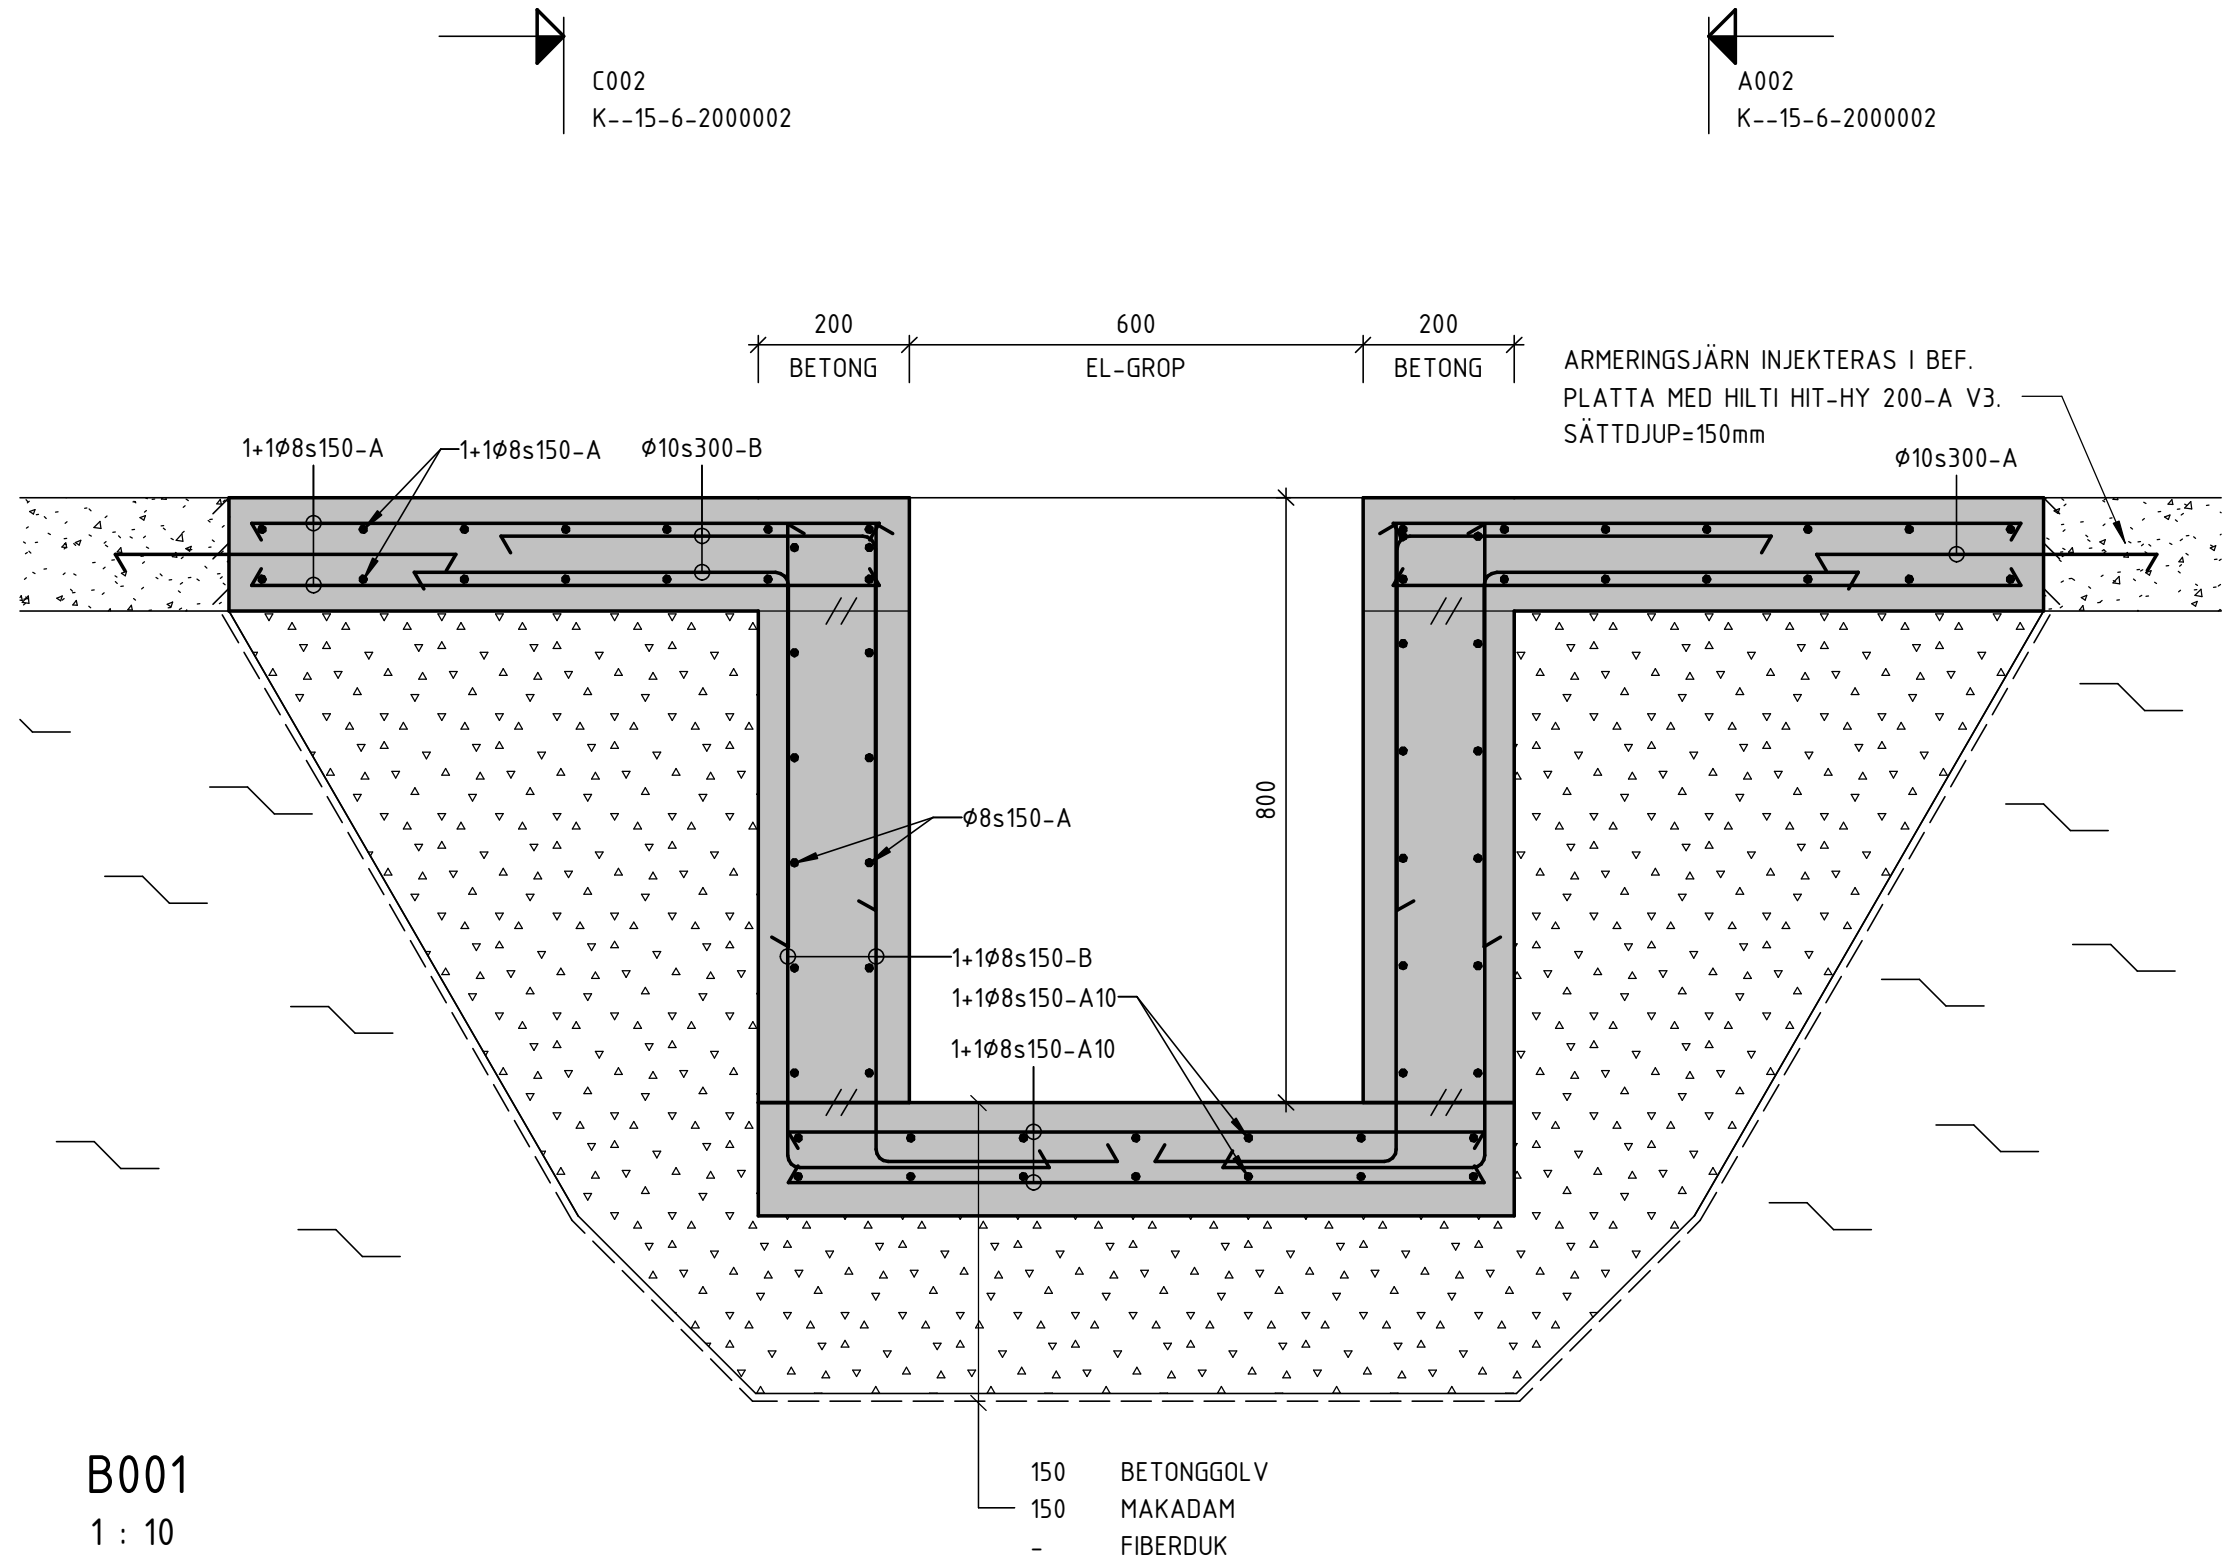

B001
1 : 10

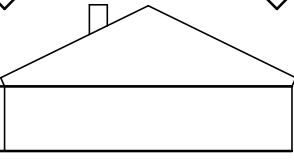BET	ÄNDRING AVSER		DATUM	SIGN
FÖRFRÅGNINGSUNDERLAG				
 HELSINGBORG FASTIGHETSFÖRVALTNINGEN				
FASTIGHET				
ORIENTEN 6				
RÖNNOWSKA SKOLAN, NYTT KÖK OCH MATSAL				
OBJEKTSNR	BYGGNADS-ID	PROJEKTNR		
1457	5-266088	60095		
BYGGNAD				
1457-20 – HUS V (BYGGNAD 449)				
ORIENTERINGSGRUPP	PLAN 03			
02 01 				
DEL				
				
VÄSTRA SANDGATAN				
A	ARKITEKTLAGET SKÅNE AB		T: 042-19 96 00	
BR	FIRETECH ENGINEERING EMRON AB		T: 042-400 02 20	
E	DEVELCON AB		T: 079-020 27 02	
K	ÅKERMANS INGENJÖRSBYRÅ AB		T: 042-12 00 10	
M	TYRÉNS SVERIGE AB		T: 010-452 20 00	
S	SWECO SVERIGE AB		T: 08-695 60 00	
SK	STORKÖKSVISION AB		T: 040-744 29	
V	SWECO SVERIGE AB		T: 08-695 60 00	
W	SWECO SVERIGE AB		T: 08-695 60 00	
C	ZYNKA BIM AB		T: 0734-45 98 99	
UPPDRAGSNR	ANSVARIG			
P1001337	HUGO JACOBSSON			
DATUM	RITAD/KONSTR AV	HANDLÄGGARE	SYSTEMBETECKNING	
2025-01-27	HJ	HJ	15-2	
Hus 20				
GRUNDSEKTIONER				
SKALA	NUMMER			REV
1 : 10	K--15-6-2000001			

ORIGINALFORMAT: A1

