




F:\PROJEKT\2022\2000546 Rönönska skolan Hus V, Helsingborg\KUP\1001337 Ombyggnad till matsal storokk\Modell\Revit\2023P\1001337_FFU.rvt 2025-01-24 09:54:08

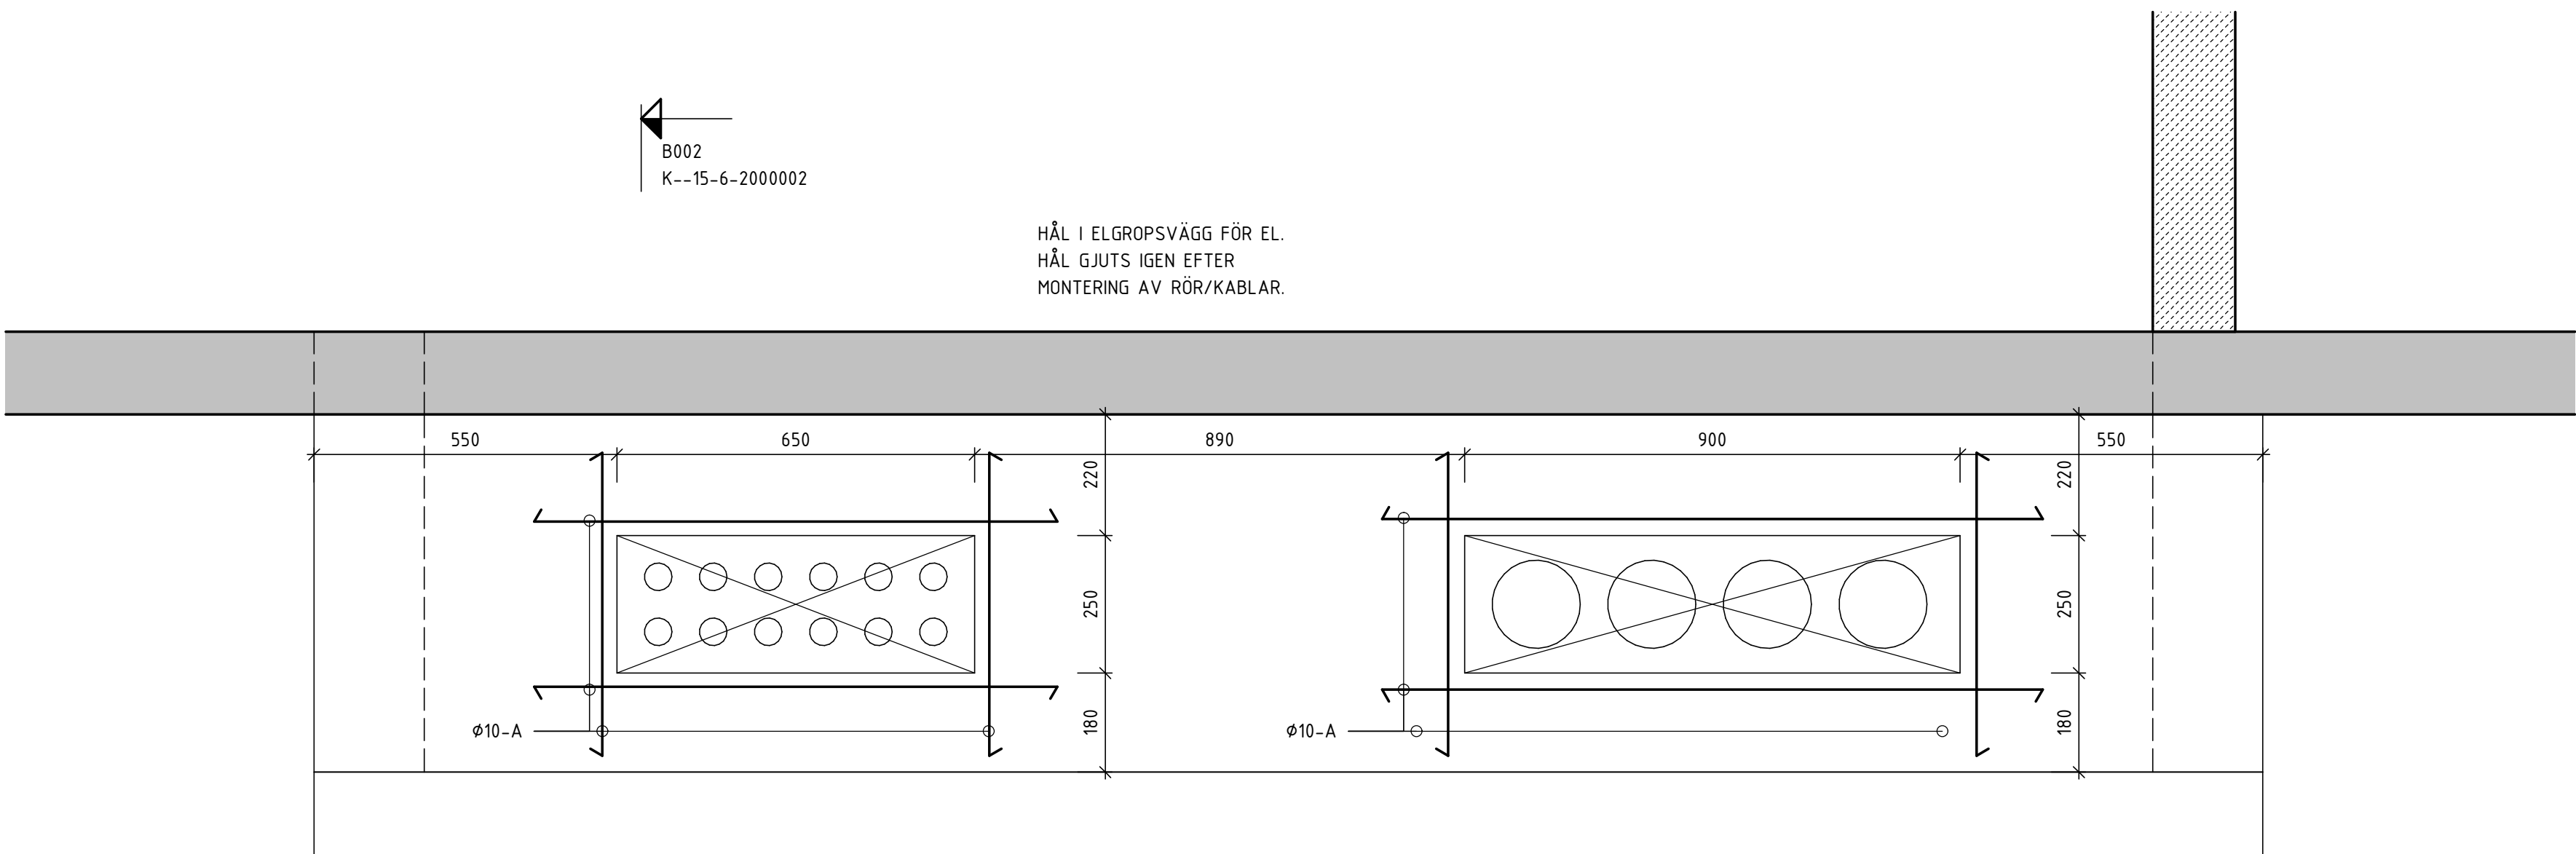

A002
1 : 10

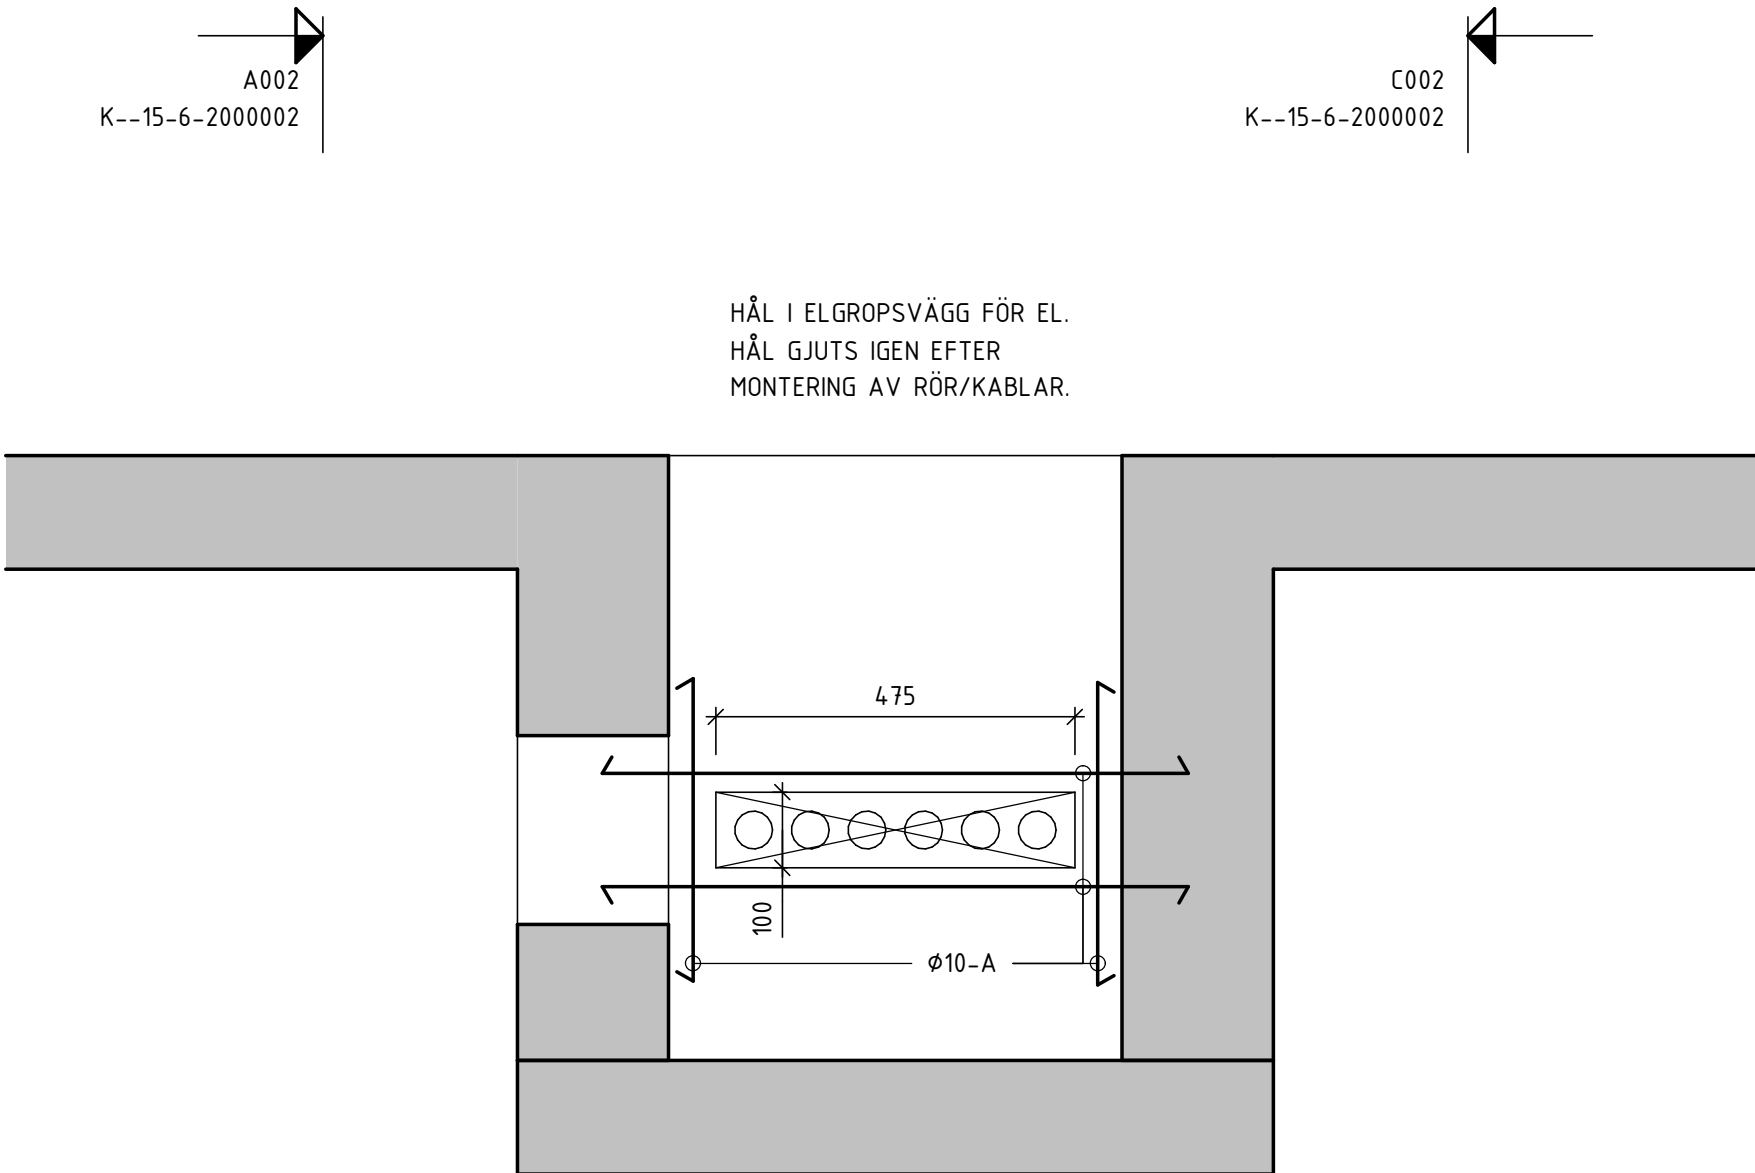


B002
1 : 10

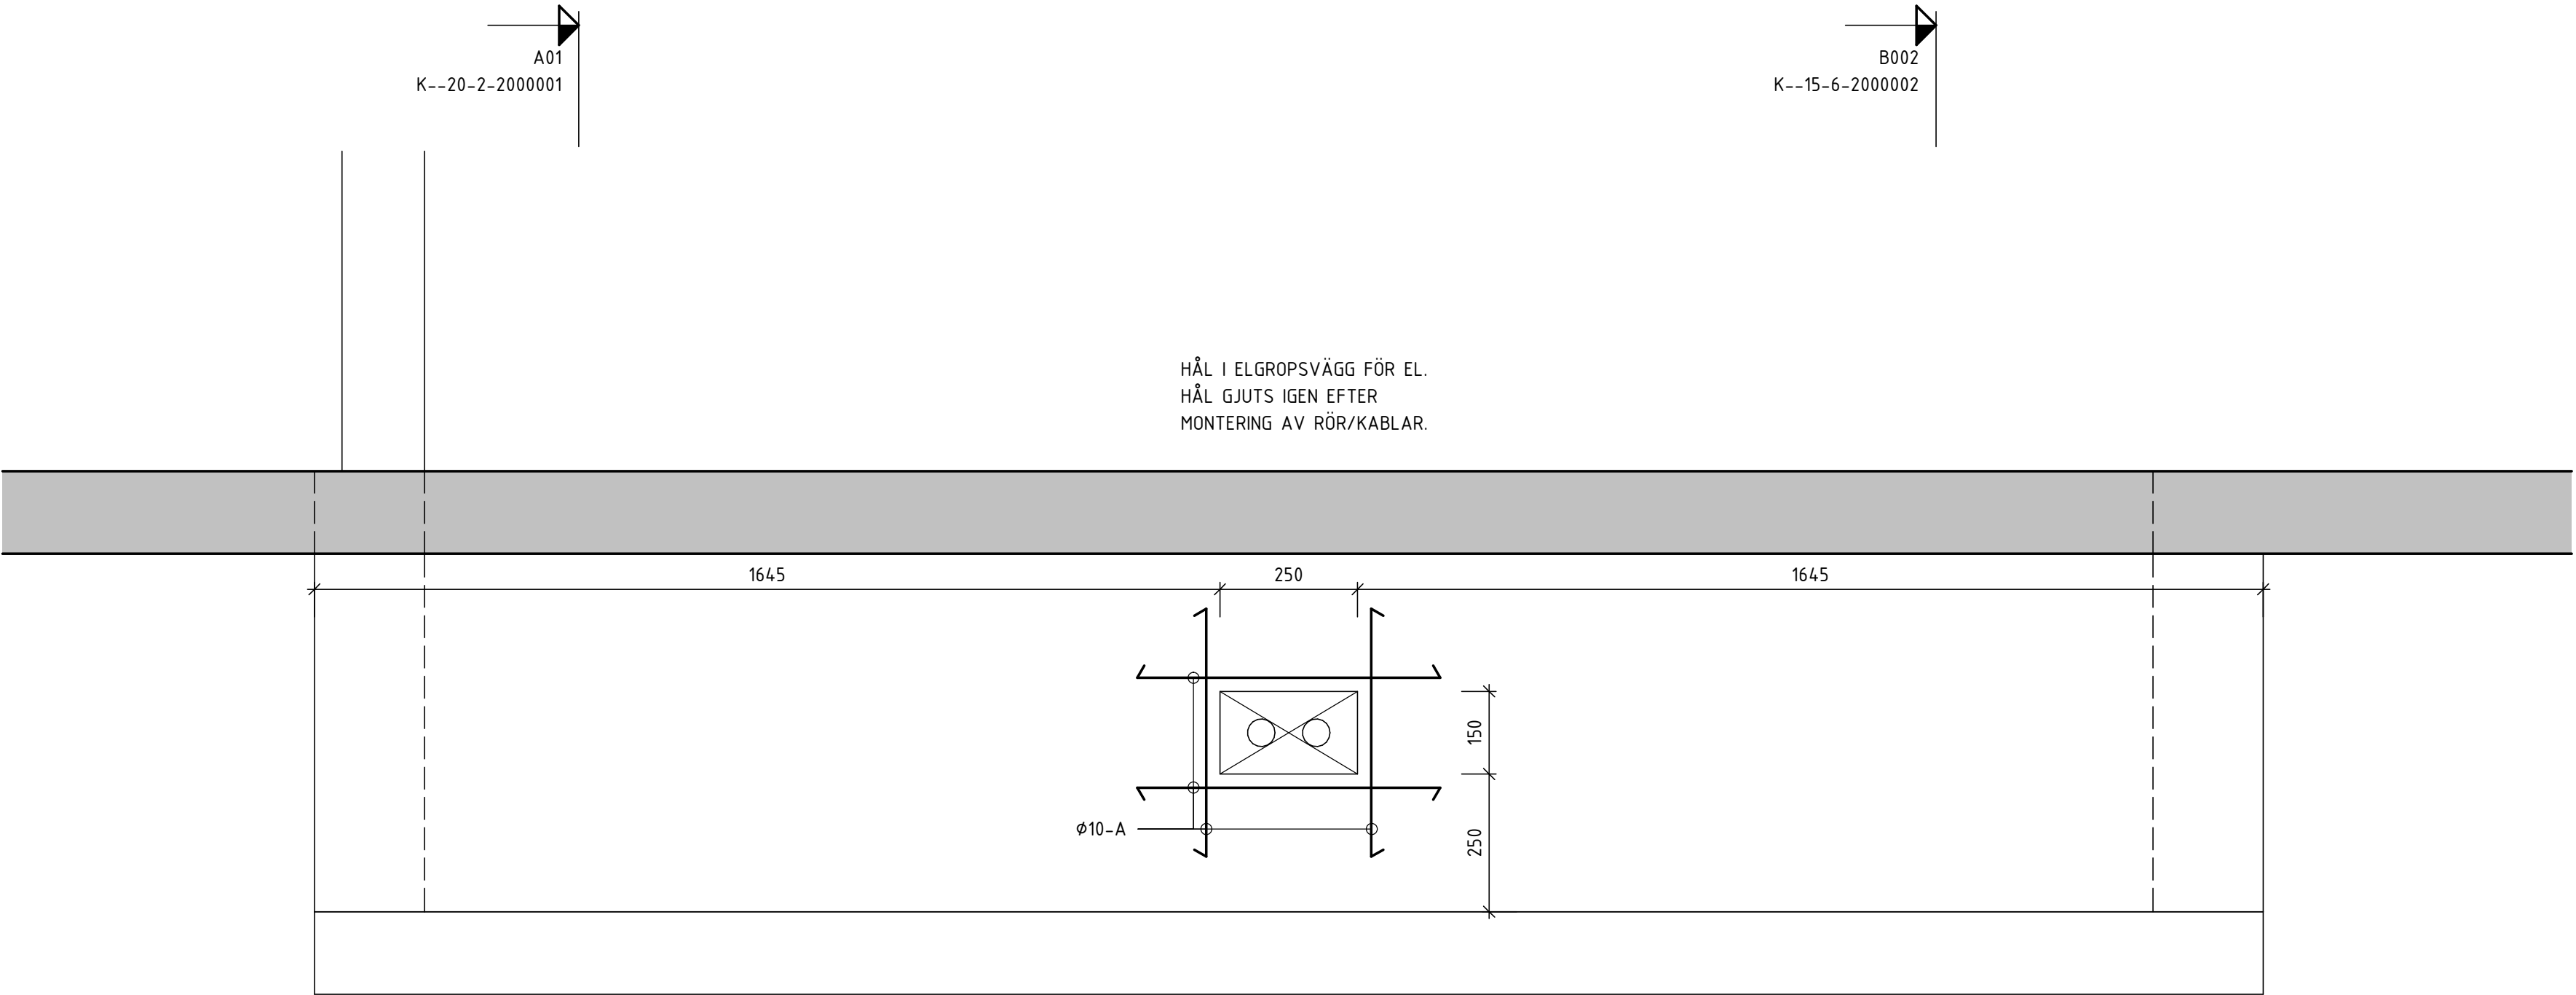

C002
1 : 10

SKALA 1:10 (A1-format) 0 0.5 1 METER

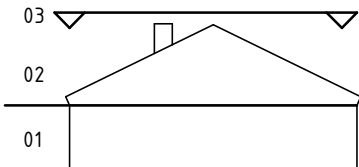BET	ÄNDRING AVSER	DATUM	SIGN
FÖRFRÅGNINGSUNDERLAG			
 HELSINGBORG FASTIGHETSFÖRVALTNINGEN			
FASTIGHET ORIENTEN 6 RÖNNOWSKA SKOLAN, NYTT KÖK OCH MATSAL			
OBJEKTSNR 1457	BYGGNADS-ID 5-266088	PROJEKTNR 60095	
BYGGNAD 1457-20 - HUS V (BYGGNAD 449)			
ORIENTERINGSFIGUR PLAN 03 02 01 DEL  VÄSTRA SANDGATAN N			
A	ARKITEKTLAGET SKÅNE AB	T: 042-19 96 00	
BR	FIRETECH ENGINEERING EMRON AB	T: 042-400 02 20	
E	DEVELCON AB	T: 079-020 27 02	
K	ÅKERMANS INGENJÖRSBYRÅ AB	T: 042-12 00 10	
M	TYRÉNS SVERIGE AB	T: 010-452 20 00	
S	SWECO SVERIGE AB	T: 08-695 60 00	
SK	STORKÖKSVISION AB	T: 040-744 29	
V	SWECO SVERIGE AB	T: 08-695 60 00	
W	SWECO SVERIGE AB	T: 08-695 60 00	
C	ZYNKA BIM AB	T: 0734-45 98 99	
UPPDRAGSNR P1001337	ANSVARIG HUGO JACOBSSON		
DATUM 2025-01-27	RITAD/KONSTR AV HJ	HANDLÄGGARE HJ	SYSTEMBETECKNING 15-2
Hus 20 GRUNDSEKTIONER HÅLBILD I ELGROP			
SKALA 1 : 10	NUMMER K--15-6-2000002	REV	

ORIGINALFORMAT: A1