



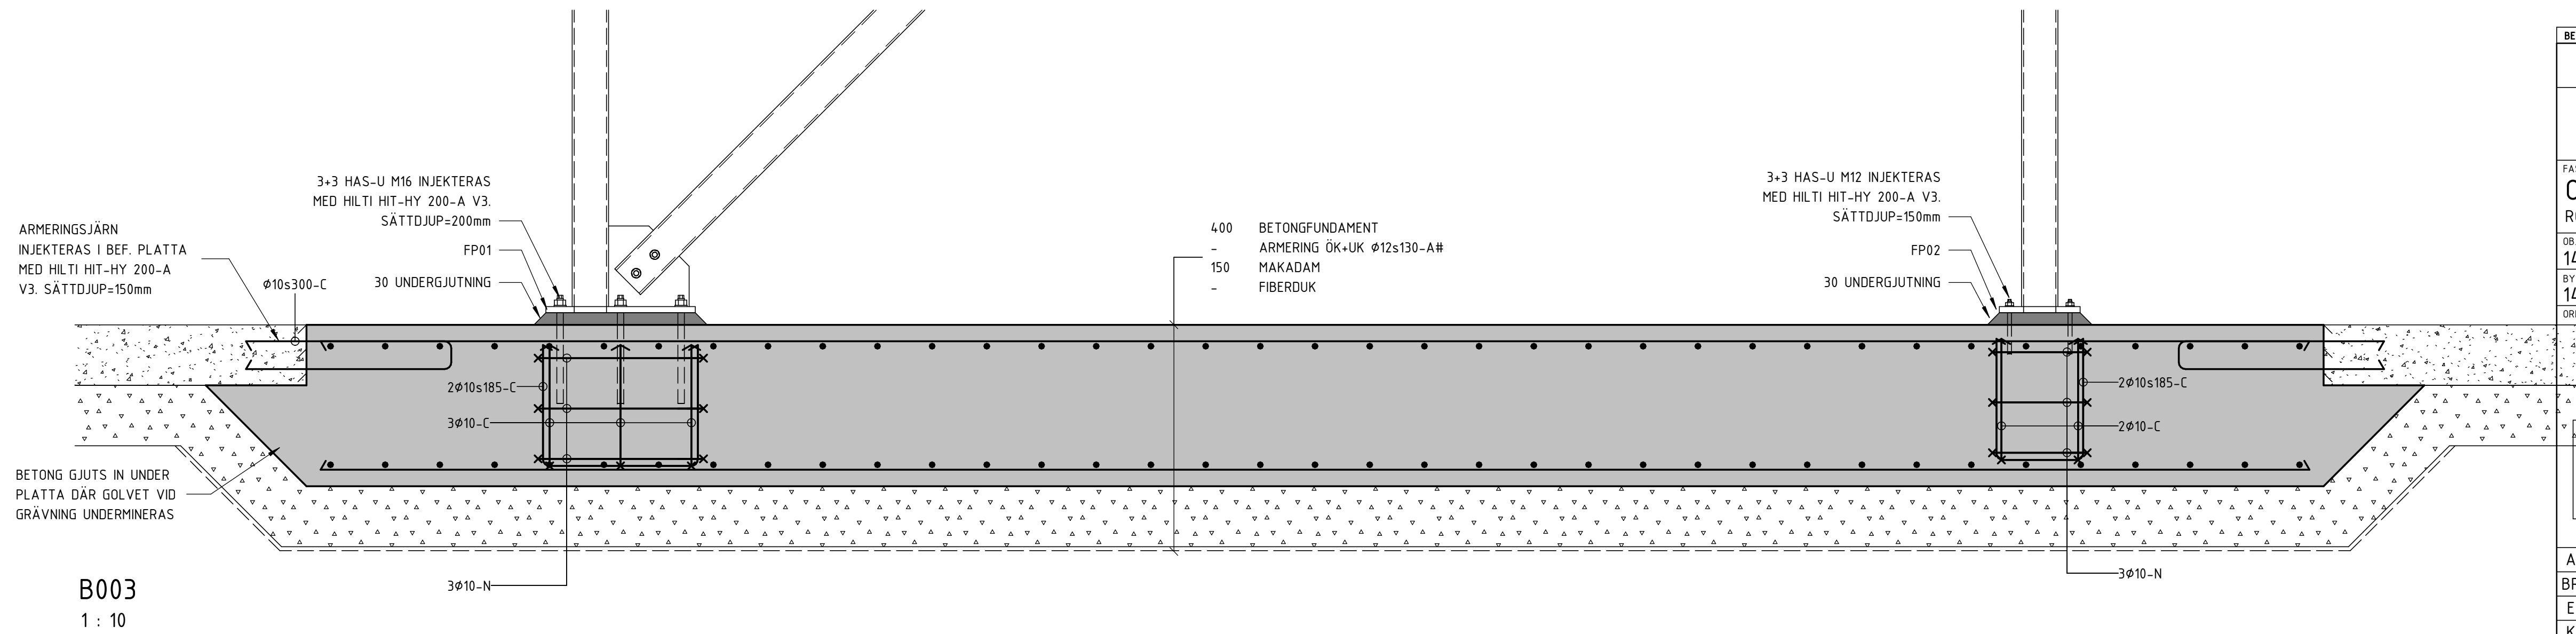

BET	ÄNDRING AVSER	DATUM	SIGN
FÖRFRÅGNINGSUNDERLAG			
HELSINGBORG FASTIGHETSFÖRVALTNINGEN			
FASTIGHET			
ORIENTEN 6			
RÖNNOWSKA SKOLAN, NYTT KÖK OCH MATSAL			
OBJEKTSNR	BYGGNADS-ID	PROJEKTNR	
1457	5-266088	60095	
BYGGNAD			
1457-20 – HUS V (BYGGNAD 449)			
ORIENTERINGSFIGUR			
PLAN 03			
02 01 <			

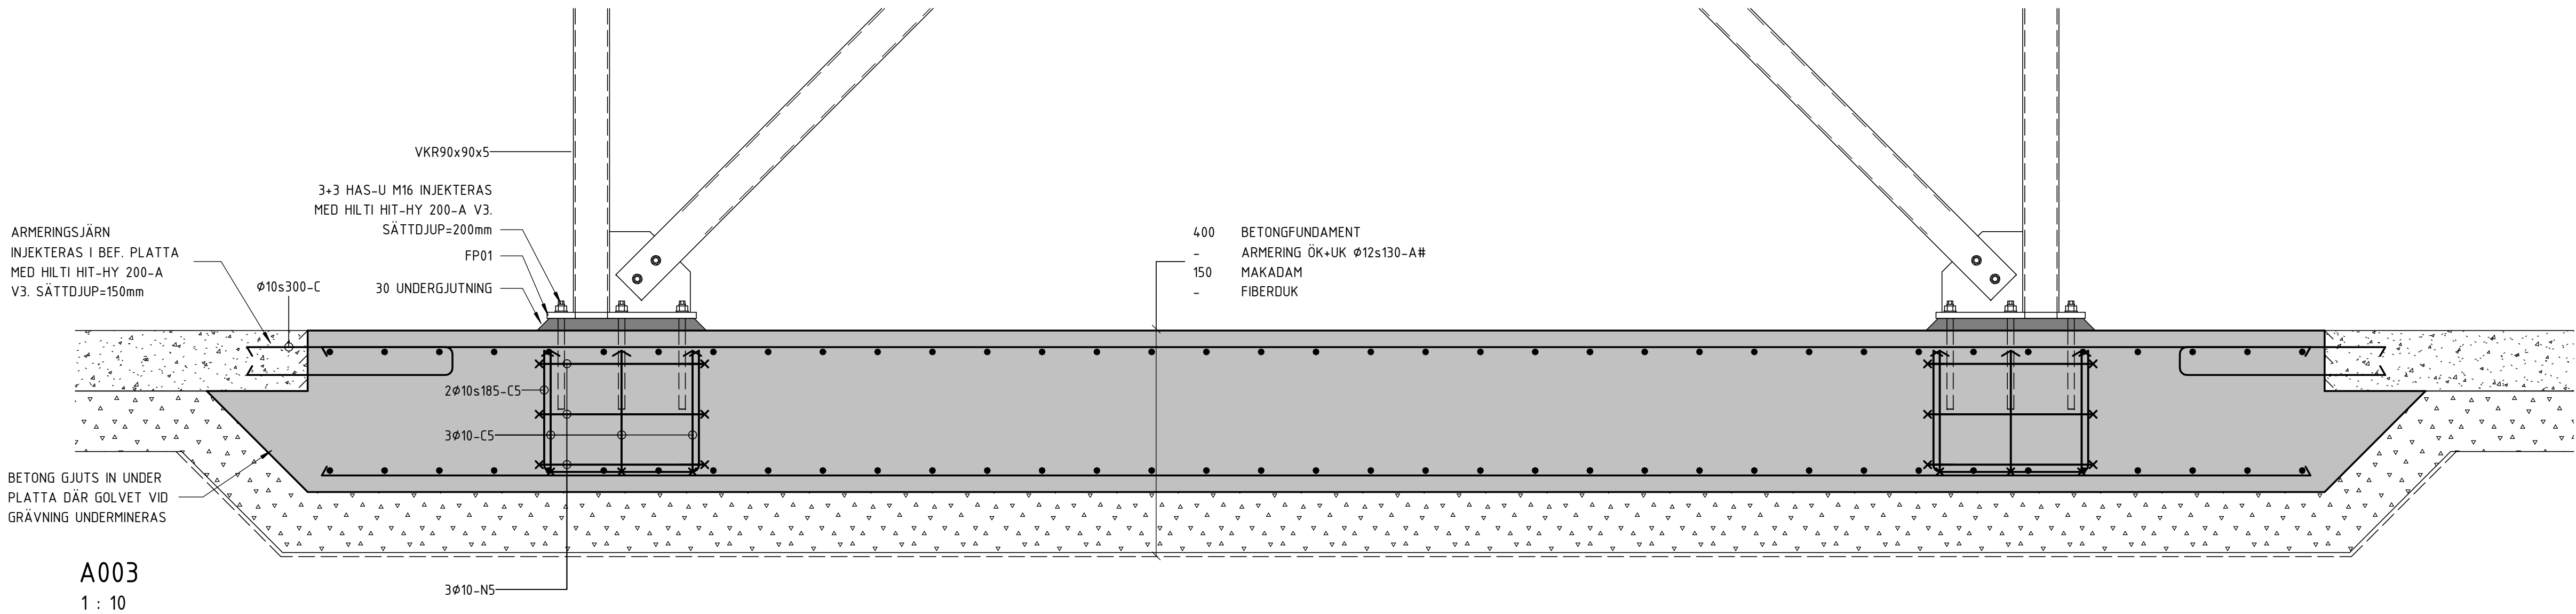