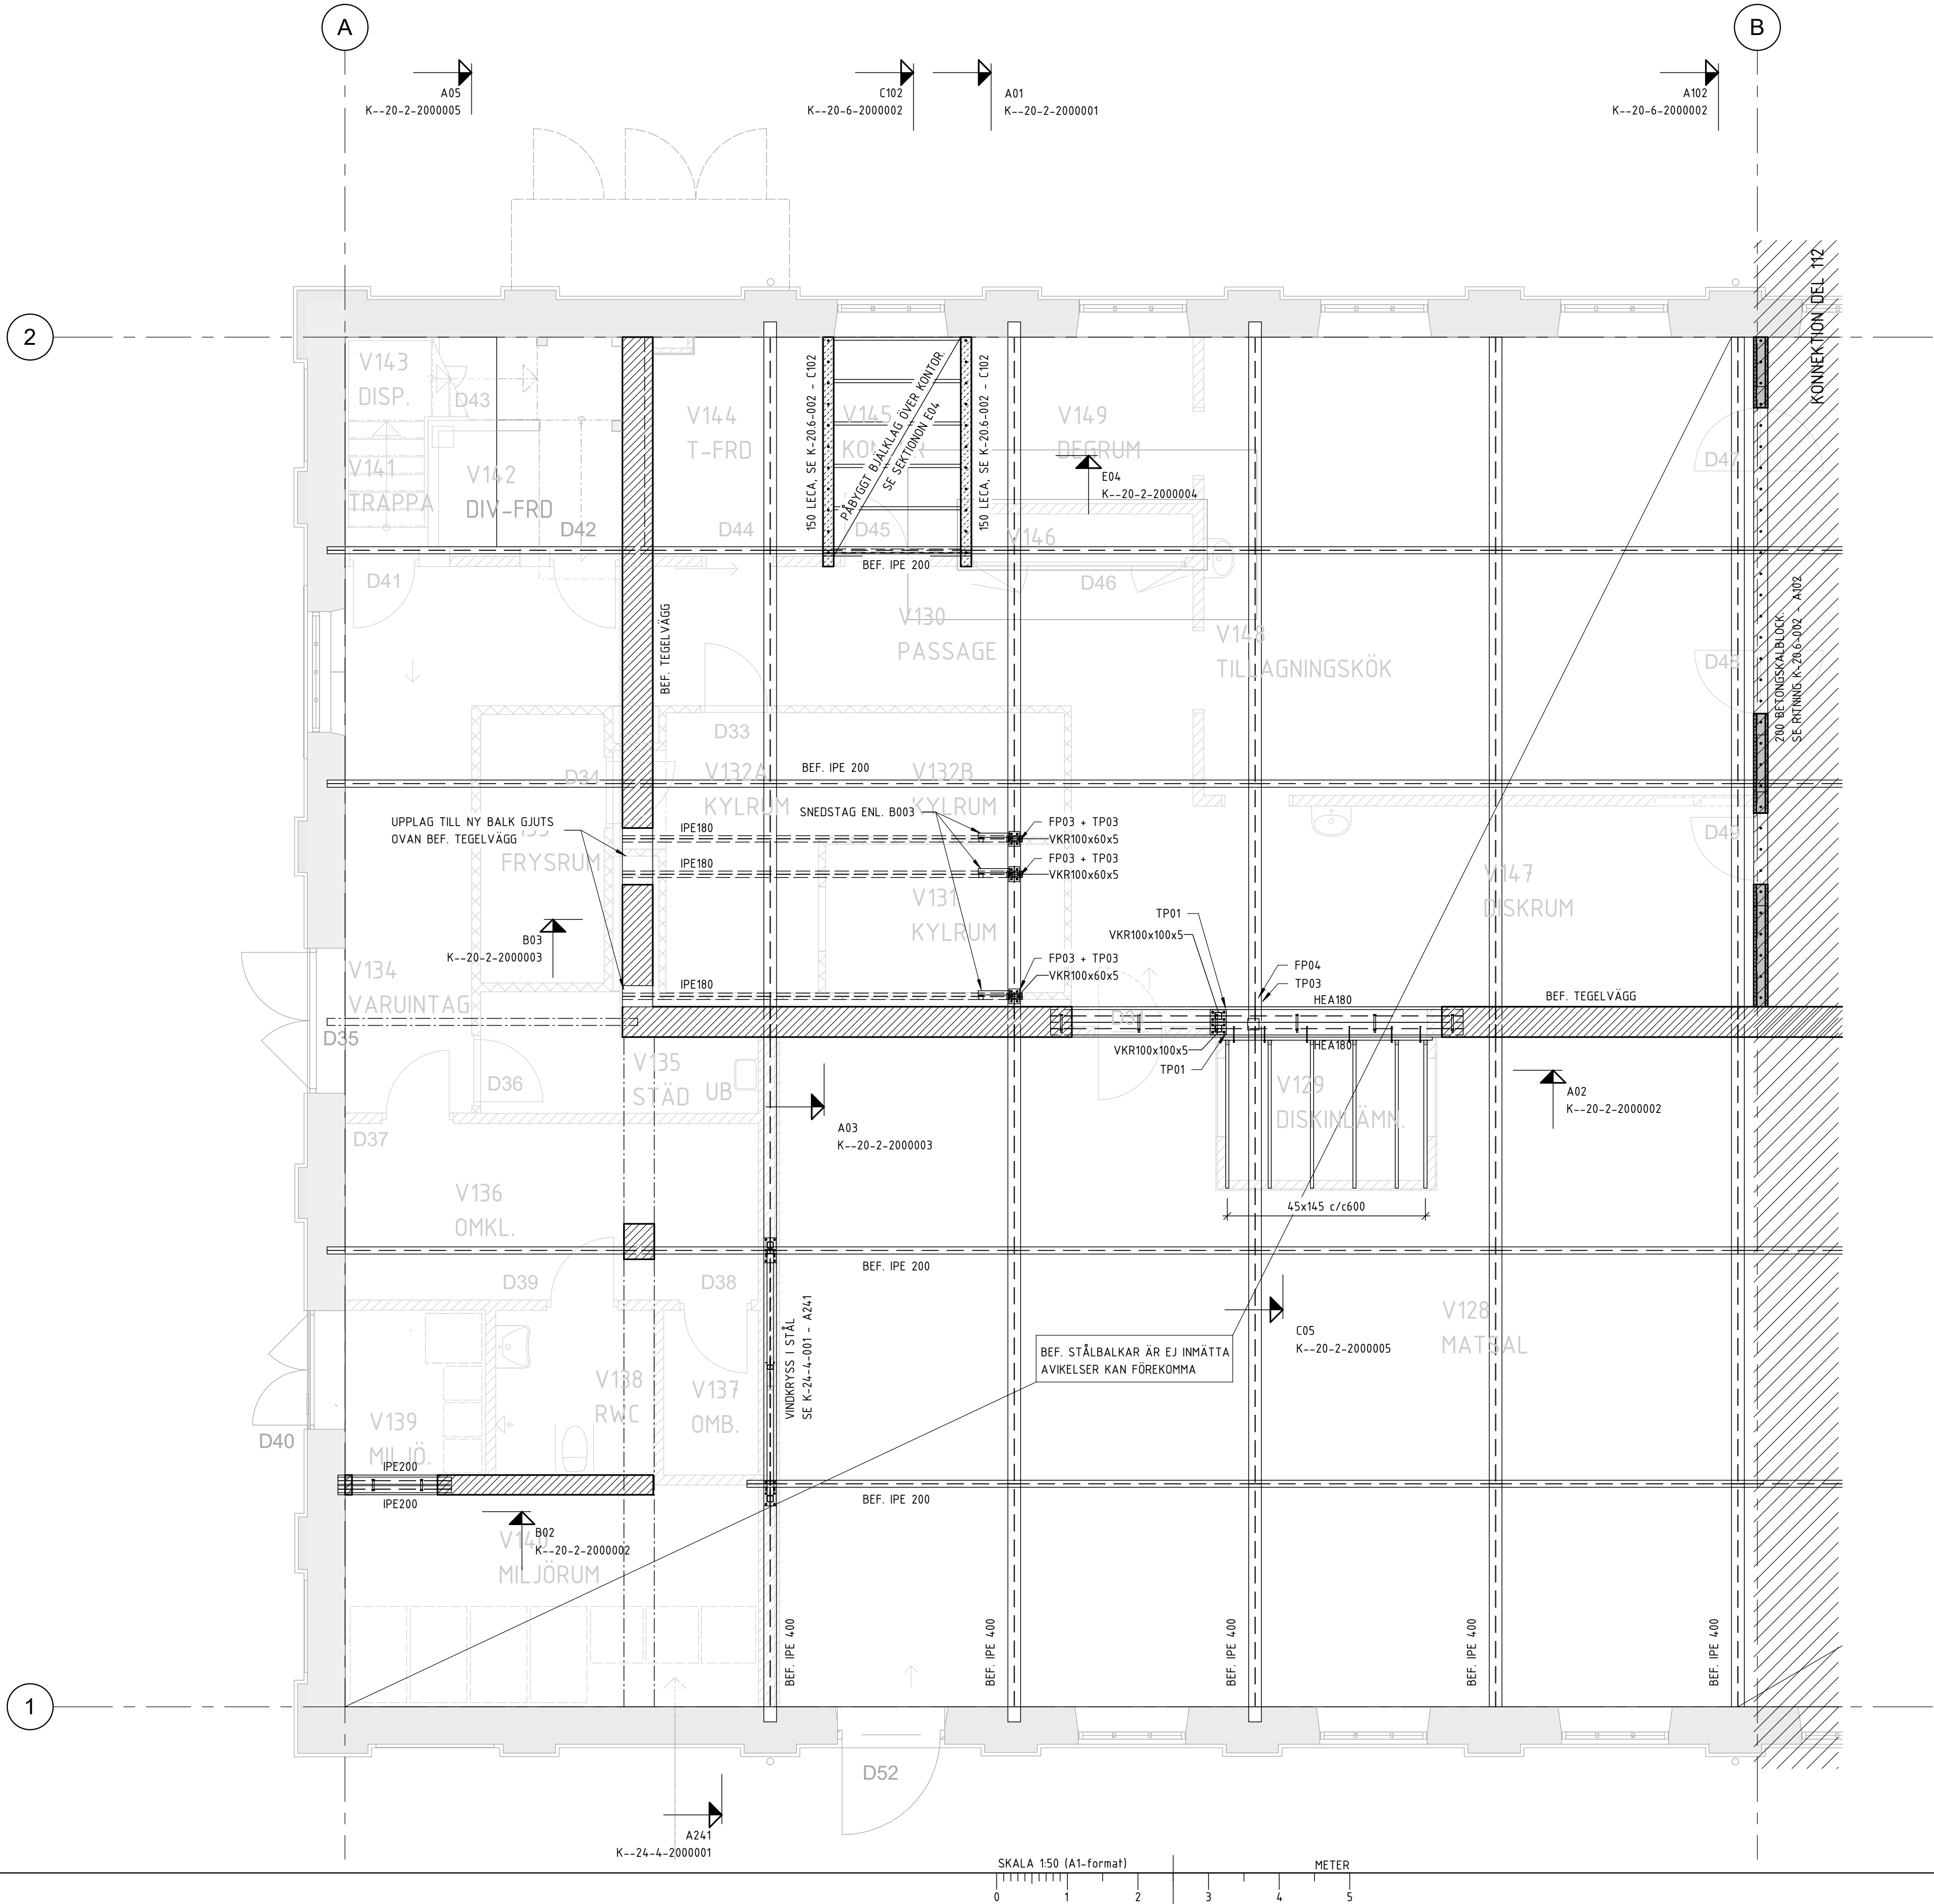




FÖRKLARINGAR

- 1 FÖRSTÄRKNING VID UPPLAG EN SIDA
- 2 FÖRSTÄRKNING VID UPPLAG BÅDA SIDOR

ÖVRIGT SE K--01-5-2000001

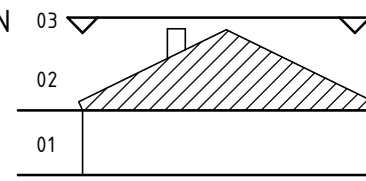
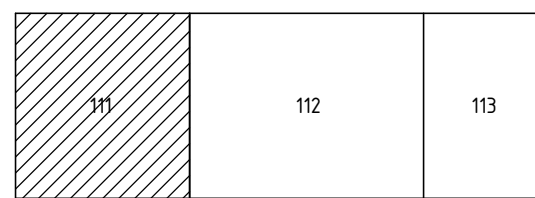
FÖRESKRIFTER

SE K--01-5-2000001

HÄNVISNINGAR

ALLMÄNNA ANVISNINGAR

K--01-5-2000001

BET	ÄNDRING AVSER		DATUM	SIGN
FÖRFRÅGNINGSUNDERLAG				
 HELSINGBORG FASTIGHETSFÖRVALTNINGEN				
FASTIGHET				
ORIENTEN 6				
RÖNNOWSKA SKOLAN, NYTT KÖK OCH MATSAL				
OBJEKTSNR	BYGGNADS-ID		PROJEKTNR	
1457	5-266088		60095	
BYGGNAD				
1457-20 – HUS V (BYGGNAD 449)				
ORIENTERINGSFIGUR				
PLAN 03 				
DEL				
				
VÄSTRA SANDGATAN				
A	ARKITEKTLAGET SKÅNE AB		T: 042-19 96 00	
BR	FIRETECH ENGINEERING EMRON AB		T: 042-400 02 20	
E	DEVELCON AB		T: 079-020 27 02	
K	ÅKERMANS INGENJÖRSBYRÅ AB		T: 042-12 00 10	
M	TYRÉNS SVERIGE AB		T: 010-452 20 00	
S	SWECO SVERIGE AB		T: 08-695 60 00	
SK	STORKÖKSVISION AB		T: 040-744 29	
V	SWECO SVERIGE AB		T: 08-695 60 00	
W	SWECO SVERIGE AB		T: 08-695 60 00	
C	ZYNKA BIM AB		T: 0734-45 98 99	
UPPDRAGSNR		ANSVARIG		
P1001337		HUGO JACOBSSON		
DATUM		RITAD/KONSTR AV	HANDLÄGGARE	SYSTEMBETECKNING
2025-01-27		HJ	HJ	20-1
HUS 20				
BJÄLKLAGSPÅN DEL 111				
SKALA		NUMMER		REV
1 : 50		K--20-1-2001111		
ORIGINALFORMAT: A1				