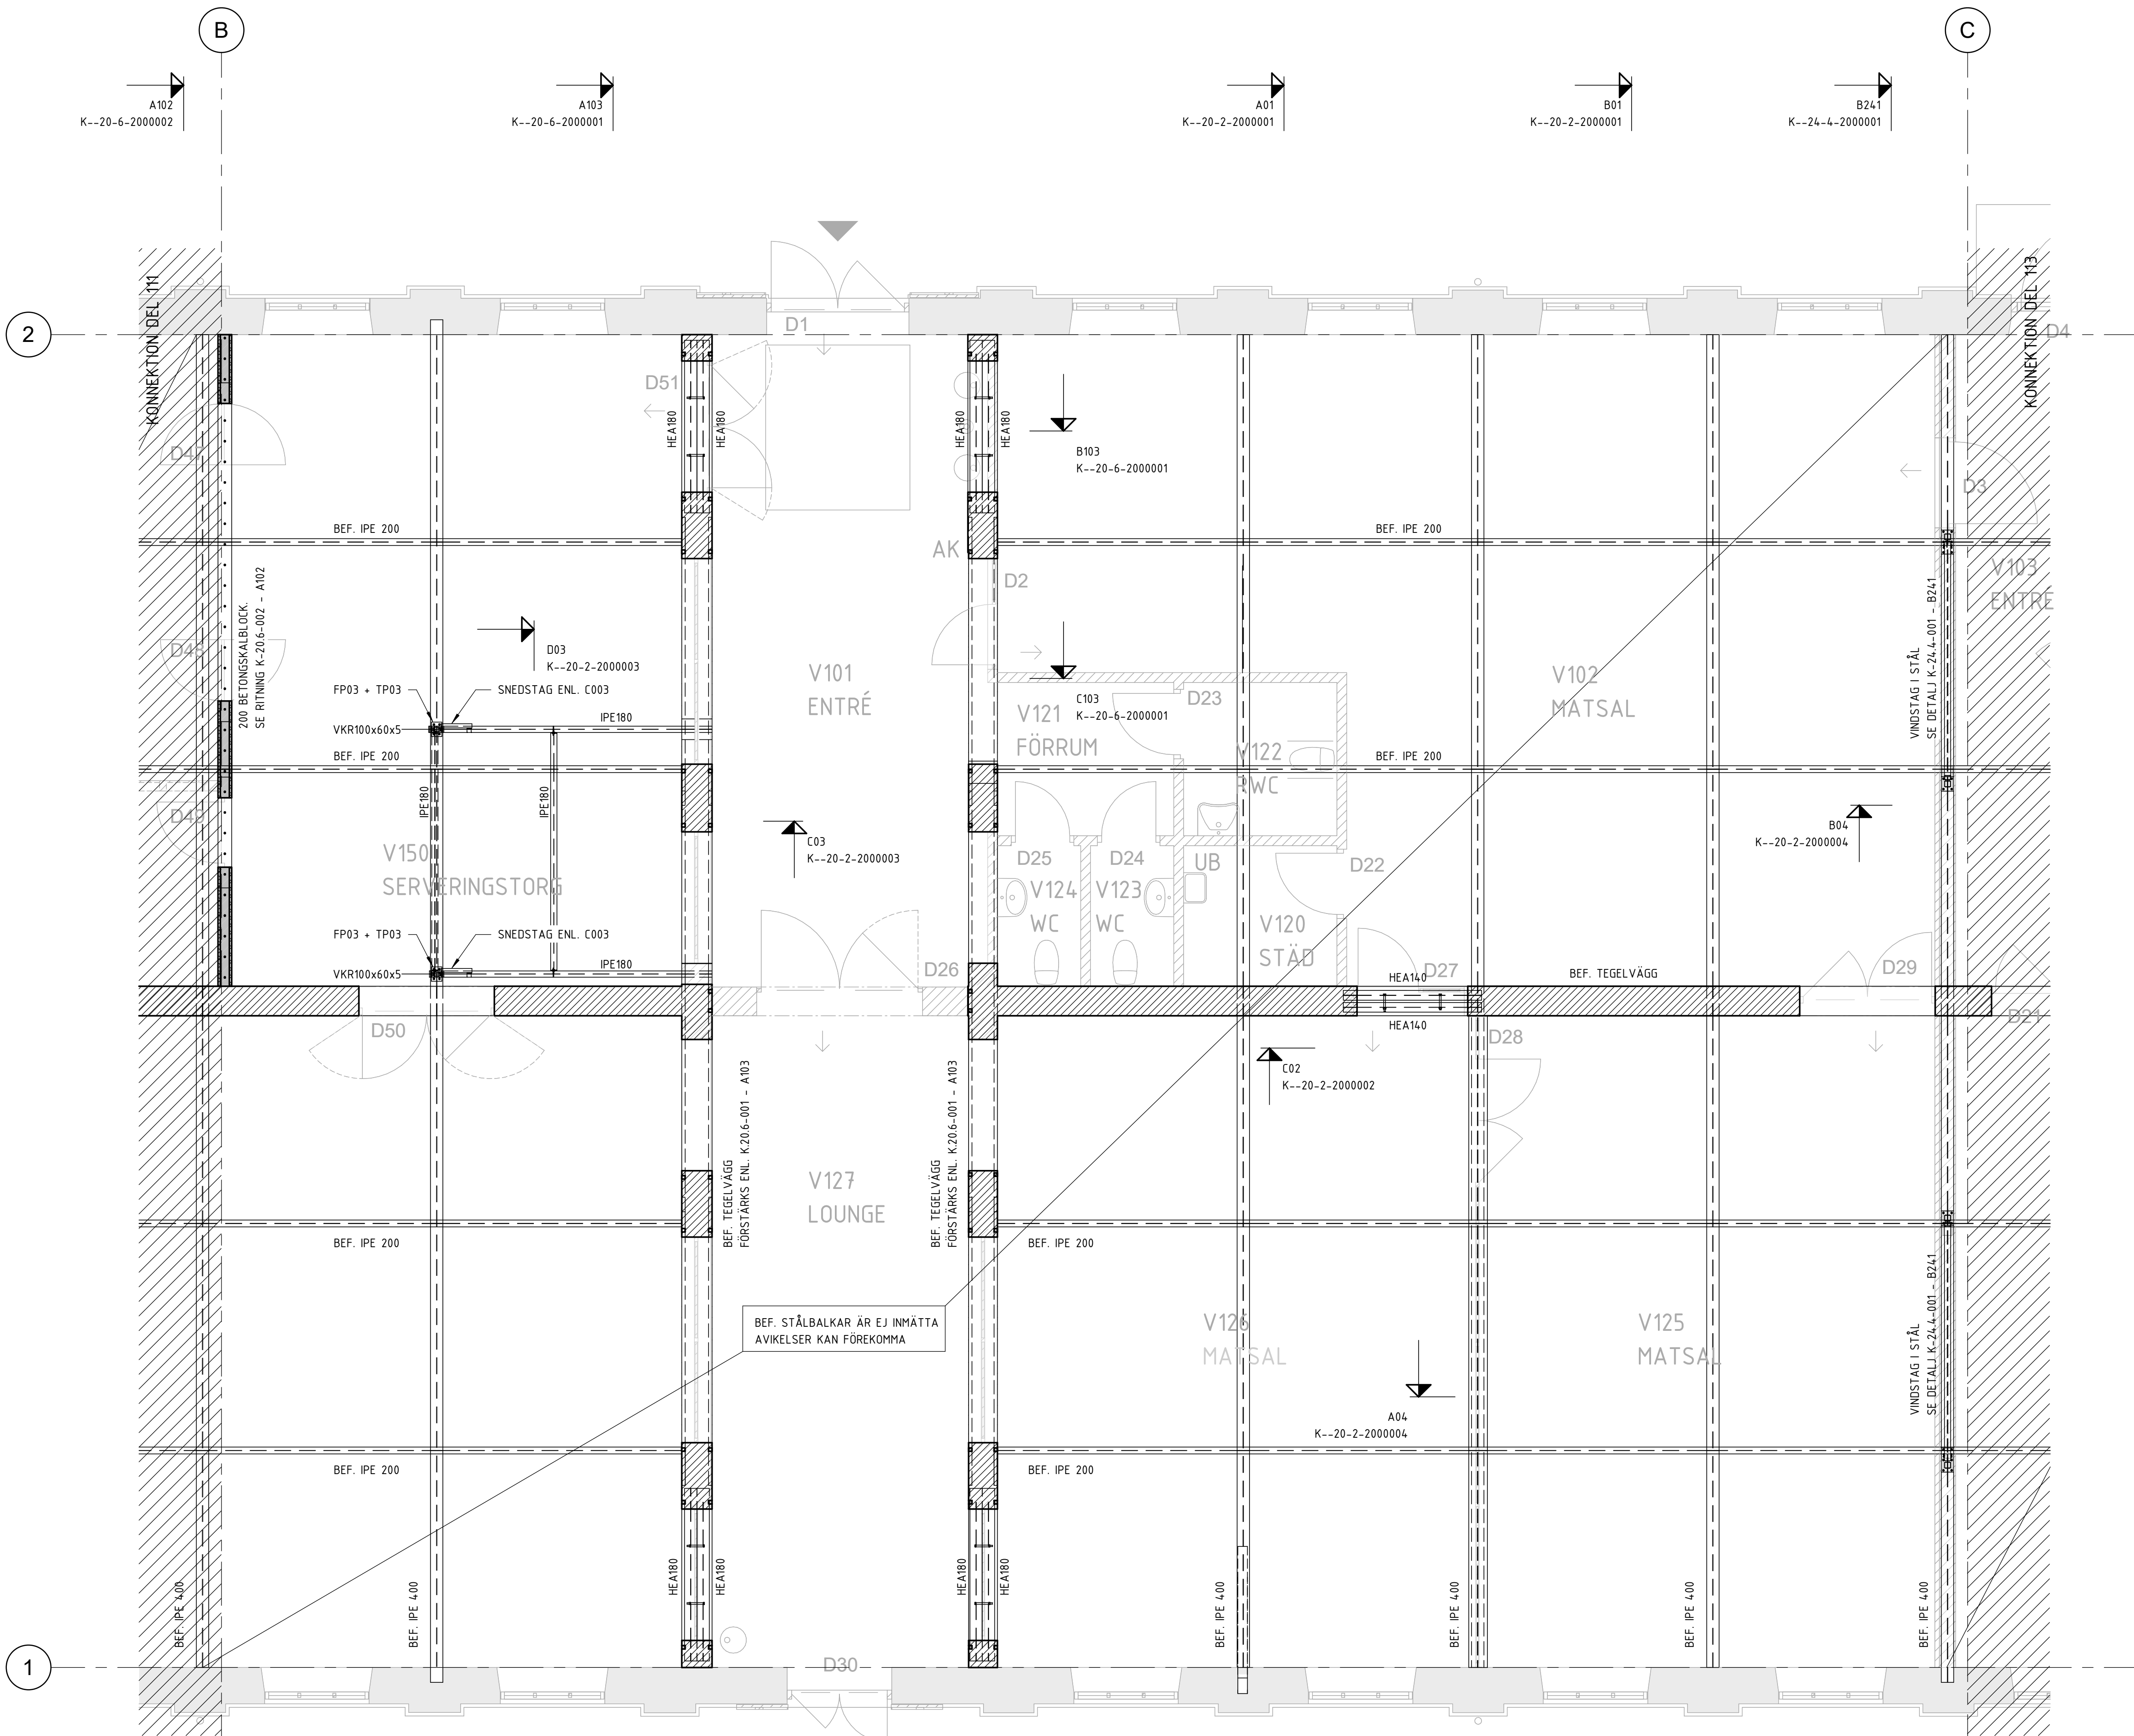




FÖRKLARINGAR

- 1 FÖRSTÄRKNING VID UPPLAG EN SIDA
- 2 FÖRSTÄRKNING VID UPPLAG BÅDA SIDOR

ÖVRIGT SE K--01-5-2000001

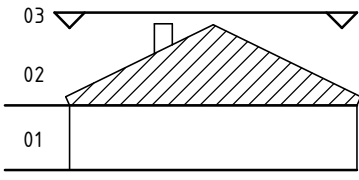
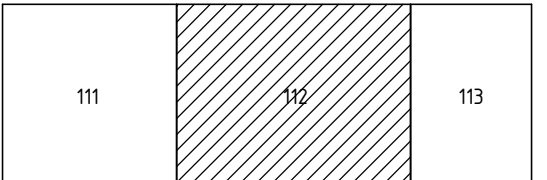
FÖRESKRIFTER

SE K--01-5-2000001

HÄNVISNINGAR

ALLMÄNNA ANVISNINGAR

K--01-5-2000001

BET	ÄNDRING AVSER	DATUM	SIGN
FÖRFRÅGNINGSUNDERLAG			
 HELSINGBORG FASTIGHETSFÖRVALTNINGEN			
FASTIGHET ORIENTEN 6 RÖNNÖWSKA SKOLAN, NYTT KÖK OCH MATSAL			
OBJEKTSNR 1457	BYGGNADS-ID 5-266088	PROJEKTNR 60095	
BYGGNAD 1457-20 - HUS V (BYGGNAD 449)			
ORIENTERINGSFIGUR PLAN 03 			
DEL  VÄSTRA SANDGATAN			
A ARKITEKTLAGET SKÅNE AB T: 042-19 96 00			
BR FIRETECH ENGINEERING EMRON AB T: 042-400 02 20			
E DEVELCON AB T: 079-020 27 02			
K ÅKERMANS INGENJÖRSBYRÅ AB T: 042-12 00 10			
M TYRÉNS SVERIGE AB T: 010-452 20 00			
S SWECO SVERIGE AB T: 08-695 60 00			
SK STORKÖKSVISION AB T: 040-744 29			
V SWECO SVERIGE AB T: 08-695 60 00			
W SWECO SVERIGE AB T: 08-695 60 00			
C ZYNKA BIM AB T: 0734-45 98 99			
UPPDRAGSNR P1001337	ANSVARIG HUGO JACOBSSON		
DATUM 2025-01-27	RITAD/KONSTR AV HJ	HANDLÄGGARE HJ	SYSTEMBETECKNING 20-1
HUS 20 BJÄLKLAGSPAN DEL 112			
SKALA 1 : 50	NUMMER K--20-1-2001112	REV	

ORIGINALFORMAT: A1