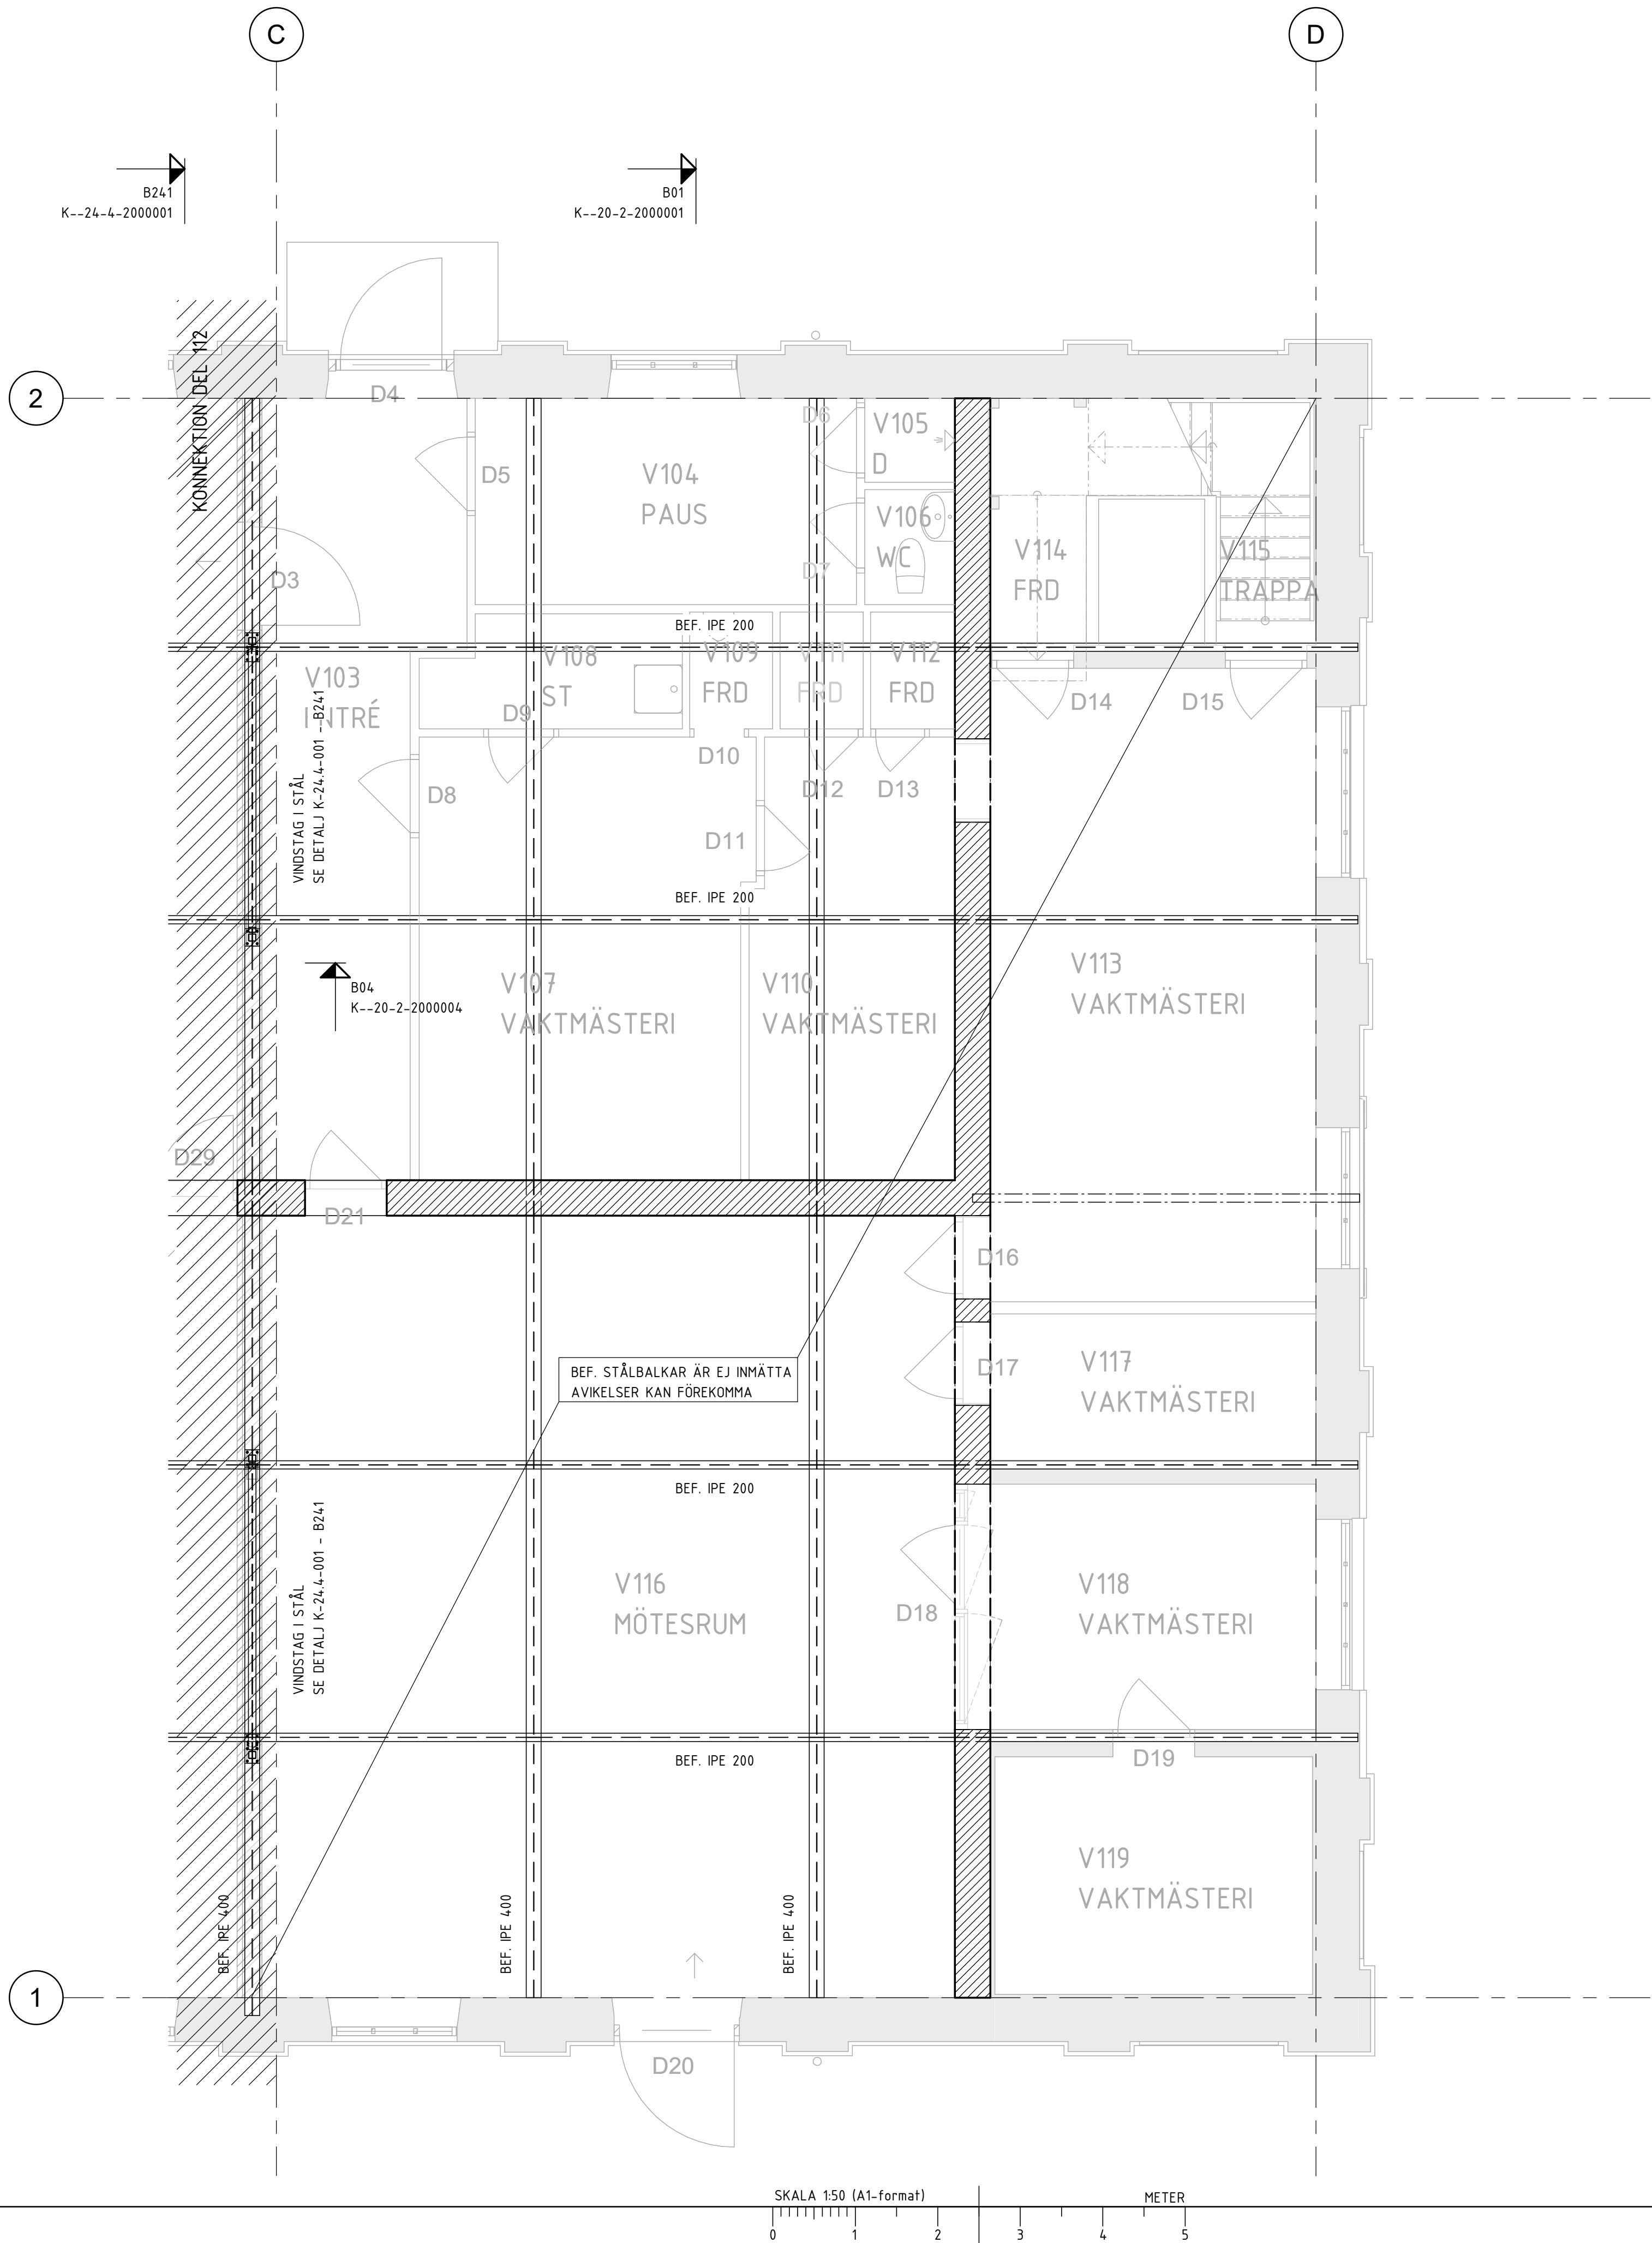




FÖRKLARINGAR

- 1 FÖRSTÄRKNING VID UPPLAG EN SIDA
- 2 FÖRSTÄRKNING VID UPPLAG BÅDA SIDOR

ÖVRIGT SE

K--01-5-2000001

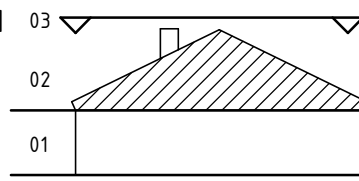
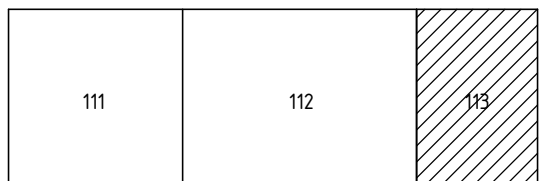
FÖRESKRIFTER

SE K--01-5-2000001

HÄNVISNINGAR

ALLMÄNNA ANVISNINGAR

K--01-5-2000001

BET	ÄNDRING AVSER		DATUM	SIGN
FÖRFRÅGNINGSUNDERLAG				
 HELSINGBORG FASTIGHETSFÖRVALTNINGEN				
FASTIGHET				
ORIENTEN 6				
RÖNNOWSKA SKOLAN, NYTT KÖK OCH MATSAL				
OBJEKTSNR	BYGGNADS-ID		PROJEKTNR	
1457	5-266088		60095	
BYGGNAD				
1457-20 – HUS V (BYGGNAD 449)				
ORIENTERINGSFIGUR				
PLAN 03				
				
DEL				
				
VÄSTRA SANDGATAN				
A	ARKITEKTLAGET SKÅNE AB			T: 042-19 96 00
BR	FIRETECH ENGINEERING EMRON AB			T: 042-400 02 20
E	DEVELCON AB			T: 079-020 27 02
K	ÅKERMANS INGENJÖRSBYRÅ AB			T: 042-12 00 10
M	TYRÉNS SVERIGE AB			T: 010-452 20 00
S	SWECO SVERIGE AB			T: 08-695 60 00
SK	STÖRKÖKSVISION AB			T: 040-744 29
V	SWECO SVERIGE AB			T: 08-695 60 00
W	SWECO SVERIGE AB			T: 08-695 60 00
C	ZYNKA BIM AB			T: 0734-45 98 99
UPPDRAGSNR		ANSVARIG		
P1001337		HUGO JACOBSSON		
DATUM		RITAD/KONSTR AV	HANDLÄGGARE	SYSTEMBETECKNING
2025-01-27		HJ	HJ	20-1
HUS 20				
BJÄLKLAGSPLAN DEL 113				
SKALA		NUMMER		REV
1 : 50		K--20-1-2001113		

ORIGINALFORMAT: A1