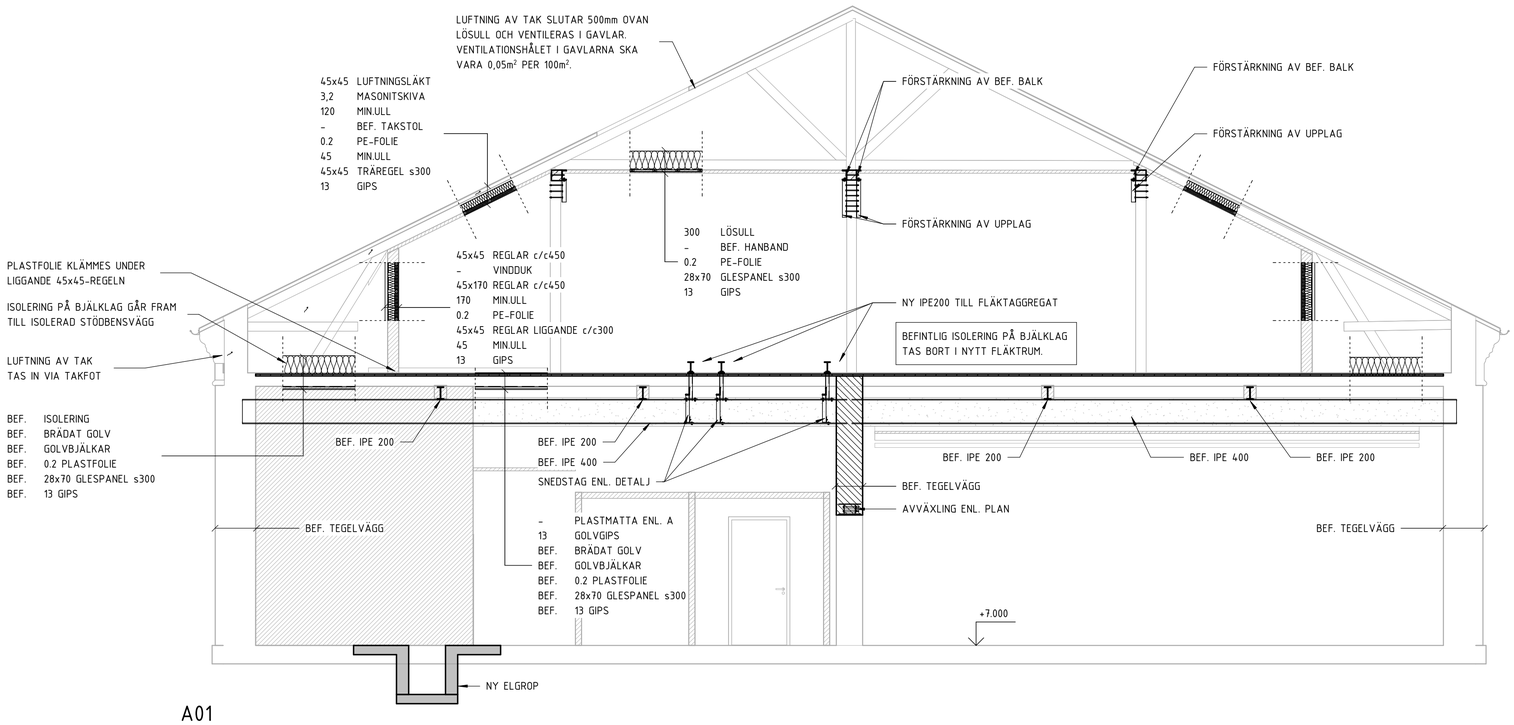

A01
1 : 50

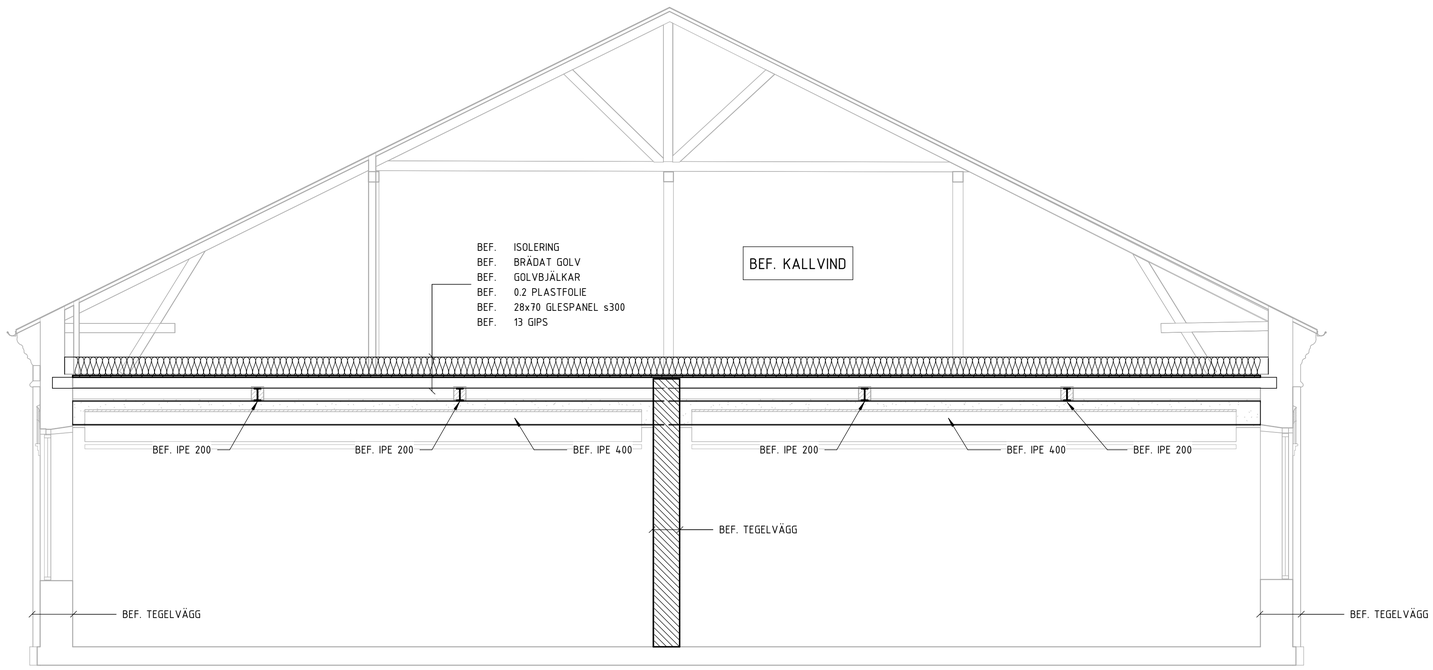

B01
1 : 50

SKALA 1:50 (A1-format)
0 1 2 3 4 5 METER

BET	ÄNDRING AVSER	DATUM	SIGN

FÖRFRÅGNINGSUNDERLAG

HELSINGBORG
FASTIGHETSFÖRVALTNINGEN

FASTIGHET
ORIENTEN 6
RÖNNOWSKA SKOLAN, NYTT KÖK OCH MATSAL

OBJEKTSNR	BYGGNADS-ID	PROJEKTNR
1457	5-266088	60095

BYGGNAD
1457-20 - HUS V (BYGGNAD 449)

ORIENTERINGSFIGUR

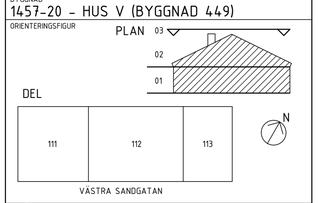

A	ARKITEKTLAGET SKÅNE AB	T: 042-19 96 00
BR	FIRETECH ENGINEERING EMRON AB	T: 042-400 02 20
E	DEVELCON AB	T: 079-020 27 02
K	ÅKERMANS INGENJÖRSBYRÅ AB	T: 042-12 00 10
M	TYRÉNS SVERIGE AB	T: 010-452 20 00
S	SWECO SVERIGE AB	T: 08-695 60 00
SK	STORKÖKSVISION AB	T: 040-744 29
V	SWECO SVERIGE AB	T: 08-695 60 00
W	SWECO SVERIGE AB	T: 08-695 60 00
C	ZYNKA BIM AB	T: 0734-45 98 99

UPPDRAGSNR	ANSVARIG		
P1001337	HUGO JACOBSSON		
DATUM	RITAD/KONSTR AV	HANDLÄGGARE	SYSTEMBETECKNING
2025-01-27	HJ	HJ	20-2

Hus 20
SEKTIONER
HUVUDSEKTIONER

SKALA	NUMMER	REV
1 : 50	K--20-2-2000001	

ORIGINALFORMAT: A1

2025-01-24 09:51:24 F:\PROJEKT\2022\22000546 Rönnowska skolan hus V, Helsingborg\KUP1001337 Ombyggnad till matsal storkök\KM\Modell\Revit 2023\P1001337_FFU.rvt