




2025-01-24 08:53:15 F:\PROJEKT\2022\2000546 Rönnowska skolan hus V. Helsingborg\KUP\1001337 Ombyggnad till matsal storkök\Modell\Revit\2023P\1001337_FFU.rvt

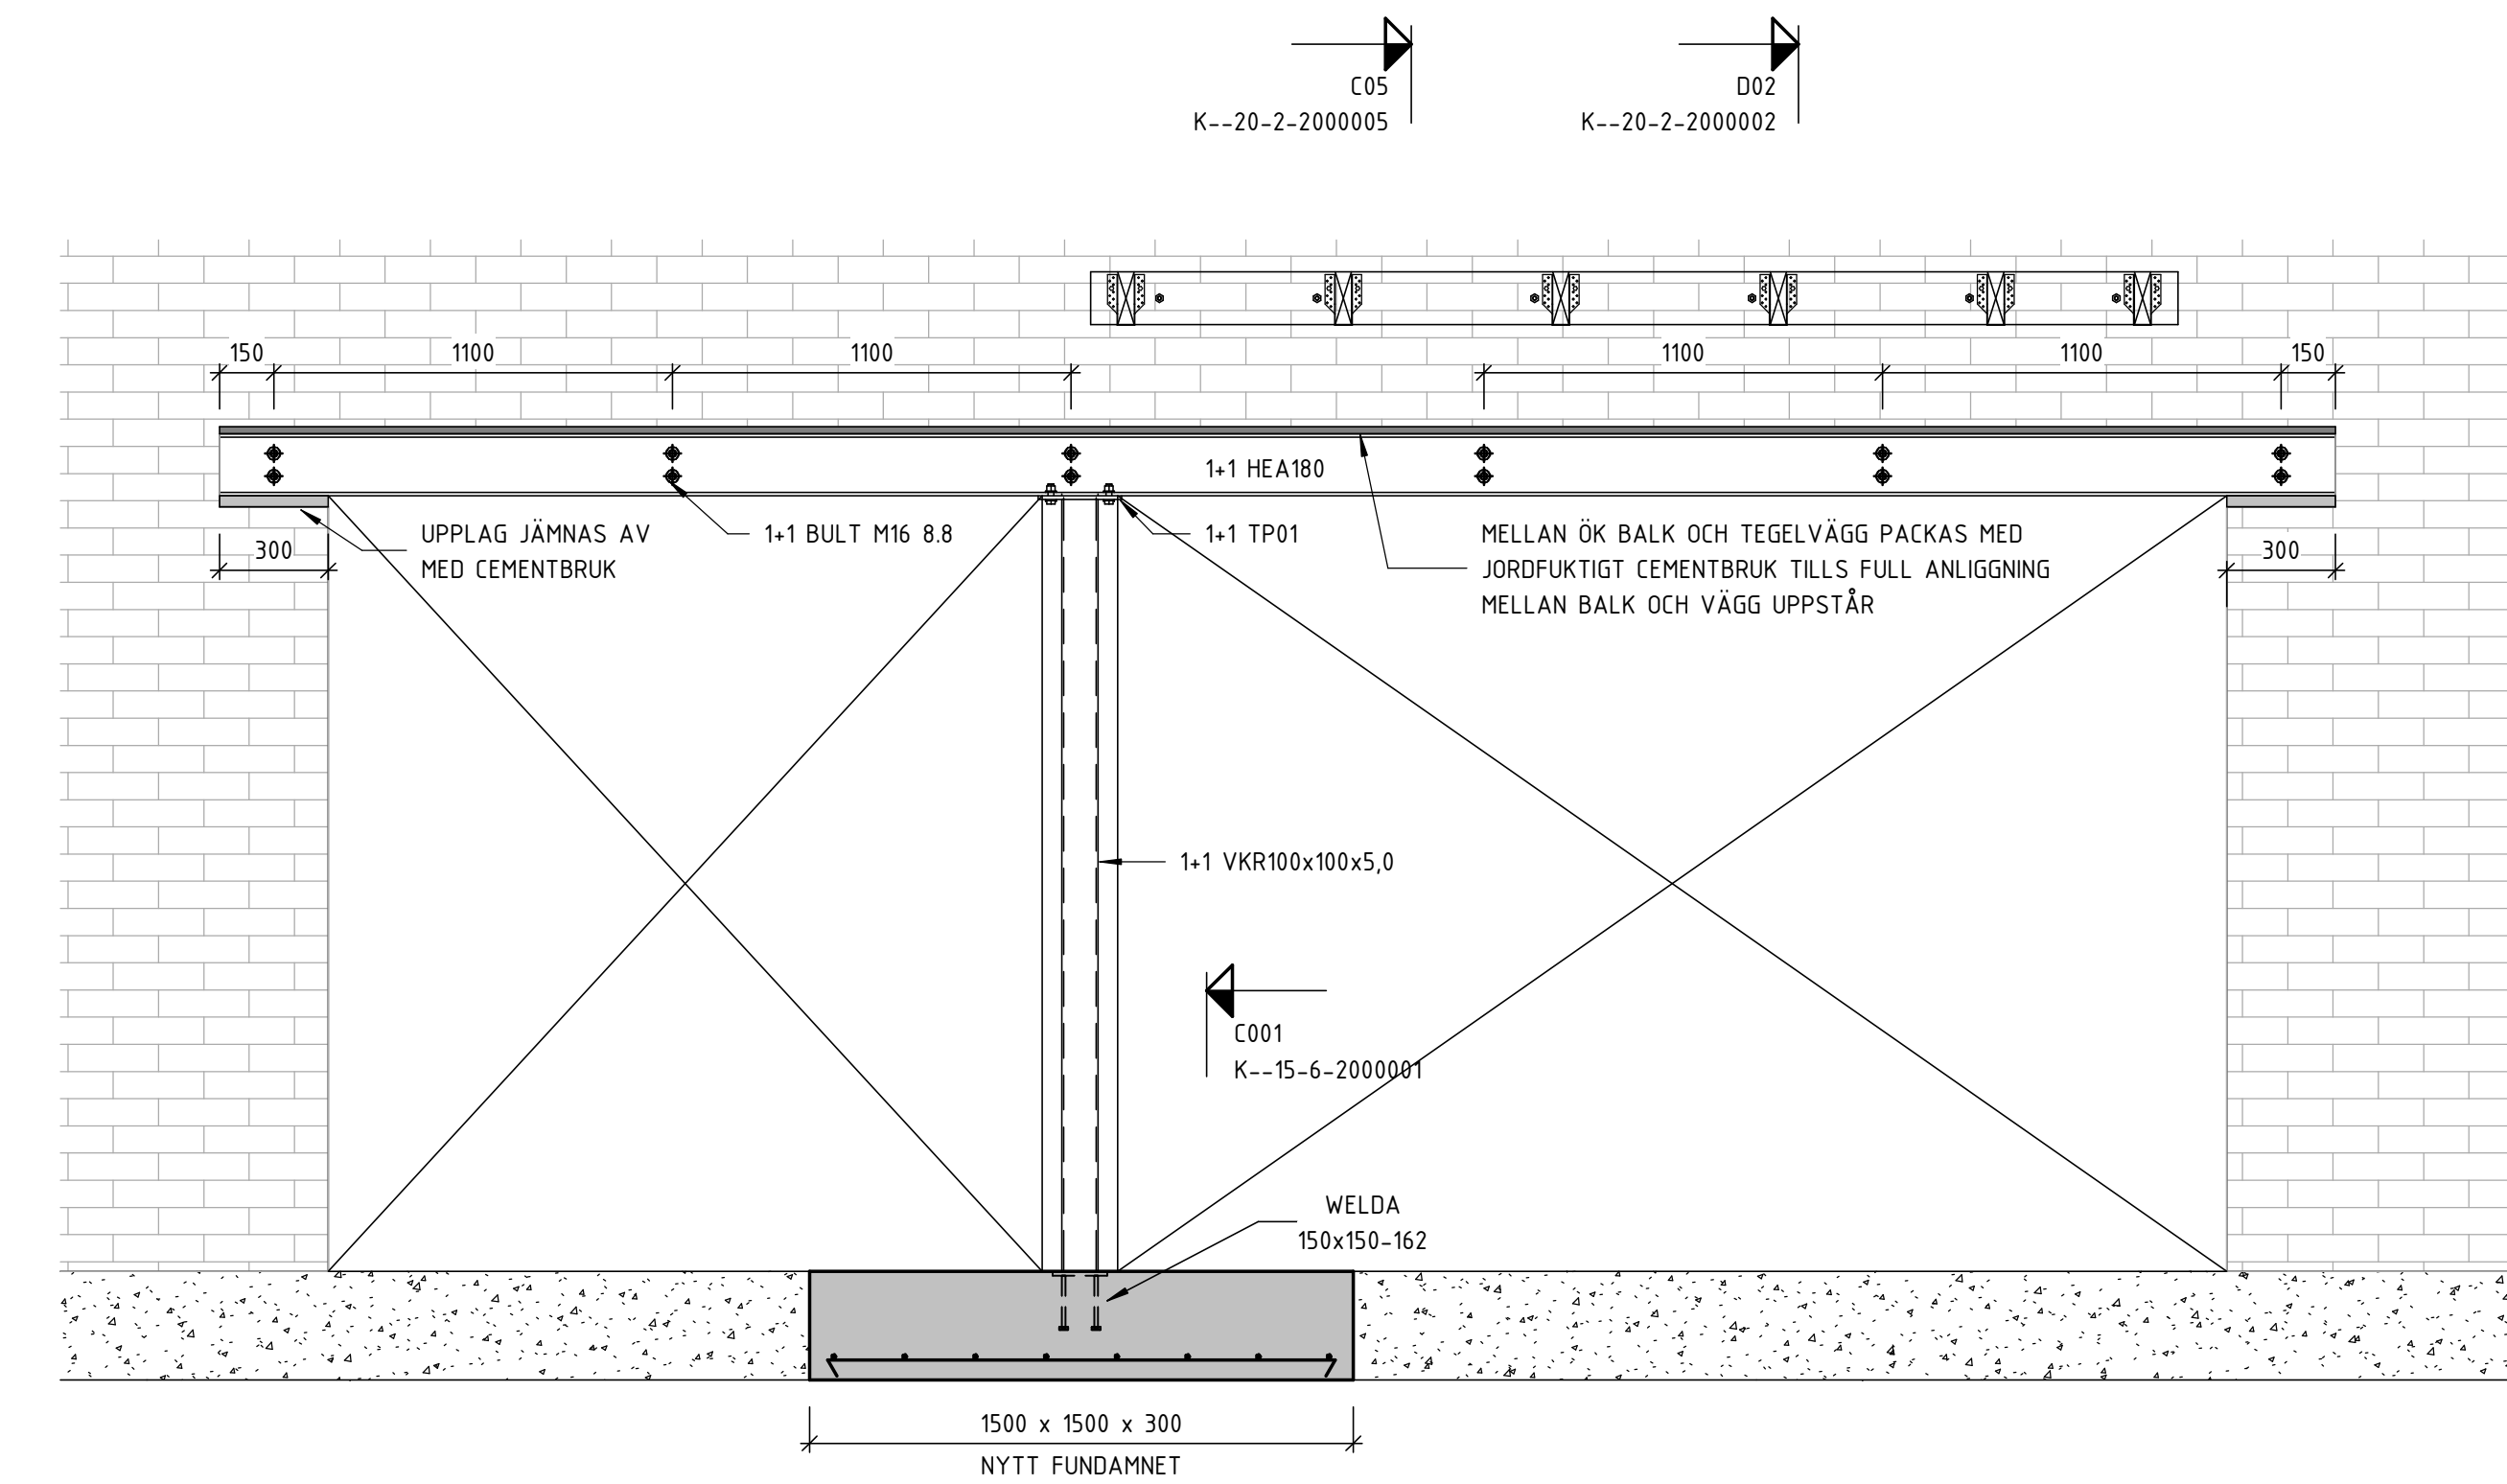


A02
1 : 20

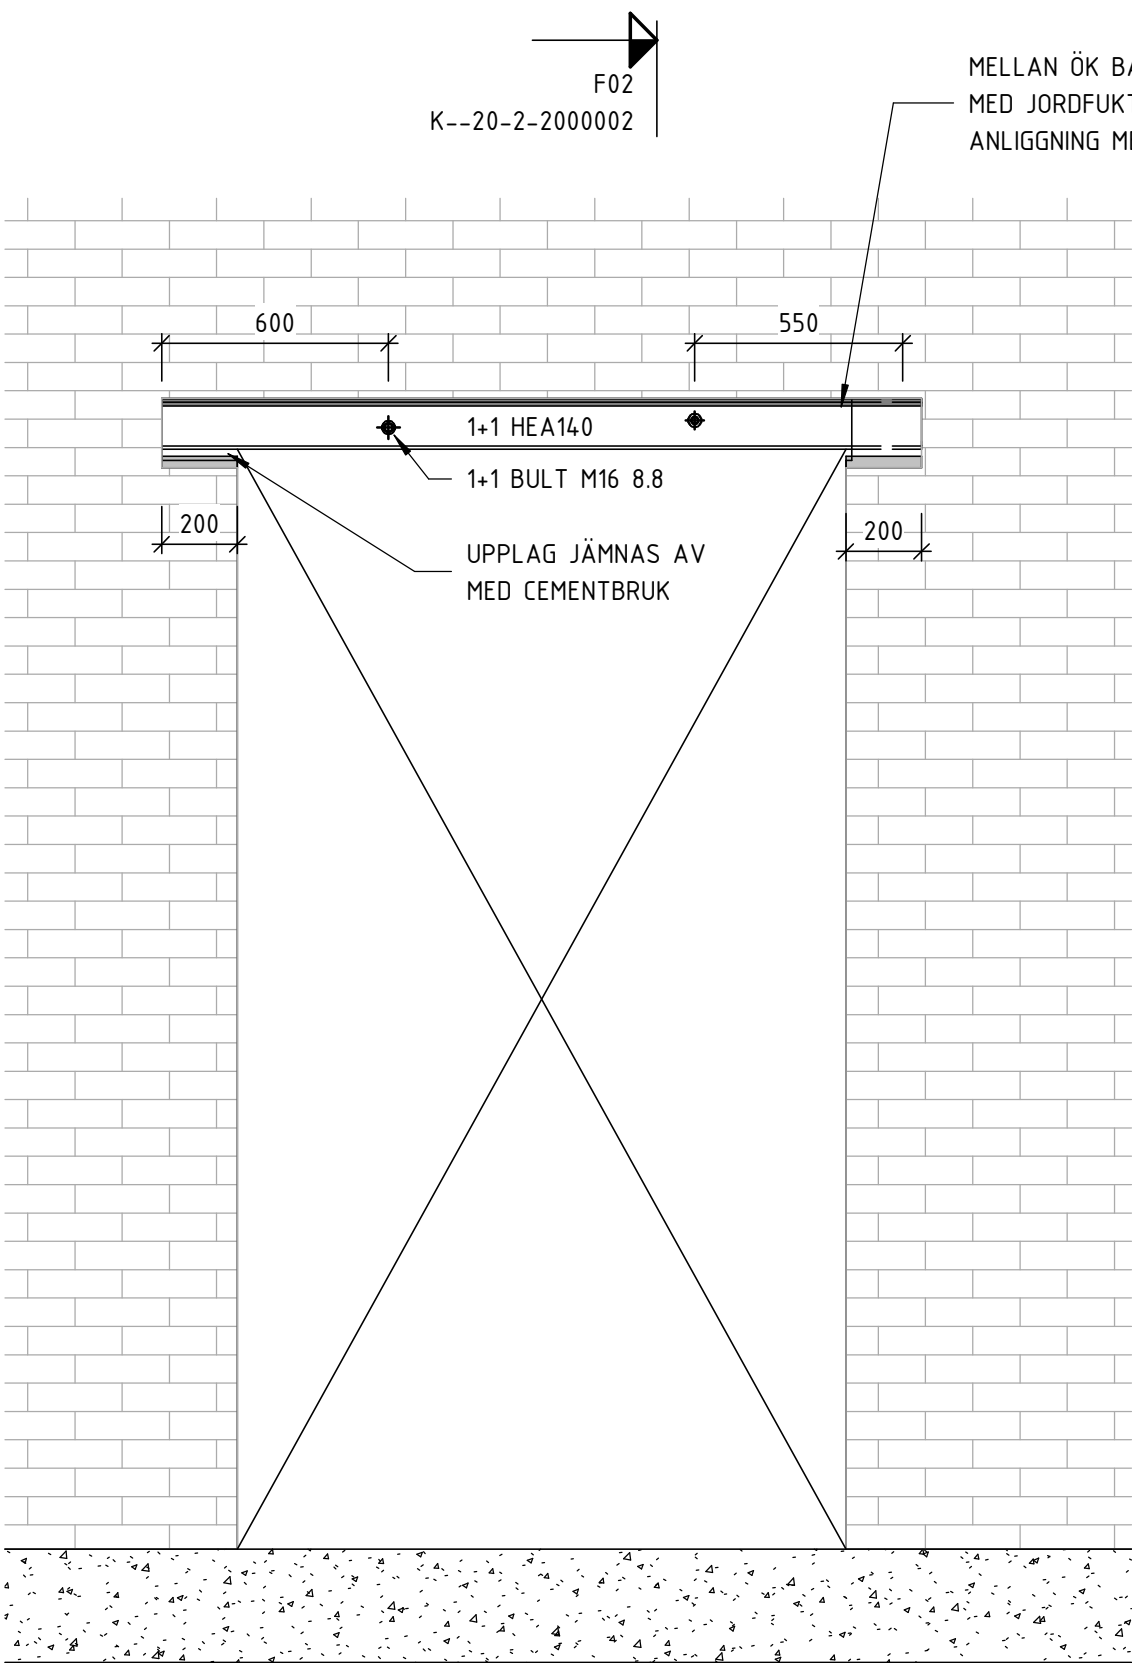


C02
1 : 20

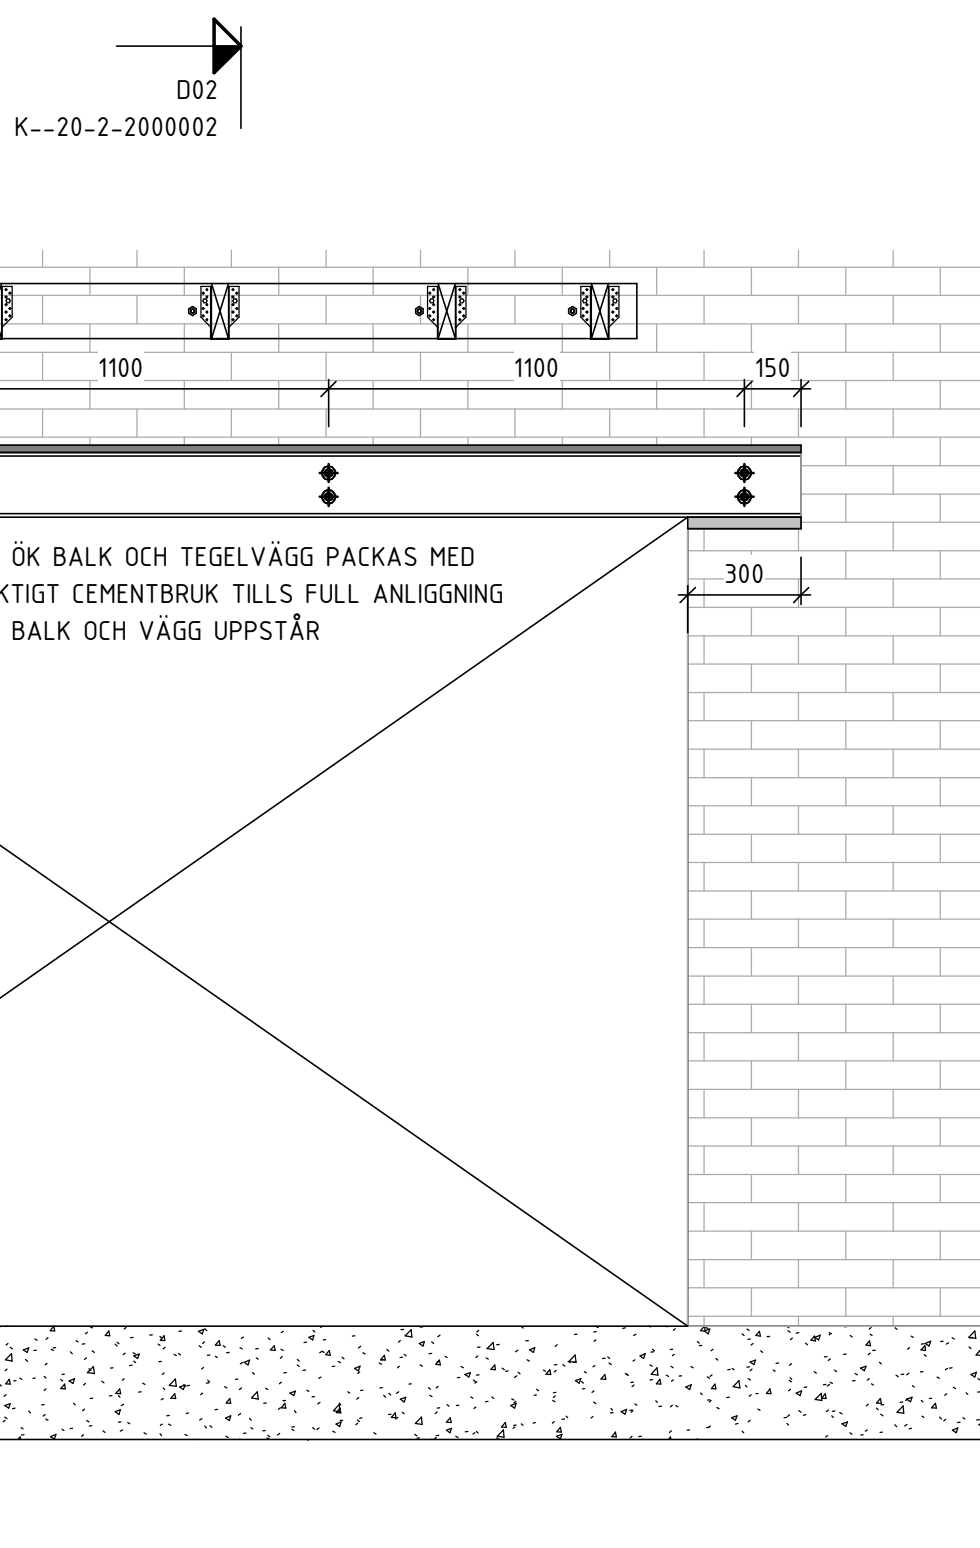


D02
1 : 10

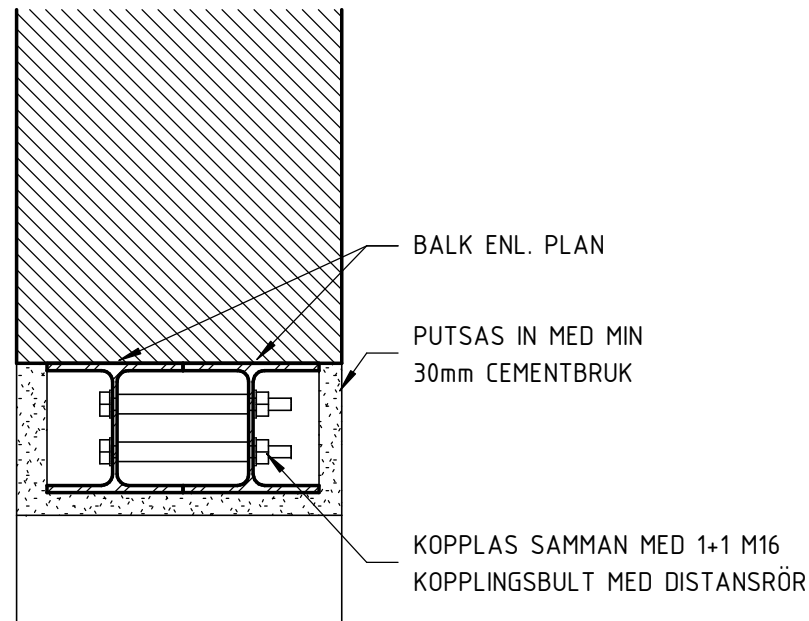


E02
1 : 10

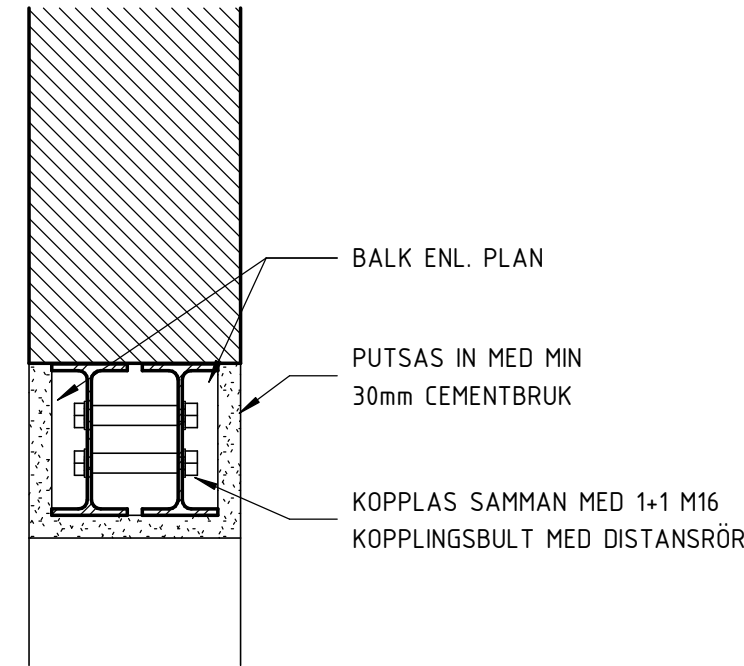



F02
1 : 10

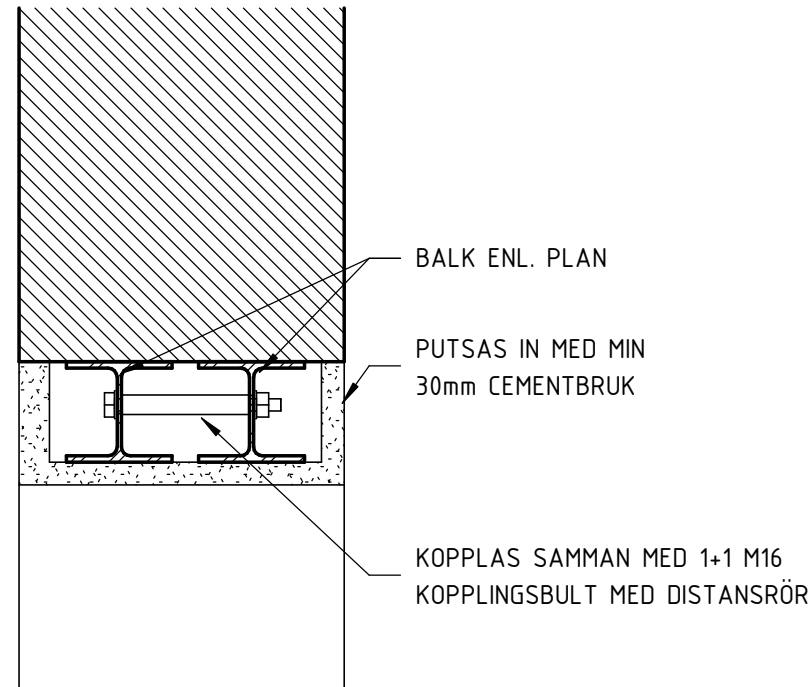

B02
1 : 20

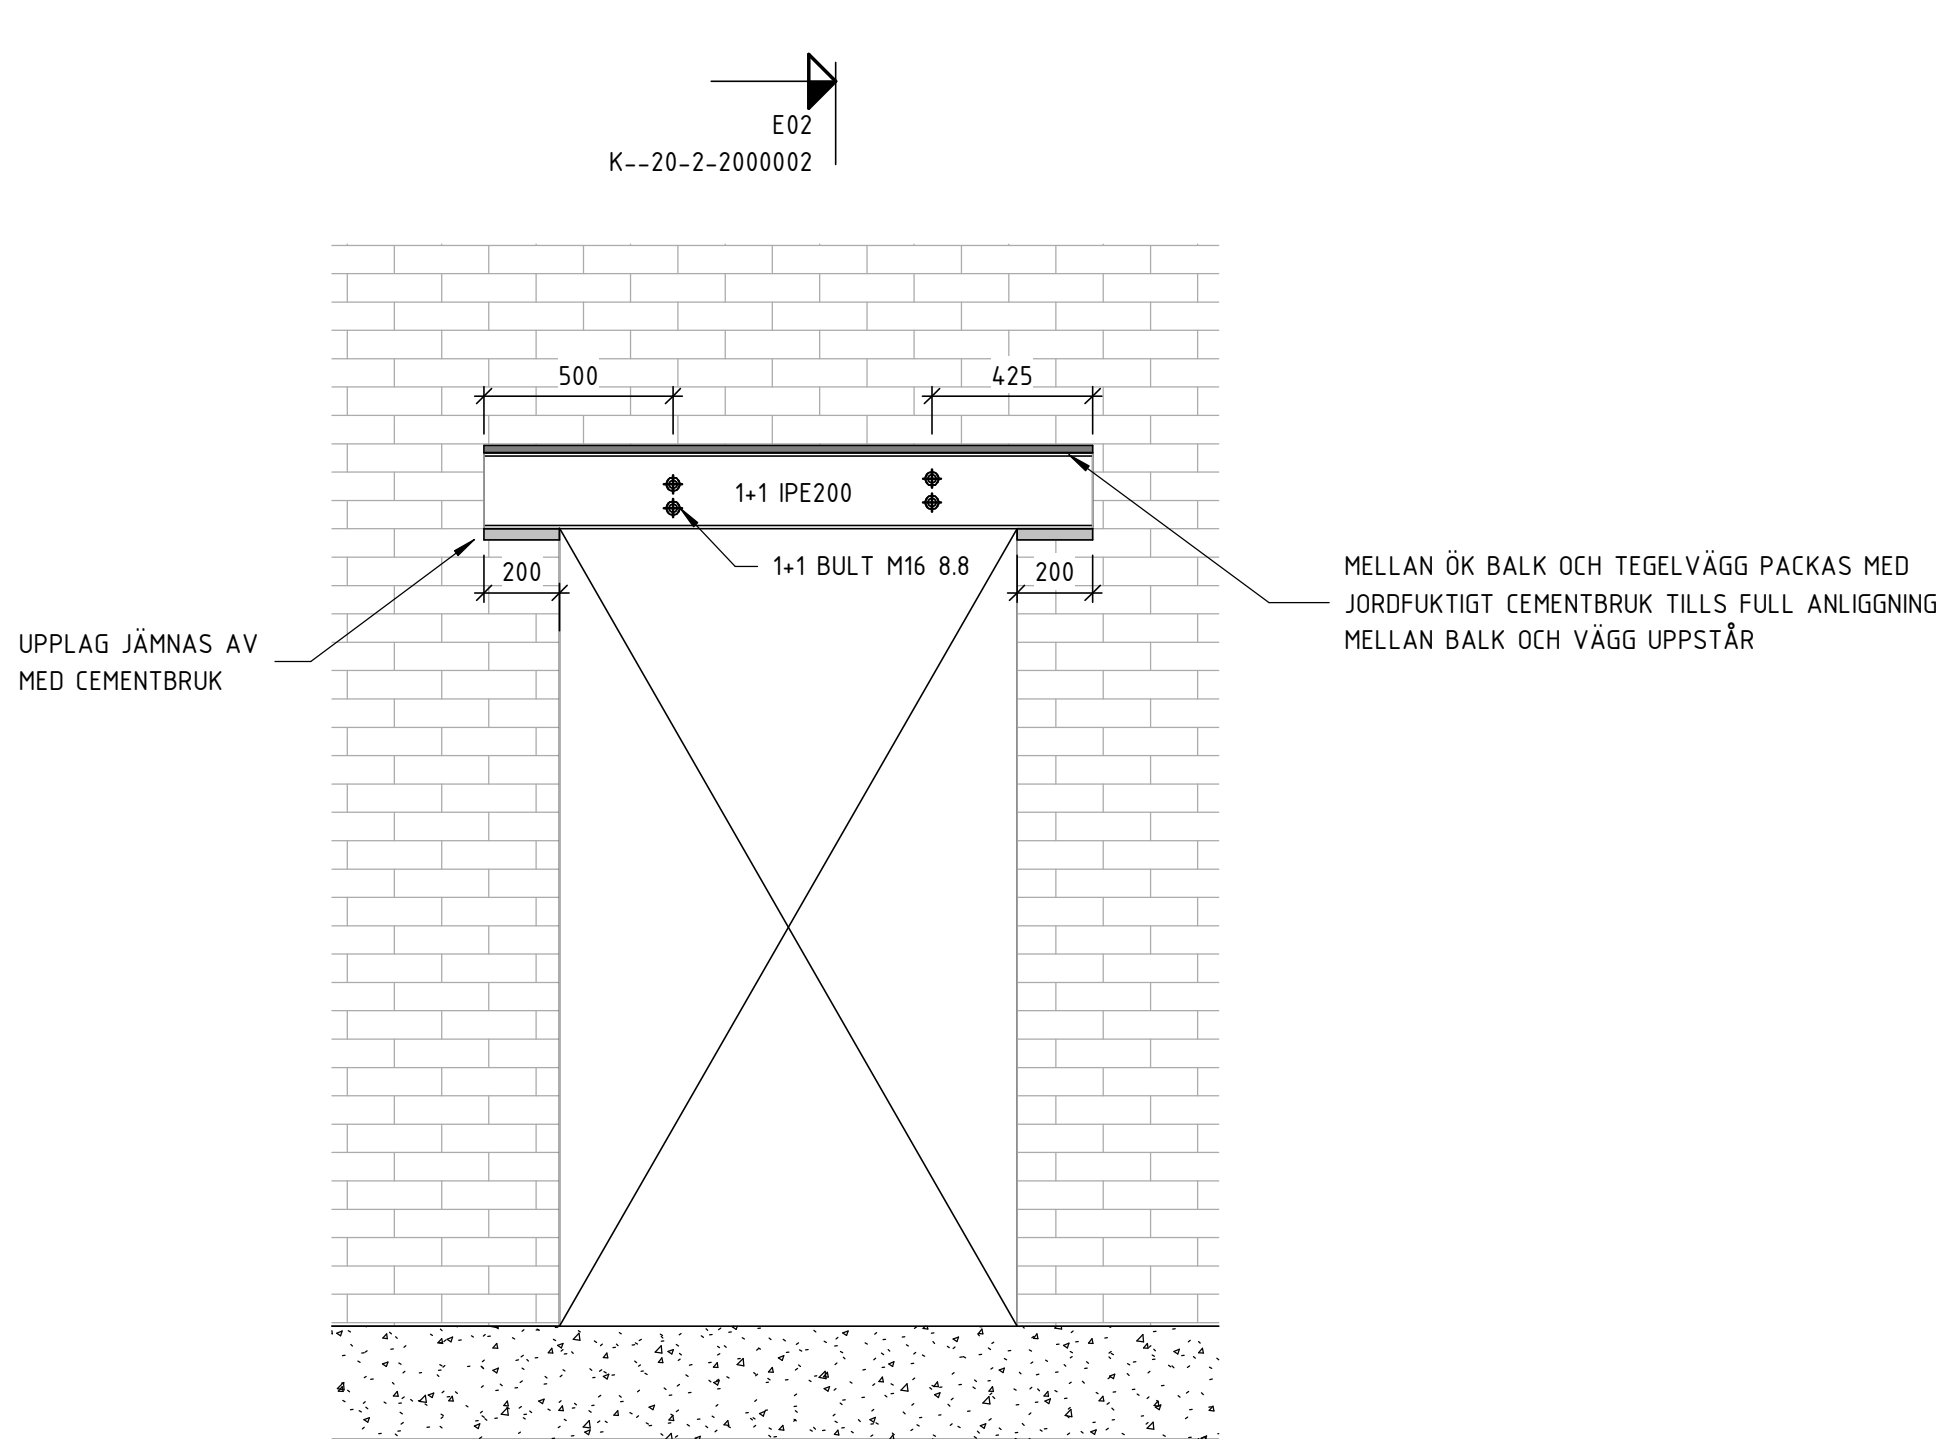

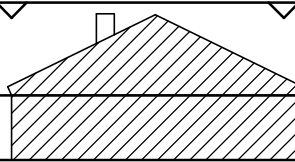BET	ÄNDRING AVSER		DATUM	SIGN
FÖRFRÅGNINGSUNDERLAG				
 HELSINGBORG FASTIGHETSFÖRVALTNINGEN				
FASTIGHET				
ORIENTEN 6				
RÖNNOWSKA SKOLAN, NYTT KÖK OCH MATSAL				
OBJEKTSNR	BYGGNADS-ID		PROJEKTSNR	
1457	5-266088		60095	
BYGGNAD				
1457-20 - HUS V (BYGGNAD 449)				
ORIENTERINGSFIGUR				
PLAN 03				
02 01 				
DEL				
111 112 113 				
VÄSTRA SANDGATAN				
A	ARKITEKTLAGET SKÅNE AB		T: 042-19 96 00	
BR	FIRETECH ENGINEERING EMRON AB		T: 042-400 02 20	
E	DEVELCON AB		T: 079-020 27 02	
K	ÅKERMANS INGENJÖRSBYRÅ AB		T: 042-12 00 10	
M	TYRÉNS SVERIGE AB		T: 010-452 20 00	
S	SWECO SVERIGE AB		T: 08-695 60 00	
SK	STORKÖKSVISION AB		T: 040-744 29	
V	SWECO SVERIGE AB		T: 08-695 60 00	
W	SWECO SVERIGE AB		T: 08-695 60 00	
C	ZYNKA BIM AB		T: 0734-45 98 99	
UPPDRAGSNR		ANSVARIG		
P1001337		HUGO JACOBSSON		
DATUM		RITAD/KONSTR AV	HANDLÄGGARE	SYSTEMBETECKNING
2025-01-27		HJ	HJ	20-2
Hus 20				
SEKTIONER				
AVVÄXLINGAR				
SKALA		NUMMER		REV
As		K--20-2-2000002		

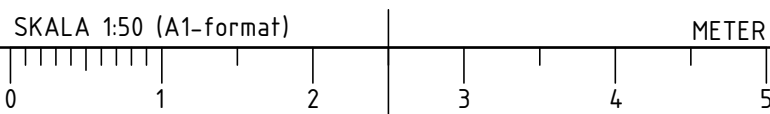

ORIENTEN 6