




2025-01-24 08:53:41 F:\PROJEKT\2022\20200546 Rönnowska skolan Hus V, Helsingborg\KUP\1001337 Ombyggnad till matsal storkök\Modell\Revit\2023\1001337_FFU.rvt

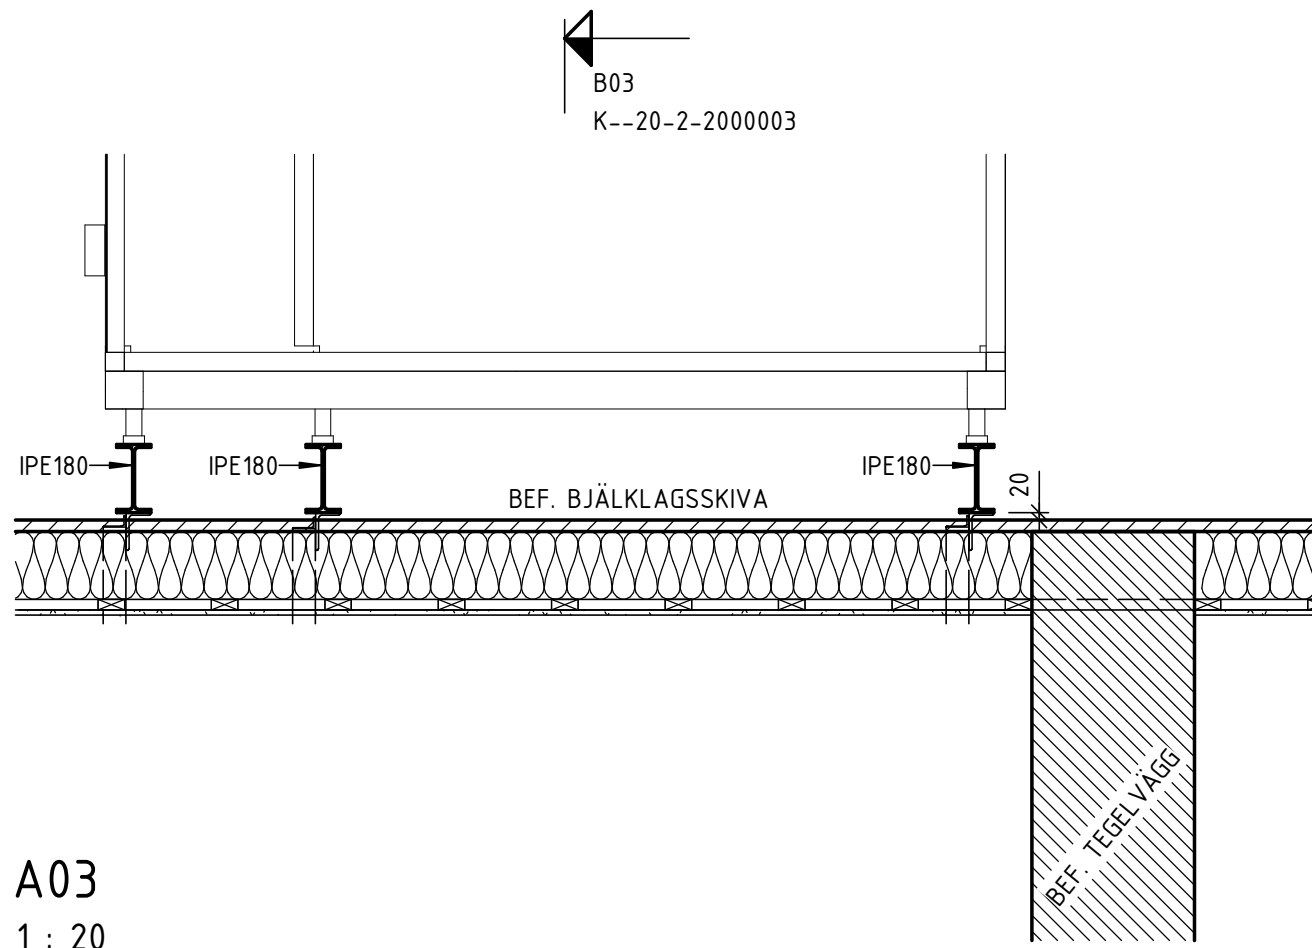


A03
1 : 20

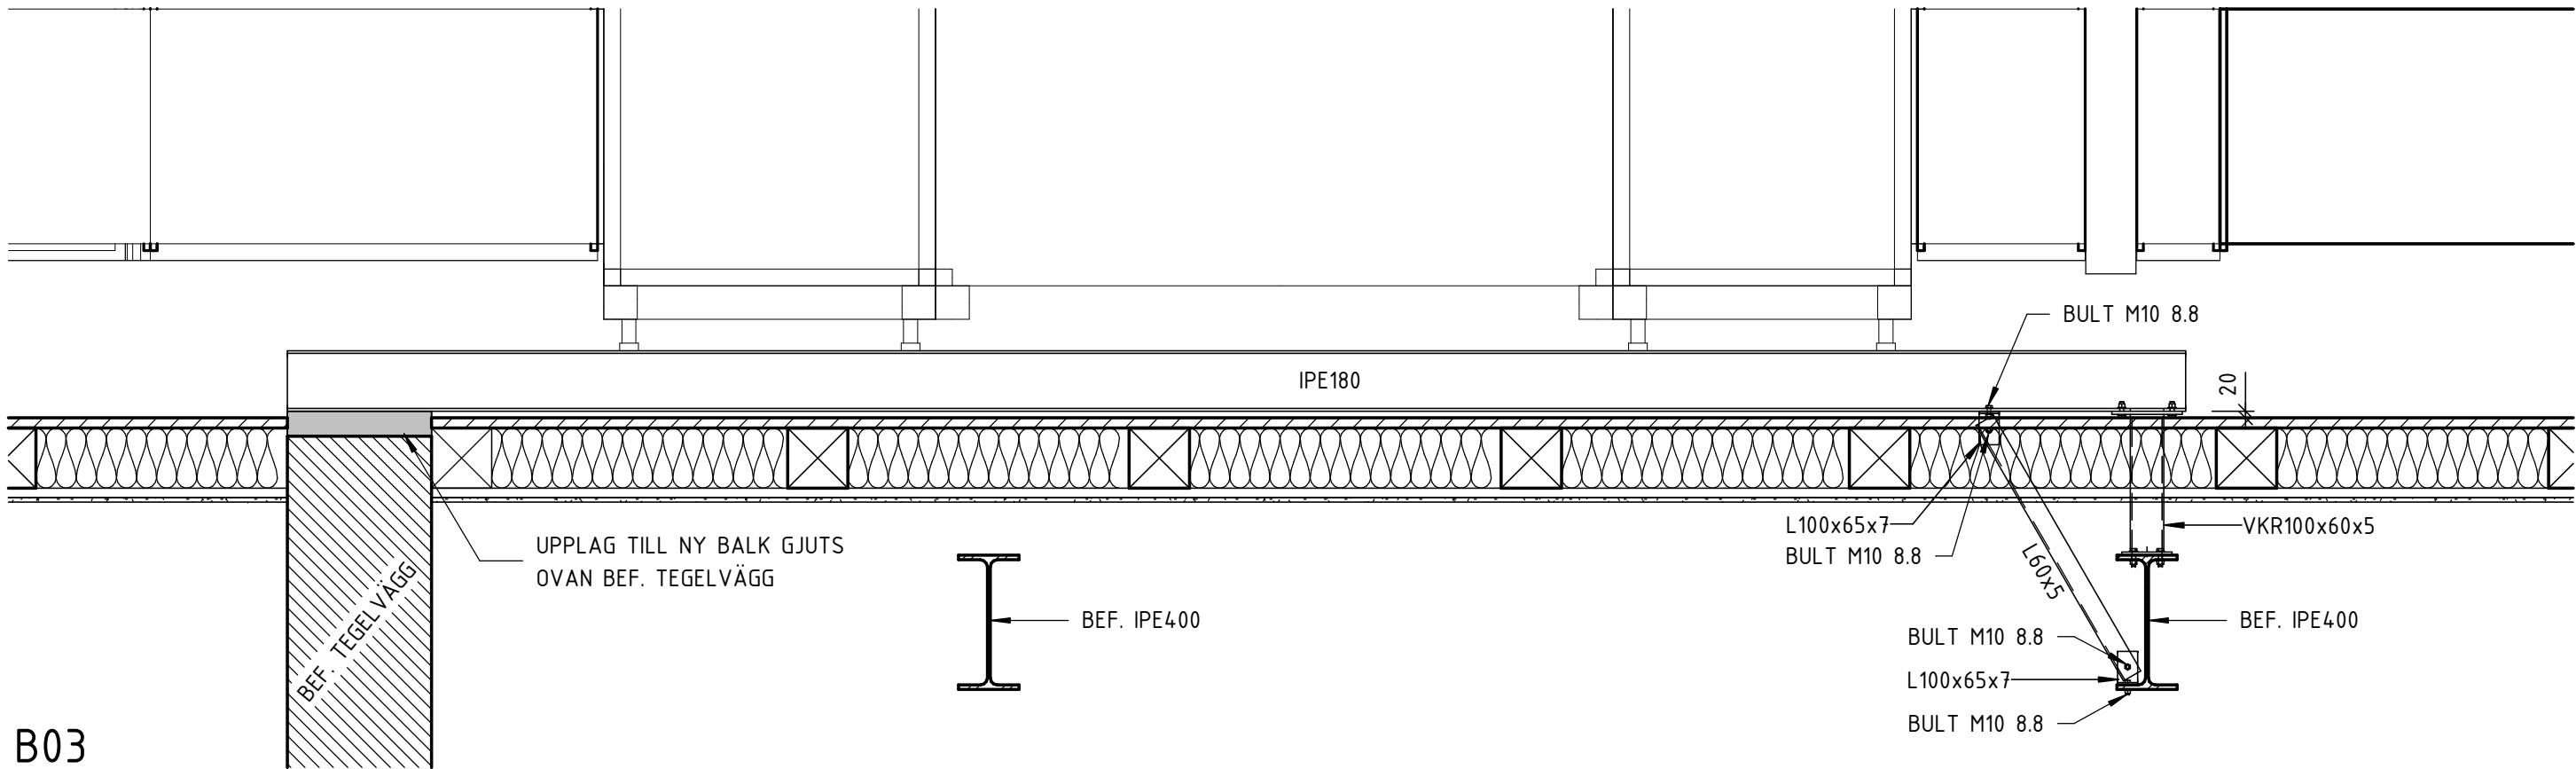


B03
1 : 20

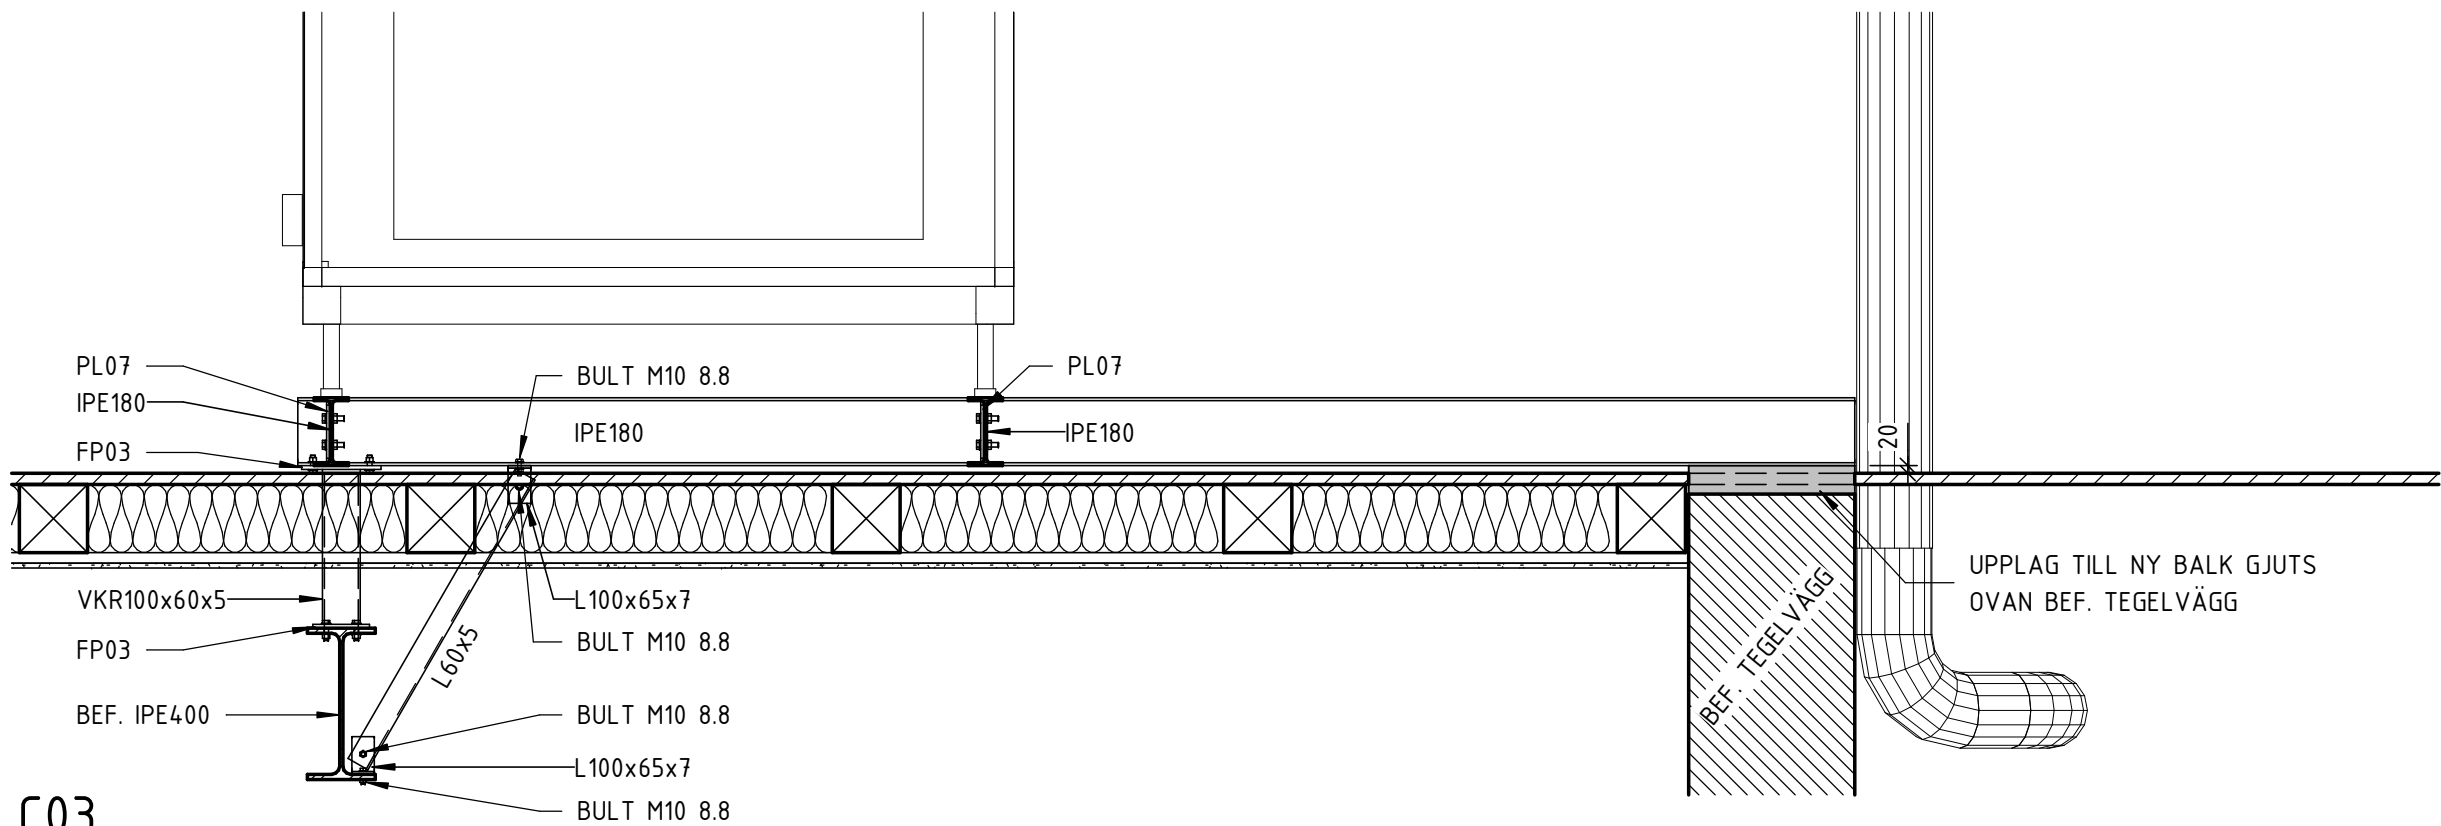


C03
1 : 20

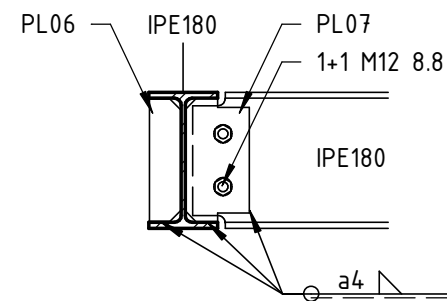


BALK-BALKKOPPLING
1 : 10

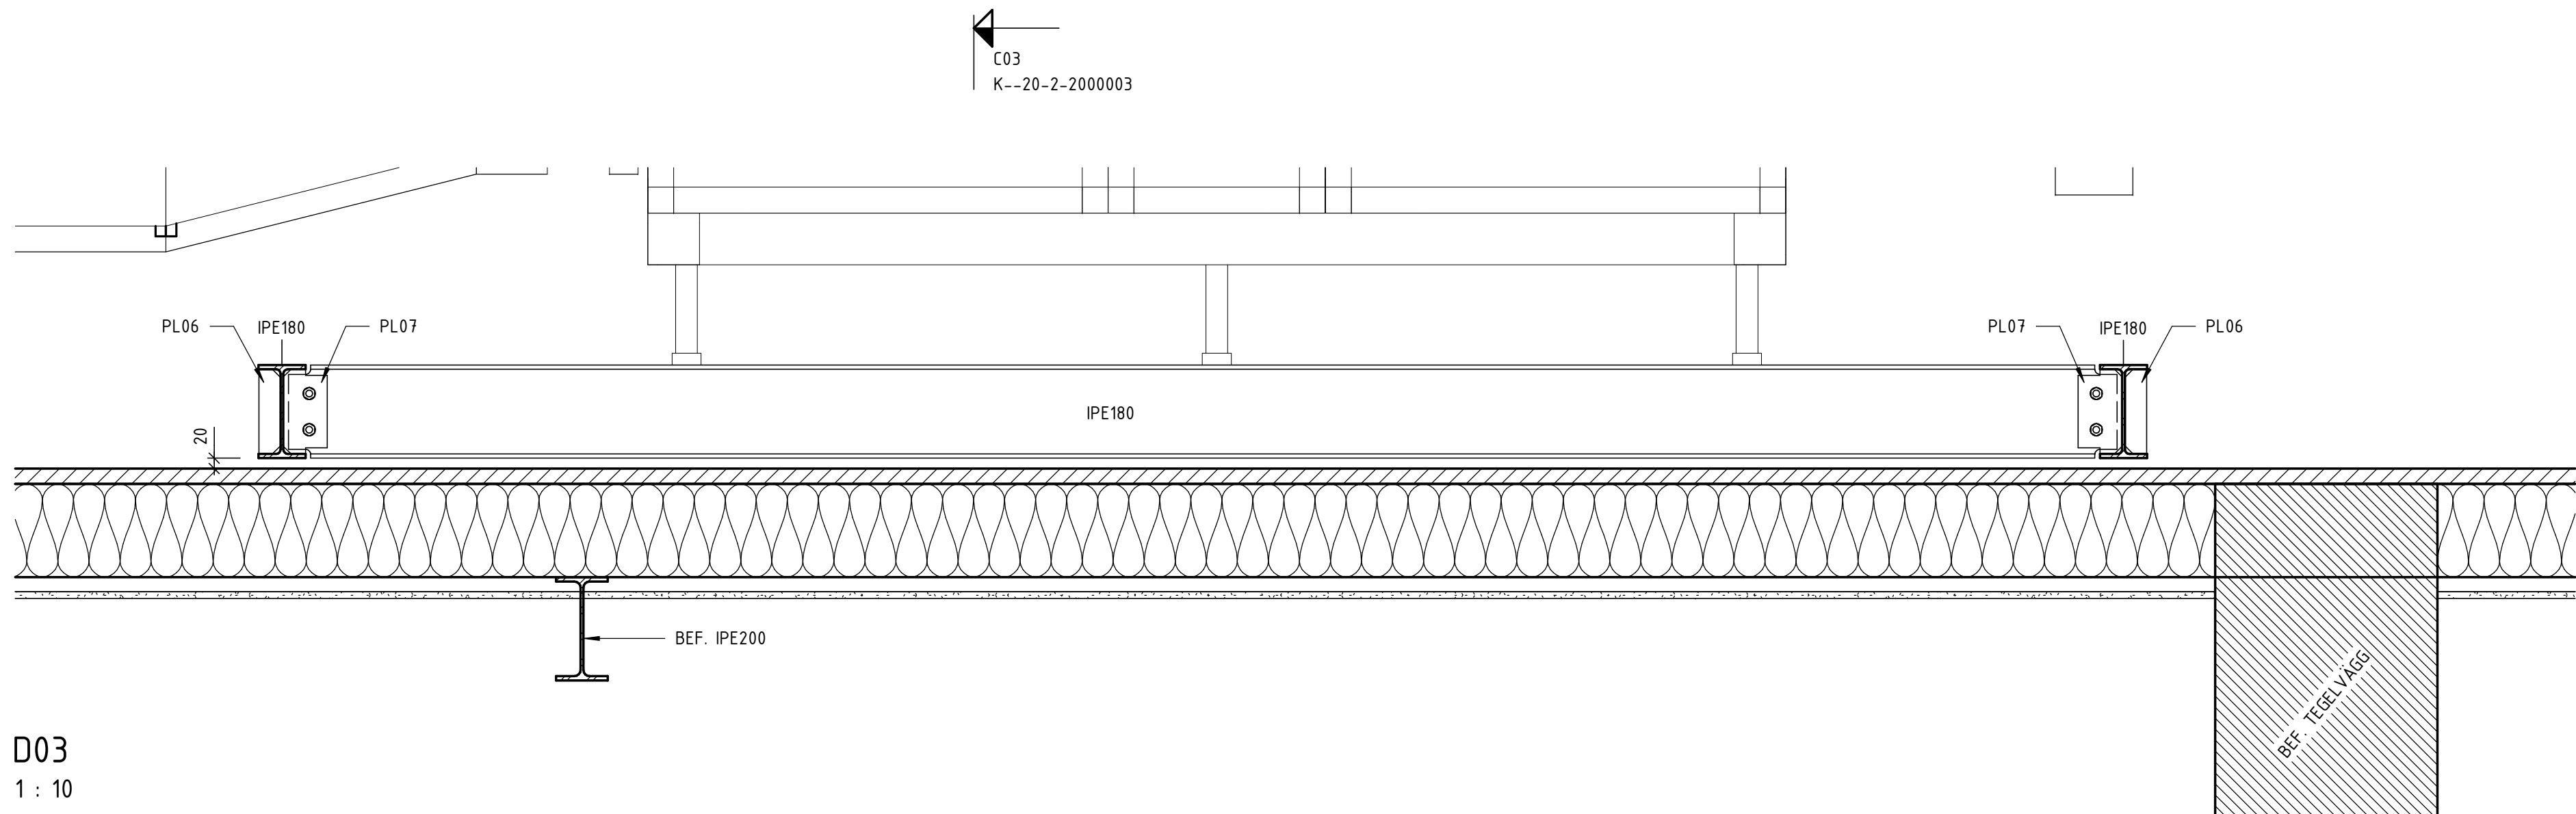

D03
1 : 10

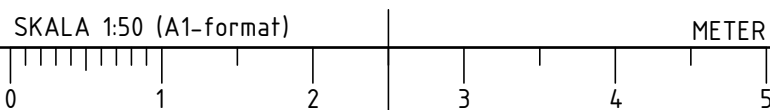

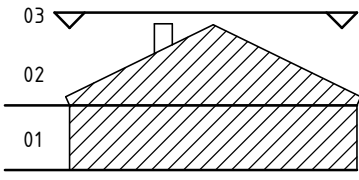BET	ÄNDRING AVSEER	DATUM	SIGN
FÖRFRÅGNINGSUNDERLAG			
 HELSINGBORG FASTIGHETSFÖRVALTNINGEN			
FASTIGHET ORIENTEN 6 RÖNNOWSKA SKOLAN, NYTT KÖK OCH MATSAL			
OBJEKTSNR 1457	BYGGNADS-ID 5-266088	PROJEKTNR 60095	
BYGGNAD 1457-20 - HUS V (BYGGNAD 449)			
ORIENTERINGSGRUPP PLAN 03			
			
DEL			
111	112	113	
VÄSTRA SANDGATAN			
A ARKITEKTLAGET SKÅNE AB T: 042-19 96 00			
BR FIRETECH ENGINEERING EMRON AB T: 042-400 02 20			
E DEVELCON AB T: 079-020 27 02			
K ÅKERMANS INGENJÖRSBYRÅ AB T: 042-12 00 10			
M TYRÉNS SVERIGE AB T: 010-452 20 00			
S SWECO SVERIGE AB T: 08-695 60 00			
SK STÖRKÖKSVISION AB T: 040-744 29			
V SWECO SVERIGE AB T: 08-695 60 00			
W SWECO SVERIGE AB T: 08-695 60 00			
C ZYNKA BIM AB T: 0734-45 98 99			
UPPDRAGSNR P1001337	ANSVARIG HUGO JACOBSSON		
DATUM 2025-01-27	RITAD/KONSTR AV HJ	HANDLÄGGARE HJ	SYSTEMBETECKNING 20-2
Hus 20 SEKTIONER STALAGE TILL AGGREGAT			
SKALA As	NUMMER K--20-2-2000003	REV	

ORIENTERINGSGRUPP