

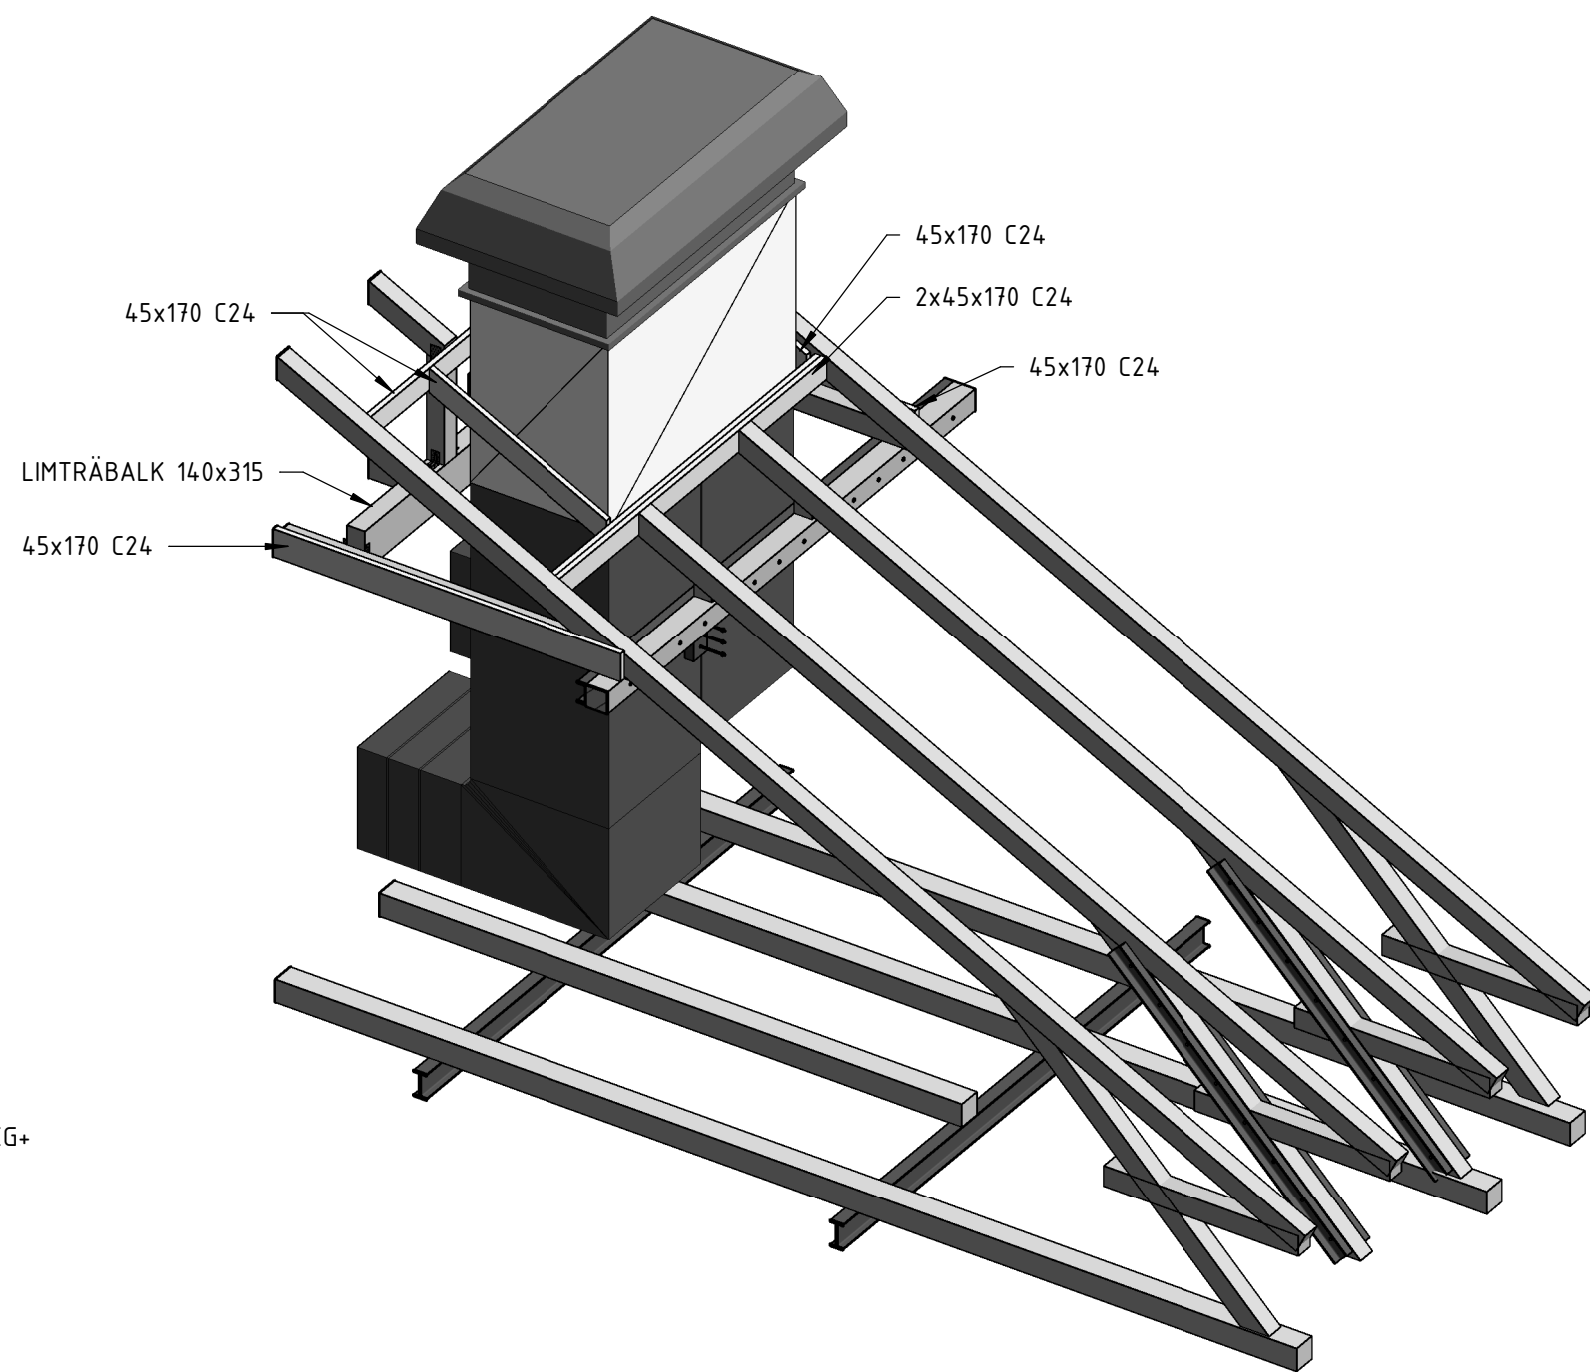
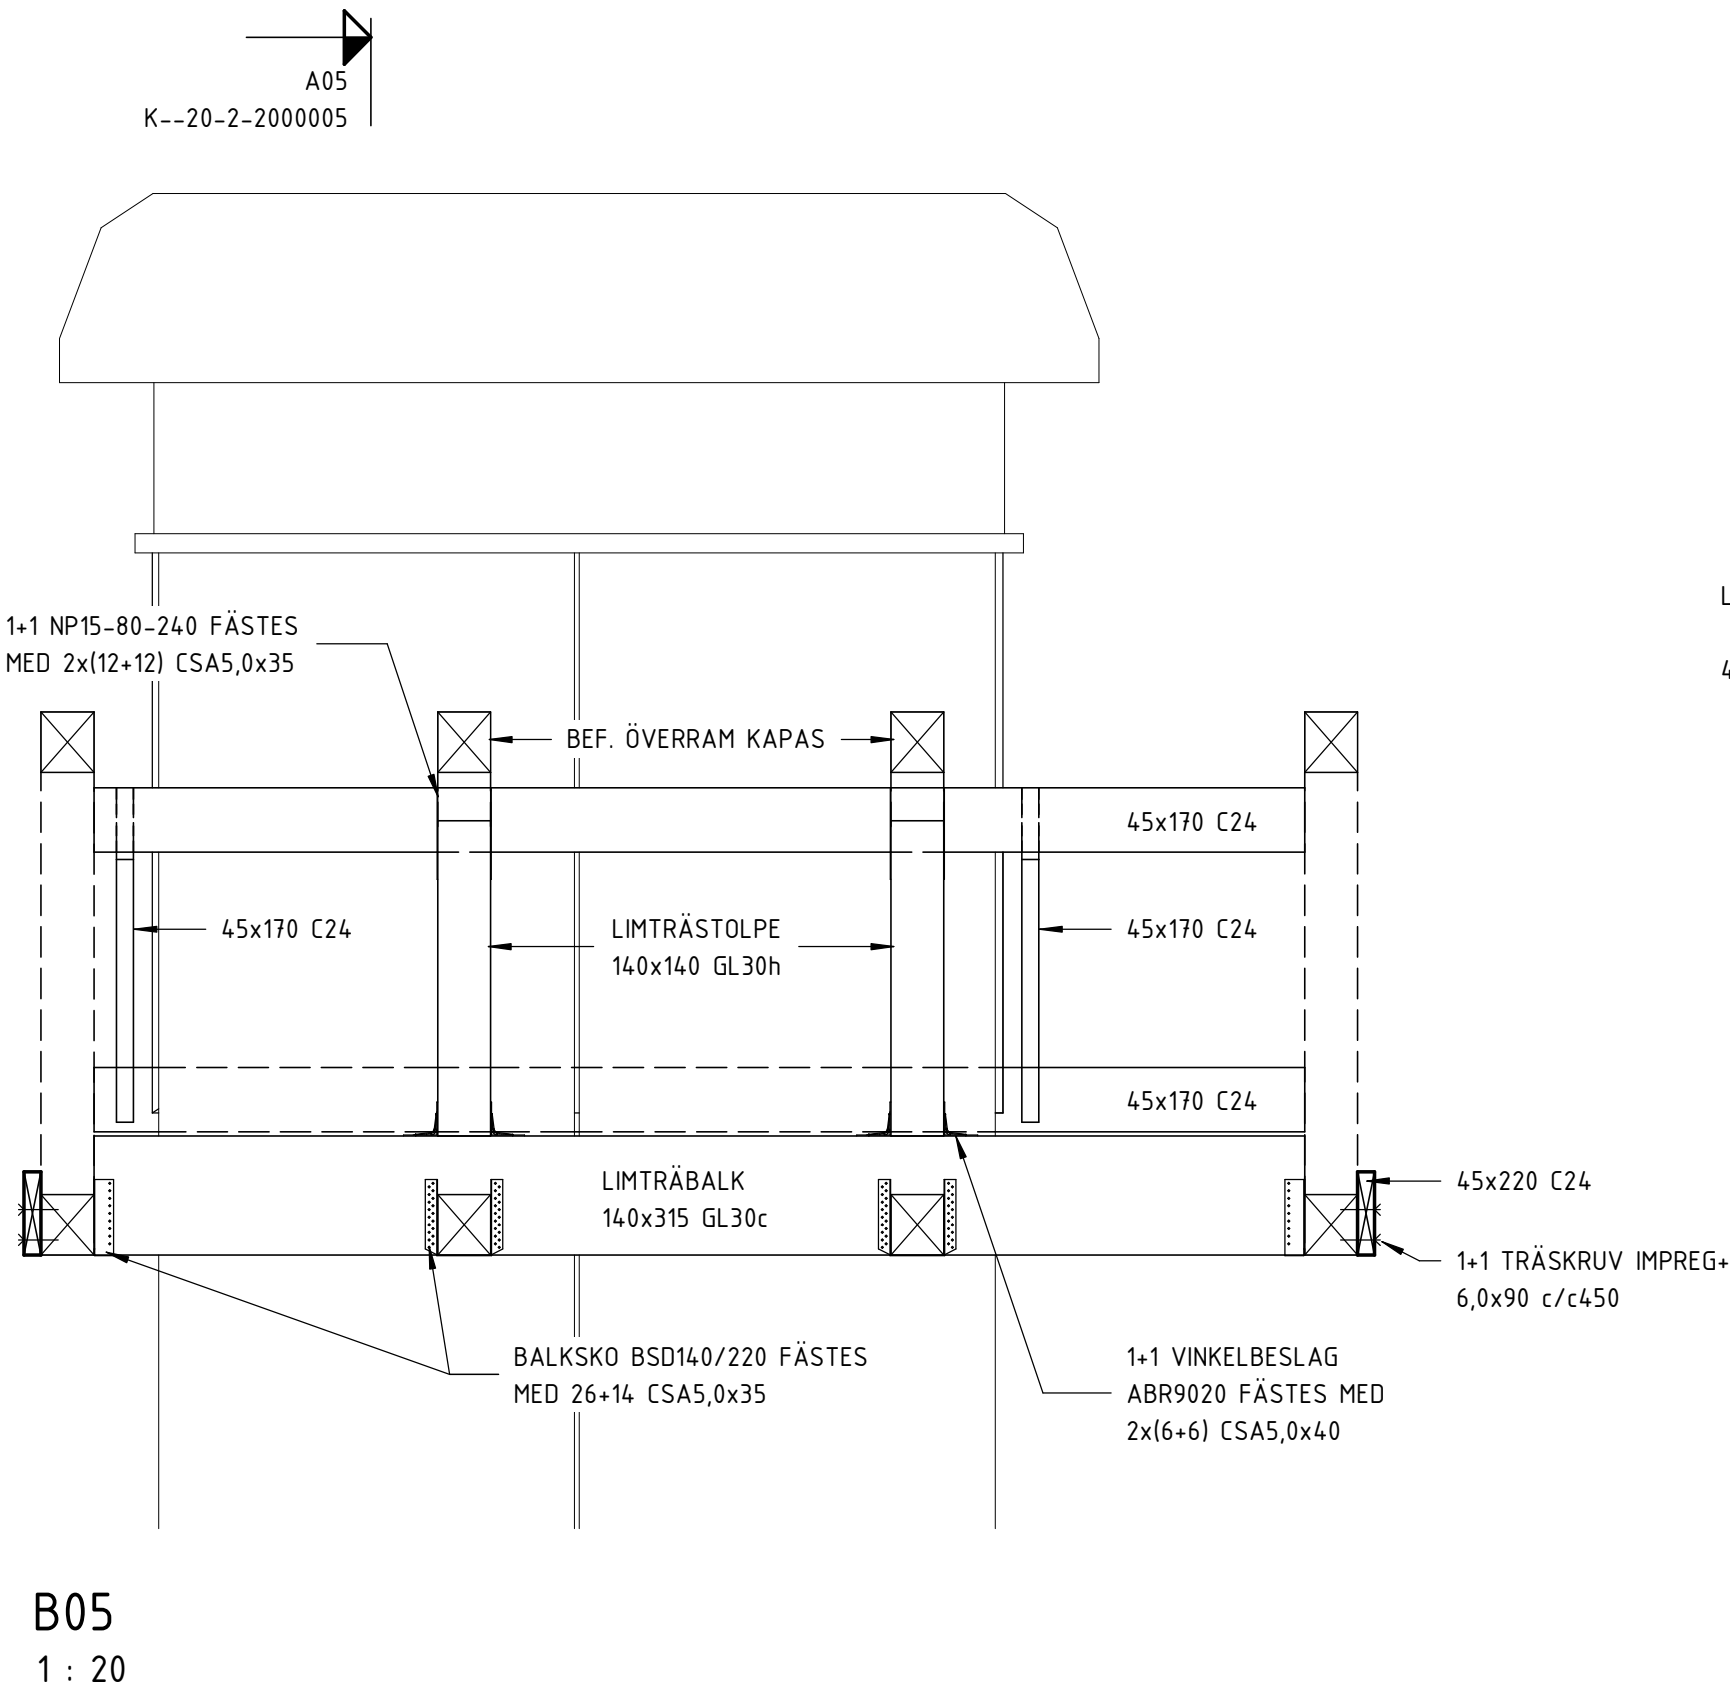
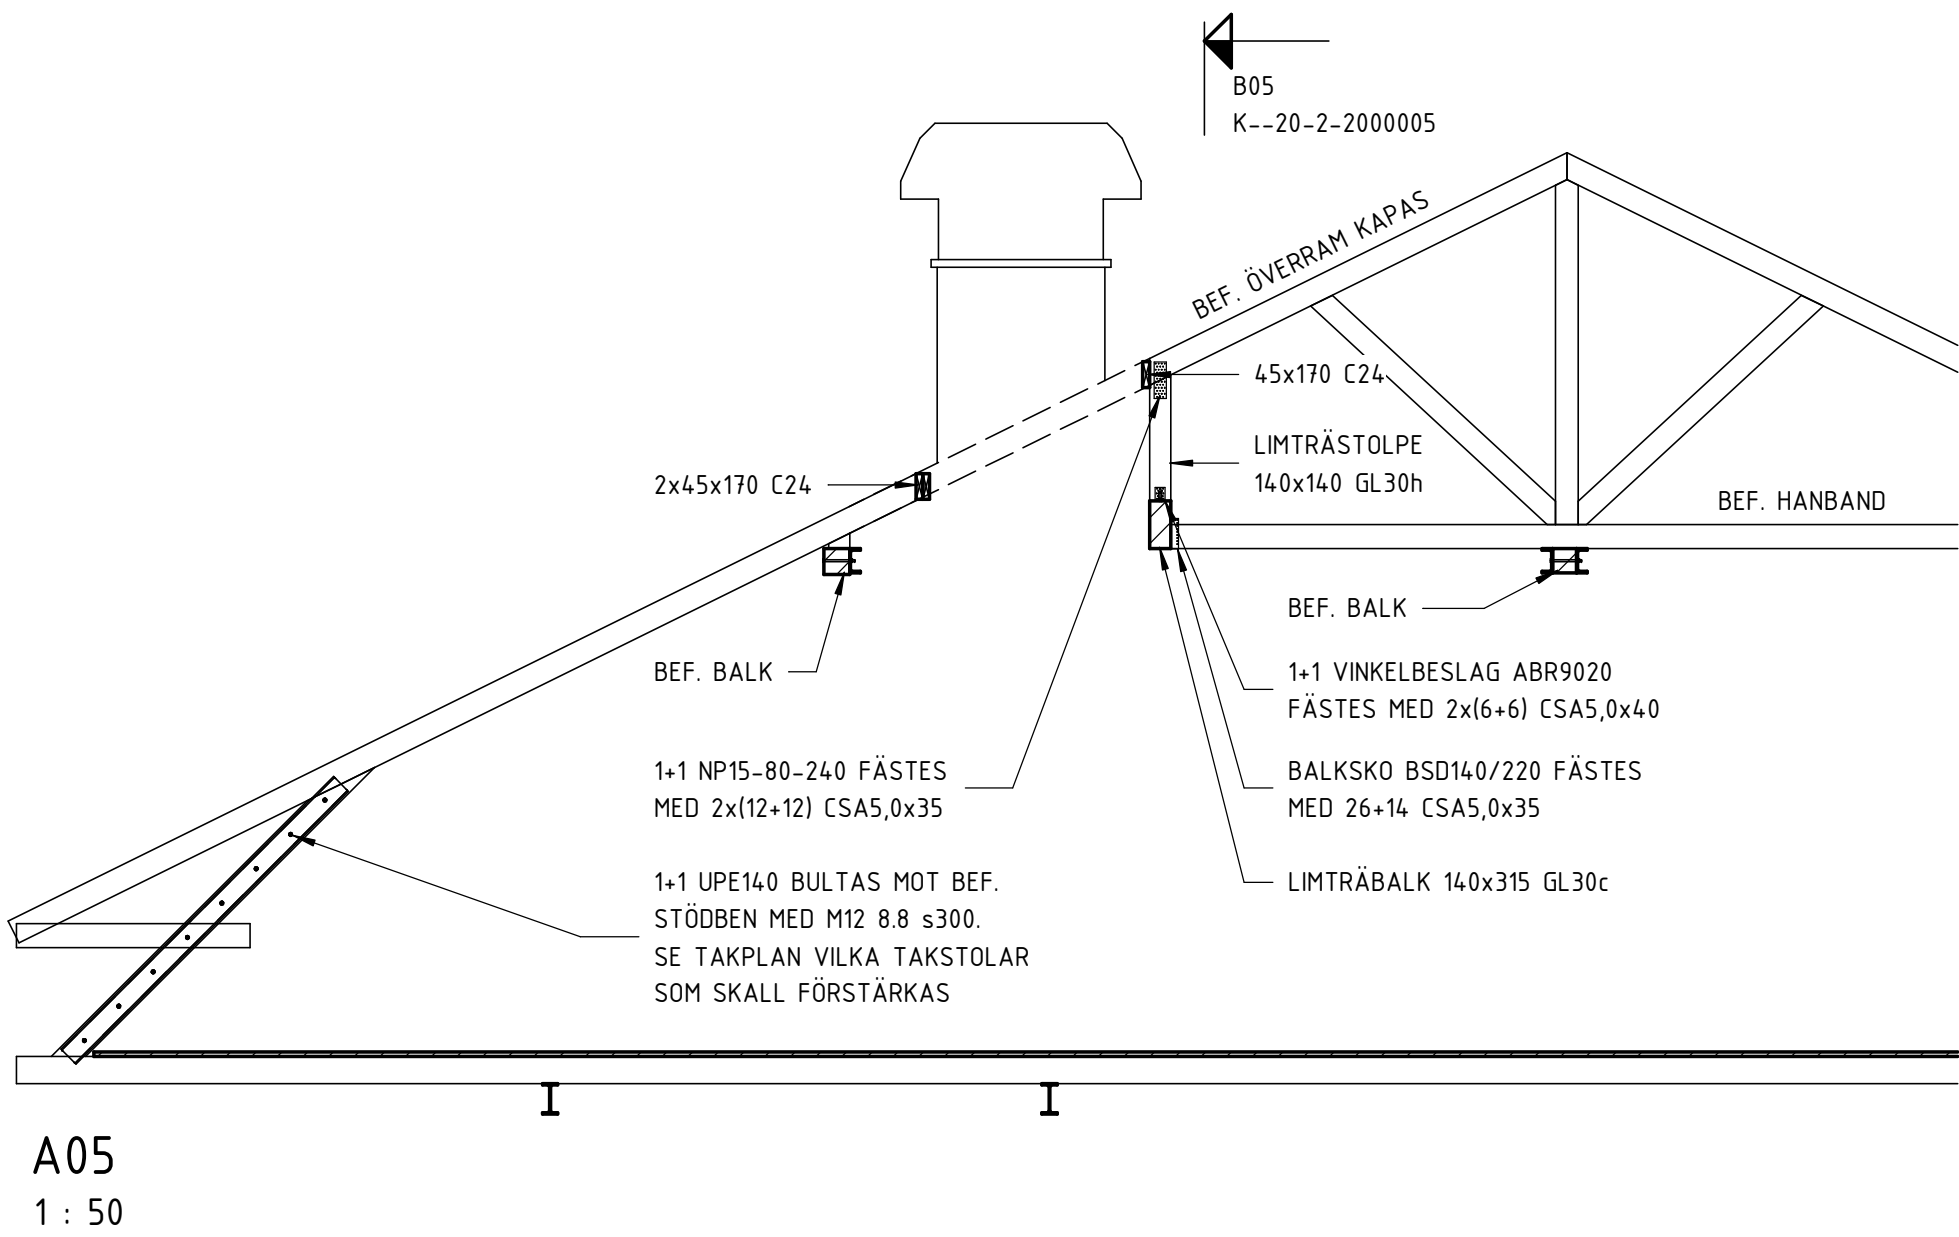
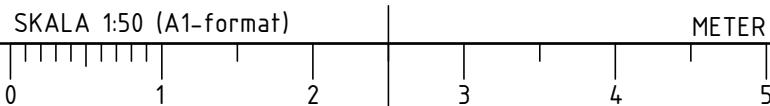
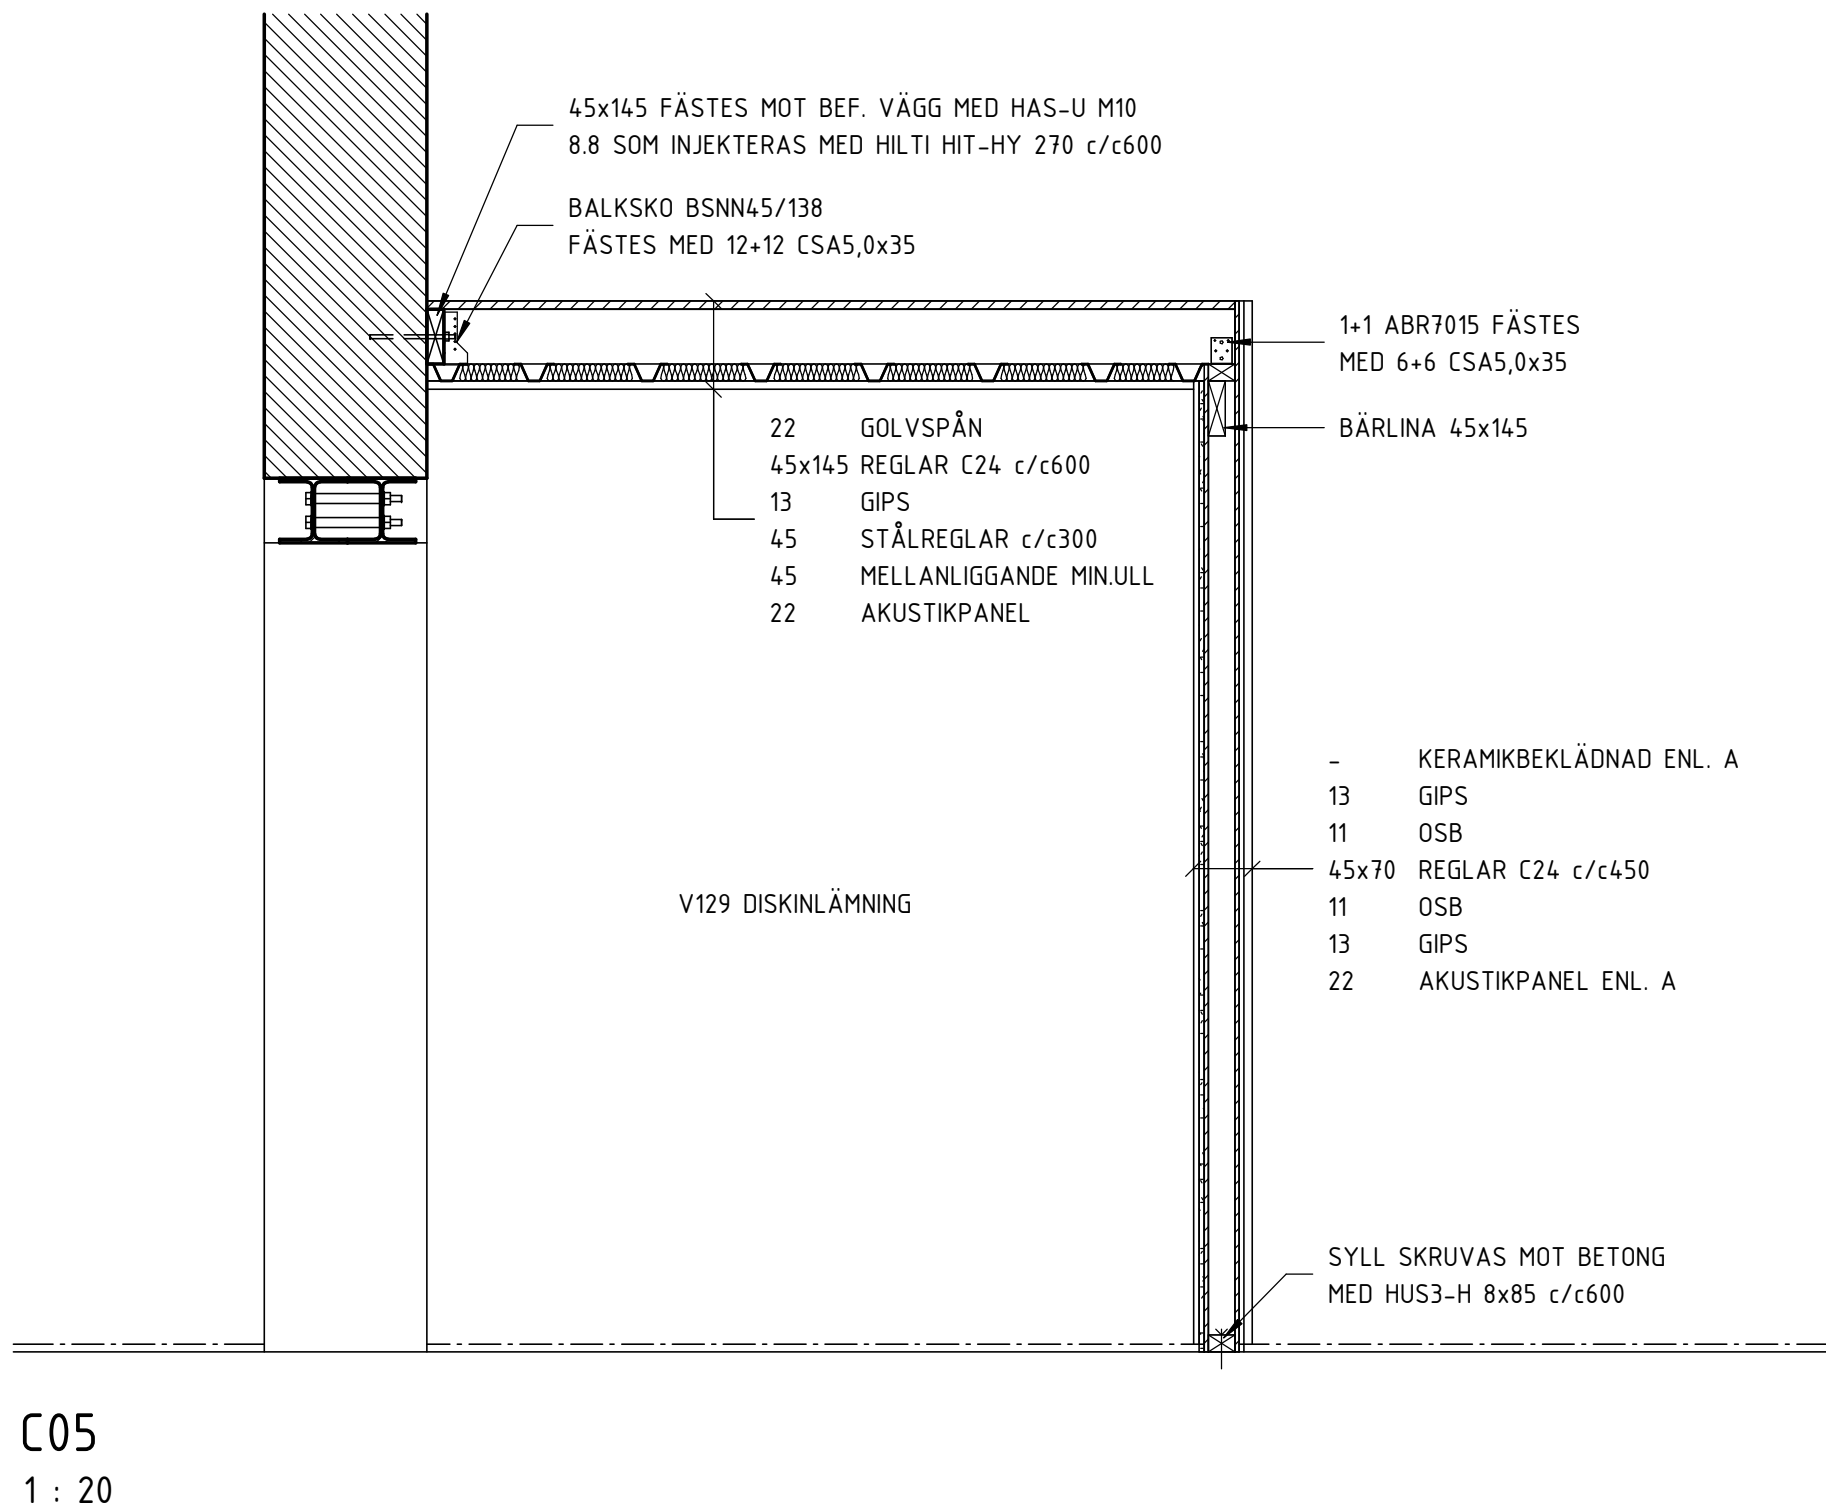


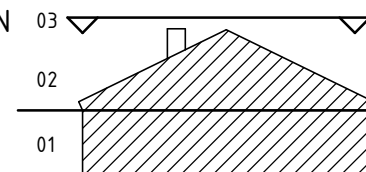

3D-VY - VENTHUV

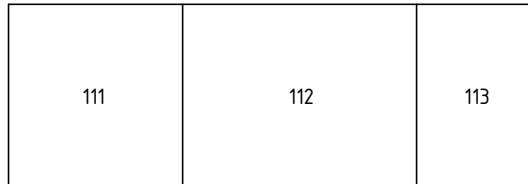

BET	ÄNDRING AVSER	DATUM	SIGN
FÖRFRÅGNINGSUNDERLAG			
 HELSINGBORG FASTIGHETSFÖRVALTNINGEN			
FASTIGHET			
ORIENTEN 6			
RÖNNOWSKA SKOLAN, NYTT KÖK OCH MATSAL			
OBJEKTSNR	BYGGNADS-ID	PROJEKTNR	
1457	5-266088	60095	
BYGGNAD			
1457-20 – HUS V (BYGGNAD 449)			
ORIENTERINGSFIGUR			
PLAN 03			
			
DEL			
			
VÄSTRA SANDGATAN			
A	ARKITEKTLAGET SKÅNE AB		T: 042-19 96 00
BR	FIRETECH ENGINEERING EMRON AB		T: 042-400 02 20
E	DEVELCON AB		T: 079-020 27 02
K	ÅKERMANS INGENJÖRSBYRÅ AB		T: 042-12 00 10
M	TYRÉNS SVERIGE AB		T: 010-452 20 00
S	SWECO SVERIGE AB		T: 08-695 60 00
SK	STORKÖKSVISION AB		T: 040-744 29
V	SWECO SVERIGE AB		T: 08-695 60 00
W	SWECO SVERIGE AB		T: 08-695 60 00
C	ZYNSKA BIM AB		T: 0734-45 98 99
UPPDRAGSNR	ANSVARIG		
P1001337	HUGO JACOBSSON		
DATUM	RITAD/KONSTR AV	HANDLÄGGARE	SYSTEMBETECKNING
2025-01-27	HJ	HJ	20-2
Hus 20			
SEKTIONER			
SKALA	NUMMER		REV
As	K--20-2-2000005		