
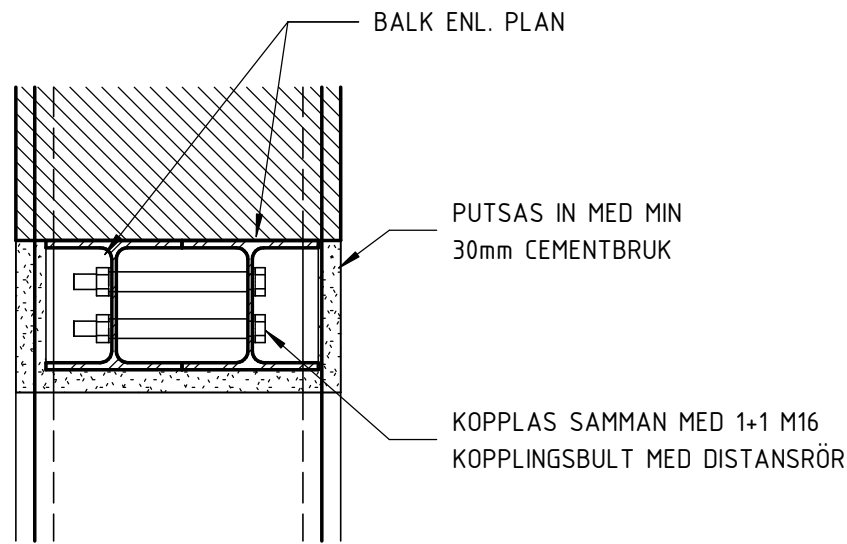
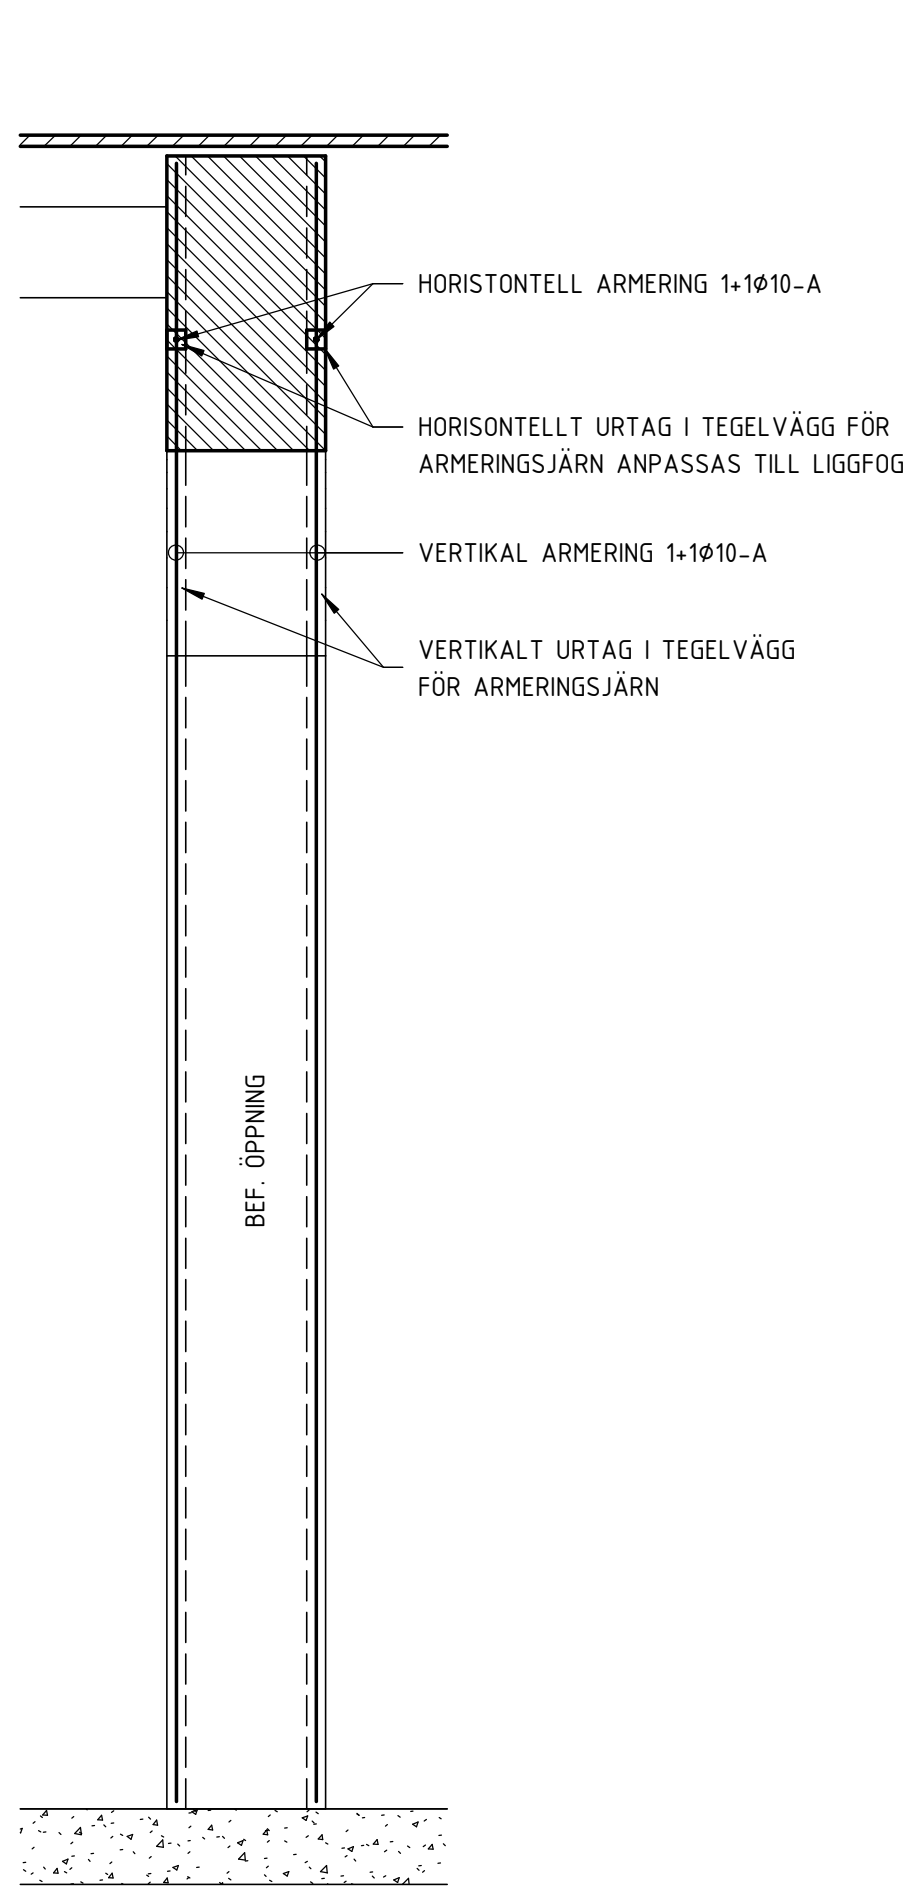
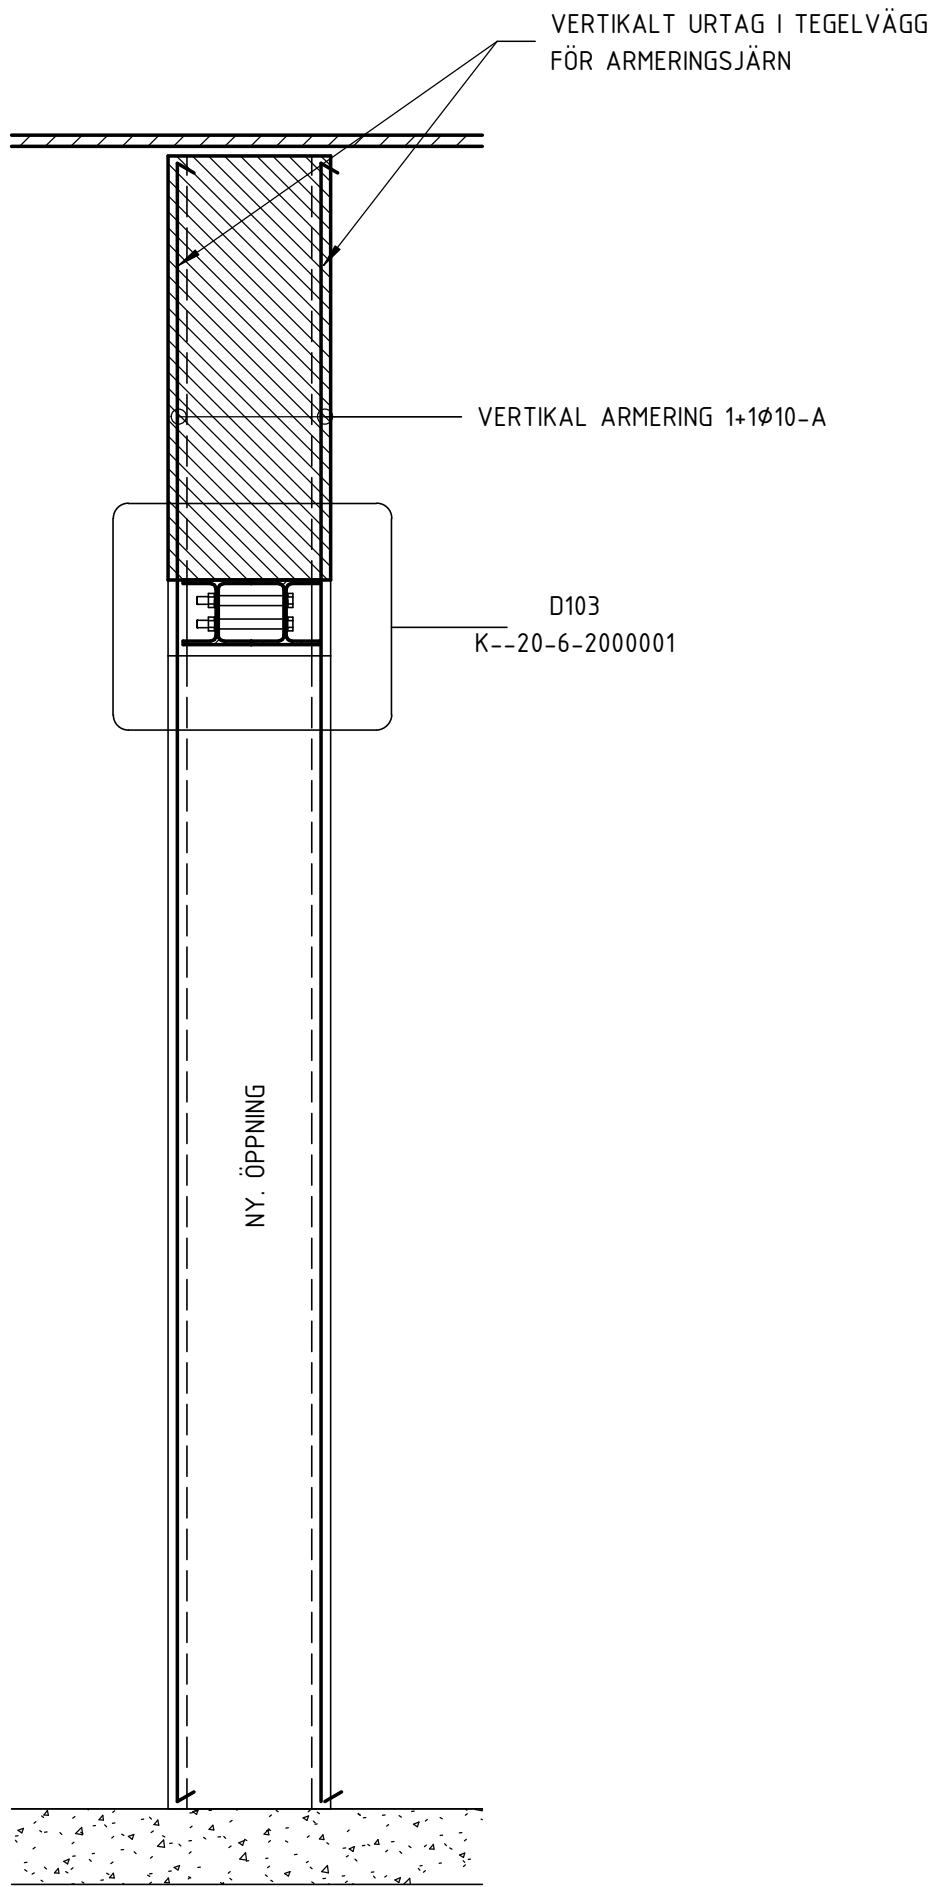


2025-01-24 08:52:31 F:\PROJEKT\2022\20200546 Rönnowska skolan Hus V. Helsingborg\KUP\1001337 Ombyggnad till matsal storkök\Modell\Revit 2023\1001337_FFU.rvt

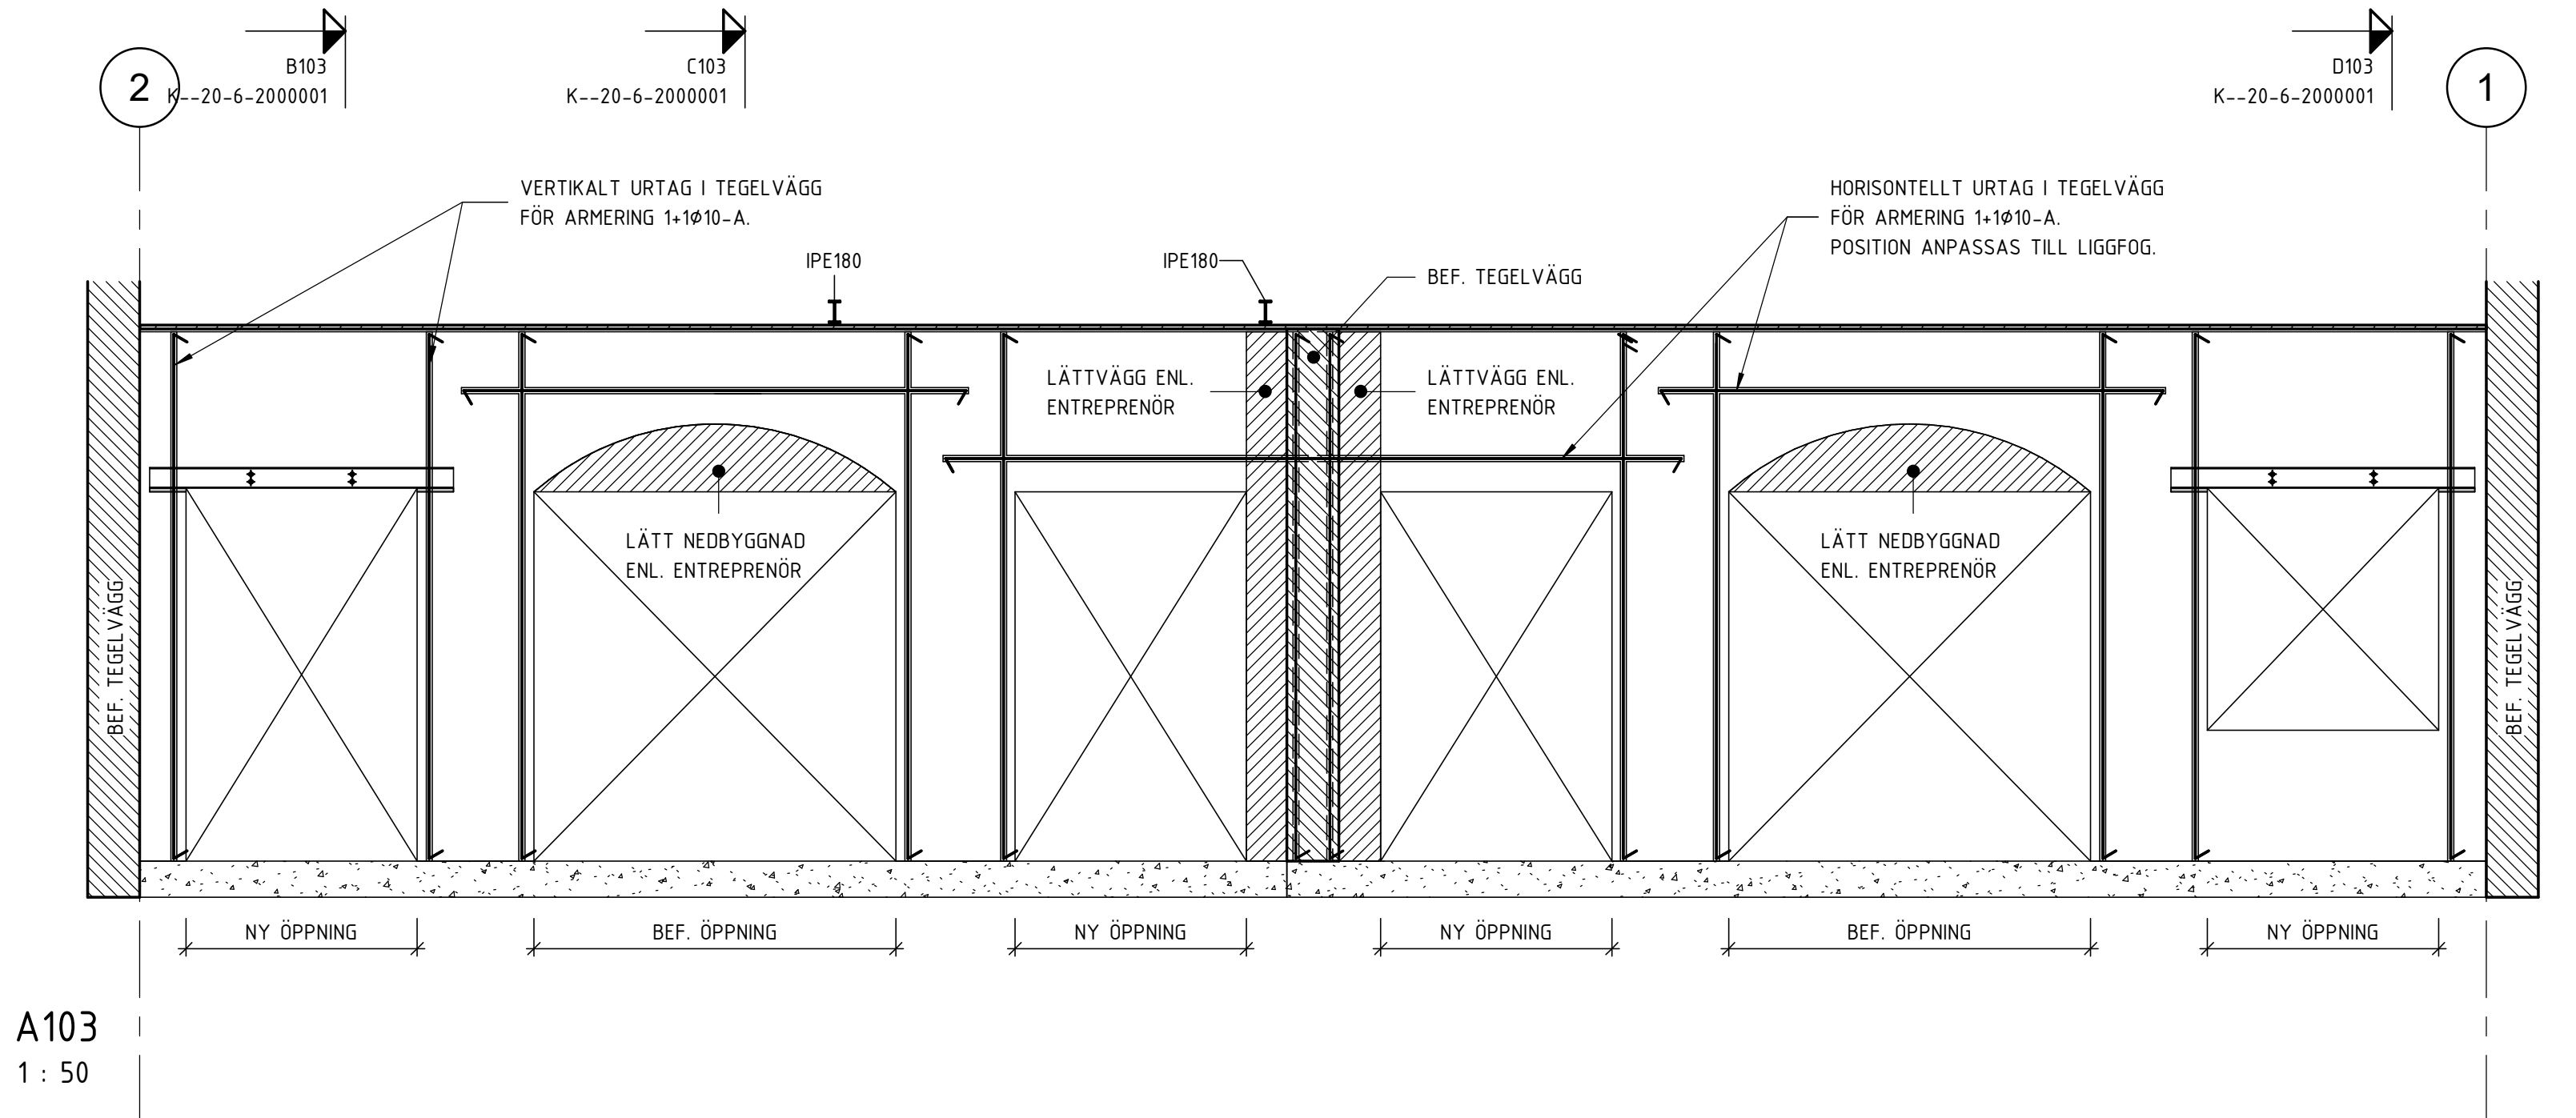

FÖRSTÄRKNING AV MURVERK:
MÅTT KONTROLLERAS PÅ PLATS.

VERTIKALA SAMT HORIZONTELLA URTAG GÖRS I BEFINTLIG TEGELVÄGG ENLIGT RITNING. DESSA FÖRLÄGGS MED FÖRDEL I BEFINTLIGA STÖT/LIGGFÖGAR.

ARMERINGSJÄRN ENLIGT RITNING PLACERAS SEDAN I SLITSAR OCH PUTSAS IGEN MED CEMENTBRUK

AVVÄXLING MED STÅLBALK:
MÅTT KONTROLLERAS PÅ PLATS.
INNAN ARBETE MED UPSÄGNING PÅBÖRJAS SKALL PROVISORIK STÄMPNING AV VÄGG OCH BJÄLKLAG UTFÖRAS.

STÅLBALK UPPLÄGGS PÅ AVJÄMNAT UPPLAG AV CEMENTBRUK. STÅLBALK KILAS I TREDJEDELPUNKTERNA. MELLAN ÖK BALK OCH TEGELVÄGG PACKS MED JORDFUKTIGT CEMENTBRUK TILL FULL ANLIGGNING ÖVER HELA BALKENS LÄNGD UPPNÅS.

STÅLBALKAR PUTSAS IN MED MIN 30mm CEMENTBRUK.

FÖRKLARINGAR


FÖRESKRIFTER

SE K-015-001

HÄNVISNINGAR

ALLMÄNNA ANVISNINGAR

K-015-001

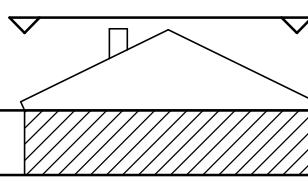ÄNDRING AVSER		DATUM	SIGN			
FÖRFRÅGNINGSUNDERLAG						
 HELSINGBORG FASTIGHETSFÖRVALTNINGEN						
FASTIGHET						
ORIENTEN 6						
RÖNNOWSKA SKOLAN, NYTT KÖK OCH MATSAL						
OBJEKTSNR	BYGGNADS-ID	PROJEKTNR				
1457	5-266088	60095				
BYGGNAD						
1457-20 - HUS V (BYGGNAD 449)						
ORIENTERINGSFIGUR						
PLAN 03 						
DEL						
<table><tr><td>111</td><td>112</td><td>113</td></tr></table> 				111	112	113
111	112	113				
VÄSTRA SANDGATAN						
A	ARKITEKTLAGET SKÅNE AB		T: 042-19 96 00			
BR	FIRETECH ENGINEERING EMRON AB		T: 042-400 02 20			
E	DEVELCON AB		T: 079-020 27 02			
K	ÅKERMANS INGENJÖRSBYRÅ AB		T: 042-12 00 10			
M	TYRÉNS SVERIGE AB		T: 010-452 20 00			
S	SWECO SVERIGE AB		T: 08-695 60 00			
SK	STORKÖKSVISION AB		T: 040-744 29			
V	SWECO SVERIGE AB		T: 08-695 60 00			
W	SWECO SVERIGE AB		T: 08-695 60 00			
C	ZYNKA BIM AB		T: 0734-45 98 99			
UPPDRAGSNR	ANSVARIG					
P1001337	HUGO JACOBSSON					
DATUM	RITAD/KONSTR AV	HANDLÄGGARE	SYSTEMBETECKNING			
2025-01-27	HJ	HJ	20-6			
Hus 20						
DETALJ VÄGG						
SKALA	NUMMER		REV			
1:50 1:20	K--20-6-2000001					

ORIGINALFORMAT: A1

