




2025-01-24 08:52:22 F:\PROJEKT\2022\22000546 Rönnowska skolan Hus V. Helsingborg\KUP\1001337 Ombyggnad till matsal storkök\Modell\Revit\2023P\1001337_FFU.rvt

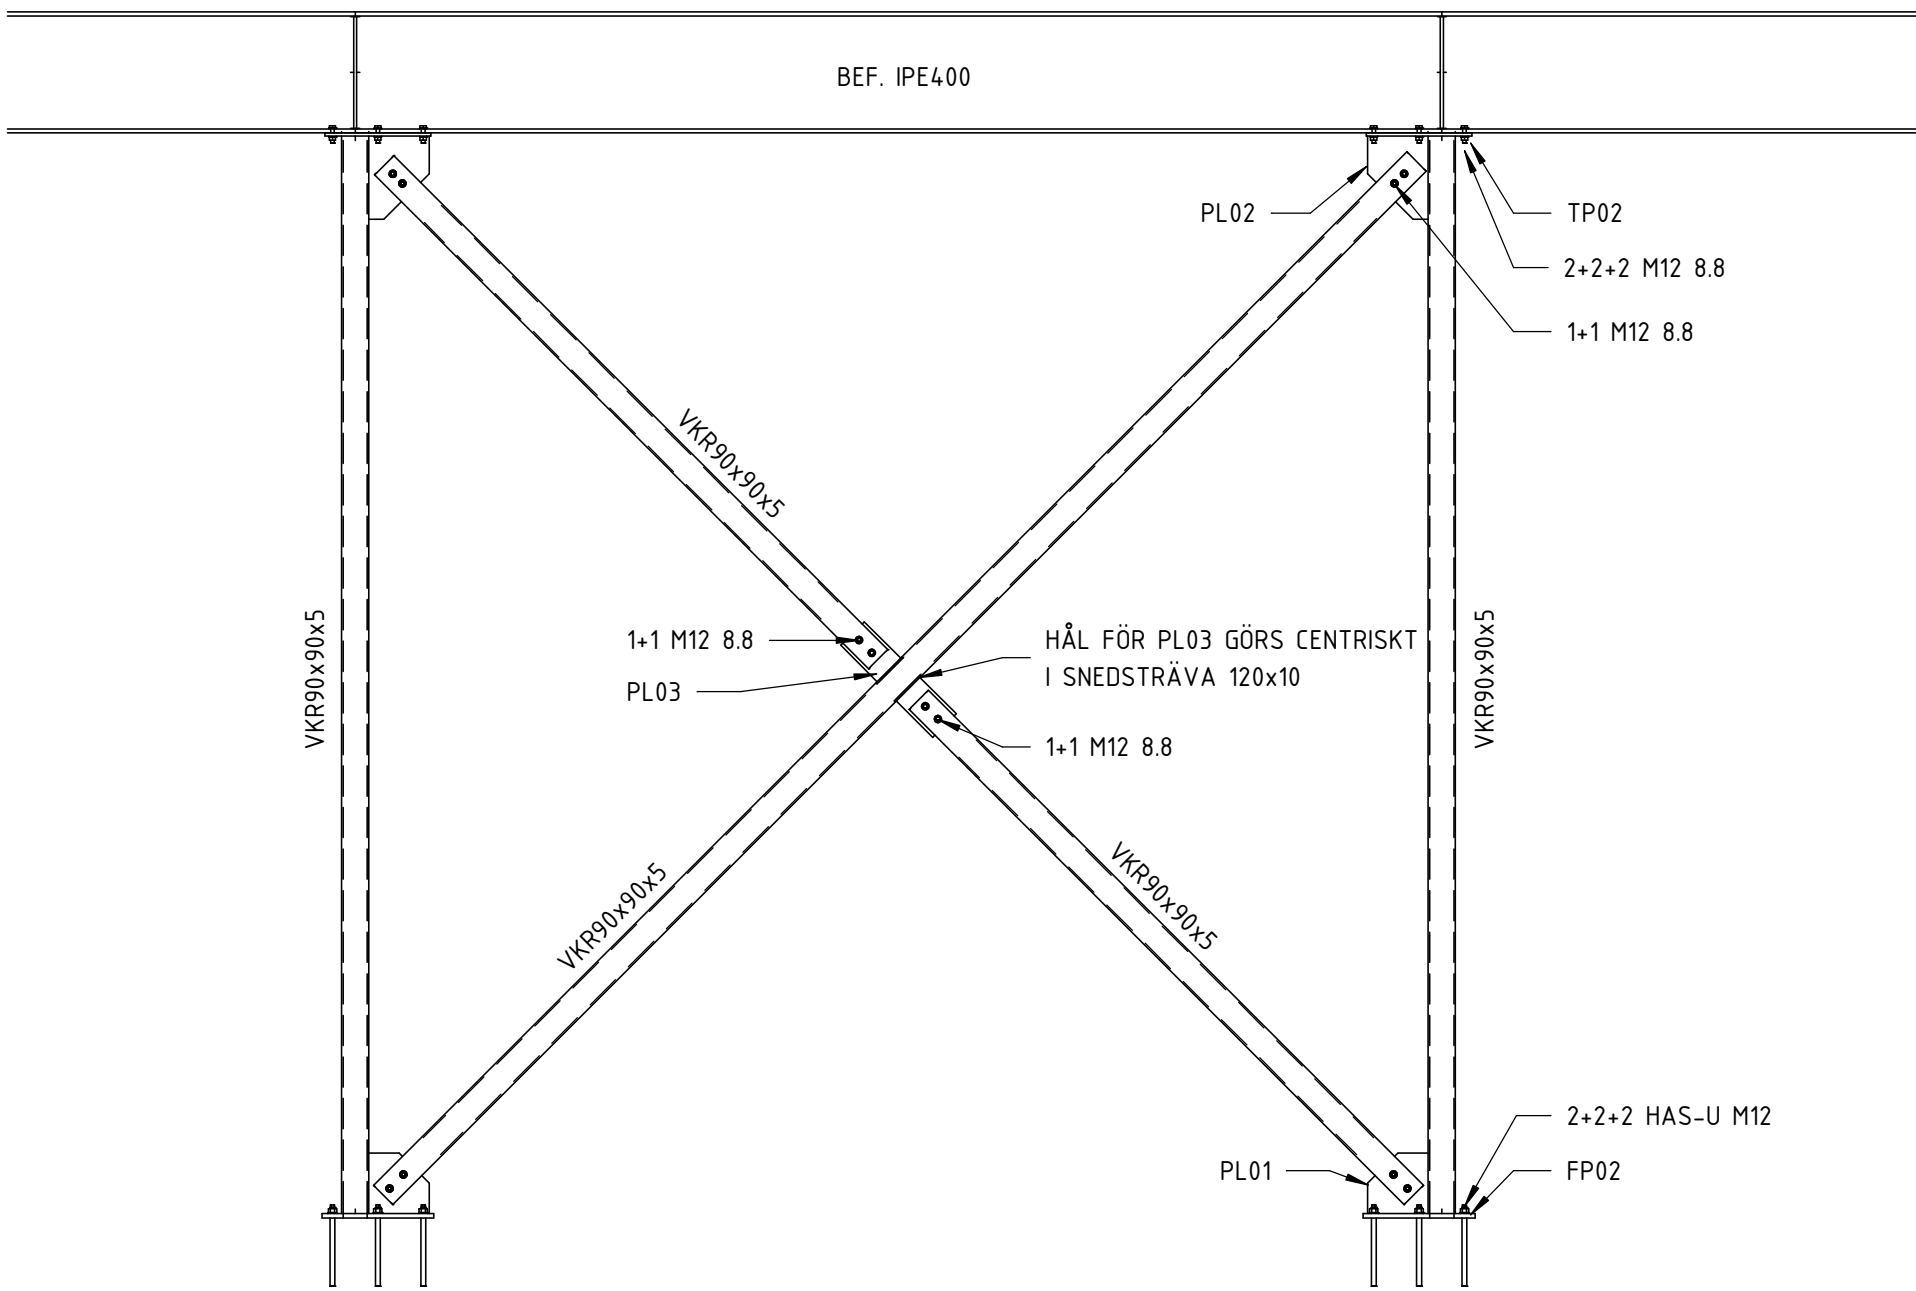

A241
1 : 25

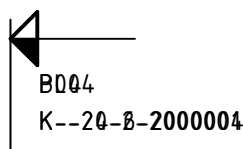

B241
1 : 25

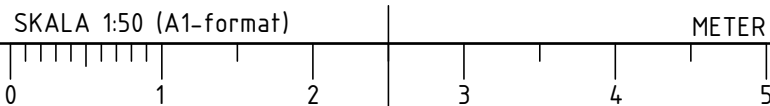

BET	ÄNDRING AVSER	DATUM	SIGN
FÖRFRÅGNINGSUNDERLAG			
 HELSINGBORG FASTIGHETSFÖRVALTNINGEN			
FASTIGHET ORIENTEN 6 RÖNNOWSKA SKOLAN, NYTT KÖK OCH MATSAL			
OBJEKTSNR 1457	BYGGNADS-ID 5-266088	PROJEKTNR 60095	
BYGGNAD 1457-20 - HUS V (BYGGNAD 449)			
ORIENTERINGSFIGUR			
PLAN 03 02 01 DEL 111 112 113 VÄSTRA SANDGATAN N			
A ARKITEKTLAGET SKÅNE AB T: 042-19 96 00			
BR FIRETECH ENGINEERING EMRON AB T: 042-400 02 20			
E DEVELCON AB T: 079-020 27 02			
K ÅKERMANS INGENJÖRSBYRÅ AB T: 042-12 00 10			
M TYRÉNS SVERIGE AB T: 010-452 20 00			
S SWECO SVERIGE AB T: 08-695 60 00			
SK STÖRKÖKSVISION AB T: 040-744 29			
V SWECO SVERIGE AB T: 08-695 60 00			
W SWECO SVERIGE AB T: 08-695 60 00			
C ZYNKA BIM AB T: 0734-45 98 99			
UPPDRAGSNR P1001337	ANSVARIG HUGO JACOBSSON		
DATUM 2025-01-27	RITAD/KONSTR AV HJ	HANDLÄGGARE HJ	SYSTEMBETECKNING 24-4
Hus 20 STÅLELEVATIONER			
SKALA 1:50 1:25	NUMMER K--24-4-2000001		REV

ORIGINALFORMAT: A1