
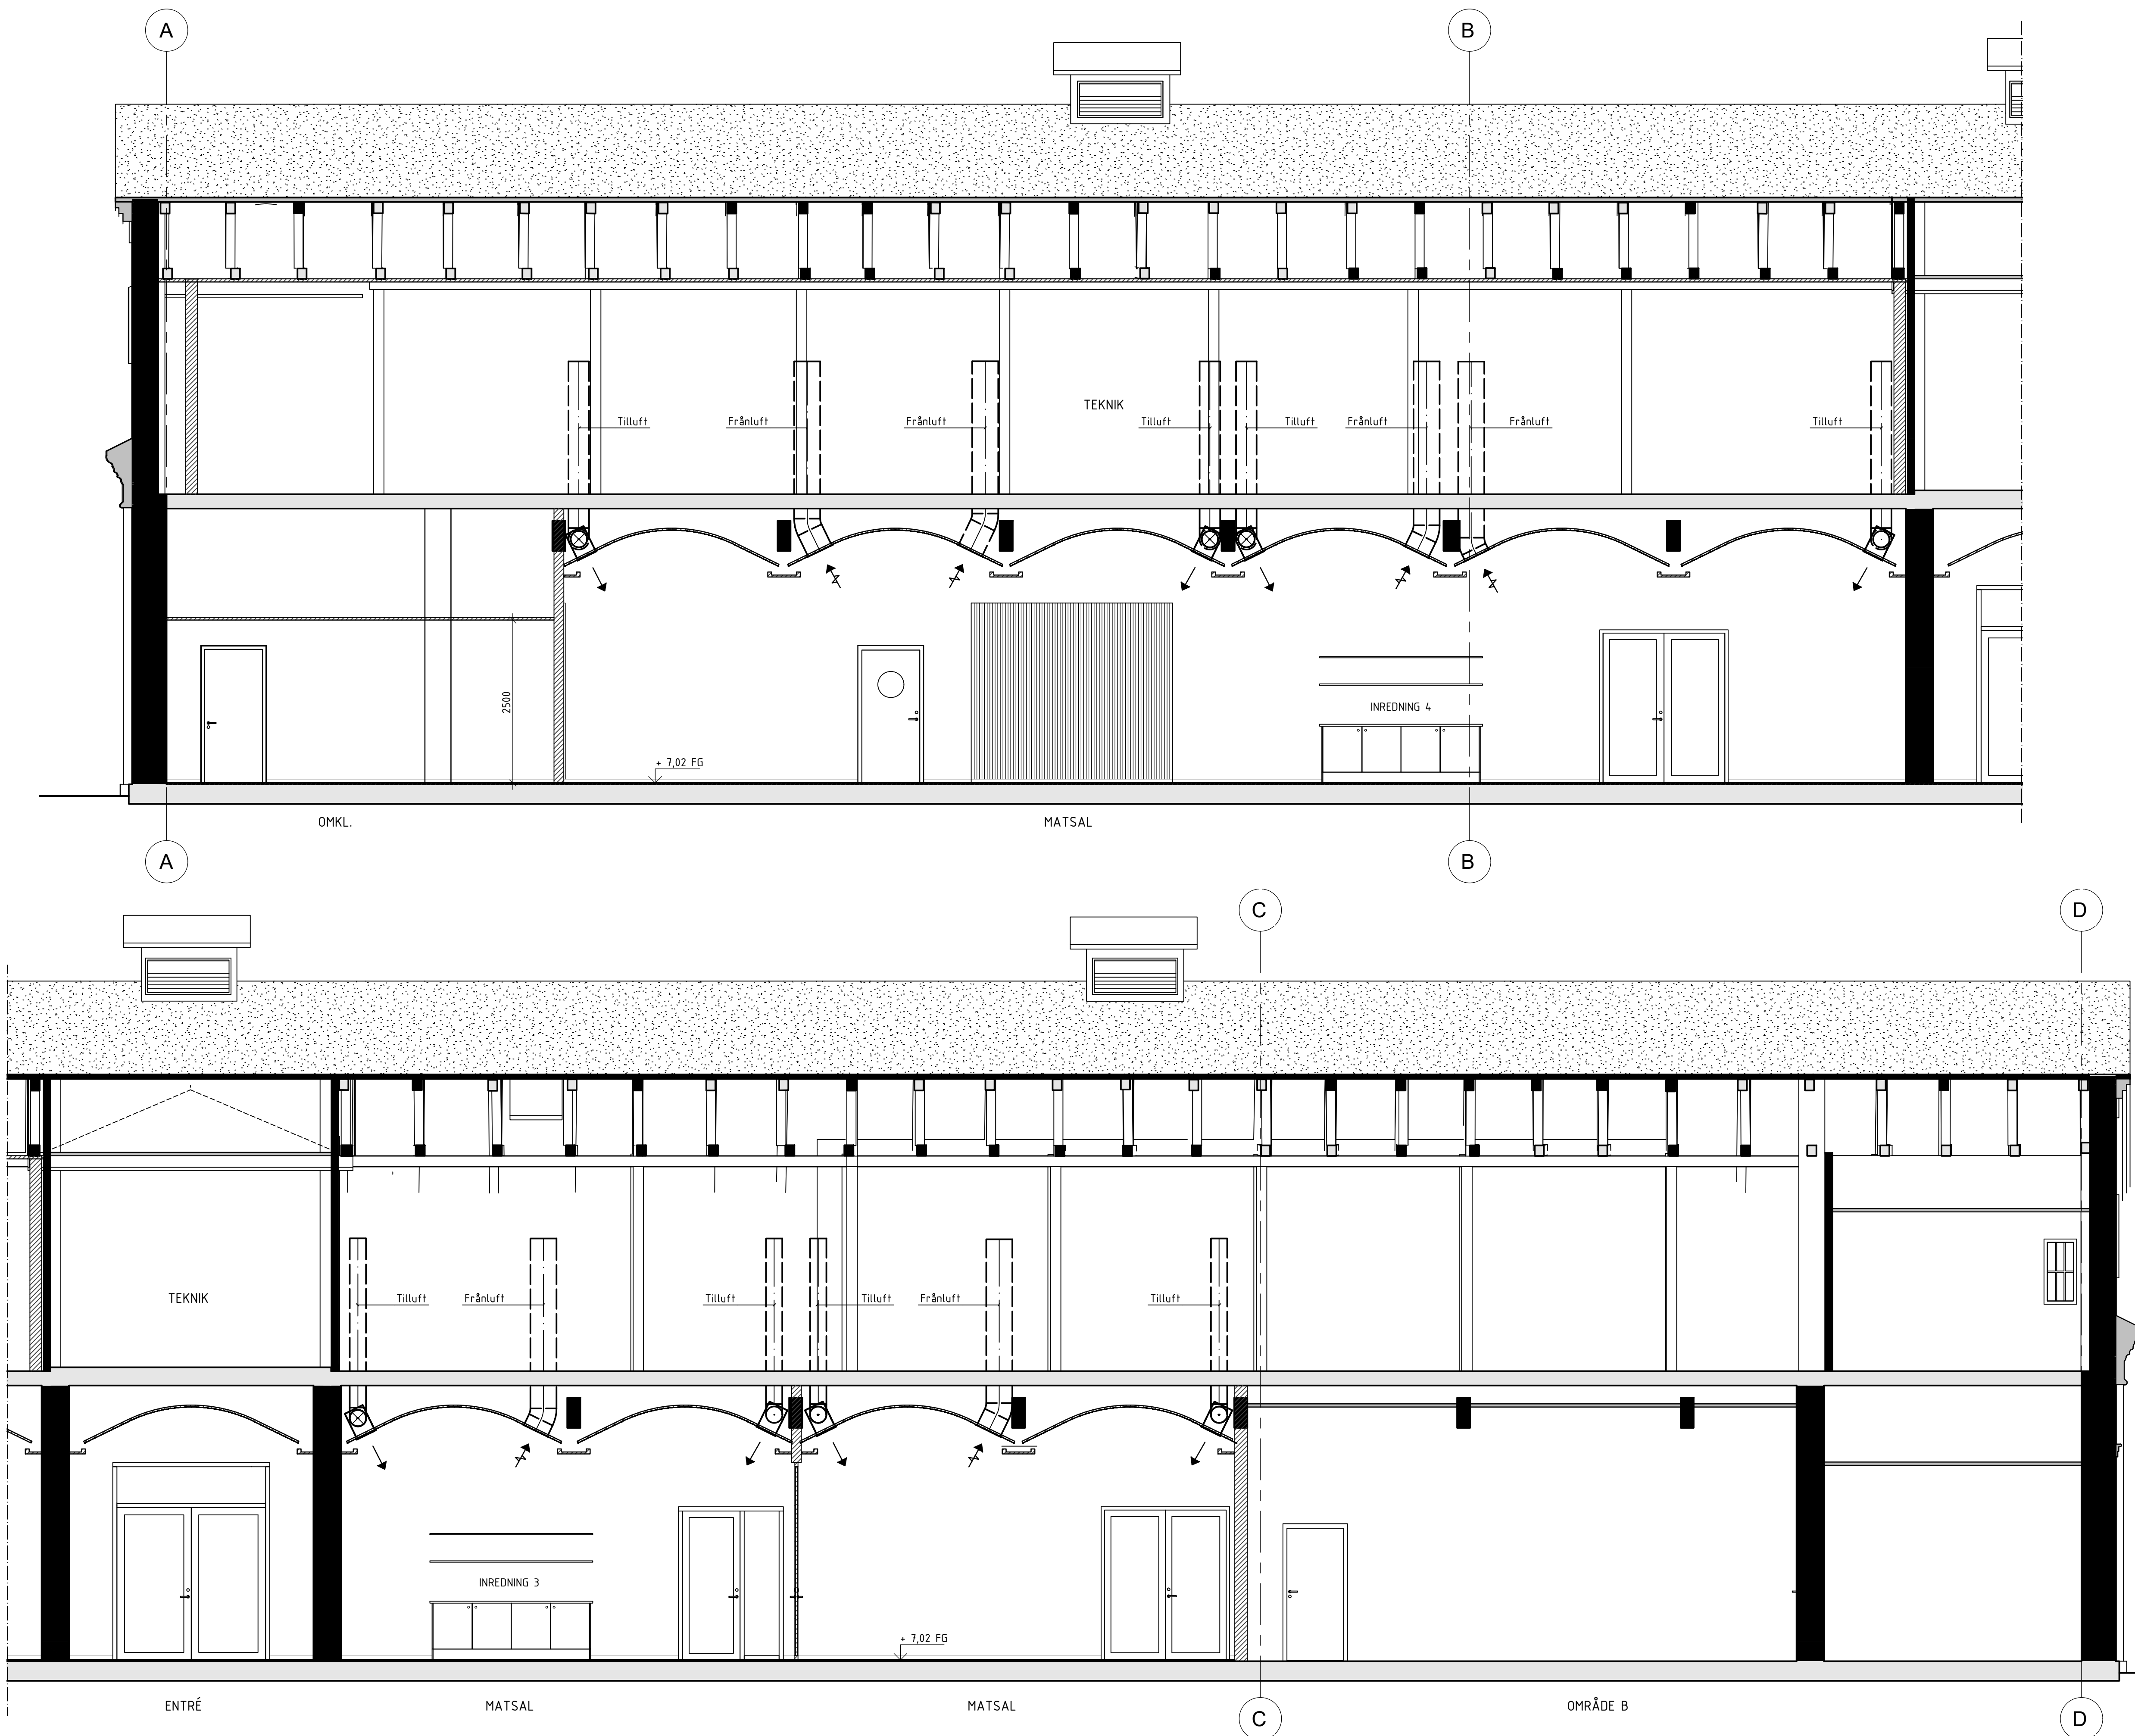
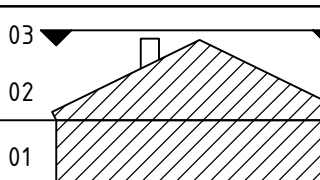
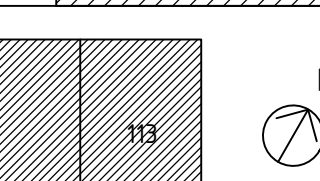


List of Xrefs:
A=40-2-2000013 [\\s\N\Media\A=40-2-2000013.dwg]
P=2000000=AT [\\s\Kont\p=2000000=AT.dwg]

2024-02-05 09:26:52 \\VALAG-FS\Redirected\Folders\mikaab\My Documents\A-00_V20001_mikaab@arkitektlaget.se.rvt

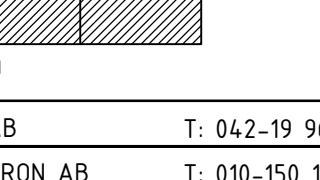

BET	ÄNDRING AVSEER		DATUM	SIGN
FÖRFRÅGNINGSUNDERLAG				
 HELSINGBORG FASTIGHETSFÖRVALTNINGEN				
FASTIGHET				
ORIENTEN 6				
RÖNNOWSKA SKOLAN, NYTT KÖK OCH MATSAL				
OBJEKTSNR	BYGGNADS-ID		PROJEKTSNR	
1457	5-266088		60095	
BYGGNAD				
1457-20 – HUS V (BYGGNAD 449)				
ORIENTERINGSFIGUR				
PLAN		03		
DEL		02		
DEL		01		
VÄSTRA SANDGATAN				
A	ARKITEKTLAGET SKÅNE AB		T: 042-19 96 00	
BR	FIRETECH ENGINEERING EMRON AB		T: 010-150 14 00	
E	DEVELCON AB		T: 079-020 27 02	
K	ÅKERMAN'S INGENJÖRSBYRÅ AB		T: 042-12 00 10	
M	TYRÉN'S AB		T: 010-452 20 00	
S	SWECO SVERIGE AB		T: 08-695 60 00	
SK	STORKÖKSVISION		T: 040-744 29	
V	SWECO SVERIGE AB		T: 08-695 60 00	
W	SWECO SVERIGE AB		T: 08-695 60 00	
UPPDRAGSNR		ANSVARIG		
30068791		JAKOB BENGTSOON		
DATUM		RITAD/KONSTR AV	HANDLÄGGARE	SYSTEMBETECKNING
2025-01-27		J.MRSO	J.B.	-
HUS 20				
SEKTION D-D				
PRINCIP VENTILATION				
-				
SKALA (A1)		NUMMER		REV
1 : 50		V--57-2-2000013		
ORIGINALFORMAT: A1				