

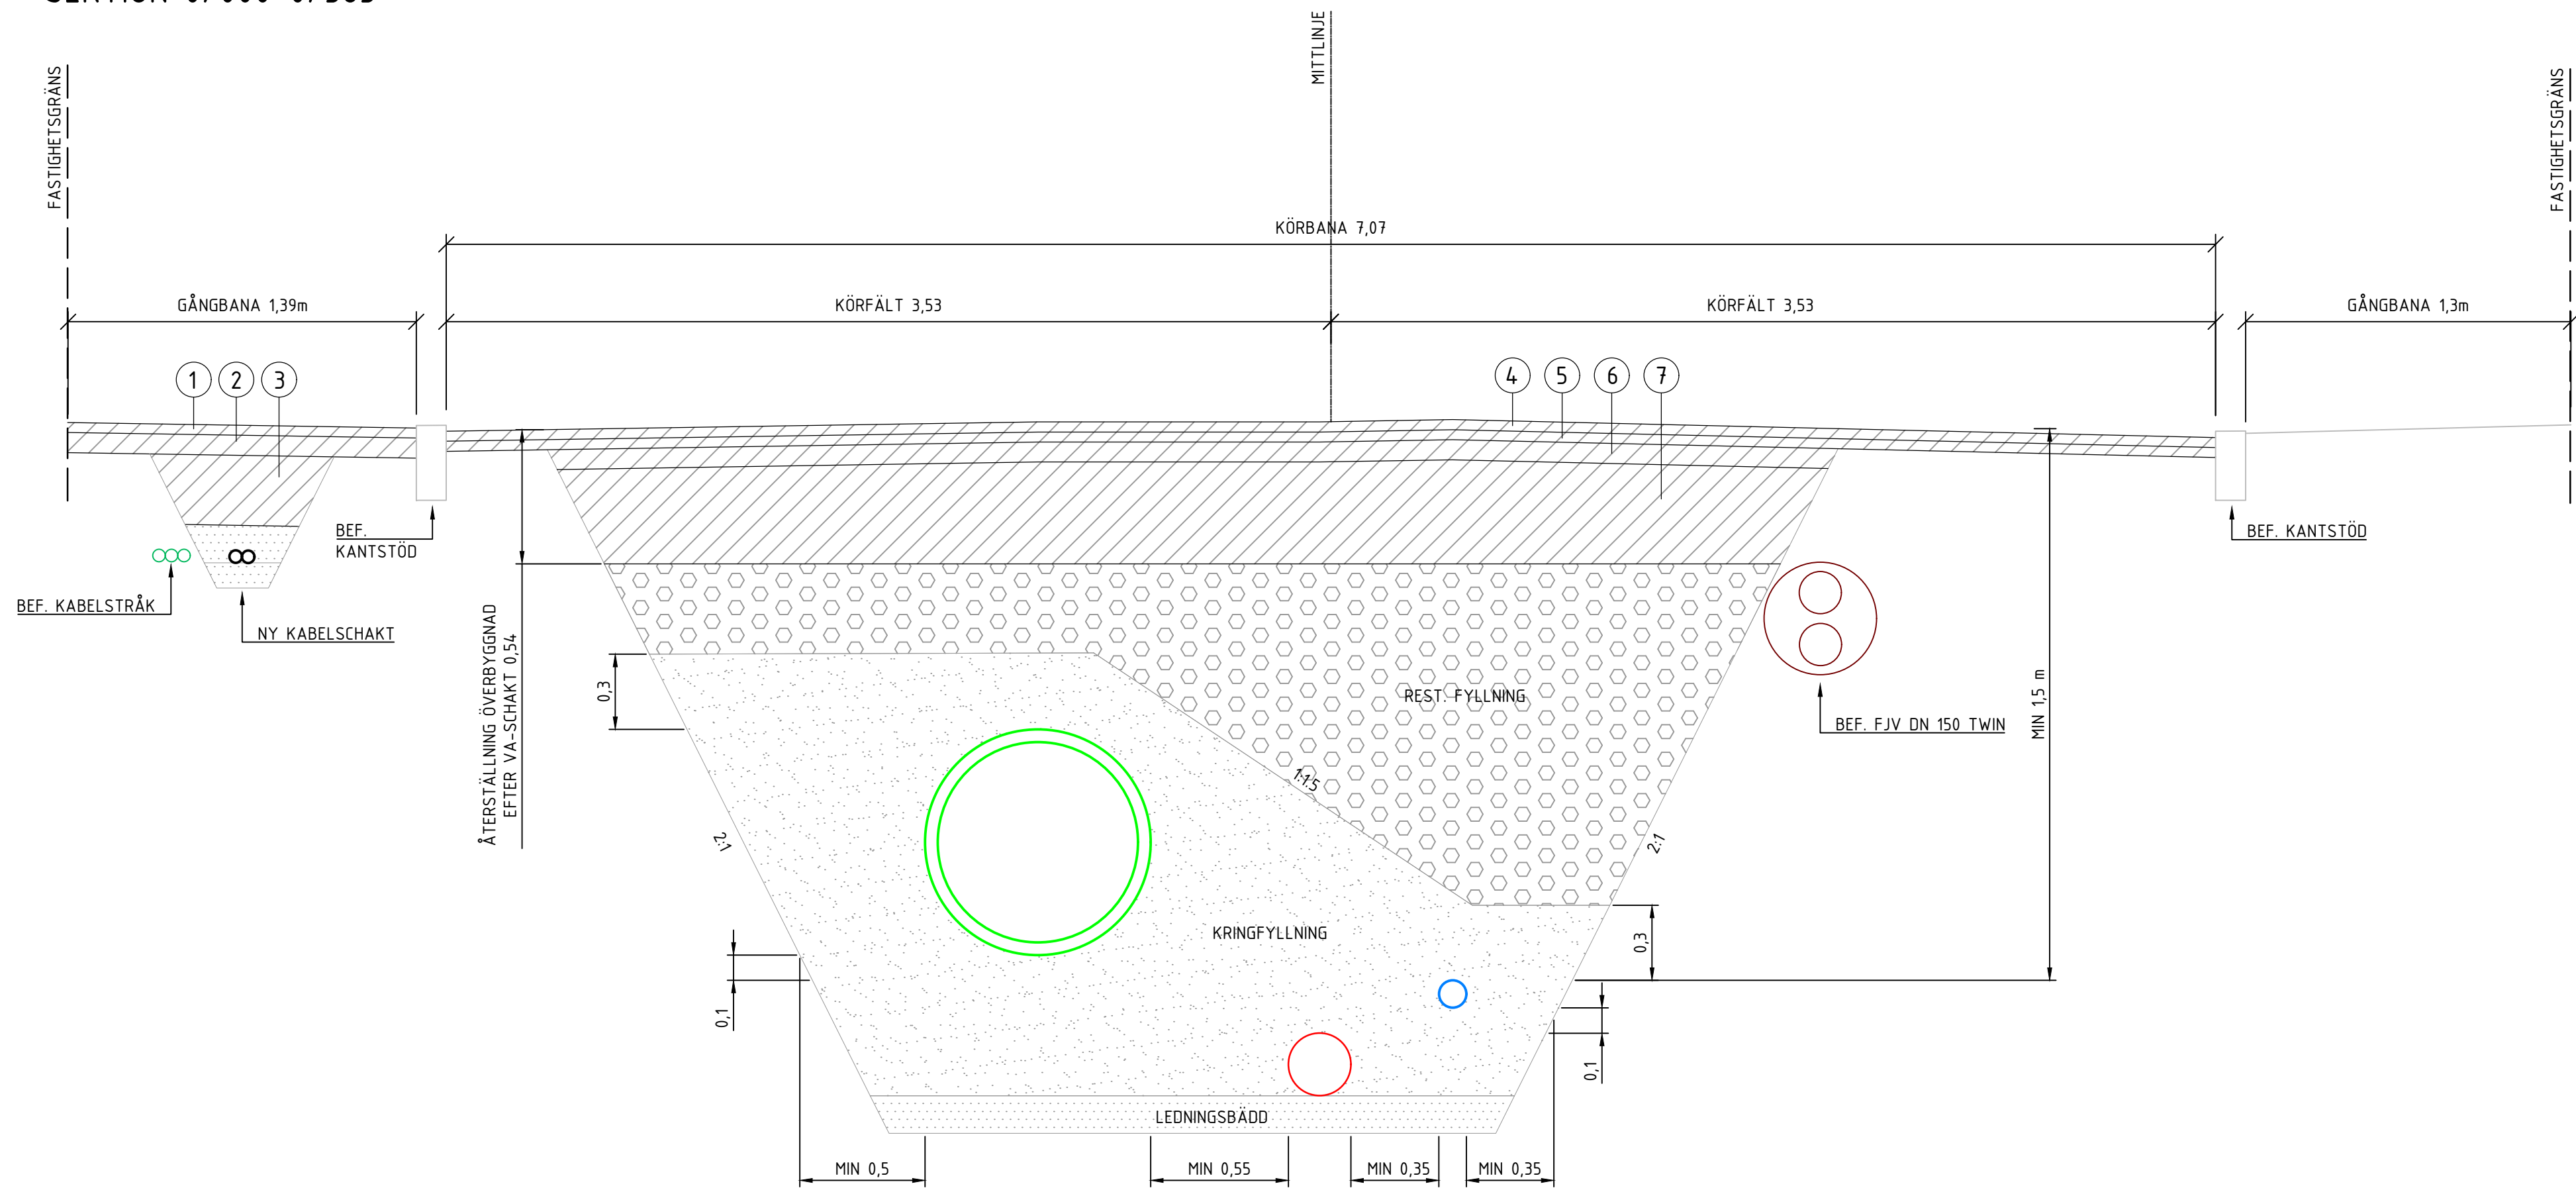


HORNSGATAN
SEKTION 0/000-0/363

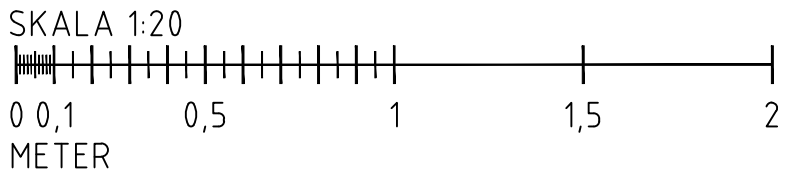

HORNSGATAN
SEKTION 0/363-0/633

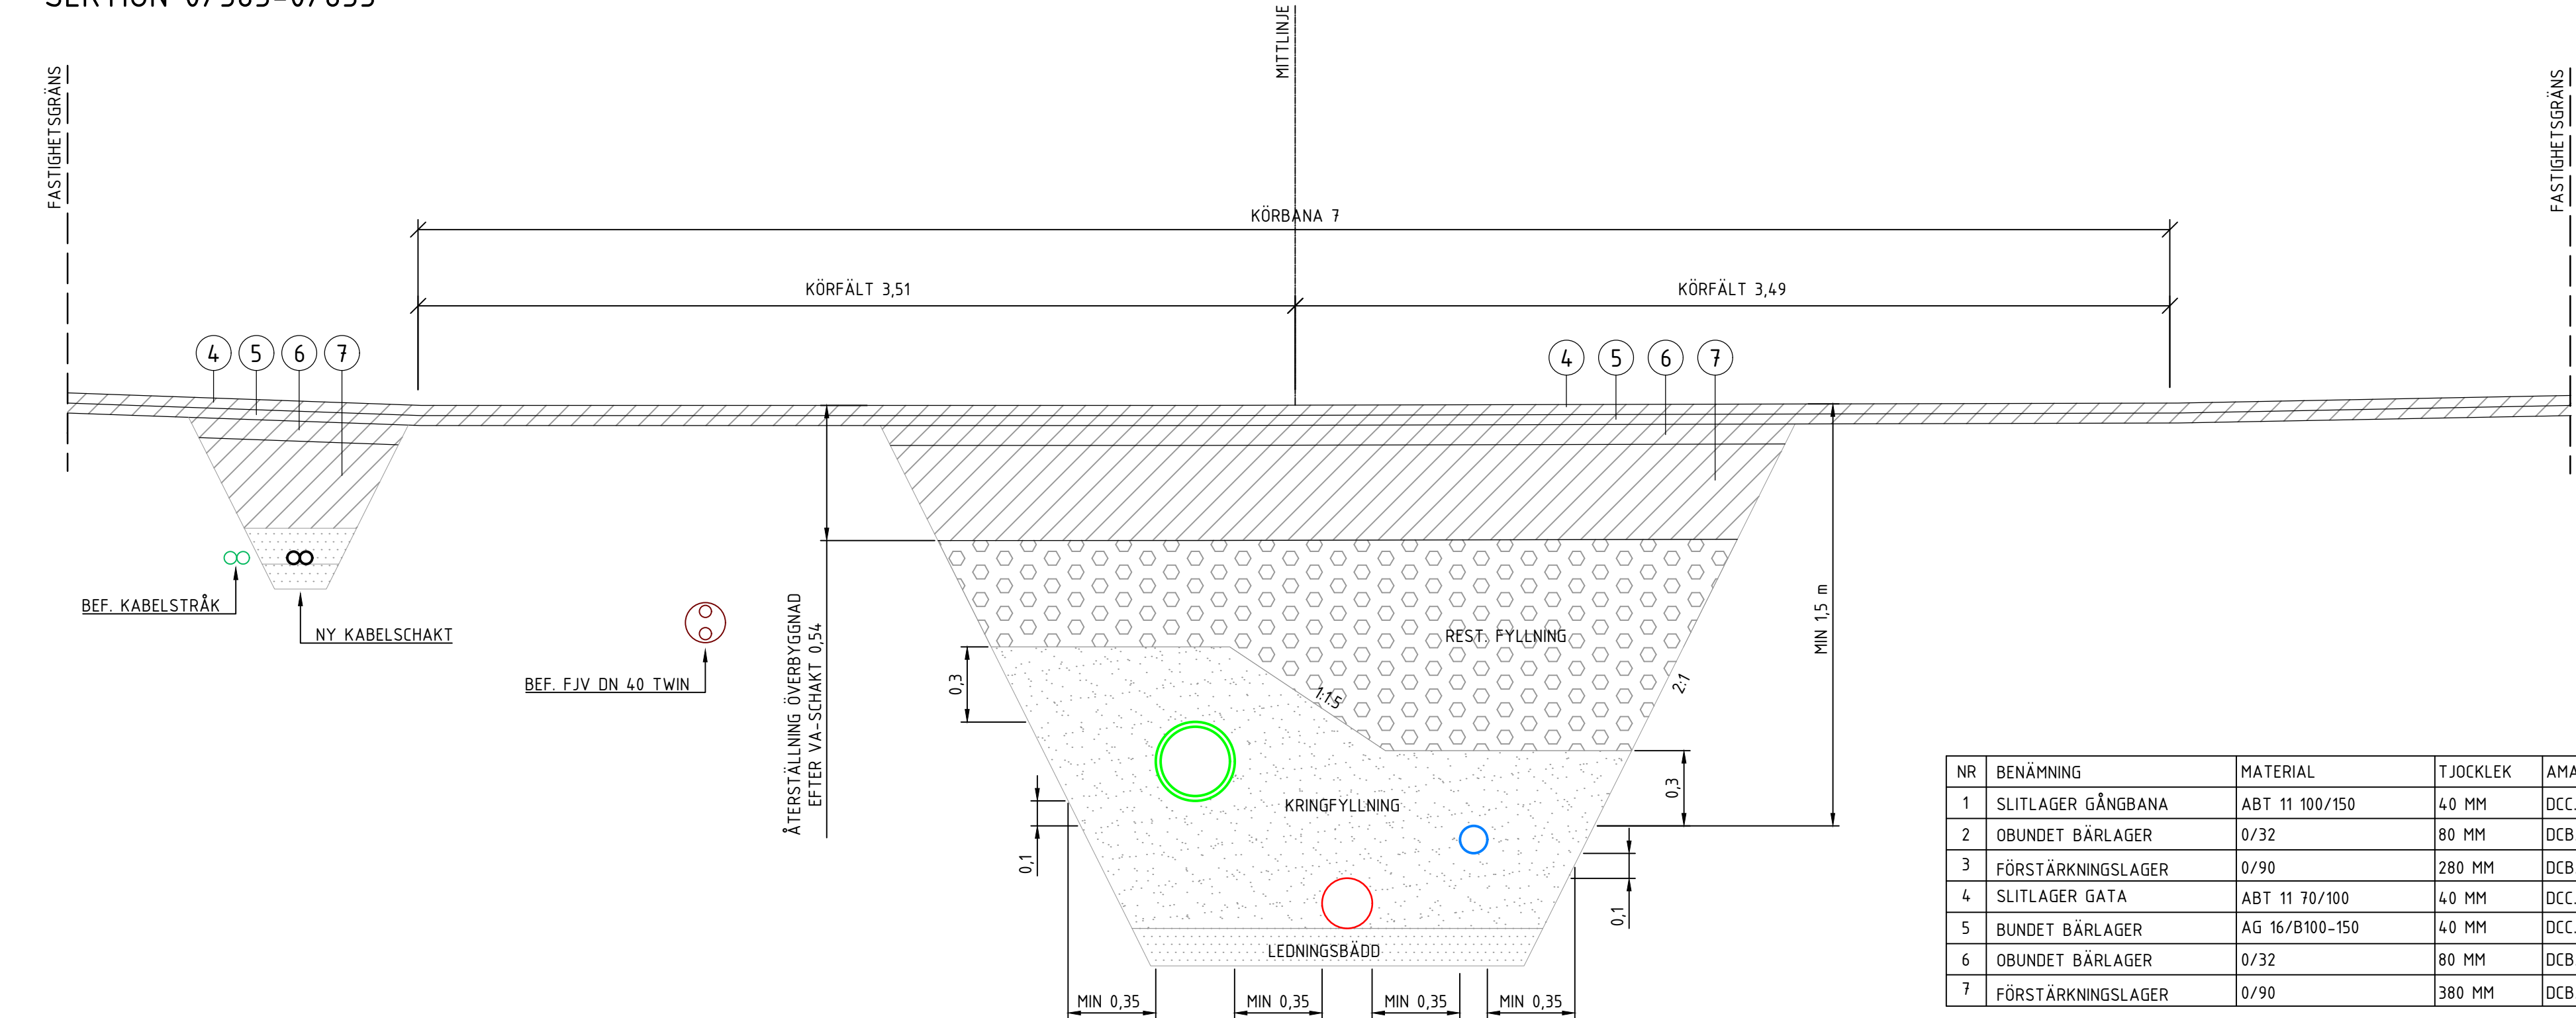

TECKENFÖRKLARING

- NY GATA
- SCHAKT
- NY DAGVATTENLEDNING
- NY SPILLVATTENLEDNING
- NY VATTENLEDNING

ANMÄRKNING

MIN TÄCKNINGSDJUP VATTENLEDNING 150M
JORDSCHAFT SLÄNTLUTNING 2:1
BERGSCHAFT SLÄNTLUTNING 5:1

KOORDINATSYSTEM

PLAN: SWEREF 991630
HÖJD: RH2000

NR	BENÄMNING	MATERIAL	TJOCKLEK	AMA-KOD
1	SLITLAGER GÅNGBANA	ABT 11 100/150	40 MM	DCC.34.11
2	OBUNDET BÄRLAGER	0/32	80 MM	DCB.313
3	FÖRSTÄRKNINGSLAGER	0/90	280 MM	DCB.213
4	SLITLAGER GATA	ABT 11 70/100	40 MM	DCC.24.11
5	BUNDET BÄRLAGER	AG 16/B100-150	40 MM	DCC.2111
6	OBUNDET BÄRLAGER	0/32	80 MM	DCB.312
7	FÖRSTÄRKNINGSLAGER	0/90	380 MM	DCB.212

BET	ANT	ÄNDRINGEN AVSER	SIGN	DATUM
FÖRFRÅGNINGSUNDERLAG				
HORNSGATAN NYBRÖ				
 NYBRÖ ENERGI <i>ditt lokala energibolag</i>				
PROJEKTBYGGAREN				
UPPDRAG NR 8524.006	RITAD AV I. P./H. K. TEL:		HANDLÄGGARE J. WIJK TEL:	
DATUM 2025-02-10	ANSVARIG J. WIJK		SANERING AV VA-LEDNINGAR SAMT EL- OCH BELYSNINGSKABLAR	
NORMALSEKTION - PRINCIPSKISS				
SKALA (A1/A3) 1:20	NUMMER R-51-2N-001		I BET	