


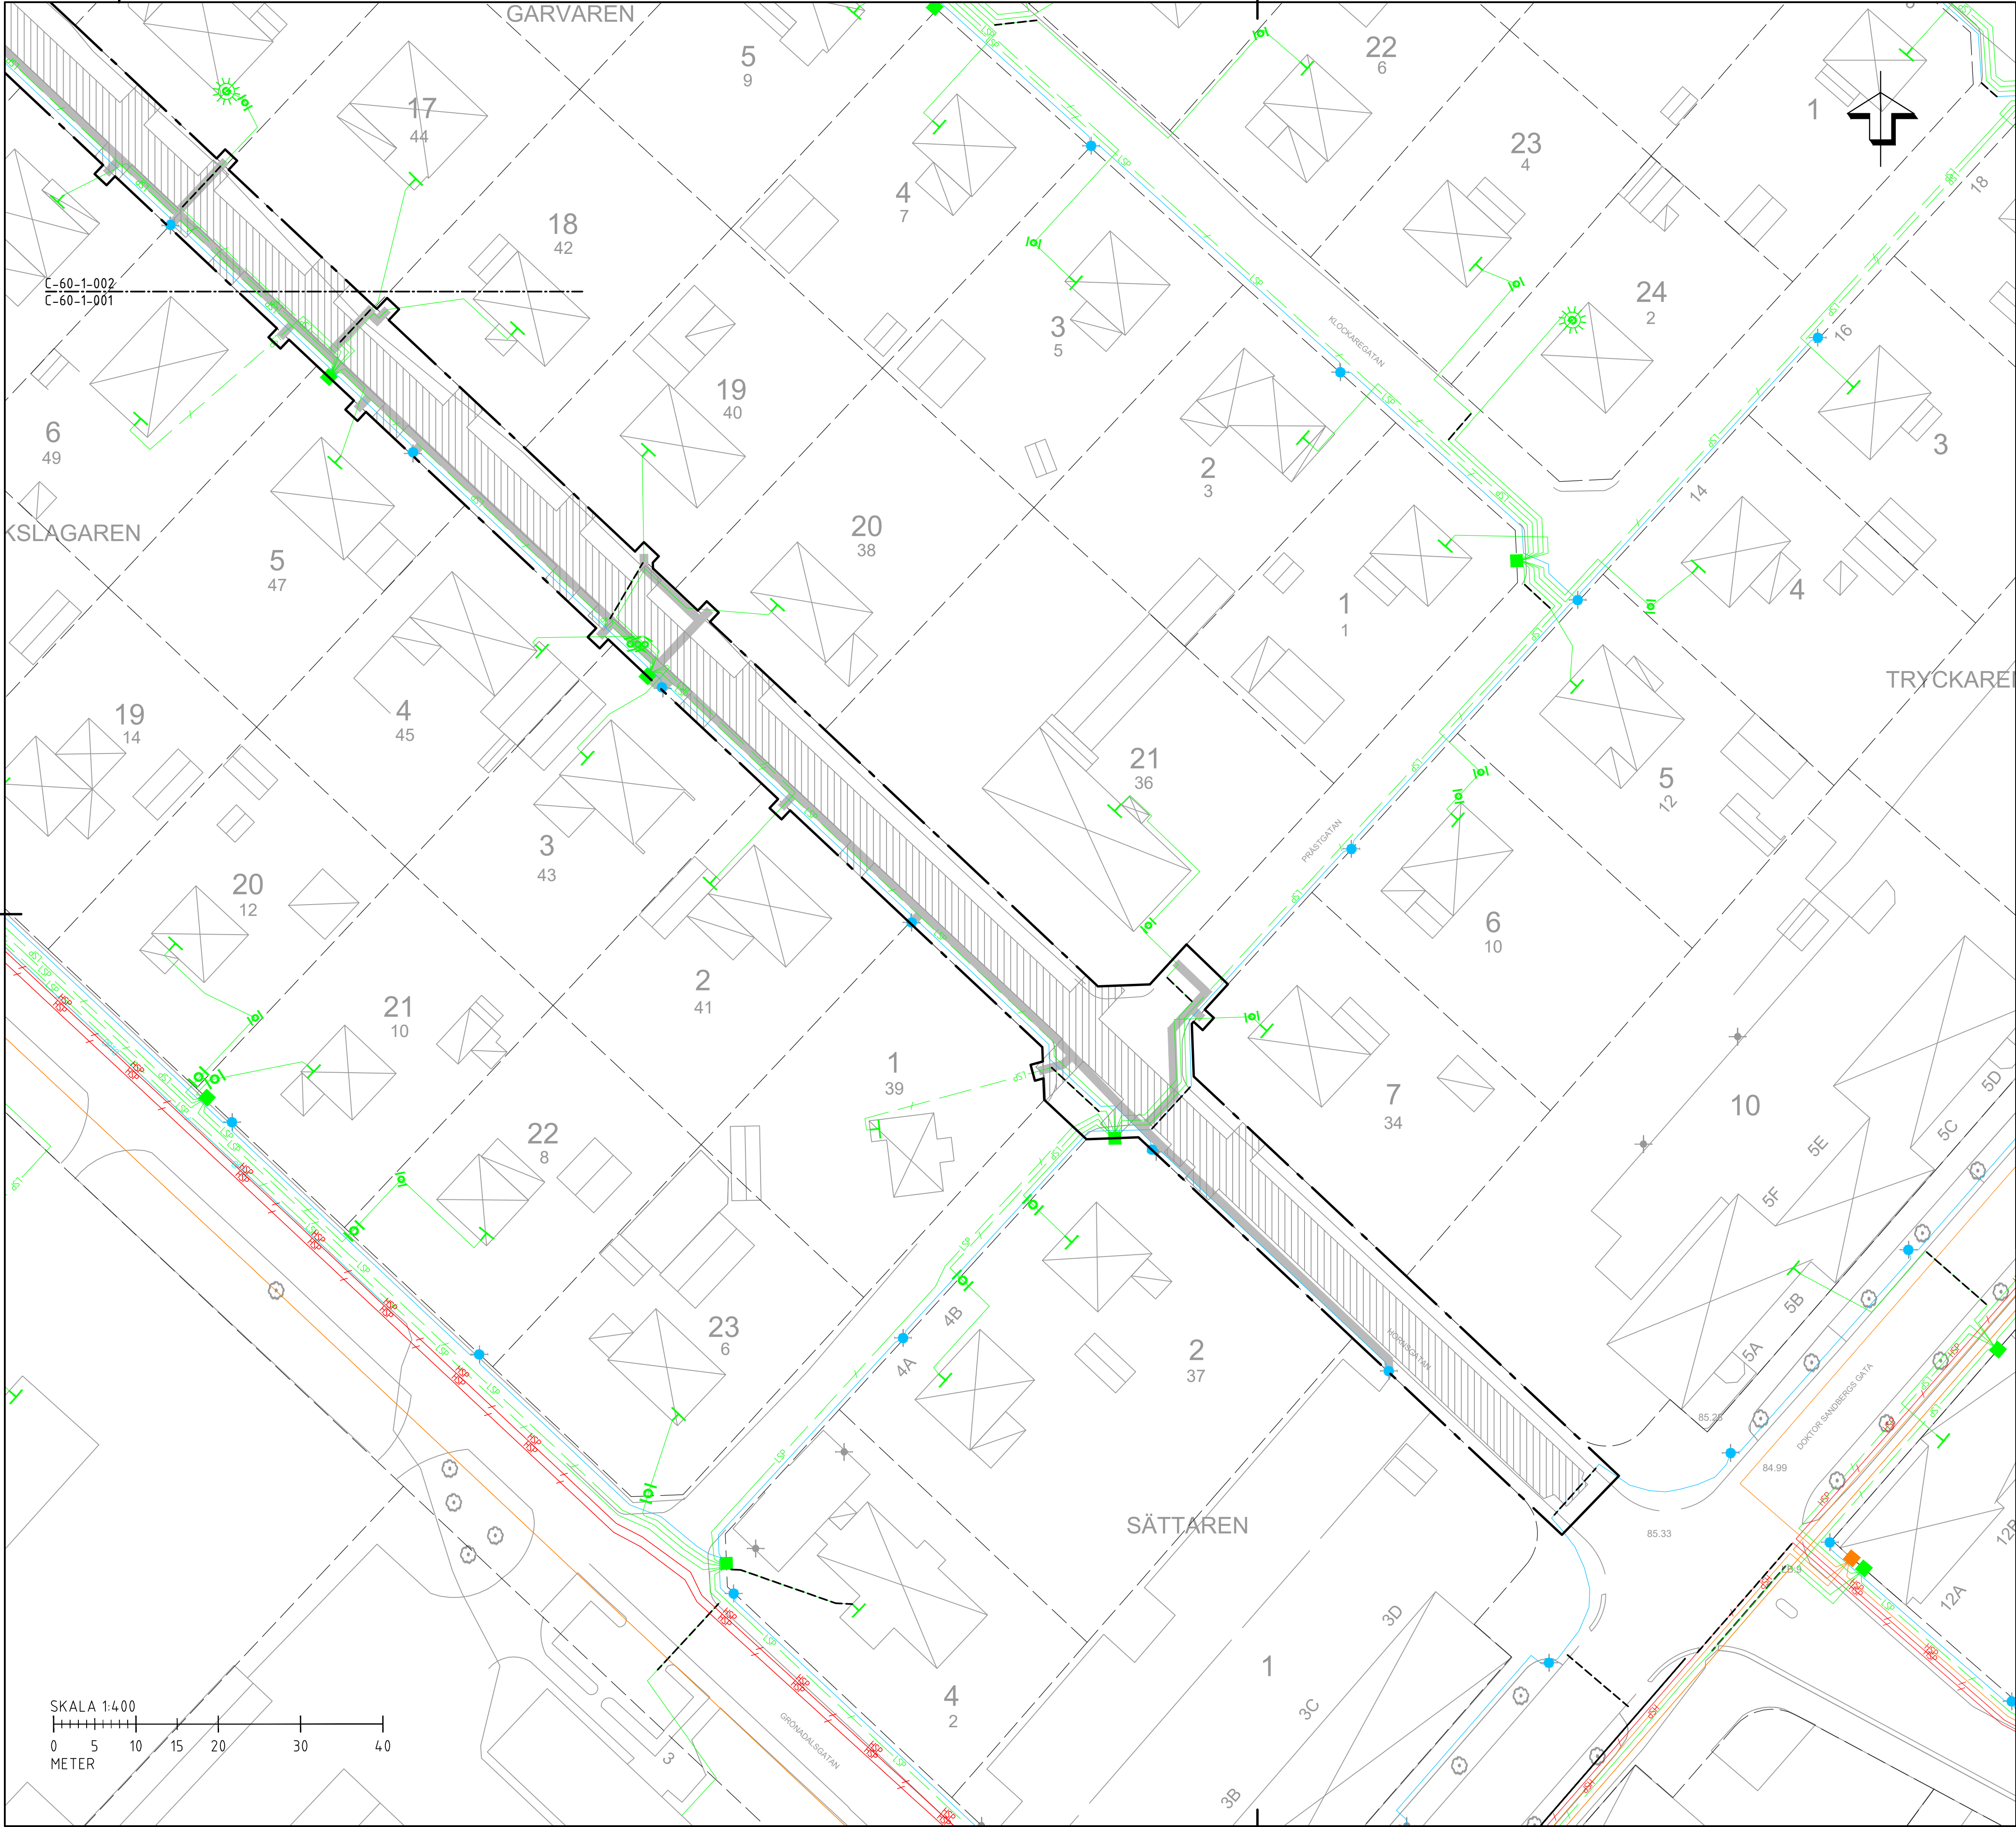


TECKENFÖRKLARING

- Bef. Belysningskabel
- Bef. Lågspänningskabel
- Bef. Högspänningskabel
- Bef. Optokabel
- Bef. Telekabel
- Bef. Skyddsror
- Fastighetsgräns
- Ny VA-schakt
- Ny el-schakt
- Arbetsområdesgräns

KOORDINATSYSTEM

PLAN: SWEREF 991630
HÖJD: RH2000

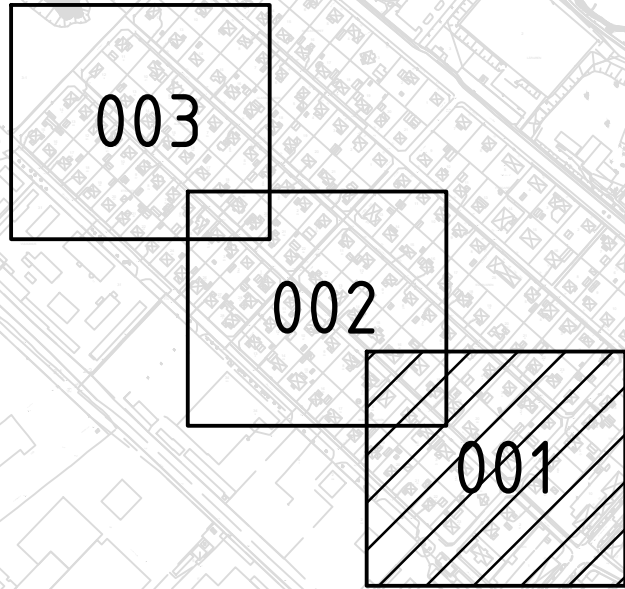

BET	ANT	ÄNDRINGEN AVSER	SIGN	DATUM		
FÖRFRÅGNINGSUNDERLAG						
HORNSGATAN NYBRO						
 NYBRO ENERGI <i>ditt lokala energibolag</i>						
PROJEKT BYGGAREN						
UPPDRAG NR 8524.006	RITAD AV I. PÅLSSON TEL:	HANDLÄGGARE J. WIJK TEL:				
DATUM 2025-02-10	ANSVARIG J. WIJK					
SANERING AV VA-LEDNINGAR SAMT EL- OCH BELYSNINGSKABLAR BEFINTLIGA KABLAR PLAN						
SKALA (A1/A3) 1:400	NUMMER C-60-1-001	I BET				